

**«Жилой комплекс» расположенный по адресу: г. Москва, ЦАО,  
Садовническая ул., вл 76/71**

***ПРОЕКТНАЯ ДОКУМЕНТАЦИЯ***

**Раздел 3. Архитектурные решения**

**Часть 1. Архитектурные решения. Планы**

**АА/БЭ- 03-ДСЗ-АР1**

**Корректировка**

**Том 3.1**

|                          |  |
|--------------------------|--|
| Взам. инв. №Взам.        |  |
| Подп. и датаПодп. и дата |  |
| Инв. № подл.Инв.         |  |

**«Жилой комплекс» расположенный по адресу: г. Москва, ЦАО,  
Садовническая ул., вл 76/71**

## ПРОЕКТНАЯ ДОКУМЕНТАЦИЯ

### Раздел 3. Архитектурные решения

#### Часть 1. Архитектурные решения. Планы

**АА/БЭ- 03-ДСЗ-АР1**

**Корректировка**

**Том 3.1**

Главный архитектор

Е.Г. Ким

Главный инженер проекта

В.В. Остроумов

Главный архитектор проекта

А.В. Добрякова

|         |  |
|---------|--|
| инв. №  |  |
| № подл. |  |

| Содержание тома     |  |                                                        |  |  |  |  |  |            |  |  |  |
|---------------------|--|--------------------------------------------------------|--|--|--|--|--|------------|--|--|--|
| Обозначение         |  | Наименование                                           |  |  |  |  |  | Примечание |  |  |  |
| AA/БЭ-03-ДСЗ-АР1.С  |  | Содержание                                             |  |  |  |  |  |            |  |  |  |
| AA/БЭ-03-ДСЗ-АР1.СС |  | Справка о соответствии                                 |  |  |  |  |  |            |  |  |  |
| AA/БЭ-03-ДСЗ-АР1.ПЗ |  | Пояснительная записка                                  |  |  |  |  |  | 1-19       |  |  |  |
| AA/БЭ-03-ДСЗ-АР1    |  | Графические материалы:                                 |  |  |  |  |  |            |  |  |  |
|                     |  | План второго подземного этажа на отм.-9.600. М 1_200.  |  |  |  |  |  | Лист 1     |  |  |  |
|                     |  | План первого подземного этажа на отм.-6.000. М 1_200.  |  |  |  |  |  | Лист 2     |  |  |  |
|                     |  | План технического пространства на отм.-1,800. М 1_200. |  |  |  |  |  | Лист 3     |  |  |  |
|                     |  | Корпуса 1, 2. План 1 этажа. М 1_200.                   |  |  |  |  |  | Лист 4     |  |  |  |
|                     |  | Корпуса 1, 2. План 2 этажа. М 1_200.                   |  |  |  |  |  | Лист 5     |  |  |  |
|                     |  | Корпуса 1, 2. План 3 этажа. М 1_200.                   |  |  |  |  |  | Лист 6     |  |  |  |
|                     |  | Корпуса 1, 2. План 4 этажа. М 1_200.                   |  |  |  |  |  | Лист 7     |  |  |  |
|                     |  | Корпуса 1, 2. План 5 этажа. М 1_200.                   |  |  |  |  |  | Лист 8     |  |  |  |
|                     |  | Корпуса 1, 2. План 6 этажа. М 1_200.                   |  |  |  |  |  | Лист 9     |  |  |  |
|                     |  | Корпуса 1, 2. План кровли. М 1_200.                    |  |  |  |  |  | Лист 10    |  |  |  |
|                     |  | Корпуса 3, 3.1. План 1 этажа. М 1_200.                 |  |  |  |  |  | Лист 11    |  |  |  |
|                     |  | Корпуса 3, 3.1. План 2 этажа. М 1_200.                 |  |  |  |  |  | Лист 12    |  |  |  |
|                     |  | Корпуса 3, 3.1. План 3 этажа. М 1_200.                 |  |  |  |  |  | Лист 13    |  |  |  |
|                     |  | Корпуса 3, 3.1. План 4 этажа. М 1_200.                 |  |  |  |  |  | Лист 14    |  |  |  |
|                     |  | Корпуса 3, 3.1. План 5 этажа. М 1_200.                 |  |  |  |  |  | Лист 15    |  |  |  |
|                     |  | Корпуса 3, 3.1. План кровли. М 1_200.                  |  |  |  |  |  | Лист 16    |  |  |  |
|                     |  | Корпус 4. План 1 этажа. М 1_200.                       |  |  |  |  |  | Лист 17    |  |  |  |
|                     |  | Корпус 4. План 2 этажа. М 1_200.                       |  |  |  |  |  | Лист 18    |  |  |  |
|                     |  | Корпус 4. План 3-15 этажей. М 1_200.                   |  |  |  |  |  | Лист 19    |  |  |  |
|                     |  | Корпус 4. План 16 этажа. М 1_200.                      |  |  |  |  |  | Лист 20    |  |  |  |
|                     |  | Корпус 4. План кровли. М 1_200.                        |  |  |  |  |  | Лист 21    |  |  |  |
|                     |  | Типы конструкций                                       |  |  |  |  |  | Лист 22    |  |  |  |
|                     |  |                                                        |  |  |  |  |  |            |  |  |  |
|                     |  |                                                        |  |  |  |  |  |            |  |  |  |
## СПРАВКА О СОБЛЮДЕНИИ ДЕЙСТВУЮЩИХ НОРМАТИВОВ.

Технические решения, принятые в проекте, соответствуют государственным нормативам, правилам, стандартам, исходным данным, а также техническим условиям и требованиям, выданным органами государственного надзора (контроля) и заинтересованными организациями при соблюдении исходно-разрешительной документации, а также нормам пожаро- и взрывобезопасности эксплуатации объекта и нормам защиты населения и устойчивости объекта в чрезвычайных ситуациях.

Гл. архитектор проекта

Добрякова А.В.

|      |         |      |        |       |      |                        |      |
|------|---------|------|--------|-------|------|------------------------|------|
|      |         |      |        |       |      | Справка о соответствии | Лист |
|      |         |      |        |       |      |                        | 2    |
| Изм. | Кол.уч. | Лист | № док. | Подп. | Дата |                        |      |



А. ОПИСАНИЕ И ОБОСНОВАНИЕ ВНЕШНЕГО И ВНУТРЕННЕГО ВИДА ОБЪЕКТА КАПИТАЛЬНОГО СТРОИТЕЛЬСТВА, ЕГО ПРОСТРАНСТВЕННОЙ, ПЛАНИРОВОЧНОЙ И ФУНКЦИОНАЛЬНОЙ ОРГАНИЗАЦИИ;

А.1. ОПИСАНИЕ ОБЪЕКТА

Проект имеет положительное заключение экспертизы №77-2-1-3-047721-2024 от 19.08.2024

Основанием данной корректировки является поручение Заказчика

- Дополнительное соглашение №3 к договору АА/БЭ-03 от 24.05.2024г
- Выписка из протокола ГЗК №37 от 1 декабря 2023г об изменении в правила землепользования и застройки города Москвы в отношении территории по адресу: Садовническая ул., влд. 76/71, земельный участок 65/2, влд. 65, стр.3 (кадастровые №№ 77:01:0002014:6383, 77:01:0002014:47, 77:01:0002014:9).

Целью корректировки является приведение проектной документации Раздела 3 «Архитектурные решения» объекта «Жилой комплекс, расположенный по адресу: г. Москва, ЦАО, Садовническая ул., влд. 76/71» в соответствии с требованиями дополнительного соглашения №3.

Корректировка выполняется в 2 этапа отдельными проектами.

- этап 1 – увеличение этажности корпуса 4 с 10 до 16 этажей, корректировка планировочных решений в соответствии требованиями дополнительного соглашения №3 и согласованными АПР;
- этап 2 – размещение отдельностоящего одноэтажного здания с расположением объекта общественного питания и БКТ.

В представленном комплекте ПД предусмотрены решения по 1-му этапу. Разработка проектных решений по 2 этапу выполняется отдельным Проектом.

Участок проектирования жилого комплекса расположен по адресу: г. Москва, ЦАО, Садовническая ул., влд. 76/71. Территория состоит из участка с кадастровым номером 77:01:0002014:6383 площадью 0,8391 га. Территория жилого комплекса расположена в центре города, в юго-восточной части «острова», образованного Москвой-рекой и Водоотводным каналом. Участок ограничен с востока Садовнической улицей, с запада Садовнической набережной, с севера и с юга – существующей застройкой, расположенной между Комиссариатским и Садовническим переулками. Станция метрополитена – Новокузнецкая – находится в 1300 метрах от территории комплекса в направлении на северо-запад, в юго-западном направлении располагается метро Павелецкая в 1100м от объекта.

|            |           |      |        |       |       |                       |        |        |
|------------|-----------|------|--------|-------|-------|-----------------------|--------|--------|
|            |           |      |        |       |       | АА/БЭ-03-ДС3-АР1      |        |        |
| Изм.       | Кол.уч    | Лист | № док. | Подп. | Дата  |                       |        |        |
| Разработал | Добрякова |      |        |       | 08.24 | Пояснительная записка | Стадия | Лист   |
| Проверил   | КИМ       |      |        |       | 08.24 |                       | П      | 1      |
|            |           |      |        |       |       |                       |        | Листов |
|            |           |      |        |       |       |                       |        | 19     |
| ГИП        | Остроумов |      |        |       | 08.24 |                       | ARTEL  |        |



Градостроительная посадка комплекса обусловлена формой участка, линиями градостроительного регулирования и функциональным назначением объекта. Без изменений, в соответствии с согласованным проектным решением (Заключение экспертизы №77-2-1-3-047721-2024 от 19.08.2024)

Класс функциональной пожарной опасности жилых корпусов 1,2, 3.1 и 4 принят Ф1.3. Класс функциональной пожарной опасности корпуса 3 принят Ф1.4.

За условную отметку 0.000 принята отметка чистого пола вестибюлей первого этажа 1-го корпуса, что соответствует абсолютной отметке:  $0.000 = 123,20$

ПОДЗЕМНАЯ ЧАСТЬ ЗДАНИЯ - без изменений, в соответствии с согласованным проектным решением (Заключение экспертизы №77-2-1-3-047721-2024 от 19.08.2024)

Подземная часть жилого комплекса имеет два этажа и техническое пространство.

В подземных этажах на отм. -6,000 и -9,600 расположена отапливаемая двухуровневая автостоянка, предназначенная для манежного хранения легковых автомобилей. В объеме подземных этажей размещены следующие помещения: электрощитовые, ГРЩ, трансформаторные, венткамеры общеобменной и противодымной вентиляции, помещения ИТП, водомерного узла, насосной ХВС и ПВП, насосной АПТ, хладоцентр, помещения временного хранения ТБО, кладовые жильцов, помещения уборочной техники, помещение для водителей, с/у, лестничные клетки и лифтовые холлы. Высота помещений для хранения автомобилей предусмотрена не ниже 2,4 м до низа выступающих конструкций.

Предусмотрена возможность въезда на -1 этаж автостоянки малотоннажного грузового автотранспорта: автомобили типа ГАЗель NEXT (или аналог) в зоне ЛЛУ для погрузки-разгрузки вещей и материалов жителей комплекса. В указанной зоне предусмотрены проезды высотой 3м.

Въезд и выезд в подземную автостоянку осуществляется с уровня земли со стороны ул. Садовническая по двупутной изолированной рампе в осях 6А/6Б - 30. Продольный уклон на прямолинейных проезжих частях рампы – 5-18%, ширина проезжих частей не менее 3,5м. На границах проезжей части рампы предусматриваются колесоотбойные устройства. В начале и конце рампы предусмотрены водосборные лотки. Также лотки и приемки для сбора воды предусмотрены в зоне хранения автомобилей. Все лотки и приемки закрыты решетками.

Предусмотрен въезд на -1 этаж автостоянки и подъезд к трансформаторным подстанциям, расположенным на -1 этаже. В указанной зоне предусмотрены проезды высотой не менее 2,8м.

Автостоянка предназначена для хранения легковых автомобилей с двигателями внутреннего сгорания, работающими на жидком моторном топливе. Хранение и зарядка электромобилей в автостоянке не предусматривается.

Запрещается хранение автомобилей, работающих на сжатом природном или сжиженном нефтяном газе.

Технологические решения подземной автостоянки подробно описаны в Разделе «Технологические решения».





этажа запроектированы террасы квартир, образованные нависающей частью второго этажа. Отметки входов/выходов первого этажа решены в одном уровне с выходом непосредственно на рельеф. Крыльца отсутствуют. Входы защищены от осадков нависающей частью верхних этажей. Для предотвращения попадания осадков в помещения первого этажа вертикальная планировка земли и отмосток выполнена с учетом уклона от здания в сторону проездов. Входные группы запроектированы без тамбуров с оборудованием воздушно-тепловой завесой. В лестничных клетках на эвакуационных выходах предусмотрено устройство утепленных дверей.

На 2-6 этажах расположены квартиры. Высота (от пола до потолка) 2-3 этажа - 3,15м, для 4-6 этажей – 3,3м. Для квартир, расположенных на 6 этаже, запроектированы террасы.

Количество квартир на этаже в каждой секции корпуса 2 – от 2 до 3 штук. Количество квартир во 2 корпусе – 23 штуки.

Эвакуация из квартир и связь этажей в каждой секции корпуса осуществляется через одну лестничную клетку типа Н2, со входом на этажах (выше первого) из межквартирного коридора, шириной не менее 1,5м. Ширина прохода в лестничной клетке корпуса между поручнем и стеной не менее 1,05м. Стальные ограждения лестничных маршей имеют поручень, непрерывный по всей высоте лестницы. Высота установки поручня 900мм. Ширина межквартирного коридора перед лифтами при однорядном расположении с глубиной кабины 1100мм – не менее 1,5м.

Эвакуация из помещений первого этажа осуществляется непосредственно или через смежные помещения наружу.

Корпус 3 - без изменений, в соответствии с согласованным проектным решением (Заключение экспертизы №77-2-1-3-047721-2024 от 19.08.2024)

Корпус 3, расположен по границе участка вдоль Садовнической улицы. Проектом предусматривается реконструкция существующего 1-2-х этажного здания по адресу: Садовническая ул., д 76/71 стр. 1 (часть 1) с целью размещения в нем жилого корпуса. Мероприятия по реконструкции подробно представлены в Разделе 4 «Конструктивные и объемно-планировочные решения». Этажность корпуса – 1- 2 этажа. В корпусе размещены 4 двухэтажных таунхауса с обособленными входами со стороны улицы. Высота (от пола до потолка) 1 этажа - 3,59м, для 2 этажа – от 3м до 6,9м. Отметка первого этажа принята выше уровня прилегающего благоустройства. При входах организованы крыльца, защищенные от осадков нависающей частью верхнего этажа.

В одноэтажном объеме 3 корпуса размещен въезд на рампу подземной автостоянки и помещение охраны.

Эвакуация из помещений таунхаусов осуществляется непосредственно наружу.

Корпус 3.1.

Корпус 3.1 (сделана перепланировка квартир и уменьшено их количество, в соответствии с согласованным проектным решением), расположен вдоль северной границы участка. Этажность корпуса - 5 этажей. В корпусе предусмотрен лестнично-лифтовой узел с двумя лифтами и лестничной клеткой со входом в нее из вестибюля (1 этаж) или межквартирного коридора (жилые этажи).







Корпус 2 (вертикальный транспорт - без изменений, в соответствии с согласованным проектным решением (Заключение экспертизы №77-2-1-3-047721-2024 от 19.08.2024):

Лифт Лф2.1 – скорость не менее 1,0 м/с, грузоподъемностью 450кг с кабиной 950 х 1050мм (ш х г). Обслуживает два подземных уровня автостоянки и наземные этажи с 1 по 6. Количество остановок 8. Ширина двери 800мм.

Лифт Лф2.2 - скорость не менее 1,0 м/с, грузоподъемностью 1000кг с режимом для перевозки пожарных подразделений и МГН, с кабиной 2100 х 1100мм (ш х г). Обслуживает два подземных уровня автостоянки и наземные этажи с 1 по 6. Количество остановок 8. Ширина двери 1200мм.

Лифт Лф2.3 – скорость не менее 1,0 м/с, грузоподъемностью 450кг с кабиной 950 х 1050мм (ш х г). Обслуживает два подземных уровня автостоянки и наземные этажи с 1 по 5. Количество остановок 7. Ширина двери 800мм.

Лифт Лф2.4 - скорость не менее 1,0 м/с, грузоподъемностью 1000кг с режимом для перевозки пожарных подразделений и МГН, с кабиной 2100 х 1100мм (ш х г). Обслуживает два подземных уровня автостоянки и наземные этажи с 1 по 5. Количество остановок 7. Ширина двери 1200мм.

Корпус 3\_таунхаусы (вертикальный транспорт - без изменений, в соответствии с согласованным проектным решением (Заключение экспертизы №77-2-1-3-047721-2024 от 19.08.2024):

Лифт Лф3.1 – скорость не менее 1,0 м/с, грузоподъемностью 630кг с кабиной 1100 х 1400мм (ш х г). Обслуживает первый подземный уровень автостоянки и первый этаж. Количество остановок 2. Ширина двери 900мм.

Лифт Лф3.2 - скорость не менее 1,0 м/с, грузоподъемностью 630кг с кабиной 1100 х 1400мм (ш х г). Обслуживает первый подземный уровень автостоянки и наземные этажи с 1 по 2. Количество остановок 3. Ширина двери 900мм.

Лифт Лф3.3 - скорость не менее 1,0 м/с, грузоподъемностью 630кг с проходной кабиной 1100 х 1300мм (ш х г). Обслуживает первый подземный уровень автостоянки и наземные этажи с 1 по 2. Количество остановок 3. Ширина двери 900мм.

Корпус 3.1 (вертикальный транспорт - без изменений, в соответствии с согласованным проектным решением (Заключение экспертизы №77-2-1-3-047721-2024 от 19.08.2024):

Лифт Лф3.4 – скорость не менее 1,0 м/с, грузоподъемностью 450кг с кабиной 950 х 1050мм (ш х г). Обслуживает два подземных уровня автостоянки и наземные этажи с 1 по 5. Количество остановок 7. Ширина двери 800мм.

Лифт Лф3.5 - скорость не менее 1,0 м/с, грузоподъемностью 1000кг с режимом для перевозки пожарных подразделений и МГН, с кабиной 2100 х 1100мм (ш х г). Обслуживает два подземных уровня автостоянки и наземные этажи с 1 по 5. Количество остановок 7. Ширина двери 1200мм.

Корпус 4 (вертикальный транспорт – изменилось количество остановок, в соответствии с согласованным проектным решением):

Лифт Лф4.1 - скорость не менее 1,0 м/с, грузоподъемностью 1000кг с режимом для перевозки пожарных подразделений и МГН, с кабиной 1100 х 2100мм (ш х г). Обслуживает два подземных уровня автостоянки и наземные этажи с 1 по 16. Количество остановок 18. Ширина двери 900мм.

Лифт Лф4.2 – скорость не менее 1,0 м/с, грузоподъемностью 630кг с кабиной 1100 х 1400мм (ш х г). Обслуживает два подземных уровня автостоянки и наземные этажи с 1 по 16. Количество остановок 18. Ширина двери 900мм.

В каждой секции корпусов 1, 2, 3.1 и 4 на каждом этаже наземной части предусмотрена одна лестница типа Н2. На всех этажах выше первого в корпусах 1, 2 и 3.1 запроектирована зона безопасности МГН в объеме лестницы Н2, в корпусе 4 зона безопасности МГН расположена в объеме лифтового холла. Конструкции лестниц - марши и площадки – запроектированы из монолитного железобетона.

Лестничные марши и площадки внутренних лестниц имеют высоту ограждений 900мм. Выход на кровлю осуществляется через люк в габаритах минимум 0,8 х 1,0м из лестничной клетки каждой секции, за исключением корпуса 3. Выходы из эвакуационных лестничных клеток защищены нависающей частью верхних этажей или козырьками из защитного многослойного стекла.

А.3. СТЕНЫ И ПЕРЕГОРОДКИ - без изменений, в соответствии с согласованным проектным решением (Заключение экспертизы №77-2-1-3-047721-2024 от 19.08.2024)

Перегородки между квартирами, между квартирами и МОП, между помещениями общего назначения и МОП запроектированы из бетонных стеновых камней типа Полигран 190 ПГ толщиной 190мм с соблюдением требований по шумоизоляции.

Перегородки коммуникационных шахт, технических помещений, кладовых блоков, помещений МОП, помещений общественного назначения – блоки из ячеистого бетона, толщиной 100 / 150 / 200мм, кирпич 120/250мм. Также для зашивки коммуникационных шахт применяются перегородки из ГСП. Перегородки между кладовыми жильцов внутри блока кладовых выполняются из газобетонных блоков, толщиной 100мм.

Внутриквартирные перегородки не выполняются. Габариты комнат обозначаются условно путем выкраски. Перегородки «мокрых» зон выполняются из пазогребневых блоков толщиной 100мм высотой на высоту одного блока.

Наружные стены для корпусов – монолитный железобетон (толщина в соответствии с разделом «Конструктивные решения») / газобетонные блоки, толщиной 200мм, утеплитель - наружный слой - минераловатные плиты, плотностью 90кг/м<sup>3</sup>, толщина 80мм внутренний слой – минераловатные плиты, плотностью 37кг/м<sup>3</sup>, толщиной 100мм; сертифицированная навесная фасадная система с вентилируемым зазором.

Наружные стены для корпуса 3 – монолитный железобетон (толщина в соответствии с разделом «Конструктивные решения») / газобетонные блоки, толщиной 200мм, утеплитель - минераловатные плиты, плотностью 80-125кг/м<sup>3</sup>, толщина 150мм; кирпичная кладка со штукатуркой и покраской.

По линии отмоксти выполнена отсечка минераловатного утеплителя для исключения намокания пеностеклом в системах отделки фасада.

|      |        |      |        |       |      |                  |      |
|------|--------|------|--------|-------|------|------------------|------|
|      |        |      |        |       |      | АА/БЭ-03-ДС3-АР1 | Лист |
|      |        |      |        |       |      |                  | 10   |
| Изм. | Кол.уч | Лист | № док. | Подп. | Дата |                  |      |

А.4. ДВЕРИ, ВОРОТА - без изменений, в соответствии с согласованным проектным решением (Заключение экспертизы №77-2-1-3-047721-2024 от 19.08.2024)

Наружные дверные блоки – в составе витражных конструкций. Наружные и внутренние стекла витражных дверей – защитное многослойное стекло. Вход в помещение охраны при рампе – дверной блок металлический, утепленный с остеклением. Ворота въезда в подземную автостоянку – рулонные, металлические утепленные, автоматические.

Дверные блоки внутренние в соответствии с назначением помещений. Огнестойкость противопожарных дверей предусмотрена по требованиям СТУ и Раздела «Мероприятия по обеспечению пожарной безопасности».

А.5. ОКНА И ВИТРАЖИ - без изменений, в соответствии с согласованным проектным решением (Заключение экспертизы №77-2-1-3-047721-2024 от 19.08.2024)

Оконные блоки и витражи – алюминиевый профиль с двухкамерным стеклопакетом с мягким селективным покрытием стекла. Открывание поворотно-откидное. Без открывания в местах установки противопожарных блоков, а также на 2-3 этажах второго корпуса по оси 2.Г в осях 13/19. В зоне глухих простенков витражей предусмотрен стеклопакет с непрозрачным заполнением

Вентрешетки воздухозаборных шахт, расположенные на 1 этаже, выполнены из алюминия.

#### А.6. КРОВЛЯ .

Кровля корпуса 1 (без изменений, в соответствии с согласованным проектным решением (Заключение экспертизы №77-2-1-3-047721-2024 от 19.08.2024) на отм +18,900; 22,450 запроектирована неэксплуатируемой, плоской с внутренним водостоком. Защитный слой покрытия кровли выполнен из гравийной засыпки. Выход на кровлю на отм. +18,900 предусмотрен через люк из лестничной клетки с площадки на отм. +16,200 ; выходы на кровлю на отм. +22.450 предусмотрены через люки из лестничных клеток с площадок на отм. +19,800. Суммарная площадь кровли на каждый выход не превышает 1000кв.м. На отм +15,100; +18,900 размещены террасы. Покрытие террас – бетонная тротуарная плитка с засыпкой швов мелким гравием. Для отвода воды с террас, размещенных на отм. +15,100 запроектирован наружный организованный водосток в системе фасада.

Кровля корпуса 2 (без изменений, в соответствии с согласованным проектным решением (Заключение экспертизы №77-2-1-3-047721-2024 от 19.08.2024) на отм +18,850; 22,450 запроектирована неэксплуатируемой, плоской с внутренним водостоком. Защитный слой покрытия кровли выполнен из гравийной засыпки. Выход на кровлю на отм. +18,850 предусмотрен через люк из лестничной клетки с площадки на отм. + 16,200; выход на кровлю на отм. +22.450 предусмотрен через люк из лестничной клетки с площадки на отм. +19,800. Суммарная площадь кровли на каждый выход не превышает 1000кв.м. На отм +18,850 размещена терраса. Покрытие террасы – бетонная тротуарная плитка с засыпкой швов мелким гравием.

Кровля корпуса 3 (без изменений, в соответствии с согласованным проектным решением (Заключение экспертизы №77-2-1-3-047721-2024 от 19.08.2024) в соответствии с проектом и требованием с «Проектом зоны охраны объектов культурного наследия в части изменения гра-

|      |        |      |        |       |      |                  |      |
|------|--------|------|--------|-------|------|------------------|------|
|      |        |      |        |       |      | АА/БЭ-03-ДС3-АР1 | Лист |
|      |        |      |        |       |      |                  | 11   |
| Изм. | Кол.уч | Лист | № док. | Подп. | Дата |                  |      |

ниц объединенной охранной зоны №84 и установления требований к градостроительным регламентам в зонах охраны объектов культурного наследия на части квартала №350 ЦАО г. Москвы» - вальмовая, с уклоном кровли не превышающим 30°. Отм. верха конька + 12,200 (абсолютная отметка 135.400, что не превышает абсолютную отметку, указанную в требованиях «Проекта охранной зоны.....» 135,700м). Для отвода воды запроектирован наружный организованный водосток. Участок плоской кровли расположен со стороны примыкающего корпуса 3.1 на отм. +8,000. Для отвода воды с плоской кровли запроектирован наружный организованный водосток. На отм. +4,350; +8,000 размещаются террасы. Покрытие террас - бетонная тротуарная плитка с засыпкой швов мелким гравием.

Кровля корпуса 3.1 (без изменений, в соответствии с согласованным проектным решением (Заключение экспертизы №77-2-1-3-047721-2024 от 19.08.2024) на отм +19,150 запроектирована неэксплуатируемой, плоской с внутренним водостоком. Защитный слой покрытия кровли выполнен из гравийной засыпки. Выход на кровлю предусмотрен через люк из лестничной клетки с площадки на отм. + 16,950. Площадь кровли не превышает 1000 кв.м. На отм +15,600 размещена терраса. Покрытие террасы – бетонная тротуарная плитка с засыпкой швов мелким гравием. Для отвода воды с террасы запроектирован наружный организованный водосток.

Кровля корпуса 4 на отм. +54,950 запроектирована неэксплуатируемой, плоской с внутренним водостоком. Защитный слой покрытия кровли выполнен из гравийной засыпки. Выход на кровлю предусмотрен через люк из лестничной клетки с площадки на отм. +52,350. Площадь кровли не превышает 1000 кв.м. На отм. +51,000 размещены террасы. Покрытие террасы – бетонная тротуарная плитка с засыпкой швов мелким гравием. Для отвода воды с террас запроектирован наружный организованный водосток.

Кровля рампы (без изменений, в соответствии с согласованным проектным решением (Заключение экспертизы №77-2-1-3-047721-2024 от 19.08.2024) на отм. +4,350 запроектирована с внутренним водостоком далее по уклону. Наклонный участок кровли озелененный, с наружным водостоком. На горизонтальном участке кровли размещена терраса. Покрытие террасы – бетонная тротуарная плитка с засыпкой швов мелким гравием.

Высота ограждений основных кровель, террас – 1200мм.

**А.7. ОСНОВНЫЕ МЕРОПРИЯТИЯ ПО ЗАЩИТЕ ОТ ГРЫЗУНОВ, СИНАТРОПНЫХ ЧЛЕНИСТОНОГИХ** - без изменений, в соответствии с согласованным проектным решением (Заключение экспертизы №77-2-1-3-047721-2024 от 19.08.2024)

Для защиты от грызунов жилых, общественных и технических помещений предусмотрено:

- Применение для изготовления порогов и нижней части входных дверей на высоту не менее 50см материалов, устойчивых к повреждению грызунами (металлические двери, металлические накладки на ПВХ и деревянные двери);
- Использование доводчиков на дверях, обеспечивающих самостоятельное закрывание;
- Устройство металлической сетки (решетки) в местах прохода инженерных коммуникаций, выхода вентиляционных отверстий, стока воды;

Исключения возможности проникновения грызунов в свободное пространство при отделке стен гипсокартонными плитами и другими материалами, монтаже подвесных потолков.

Эксплуатирующая организация после завершения строительства может дополнительно установить отпугивающие ультразвуковые устройства. Также при эксплуатации комплекса следует соблюдать следующие меры:

- Своевременный ремонт отмосток, дверных, оконных проемов, мест прохождения коммуникаций в стенах, перекрытиях, ограждениях.

Для защиты от синантропных членистоногих жилых, общественных и технических помещений предусмотрена герметизация швов и стыков плит и межэтажных перекрытий, мест ввода и прохождения электропроводки, санитарно-технических и других коммуникаций через перекрытия, стены и другие ограждения, мест стыковки вентиляционных блоков.

В соответствии с Заданием на проектирование мусоропровод жилого комплекса не предусмотрен.

Б. ОБОСНОВАНИЕ ПРИНЯТЫХ ОБЪЕМНО-ПРОСТРАНСТВЕННЫХ И АРХИТЕКТУРНО ХУДОЖЕСТВЕННЫХ РЕШЕНИЙ, В ТОМ ЧИСЛЕ СОБЛЮДЕНИЯ ПРЕДЕЛЬНЫХ ПАРАМЕТРОВ РАЗРЕШЕННОГО СТРОИТЕЛЬСТВА ОБЪЕКТА КАПИТАЛЬНОГО СТРОИТЕЛЬСТВА - без изменений, в соответствии с согласованным проектным решением (Заключение экспертизы №77-2-1-3-047721-2024 от 19.08.2024)

Проект «Жилого комплекса» по адресу: г. Москва, ЦАО, Садовническая ул., вл 76/71 разработан на основании:

- Договора АА/БЭ-03-ДС3;
- Градостроительного плана земельного участка, утвержденного в установленном порядке;
- Проектом зоны охраны объектов культурного наследия в части изменения границ объединенной охранной зоны №84 и установления требований к градостроительным регламентам в зонах охраны объектов культурного наследия на части квартала №350 ЦАО г. Москвы;
- Задания на проектирование, утвержденного в установленном порядке;
- Архитектурной концепцией, согласованной Заказчиком.

Проектные решения разработаны и запроектированы в соответствии с требованиями технических регламентов, а также действующих нормативных документов, включенных в перечень национальных стандартов, обеспечивающих требования №384-ФЗ от 30.12.2009, но не ограничиваясь:

- СП 54.13330.2016 «Здания жилые многоквартирные»
- СП 50.13330.2012 «Тепловая защита зданий»
- СП 51.13330.2011 «Защита от шума»
- СП 59.13330.2020 «Доступность зданий и сооружений для маломобильных групп населения»
- СП 113.13330.2016 «Стоянки автомобилей»
- СанПин 1.2.3685-21 «Гигиенические нормативы и требования к обеспечению безопасности и (или) безвредности для человека факторов среды обитания»
- ФЗ №123 – ФЗ «Технический регламент о требованиях пожарной безопасности»

- СТУ на проектирование и строительство, в части обеспечения пожарной безопасности объекта

- СТУ на проектирование и строительство объекта.

Габариты и конфигурация корпусов жилого комплекса определяются из положения зданий в системе застройки с учетом обеспечения инсоляции помещений существующих и проектируемых корпусов в соответствии с действующими нормативами.

Этажность и габариты приняты максимально допустимыми (оптимальными) исходя из:

- экономической эффективности застройки;
- нормативной плотности территории;
- режимом использования земель земельных участков в границах охранных зон;
- геологических условий застраиваемого участка (с учетом несущей способности грунтов).

Максимальная высота по объекту 56,4м, суммарная поэтажная площадь в габаритах наружных стен по проекту (в рамках 1-го этапа) – 30 765м<sup>2</sup>. Проектные показатели не превышают соответствующих требований **Градостроительного плана земельного участка**, утвержденного в установленном порядке. Предельная высота объекта по ГПЗУ (по протоколу ГЗК) – 59м, суммарная поэтажная площадь в габаритах наружных стен по ГПЗУ – 31 539м<sup>2</sup>.

Б.1. ОБОСНОВАНИЕ ПРИНЯТЫХ АРХИТЕКТУРНЫХ РЕШЕНИЙ В ЧАСТИ ОБЕСПЕЧЕНИЯ СОТВЕТСТВИЯ ЗДАНИЙ, СТРОЕНИЙ И СООРУЖЕНИЙ УСТАНОВЛЕННЫМ ТРЕБОВАНИЯМ ЭНЕРГЕТИЧЕСКОЙ ЭФФЕКТИВНОСТИ (ЗА ИСКЛЮЧЕНИЕМ ЗДАНИЙ, СТРОЕНИЙ, СООРУЖЕНИЙ, НА КОТОРЫЕ ТРЕБОВАНИЯ ЭНЕРГЕТИЧЕСКОЙ ЭФФЕКТИВНОСТИ НЕ РАСПРОСТРАНЯЮТСЯ) - без изменений, в соответствии с согласованным проектным решением (Заключение экспертизы №77-2-1-3-047721-2024 от 19.08.2024)

Проектом предусмотрены следующие мероприятия по обеспечению нормативного уровня тепловой защиты здания:

- Выбор оптимальной формы здания, обеспечивающей минимальные теплопотери в зимний период и минимальные тепlopоступления летний период года;
- Выполнение многослойных наружных стен с эффективным утеплителем. Стены подземной части утеплены на глубину промерзания экструдированным пенополистиролом;
- Применение эффективного утеплителя в составе «пирога» кровли для покрытий корпусов;
- Применение светопрозрачных наружных ограждающих конструкций с повышенными теплозащитными характеристиками;
- На входах в жилые группы комплекса запроектированы тепловые завесы. Все входные двери утепленные;
- Установка доводчиков входных дверей;
- Максимальное использование естественного освещения помещений для снижения затрат электрической энергии.

Б.2. ПЕРЕЧЕНЬ МЕРОПРИЯТИЙ ПО ОБЕСПЕЧЕНИЮ УСТАНОВЛЕННЫХ ТРЕБОВАНИЙ ЭНЕРГЕТИЧЕСКОЙ ЭФФЕКТИВНОСТИ К АРХИТЕКТУРНЫМ РЕШЕНИЯМ, ВЛИЯЮЩИМ НА ЭНЕРГЕТИЧЕСКУЮ ЭФФЕКТИВНОСТЬ ЗДАНИЙ, СТРОЕНИЙ И СООРУЖЕНИЙ (ЗА ИСКЛЮЧЕНИЕМ ЗДАНИЙ, СТРОЕНИЙ, СООРУЖЕНИЙ, НА КОТОРЫЕ ТРЕБОВАНИЯ ЭНЕРГЕТИЧЕСКОЙ ЭФФЕКТИВНОСТИ НЕ РАСПРОСТРАНЯЮТСЯ) - без изменений, в соответствии с согласованным проектным решением (Заключение экспертизы №77-2-1-3-047721-2024 от 19.08.2024)

- Устройство эффективных наружных ограждающих конструкций здания и заполнения световых проемов;
- Автоматическое поддержание давления, необходимого для оптимальной работы санитарно-технических систем;
- Изоляция трубопроводов водоснабжения от потерь;
- Установка приборов учета воды;
- Для освещения холлов, вестибюлей, лестничных клеток используются светильники с энергосберегающими лампами;
- Учет электроэнергии, расходуемой в квартирах, производится с помощью многотарифных счетчиков, что стимулирует потребление электроэнергии в ночное время суток.

В. ОПИСАНИЕ И ОБОСНОВАНИЕ ИСПОЛЬЗОВАННЫХ КОМПОЗИЦИОННЫХ ПРИЕМОВ ПРИ ОФОРМЛЕНИИ ФАСАДОВ И ИНТЕРЬЕРОВ ОБЪЕКТА КАПИТАЛЬНОГО СТРОИТЕЛЬСТВА - без изменений, в соответствии с согласованным проектным решением (Заключение экспертизы №77-2-1-3-047721-2024 от 19.08.2024)

Фасады корпусов 1, 2, 3.1 и 4 решены в едином современном стиле. Вертикальные чередующиеся пилоны разной геометрии корпусов 1 и 2 формируют глубокие оконные откосы. Для сохранения архитектурно-градостроительного облика Садовнической набережной 5 и 6 этажи корпуса 1 заглублены от линии улицы. Фасадное решение Корпуса 3 предусматривает сохранение композиции главного уличного фасада, в формах эклектики конца XIX в. При воссоздании исторического облика доходного дома XIX века, использованы архивные материалы внешнего вида исторического фасада, с применением современных материалов.

Наружная отделка фасадов:

- Отделка цоколя – облицовка натуральным камнем в системе вентилируемого фасада / облицовка натуральным камнем на растворе;
- Наземная часть корпуса 1 и 2 – наружные стены – облицовка плиты из натурального облицовочного камня в составе сертифицированной навесной фасадной системы. Ветрозащита утеплителя в системе вентилируемого фасада не предусматривается. Декоративные элементы выполнены из плит натурального бучардированного облицовочного камня в соответствии с фасадным решением. Откосы оконных и витражных конструкций в материале фасада – натуральный камень. В зоне глухих простенков витражей предусмотрен стеклопакет с непрозрачным заполнением. Отдельные элементы в соответствии с фасадным решением - композитные панели.;





Г. ОПИСАНИЕ РЕШЕНИЙ ПО ОТДЕЛКЕ ПОМЕЩЕНИЙ ОСНОВНОГО, ВСПОМОГАТЕЛЬНОГО, ОБСЛУЖИВАЮЩЕГО И ТЕХНИЧЕСКОГО НАЗНАЧЕНИЯ - без изменений, в соответствии с согласованным проектным решением (Заключение экспертизы №77-2-1-3-047721-2024 от 19.08.2024)

Материалы отделки приняты в соответствии с функциональным назначением помещения, с учетом требования противопожарных норм проектирования, СТУ. Все применяемые материалы для отделки помещений соответствуют требованиям Федерального закона от 22.07.2008 №123-ФЗ «Технический регламент о требованиях пожарной безопасности в редакции от 10.07.2012., имеют действующие «Сертификаты соответствия нормам Российской Федерации» и Санитарно-эпидемиологические заключения о возможности применения данных материалов в жилых зданиях.

Для сдачи комплекса в эксплуатацию предусматривается отделка следующих помещений (по отдельному дизайн-проекту):

- МОПы (лестничные клетки, вестибюли, лифтовые холлы, коридоры наземных этажей)
- Силами и средствами собственников предусматривается отделка следующих помещений:
- Квартиры, таунхаусы;
  - Кладовые жильцов;
  - Помещения общего назначения.

В соответствии с требованиями №123-ФЗ от 22.07.2008г., класс пожарной опасности отделочных материалов помещений не более указанного в Таблицах 28, 29 и пожарных СТУ.

Описание отделочных материалов по типам помещений:

Технические помещения (венткамеры, электрощитовые, помещения СС, ИТП, узел ввода, хладоцентр и т.п), коридоры блоков кладовых жильцов:

- полы – керамогранит с шероховатой поверхностью не допускающий скольжения/фальшпол при необходимости/обеспыливающее покрытие по цементно-песчаной стяжке;
- стены, потолки – улучшенная покраска воднодисперсионной краской;

Помещение хранения автомобилей, рампа:

- полы – бетонное основание со сверхпрочным непылящим покрытием типа LEVEL Top-Q; для рампы – 2 слоя эпоксидной смолы QTR с засыпкой кварцевым песком;
- стены, потолки – улучшенная покраска воднодисперсионной краской.

Техническое пространство для прокладки инженерных коммуникаций:

- полы – обеспыливающее покрытие по цементно-песчаной стяжке и/или монолитному железобетону
- стены, потолки – простая покраска воднодисперсионной краской и/или обеспыливающее покрытие

Лестничные клетки:

- полы – керамогранит с шероховатой поверхностью не допускающий скольжения, на ступенях с противоскользящей насечкой;

- стены, потолки – окраска акриловой краской на водной основе.

Вестибюли, лифтовые холлы, межквартирные коридоры (уточняется дизайн-проектом):

- полы – керамогранит с шероховатой поверхностью не допускающий скольжения;
- стены – высококачественная покраска воднодисперсионной краской;
- потолки - высококачественная покраска воднодисперсионной краской/сертифицированные подвесные потолочные системы;

Квартиры, таунхаусы, помещения общего назначения, кладовые жильцов:

- Полы – без отделки / в «мокрых» помещениях гидроизоляция;
- Стены, потолки – без отделки.

Д. ОПИСАНИЕ АРХИТЕКТУРНЫХ РЕШЕНИЙ, ОБЕСПЕЧИВАЮЩИХ ЕСТЕСТВЕННОЕ ОСВЕЩЕНИЕ С ПОСТОЯННЫМ ПРЕБЫВАНИЕМ ЛЮДЕЙ без изменений, в соответствии с согласованным проектным решением (Заключение экспертизы №77-2-1-3-047721-2024 от 19.08.2024)

Жилые комнаты квартир, рабочие комнаты с постоянным пребыванием людей имеют естественное освещение согласно требованиям СанПин 1.2.3685-21. Подробно мероприятия описаны в Разделе «Расчет инсоляции и естественной освещенности».

Е. ОПИСАНИЕ АРХИТЕКТУРНО-СТРОИТЕЛЬНЫХ МЕРОПРИЯТИЙ, ОБЕСПЕЧИВАЮЩИХ ЗАЩИТУ ПОМЕЩЕНИЙ ОТ ШУМА, ВИБРАЦИИ И ДРУГОГО ВОЗДЕЙСТВИЯ без изменений, в соответствии с согласованным проектным решением (Заключение экспертизы №77-2-1-3-047721-2024 от 19.08.2024)

Для снижения структурного шума (вибрации), передаваемого строительным конструкциям здания из помещений с инженерным оборудованием, предусмотрено применение «плавающего пола» в помещениях с источником шума, где оборудование устанавливается на пол. По периметру помещений предусмотрен акустический шов.

Для снижения шума и вибрации от вентиляционного оборудования, устанавливаемого в венткамерах на пол, предусмотрены виброизолирующие основания и устройство гибких вставок между вентиляторами и воздуховодами или вентиляционной камерой. Также предусматривается виброизоляция труб, их крепления в местах первых проходов через строительные конструкции минераловатными матами толщиной 15-20мм. Для виброизоляции оборудования, которое подвешивается к перекрытию (например, канальные вентиляторы), применяются виброизолирующие крепления и подвесы по типу Виброфлекс М8 или аналог.

Лифтовые шахт расположены так, что не примыкают к жилым комнатам квартир и общественным помещениям с постоянным пребыванием людей.

Крепление трубопроводов в сантехнических нишах непосредственно к межквартирным стенам или перегородкам, ограждающим жилые комнаты не предусмотрено.

Холодильное и вентиляционное оборудование, размещаемое на кровле, устанавливается на отдельно стоящие виброгасящие фундаменты под оборудование через вибродемпфирующие прокладки или виброопоры.

|      |        |      |        |       |      |                  |      |
|------|--------|------|--------|-------|------|------------------|------|
|      |        |      |        |       |      | АА/БЭ-03-ДС3-АР1 | Лист |
|      |        |      |        |       |      |                  | 18   |
| Изм. | Кол.уч | Лист | № док. | Подп. | Дата |                  |      |

Подробно мероприятия описаны в Разделе «Перечень мероприятий по охране окружающей среды».

#### Ж. ОПИСАНИЕ РЕШЕНИЙ ПО СВЕТООГРАЖДЕНИЮ ОБЪЕКТА, ОБЕСПЕЧИВАЮЩИХ БЕЗОПАСНОСТЬ ПОЛЕТА ВОЗДУШНЫХ СУДОВ (ПРИ НЕОБХОДИМОСТИ)

Устройство ночного светоограждения выполняется в соответствии с Федеральными авиационными правилами «Размещение маркировочных знаков и устройств на зданиях, сооружениях, линиях связи, линиях электропередачи, радиотехническом оборудовании и других объектах, устанавливаемых в целях обеспечения безопасности полетов воздушных судов» ПРИКАЗ от 28 ноября 2007 года N 119.


Максимальная высота корпуса 4 составляет 56,4м. Согласно РЭГА РФ-94 (п. 3.3.23) предусматривается светоограждение сверху вниз до высоты 45м. При этом в верхних точках препятствий установлено не менее двух заградительных огней, работающих одновременно. В соответствии с Приложением №5 ФАП-119, светомаркировка наносится на все препятствия с установкой огней средней интенсивности тип А. Заградительный огонь средней интенсивности: типа «А» - проблесковый огонь с излучением белого цвета и эффективной интенсивностью 20000/2000 кд. Тип сигнала (частота проблесков) -Проблесков. (20-60 fpm);

#### З. ОПИСАНИЕ РЕШЕНИЙ ПО ДЕКОРАТИВНО-ХУДОЖЕСТВЕННОЙ И ЦВЕТОВОЙ ОТДЕЛКЕ ИНТЕРЬЕРОВ – ДЛЯ ОБЪЕКТОВ НЕПРОИЗВОДСТВЕННОГО ЗНАЧЕНИЯ.


Декоративно-художественная и цветовая отделка мест общего пользования и квартир разрабатывается по отдельному дизайн-проекту.

|      |        |      |        |       |      |                  |      |
|------|--------|------|--------|-------|------|------------------|------|
|      |        |      |        |       |      | АА/БЭ-03-ДС3-АР1 | Лист |
|      |        |      |        |       |      |                  | 19   |
| Изм. | Кол.уч | Лист | № док. | Подп. | Дата |                  |      |



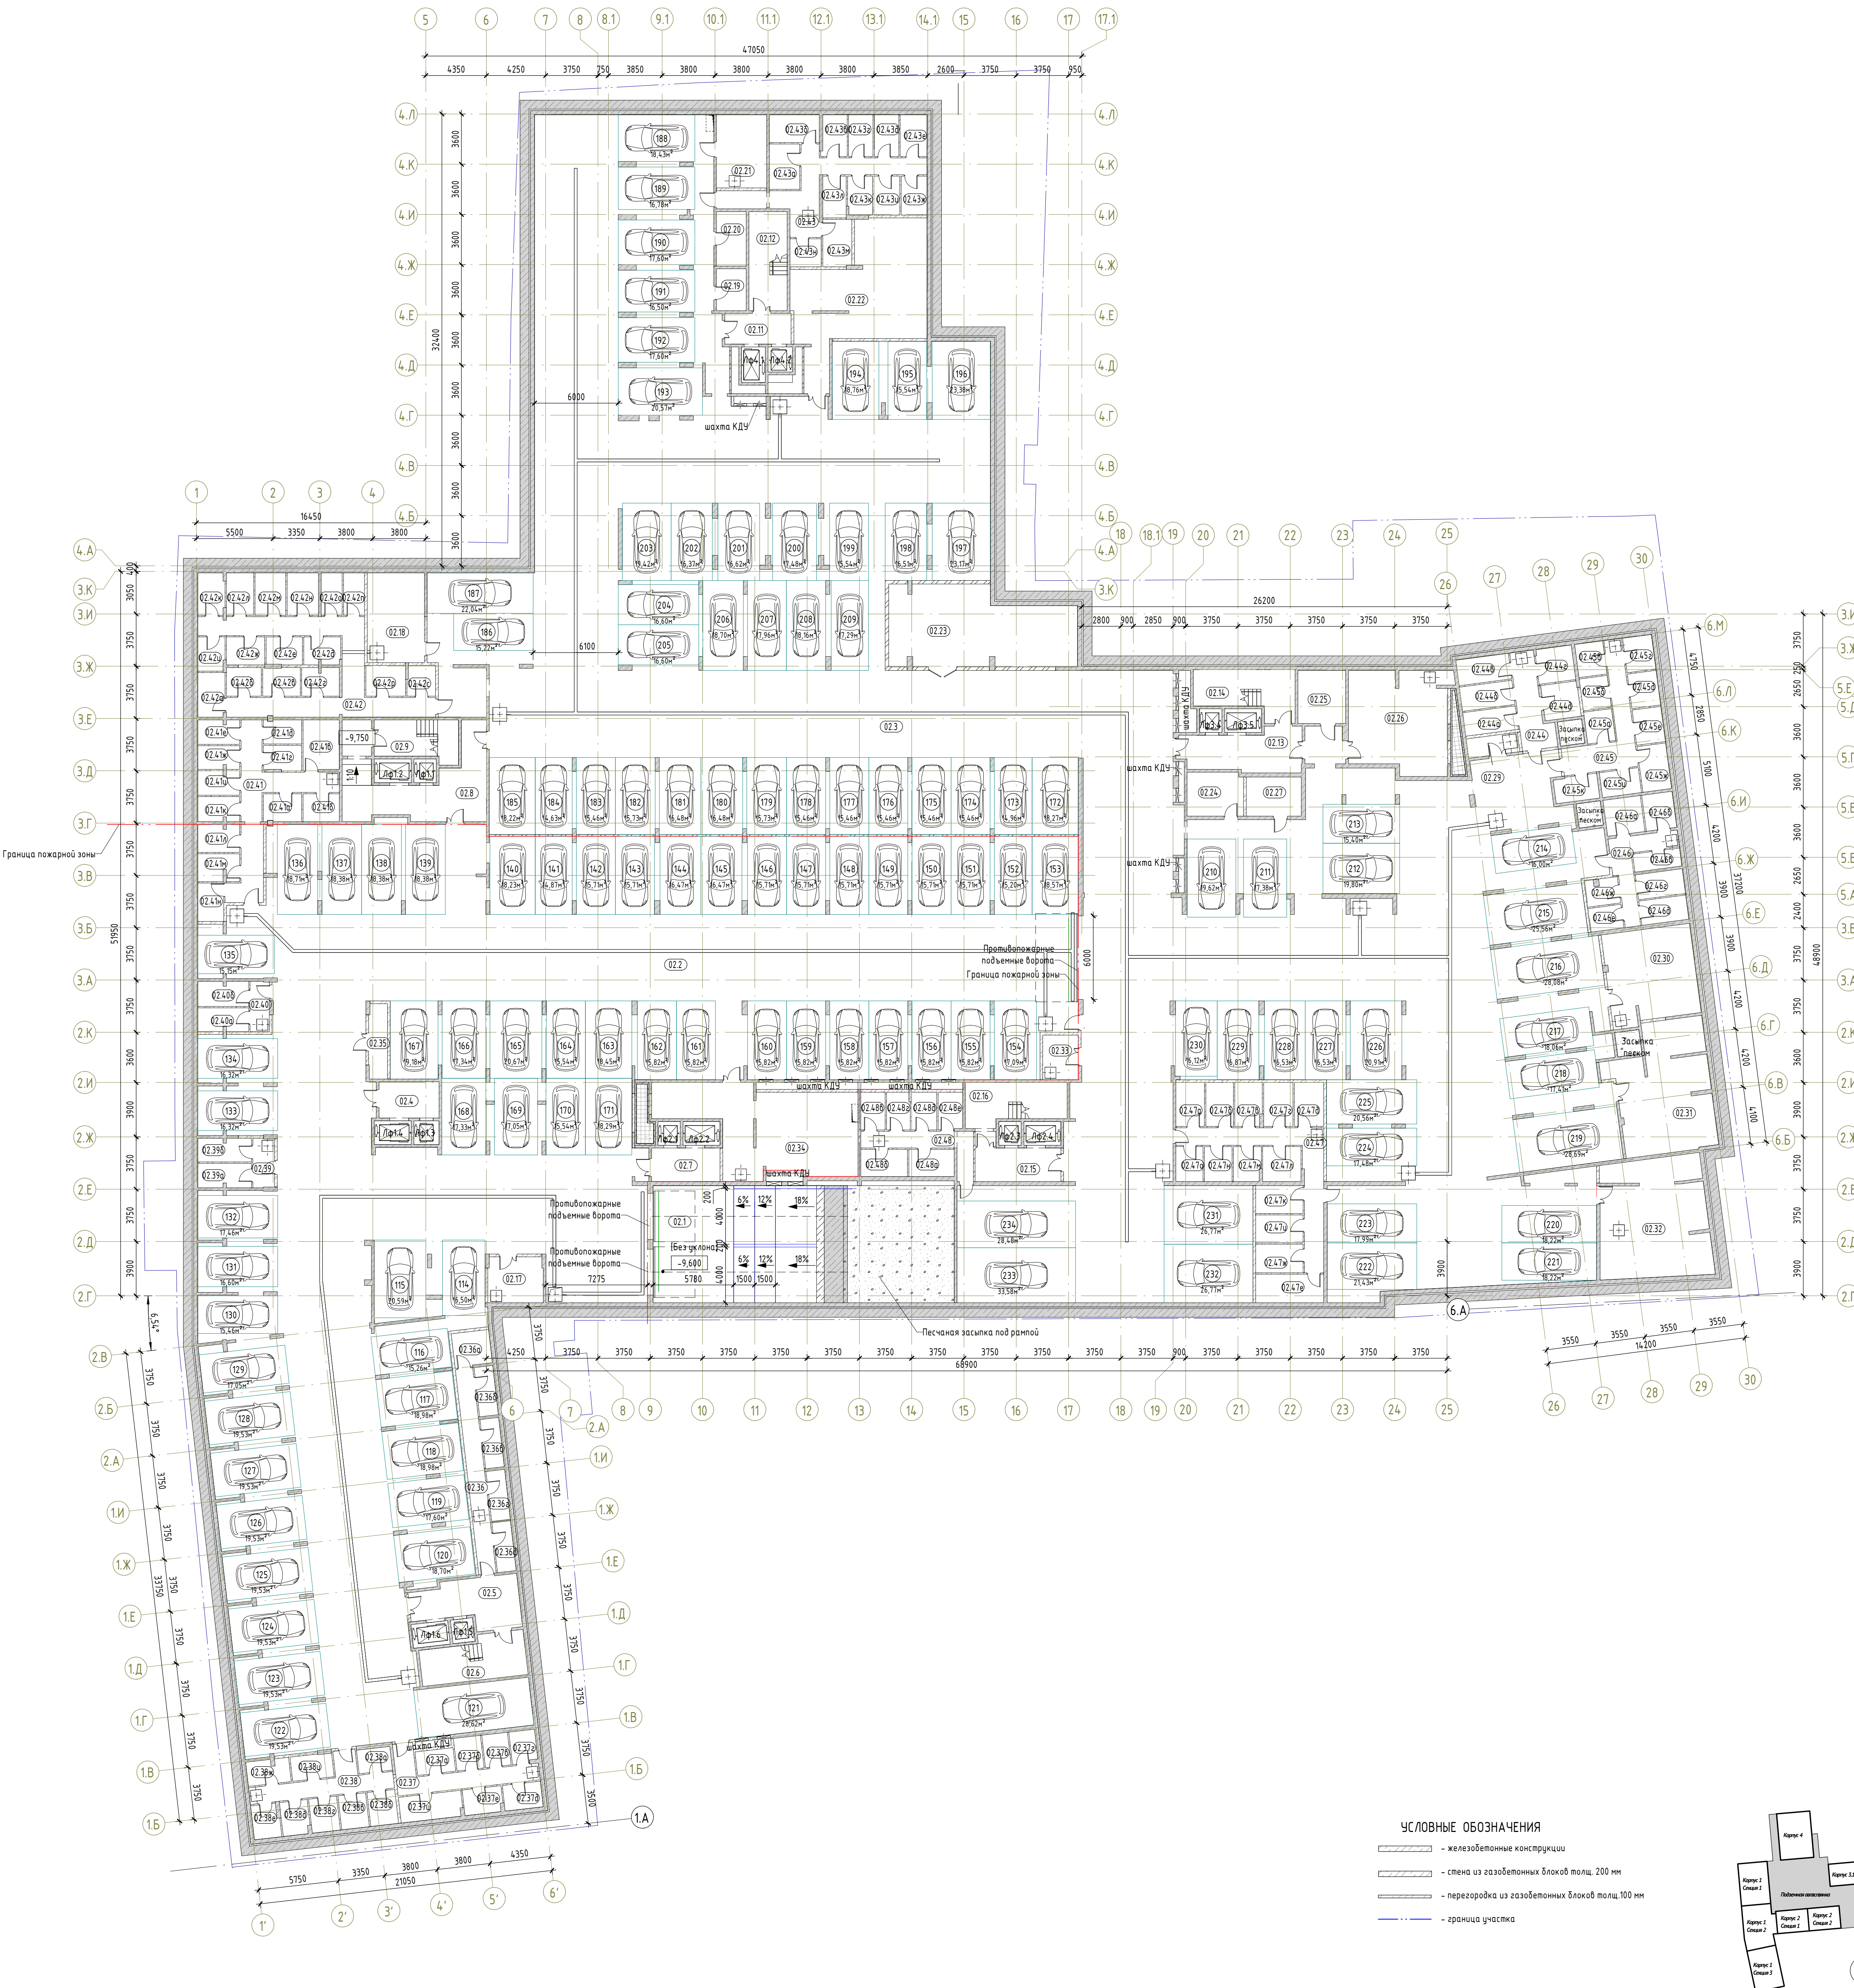


- УСЛОВНЫЕ ОБОЗНАЧЕНИЯ
- железобетонные конструкции
  - стена из газобетонных блоков толщ. 200 мм
  - перегородка из газобетонных блоков толщ. 100 мм
  - граница участка

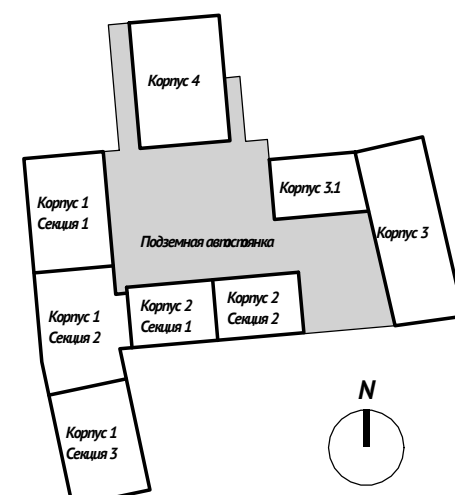


| Экспликация помещений |                                                   |             |                |  |
|-----------------------|---------------------------------------------------|-------------|----------------|--|
| Номер помещения       | Наименование                                      | Площадь, м² | Кат. помещения |  |
| 02.1                  | Рампа                                             | 185,03      | B3             |  |
| 02.2                  | Помещение хранения автомобилей 02.1               | 2019,94     | B2             |  |
| 02.3                  | Помещение хранения автомобилей 02.2               | 2799,81     | B2             |  |
| 02.4                  | Лифтовой холл                                     | 11,18       |                |  |
| 02.5                  | Лифтовой холл                                     | 23,49       |                |  |
| 02.6                  | Лестничная клетка Лп1.3                           | 21,91       |                |  |
| 02.7                  | Лифтовой холл                                     | 11,76       |                |  |
| 02.8                  | Лифтовой холл                                     | 45,68       |                |  |
| 02.9                  | Лестничная клетка Лп1.1                           | 16,48       |                |  |
| 02.11                 | Лифтовой холл                                     | 10,45       |                |  |
| 02.12                 | Лестничная клетка Лп4                             | 19,45       |                |  |
| 02.13                 | Лифтовой холл                                     | 24,34       |                |  |
| 02.14                 | Лестничная клетка Лп3.1                           | 21,73       |                |  |
| 02.15                 | Лифтовой холл                                     | 14,76       |                |  |
| 02.16                 | Лестничная клетка Лп2.2                           | 22,44       |                |  |
| 02.17                 | Помещение хранения уборочной техники              | 12,96       | B3             |  |
| 02.18                 | Помещение тех. учета                              | 26,40       |                |  |
| 02.19                 | Помещение хранения уборочной техники              | 6,39        | B4             |  |
| 02.20                 | Помещение СС                                      | 8,31        |                |  |
| 02.21                 | Венткамера приточная                              | 18,90       | Д              |  |
| 02.22                 | Венткамера вытяжная                               | 73,94       | B3             |  |
| 02.23                 | Техническое помещение - абсорбция трансформаторов | 70,11       |                |  |
| 02.24                 | Помещение СС                                      | 12,64       |                |  |
| 02.25                 | Техническое помещение                             | 13,02       |                |  |
| 02.26                 | Венткамера                                        | 50,82       | Д              |  |
| 02.27                 | Помещение хранения уборочной техники              | 11,06       | B4             |  |
| 02.29                 | Помещение хранения уборочной техники              | 5,18        | B4             |  |
| 02.30                 | Венткамера                                        | 41,73       | Д              |  |
| 02.31                 | Техническое помещение                             | 57,83       |                |  |
| 02.32                 | Венткамера                                        | 64,38       | Д              |  |
| 02.33                 | Помещение хранения уборочной техники              | 8,16        | B4             |  |
| 02.34                 | Венткамера                                        | 72,53       | Д              |  |
| 02.35                 | Помещение хранения уборочной техники              | 7,16        | B4             |  |
| 02.36                 | Коридор                                           | 18,50       |                |  |
| 02.36a                | Кладовая                                          | 6,60        |                |  |
| 02.36b                | Кладовая                                          | 4,79        |                |  |
| 02.36c                | Кладовая                                          | 4,79        |                |  |
| 02.36d                | Кладовая                                          | 4,86        |                |  |
| 02.36e                | Кладовая                                          | 4,86        |                |  |
| 02.37                 | Коридор                                           | 15,93       |                |  |
| 02.37a                | Кладовая                                          | 4,67        |                |  |
| 02.37b                | Кладовая                                          | 4,58        |                |  |
| 02.37c                | Кладовая                                          | 4,35        |                |  |
| 02.37d                | Кладовая                                          | 4,23        |                |  |
| 02.37e                | Кладовая                                          | 5,09        |                |  |
| 02.37f                | Кладовая                                          | 5,06        |                |  |
| 02.37g                | Кладовая                                          | 8,21        |                |  |
| 02.38                 | Коридор                                           | 15,52       |                |  |
| 02.38a                | Кладовая                                          | 4,08        |                |  |
| 02.38b                | Кладовая                                          | 4,90        |                |  |
| 02.38c                | Кладовая                                          | 4,90        |                |  |
| 02.38d                | Кладовая                                          | 4,95        |                |  |
| 02.38e                | Кладовая                                          | 4,78        |                |  |
| 02.38f                | Кладовая                                          | 4,63        |                |  |
| 02.38g                | Кладовая                                          | 5,28        |                |  |
| 02.38h                | Кладовая                                          | 5,20        |                |  |
| 02.39                 | Коридор                                           | 5,42        |                |  |
| 02.39a                | Кладовая                                          | 6,65        |                |  |
| 02.39b                | Кладовая                                          | 6,46        |                |  |
| 02.40                 | Коридор                                           | 4,93        |                |  |
| 02.40a                | Кладовая                                          | 6,11        |                |  |
| 02.40b                | Кладовая                                          | 6,48        |                |  |
| 02.41                 | Коридор                                           | 29,78       |                |  |
| 02.41a                | Кладовая                                          | 5,46        |                |  |
| 02.41b                | Кладовая                                          | 5,20        |                |  |
| 02.41c                | Кладовая                                          | 9,34        |                |  |
| 02.41d                | Кладовая                                          | 4,89        |                |  |
| 02.41e                | Кладовая                                          | 4,70        |                |  |
| 02.41f                | Кладовая                                          | 5,16        |                |  |
| 02.41g                | Кладовая                                          | 5,01        |                |  |
| 02.41h                | Кладовая                                          | 5,16        |                |  |
| 02.41i                | Кладовая                                          | 5,31        |                |  |
| 02.41j                | Кладовая                                          | 5,91        |                |  |
| 02.41k                | Кладовая                                          | 5,78        |                |  |
| 02.41l                | Кладовая                                          | 5,10        |                |  |

| Экспликация помещений |              |             |                |  |
|-----------------------|--------------|-------------|----------------|--|
| Номер помещения       | Наименование | Площадь, м² | Кат. помещения |  |
| 02.42                 | Коридор      | 44,10       |                |  |
| 02.42a                | Кладовая     | 6,18        |                |  |
| 02.42b                | Кладовая     | 5,31        |                |  |
| 02.42c                | Кладовая     | 5,48        |                |  |
| 02.42d                | Кладовая     | 5,46        |                |  |
| 02.42e                | Кладовая     | 5,18        |                |  |
| 02.42f                | Кладовая     | 5,15        |                |  |
| 02.42g                | Кладовая     | 5,49        |                |  |
| 02.42h                | Кладовая     | 4,67        |                |  |
| 02.42i                | Кладовая     | 5,79        |                |  |
| 02.42j                | Кладовая     | 5,95        |                |  |
| 02.42k                | Кладовая     | 6,71        |                |  |
| 02.42l                | Кладовая     | 6,85        |                |  |
| 02.42m                | Кладовая     | 4,57        |                |  |
| 02.42n                | Кладовая     | 4,57        |                |  |
| 02.42o                | Кладовая     | 6,30        |                |  |
| 02.42p                | Кладовая     | 4,43        |                |  |
| 02.43                 | Коридор      | 27,71       |                |  |
| 02.43a                | Кладовая     | 7,05        |                |  |
| 02.43b                | Кладовая     | 7,15        |                |  |
| 02.43c                | Кладовая     | 5,31        |                |  |
| 02.43d                | Кладовая     | 5,25        |                |  |
| 02.43e                | Кладовая     | 5,25        |                |  |
| 02.43f                | Кладовая     | 5,78        |                |  |
| 02.43g                | Кладовая     | 5,18        |                |  |
| 02.43h                | Кладовая     | 5,18        |                |  |
| 02.43i                | Кладовая     | 4,98        |                |  |
| 02.43j                | Кладовая     | 5,03        |                |  |
| 02.43k                | Кладовая     | 7,01        |                |  |
| 02.43l                | Кладовая     | 4,51        |                |  |
| 02.44                 | Коридор      | 13,56       |                |  |
| 02.44a                | Кладовая     | 6,46        |                |  |
| 02.44b                | Кладовая     | 6,65        |                |  |
| 02.44c                | Кладовая     | 7,03        |                |  |
| 02.44d                | Кладовая     | 6,58        |                |  |
| 02.44e                | Кладовая     | 6,61        |                |  |
| 02.44f                | Кладовая     | 19,50       |                |  |
| 02.44g                | Кладовая     | 4,65        |                |  |
| 02.44h                | Кладовая     | 4,65        |                |  |
| 02.44i                | Кладовая     | 4,85        |                |  |
| 02.44j                | Кладовая     | 5,20        |                |  |
| 02.44k                | Кладовая     | 5,20        |                |  |
| 02.44l                | Кладовая     | 5,30        |                |  |
| 02.44m                | Кладовая     | 6,86        |                |  |
| 02.44n                | Кладовая     | 5,08        |                |  |
| 02.44o                | Кладовая     | 5,59        |                |  |
| 02.44p                | Кладовая     | 12,36       |                |  |
| 02.44q                | Кладовая     | 7,02        |                |  |
| 02.44r                | Кладовая     | 5,72        |                |  |
| 02.44s                | Кладовая     | 4,42        |                |  |
| 02.44t                | Кладовая     | 6,12        |                |  |
| 02.44u                | Кладовая     | 5,95        |                |  |
| 02.44v                | Кладовая     | 4,08        |                |  |
| 02.44w                | Кладовая     | 4,36        |                |  |
| 02.44x                | Кладовая     | 26,09       |                |  |
| 02.44y                | Кладовая     | 6,46        |                |  |
| 02.44z                | Кладовая     | 6,22        |                |  |
| 02.45                 | Кладовая     | 6,04        |                |  |
| 02.45a                | Кладовая     | 6,62        |                |  |
| 02.45b                | Кладовая     | 6,61        |                |  |
| 02.45c                | Кладовая     | 9,99        |                |  |
| 02.45d                | Кладовая     | 6,97        |                |  |
| 02.45e                | Кладовая     | 6,80        |                |  |
| 02.45f                | Кладовая     | 6,80        |                |  |
| 02.45g                | Кладовая     | 4,86        |                |  |
| 02.45h                | Кладовая     | 4,94        |                |  |
| 02.45i                | Кладовая     | 4,87        |                |  |
| 02.45j                | Кладовая     | 12,53       |                |  |
| 02.45k                | Кладовая     | 6,34        |                |  |
| 02.45l                | Кладовая     | 6,53        |                |  |
| 02.45m                | Кладовая     | 4,73        |                |  |
| 02.45n                | Кладовая     | 4,52        |                |  |
| 02.45o                | Кладовая     | 4,86        |                |  |
| 02.45p                | Кладовая     | 4,67        |                |  |
| 02.45q                | Кладовая     | 6639,07     |                |  |



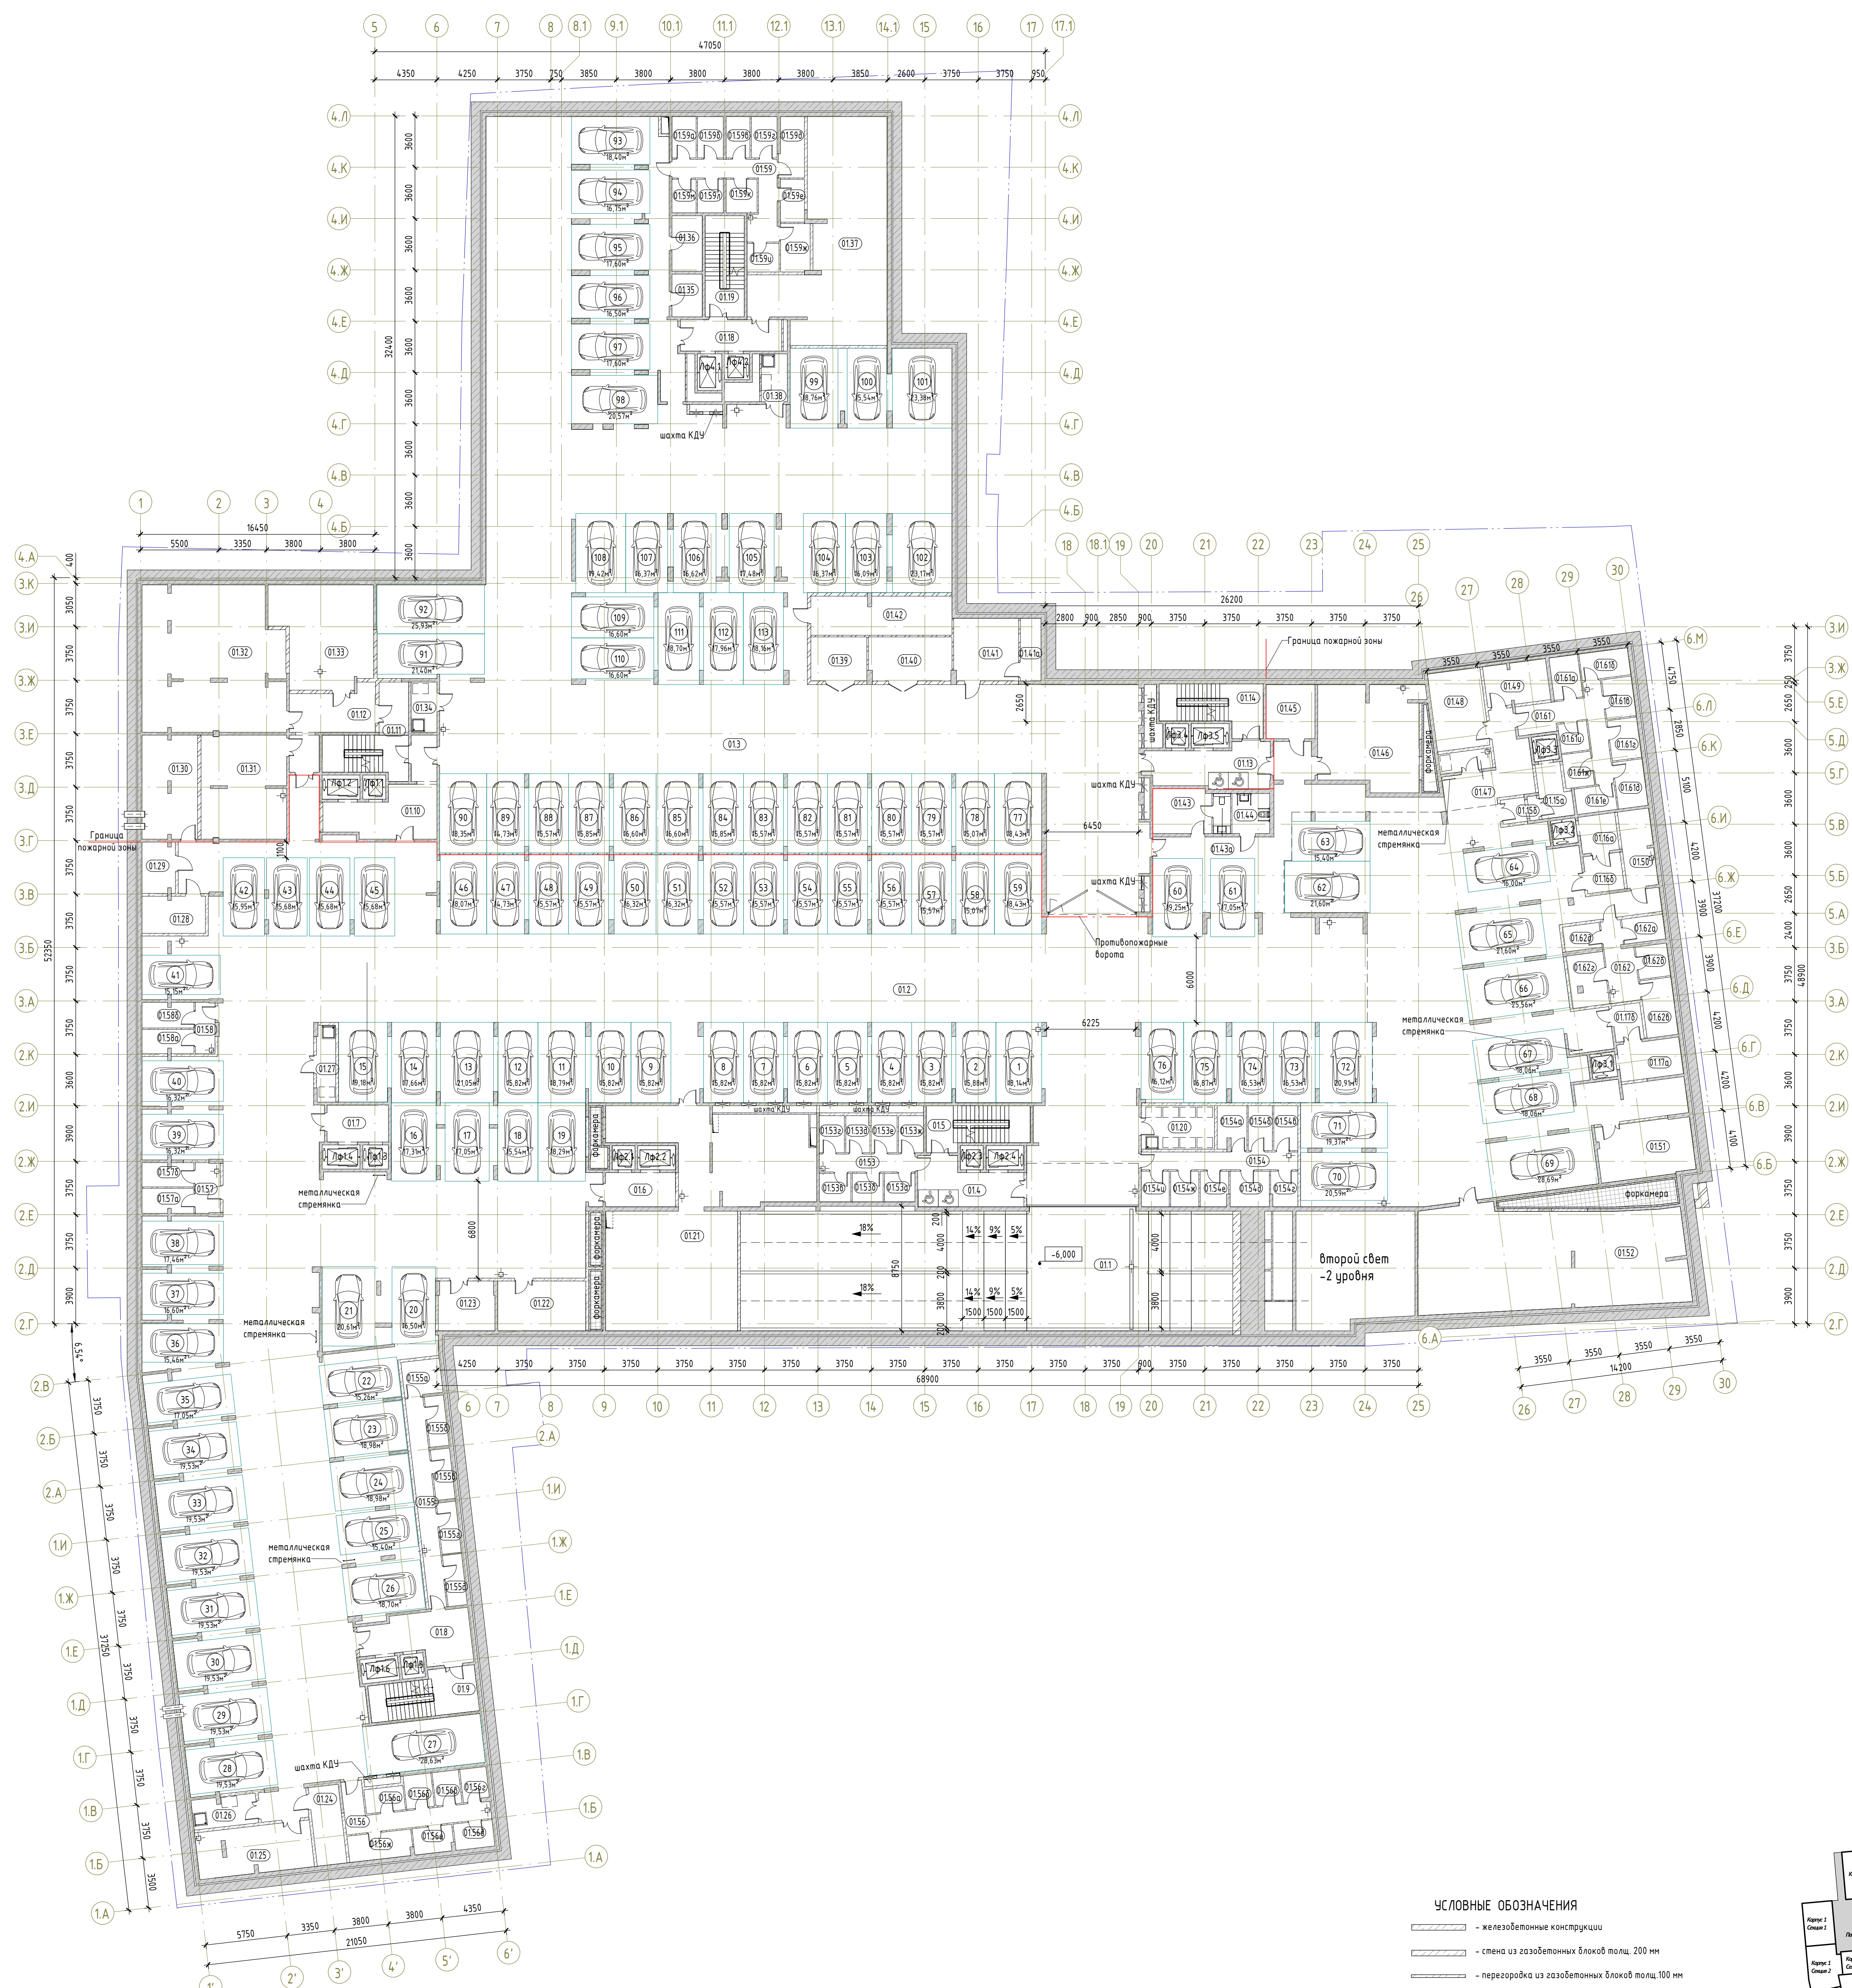

- УСЛОВНЫЕ ОБОЗНАЧЕНИЯ**
- железобетонные конструкции
  - стены из газобетонных блоков толщ. 200 мм
  - перегородка из газобетонных блоков толщ. 100 мм
  - граница участка

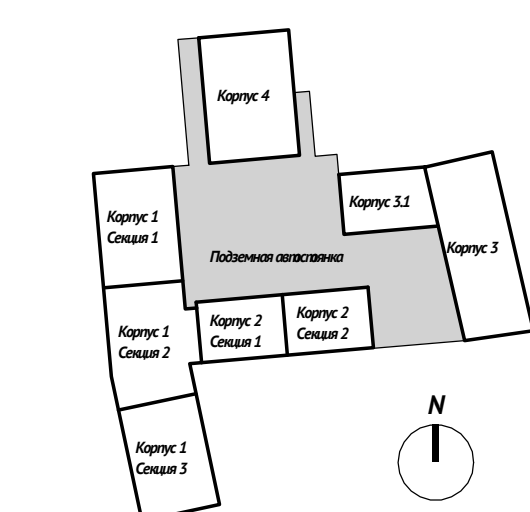

| Экспликация помещений |                                      |             |                  |
|-----------------------|--------------------------------------|-------------|------------------|
| Номер помеще-ния      | Наименование                         | Площадь, м² | Кат. поме-ще-ния |
| 01.1                  | Ремпа                                | 352,15      | B2               |
| 01.2                  | Помещение хранения автомобилей 01.1  | 2970,97     | B2               |
| 01.3                  | Помещение хранения автомобилей 01.2  | 1525,46     | B2               |
| 01.4                  | Лифтовой холл ПБ3                    | 21,24       |                  |
| 01.5                  | Лестничная клетка Лп2.2              | 20,52       |                  |
| 01.6                  | Лифтовой холл                        | 11,76       |                  |
| 01.7                  | Лифтовой холл                        | 11,18       |                  |
| 01.8                  | Лифтовой холл                        | 23,49       |                  |
| 01.9                  | Лестничная клетка Лп1.3              | 21,91       |                  |
| 01.10                 | Лифтовой холл                        | 29,92       |                  |
| 01.11                 | Лестничная клетка Лп1.1              | 24,28       |                  |
| 01.12                 | Тамбур-шлюз                          | 23,34       |                  |
| 01.13                 | Лифтовой холл ПБ3                    | 24,34       |                  |
| 01.14                 | Лестничная клетка Лп3.1              | 21,73       |                  |
| 01.15а                | Лифтовой холл                        | 7,67        |                  |
| 01.15б                | тамбур-шлюз                          | 4,26        |                  |
| 01.16а                | Лифтовой холл                        | 6,76        |                  |
| 01.16б                | тамбур-шлюз                          | 6,76        |                  |
| 01.17а                | Лифтовой холл                        | 11,44       |                  |
| 01.17б                | тамбур-шлюз                          | 5,10        |                  |
| 01.18                 | Лифтовой холл                        | 15,62       |                  |
| 01.19                 | Лестничная клетка Лп4                | 19,45       |                  |
| 01.20                 | Помещение временного хранения ТБ0    | 15,63       | B3               |
| 01.21                 | Приточная венткамера                 | 152,50      | Д                |
| 01.22                 | Приточная венткамера жилых корпусов  | 21,61       | Д                |
| 01.23                 | Помещение СС                         | 13,71       | B3               |
| 01.24                 | Помещение СС                         | 11,66       | B3               |
| 01.25                 | Техническое помещение                | 26,19       | B3               |
| 01.26                 | Помещение временного хранения ТБ0    | 9,41        | B3               |
| 01.27                 | Помещение временного хранения ТБ0    | 7,16        | B3               |
| 01.28                 | Электроштабная                       | 11,51       | B3               |
| 01.29                 | Входное помещение СС                 | 8,05        | B3               |
| 01.30                 | Водометный узел                      | 28,07       |                  |
| 01.31                 | Насосная АПТ                         | 43,18       |                  |
| 01.32                 | ИТП                                  | 98,46       |                  |
| 01.33                 | Насосная ХВС + ПВП                   | 46,82       |                  |
| 01.34                 | Помещение временного хранения ТБ0    | 6,34        | B3               |
| 01.35                 | Помещение хранения уборочной техники | 6,39        | B4               |
| 01.36                 | Помещение СС                         | 8,31        | B3               |
| 01.37                 | Кладоцентр                           | 102,48      |                  |
| 01.38                 | Помещение временного хранения ТБ0    | 6,13        | B3               |
| 01.39                 | Трансформаторная                     | 12,13       | B3               |
| 01.40                 | Трансформаторная                     | 17,83       | B3               |
| 01.41                 | РЧ                                   | 19,91       |                  |
| 01.41а                | Кабельная                            | 6,38        |                  |
| 01.42                 | ГРЩ                                  | 26,90       |                  |
| 01.43                 | Помещение для водителей              | 12,92       |                  |
| 01.43а                | с/у                                  | 3,36        |                  |
| 01.44                 | Универсальный санузел                | 7,42        |                  |
| 01.45                 | Электроштабная                       | 13,01       | B3               |
| 01.46                 | Приточная венткамера                 | 50,82       | Д                |
| 01.47                 | Помещение временного хранения ТБ0    | 5,18        | B3               |
| 01.48                 | Приточная венткамера                 | 20,35       | Д                |
| 01.49                 | Электроштабная                       | 12,75       | B3               |
| 01.50                 | Помещение СС                         | 11,79       | B3               |
| 01.51                 | Венткамера                           | 25,87       | Д                |
| 01.52                 | Приточная венткамера                 | 130,84      | Д                |
| 01.53                 | Коридор                              | 8,38        |                  |
| 01.53а                | Кладовая                             | 4,26        |                  |
| 01.53б                | Кладовая                             | 4,32        |                  |

| Экспликация помещений |              |             |                  |
|-----------------------|--------------|-------------|------------------|
| Номер помеще-ния      | Наименование | Площадь, м² | Кат. поме-ще-ния |
| 01.53б                | Кладовая     | 4,42        |                  |
| 01.53з                | Кладовая     | 4,55        |                  |
| 01.53д                | Кладовая     | 4,35        |                  |
| 01.53е                | Кладовая     | 4,68        |                  |
| 01.53ж                | Кладовая     | 4,55        |                  |
| 01.54                 | Коридор      | 13,72       |                  |
| 01.54а                | Кладовая     | 6,20        |                  |
| 01.54б                | Кладовая     | 5,32        |                  |
| 01.54в                | Кладовая     | 5,31        |                  |
| 01.54г                | Кладовая     | 4,61        |                  |
| 01.54д                | Кладовая     | 6,88        |                  |
| 01.54е                | Кладовая     | 4,86        |                  |
| 01.54ж                | Кладовая     | 4,94        |                  |
| 01.54и                | Кладовая     | 4,87        |                  |
| 01.55                 | Коридор      | 18,50       |                  |
| 01.55а                | Кладовая     | 6,61        |                  |
| 01.55б                | Кладовая     | 4,79        |                  |
| 01.55в                | Кладовая     | 4,79        |                  |
| 01.55г                | Кладовая     | 4,86        |                  |
| 01.55д                | Кладовая     | 4,86        |                  |
| 01.56                 | Коридор      | 15,93       |                  |
| 01.56а                | Кладовая     | 4,67        |                  |
| 01.56б                | Кладовая     | 4,58        |                  |
| 01.56в                | Кладовая     | 4,35        |                  |
| 01.56г                | Кладовая     | 4,23        |                  |
| 01.56д                | Кладовая     | 5,09        |                  |
| 01.56е                | Кладовая     | 5,06        |                  |
| 01.56ж                | Кладовая     | 8,21        |                  |
| 01.57                 | Коридор      | 6,13        |                  |
| 01.57а                | Кладовая     | 6,30        |                  |
| 01.57б                | Кладовая     | 6,12        |                  |
| 01.58                 | Коридор      | 4,93        |                  |
| 01.58а                | Кладовая     | 6,11        |                  |
| 01.58б                | Кладовая     | 6,48        |                  |
| 01.59                 | Коридор      | 17,19       |                  |
| 01.59а                | Кладовая     | 4,93        |                  |
| 01.59б                | Кладовая     | 5,22        |                  |
| 01.59в                | Кладовая     | 4,86        |                  |
| 01.59г                | Кладовая     | 5,22        |                  |
| 01.59д                | Кладовая     | 7,46        |                  |
| 01.59е                | Кладовая     | 5,18        |                  |
| 01.59ж                | Кладовая     | 7,01        |                  |
| 01.59и                | Кладовая     | 4,51        |                  |
| 01.59к                | Кладовая     | 5,10        |                  |
| 01.59л                | Кладовая     | 4,23        |                  |
| 01.59м                | Кладовая     | 4,00        |                  |
| 01.61                 | Коридор      | 17,93       |                  |
| 01.61а                | Кладовая     | 6,06        |                  |
| 01.61б                | Кладовая     | 6,52        |                  |
| 01.61в                | Кладовая     | 5,82        |                  |
| 01.61г                | Кладовая     | 5,93        |                  |
| 01.61д                | Кладовая     | 6,86        |                  |
| 01.61е                | Кладовая     | 5,08        |                  |
| 01.61ж                | Кладовая     | 4,85        |                  |
| 01.61и                | Кладовая     | 4,14        |                  |
| 01.62                 | Коридор      | 10,58       |                  |
| 01.62а                | Кладовая     | 5,08        |                  |
| 01.62б                | Кладовая     | 5,06        |                  |
| 01.62в                | Кладовая     | 8,91        |                  |
| 01.62г                | Кладовая     | 9,42        |                  |
| 01.62д                | Кладовая     | 4,55        |                  |
|                       |              | 6570,94     |                  |



|                                                           |           |
|-----------------------------------------------------------|-----------|
| Кровля тип К7 (покрытие автостоянки)                      |           |
| Покрытие см. разлел ПЗУ                                   |           |
| Щебень фракции 5-20мм                                     | -перем.   |
| Мембрана ВИЛЛАДРЕЙН 8 Гео                                 | -10 мм    |
| Гидроизоляция УЛЬТРАНАП, наплавлена                       | -5 мм     |
| Гидроизоляция ИКОПАЛ Н ЭП, наплавлена                     | -5 мм     |
| Профлист СБС ИКОПАЛ                                       |           |
| Бетонная разгрузочная плита В25, армированная 4Вr1100х100 | -150 мм   |
| Уклонообразующий слой из керамзитобетона 900 кг/м3        | -0.550 мм |
| Полупрозрачная пленка                                     |           |
| Жесткий дорожный утеплитель Ravatherm XPS Standard 50     | -50 мм    |
| Изоляция УЛЬТРАДРАЙВ, наплавлена, 1 слой                  | -10 мм    |
| Профлист СБС ИКОПАЛ                                       |           |
| Железобетонная плита                                      |           |


Экспликация помещений

| Номер помеще-ния | Наименование            | Площадь, м² | Кат. помеще-ния |
|------------------|-------------------------|-------------|-----------------|
| 0.1              | Лестничная клетка Лп1.1 | 28,98       |                 |
| 0.2              | Лестничная клетка Лп1.3 | 22,23       |                 |
| 0.3              | Лестничная клетка Лп2.1 | 21,16       |                 |
| 0.4              | Лестничная клетка Лп2.2 | 20,52       |                 |
| 0.5              | Лестничная клетка Лп3.1 | 18,98       |                 |
| 0.6              | Лестничная клетка Лп4   | 36,36       |                 |
|                  |                         | 148,23      |                 |

Экспликация технических пространств


| Наименование                                 | Площадь, м² | Кат. помеще-ния |
|----------------------------------------------|-------------|-----------------|
| Корпус1. Секция1. Техническое пространство   | 480,70      |                 |
| Корпус1. Секция2. Техническое пространство   | 630,46      |                 |
| Корпус1. Секция3. Техническое пространство   | 234,12      |                 |
| Корпус1. Секция3. Техническое пространство   | 206,12      |                 |
| Корпус 2. Секция 1. Техническое пространство | 259,95      |                 |
| Корпус 2. Секция 2. Техническое пространство | 260,18      |                 |
| Корпус 3.1. Техническое пространство         | 357,39      |                 |
| Корпус 3. Техническое пространство           | 479,91      |                 |
| Корпус 4. Техническое пространство           | 615,47      |                 |
|                                              | 3524,30     |                 |

|               |        |
|---------------|--------|
| Канал теплоты | 197,28 |
|---------------|--------|

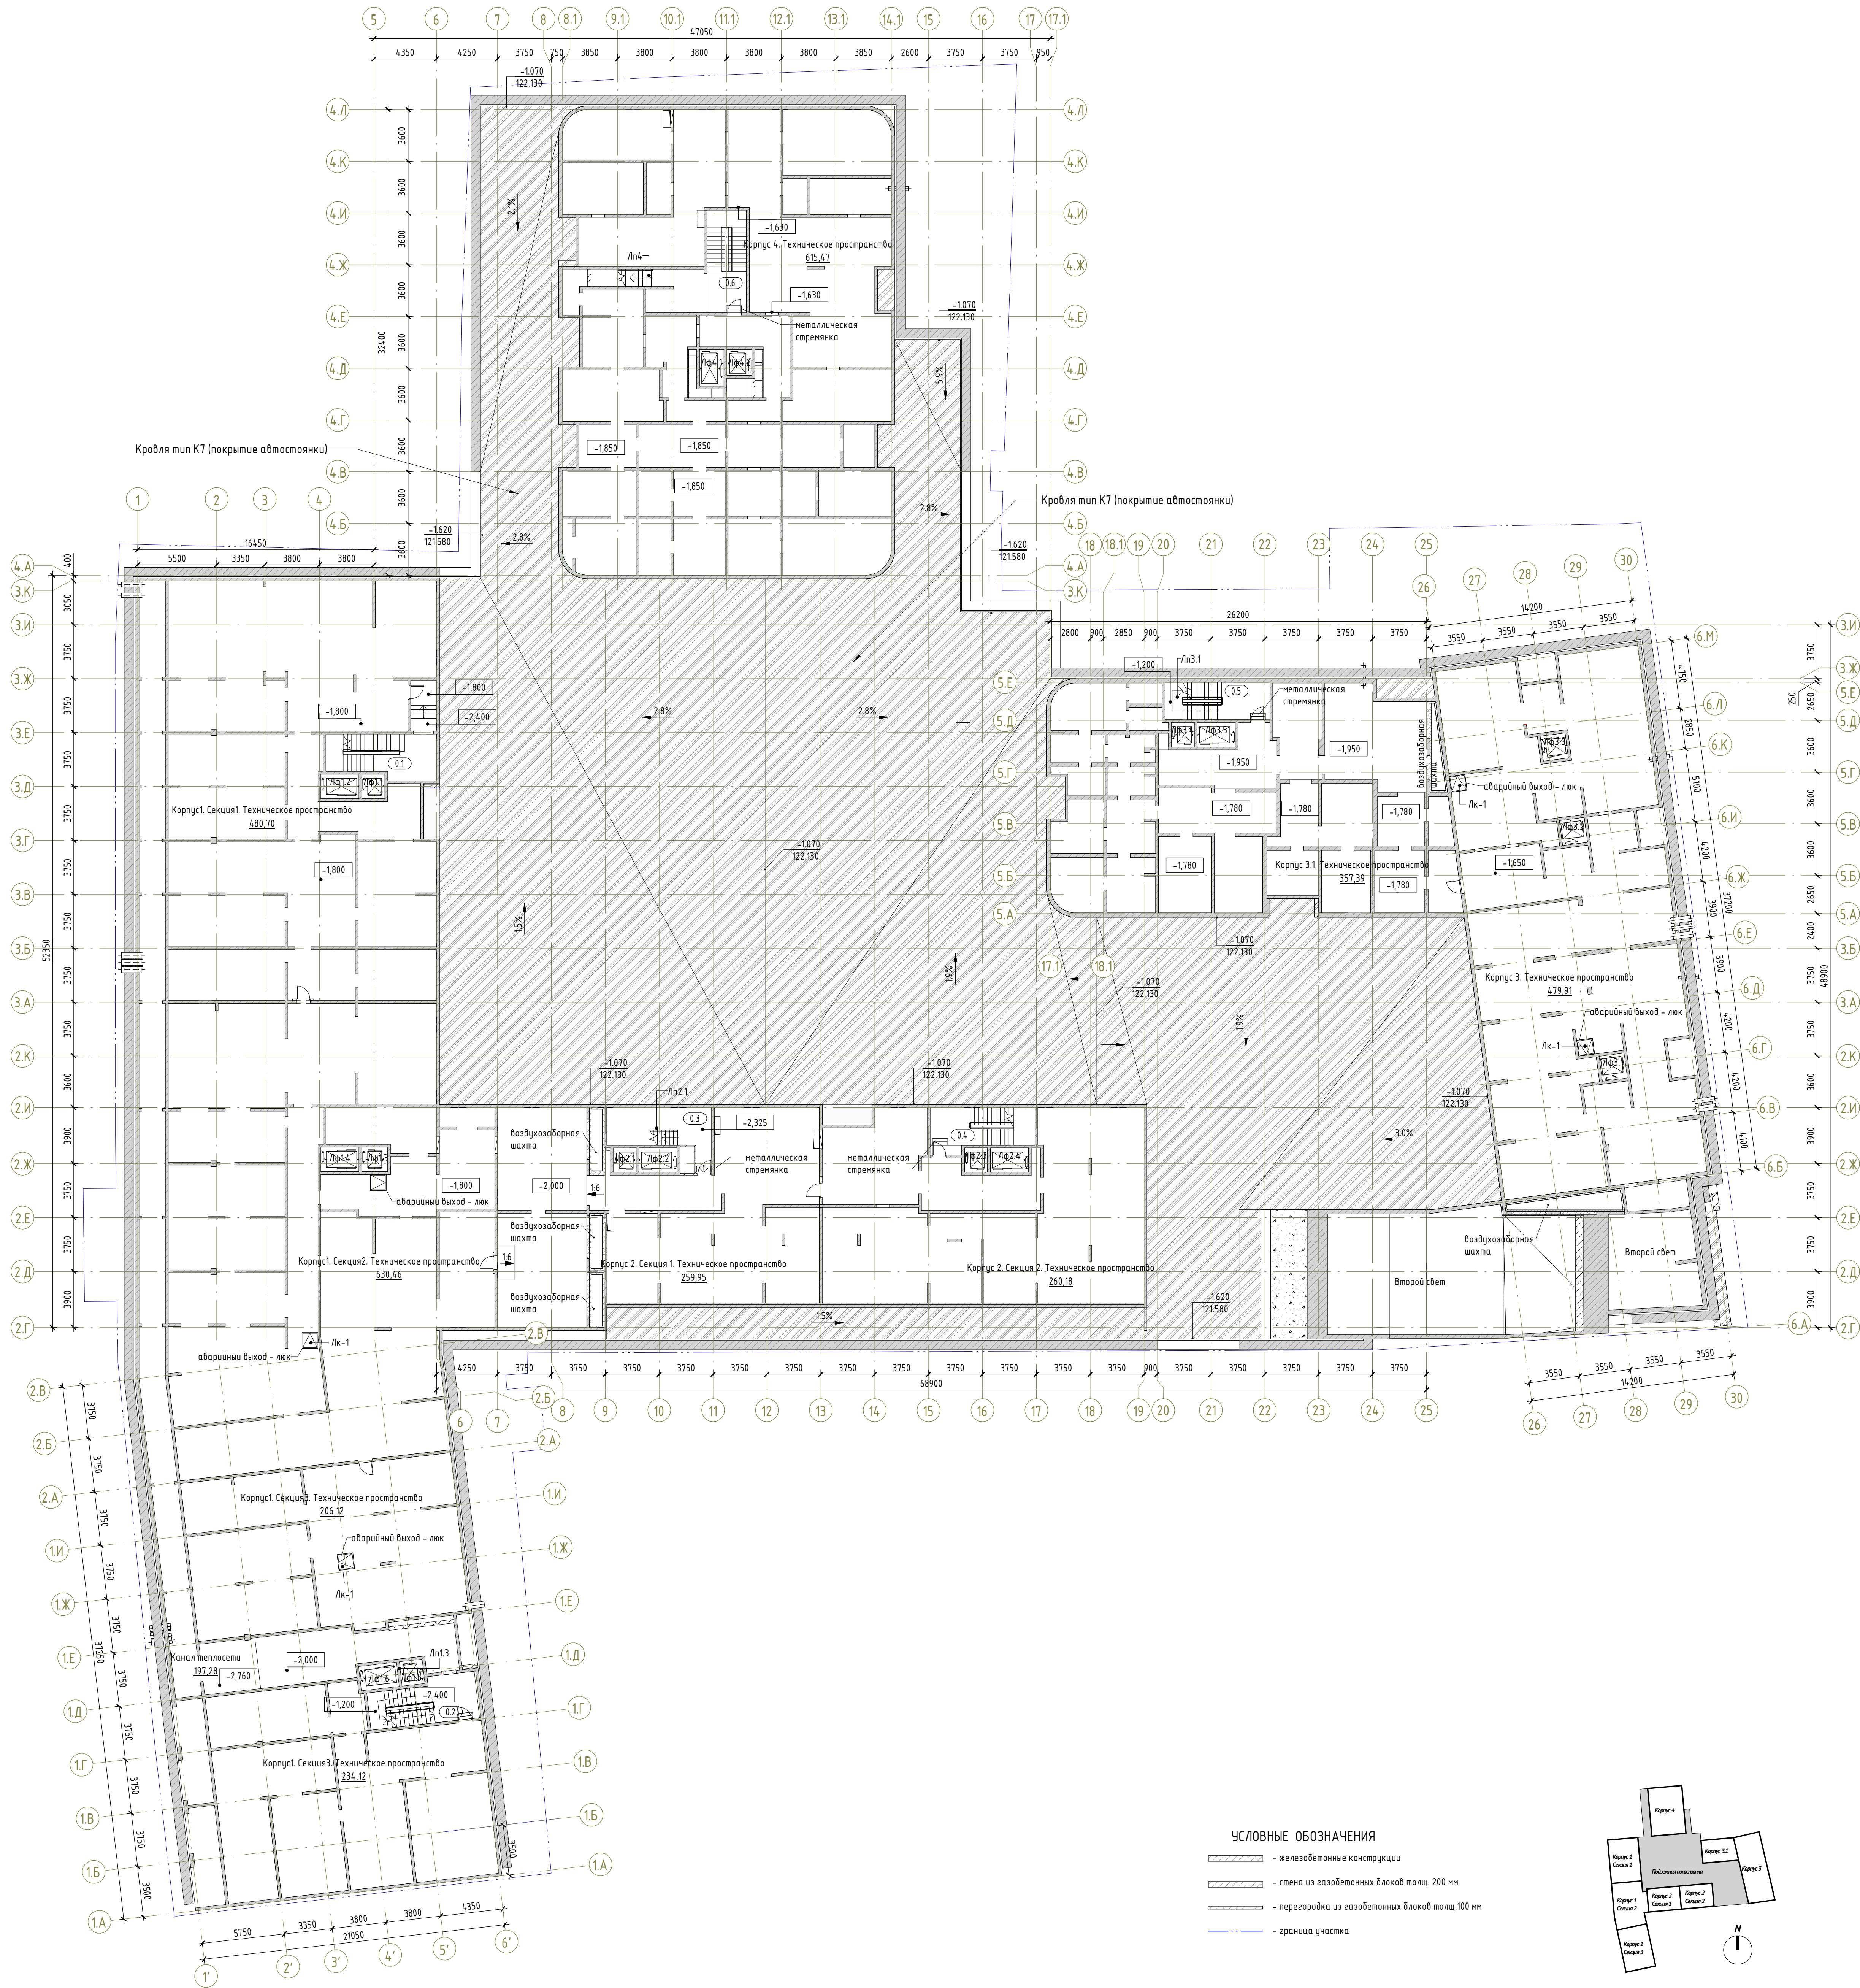

УСЛОВНЫЕ ОБОЗНАЧЕНИЯ

- железобетонные конструкции
- стена из газобетонных блоков толщ. 200 мм
- перегородка из газобетонных блоков толщ. 100 мм
- граница участка

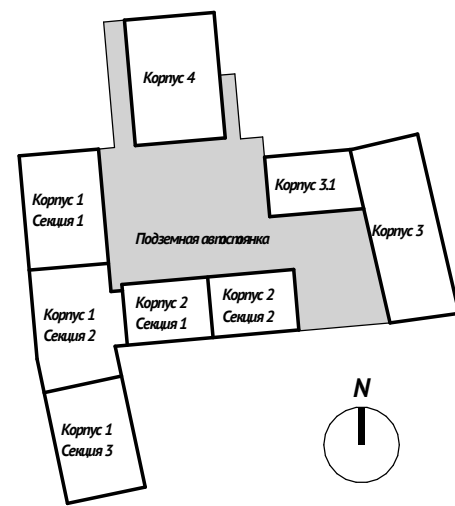

|                                                                                      |           |       |           |       |        |
|--------------------------------------------------------------------------------------|-----------|-------|-----------|-------|--------|
| АА/БЗ-03-ДС3 - АР1                                                                   |           |       |           |       |        |
| Жилой комплекс, расположенный по адресу: г. Москва, ЦАО, Садовническая ул., д. 76/71 |           |       |           |       |        |
| Изм.                                                                                 | Кол. чл.  | Лист  | № док.    | Подп. | Дата   |
| Разработал                                                                           | Карасев   | 08.24 |           |       | 08.24  |
| Разработал                                                                           | Заварина  | 08.24 |           |       | 08.24  |
| Проверил                                                                             | Добрыкина | 08.24 |           |       | 08.24  |
| Часть 1. Архитектурные решения. Планы                                                |           |       |           |       |        |
| План технического пространства на отм. -1,800, М1_200                                |           |       |           |       |        |
| Норм. контр.                                                                         | Добрыкина | 08.24 |           |       |        |
|                                                                                      |           |       | П         | З     | Листов |
|                                                                                      |           |       | А R T E Л |       |        |



| Экспликация МОП 1 этажа (корпус 1) |              |             |                |
|------------------------------------|--------------|-------------|----------------|
| Номер помещения                    | Наименование | Площадь, м² | Категория пом. |

|          |                         |       |  |
|----------|-------------------------|-------|--|
| Секция 1 |                         |       |  |
| 101.1    | Лестничная клетка Л1.1  | 7,51  |  |
| 101.1п   | Лестничная клетка Лп1.1 | 13,28 |  |
| 101.2    | Вестибюль               | 71,89 |  |
| 101.3    | ПУИ                     | 3,10  |  |
| 101.4    | Колясочная              | 9,60  |  |
| 101.5    | Универсальный санузел   | 5,20  |  |

|          |                                       |        |  |
|----------|---------------------------------------|--------|--|
| Секция 2 |                                       |        |  |
| 101.6    | Лестничная клетка Л1.2                | 20,49  |  |
| 101.7    | Вестибюль                             | 166,71 |  |
| 101.8    | ПУИ                                   | 2,95   |  |
| 101.9    | Колясочная                            | 15,95  |  |
| 101.10   | Универсальный санузел                 | 5,05   |  |
| 101.11   | Помещение хранения уличного инвентаря | 9,15   |  |
| 101.12   | Диспетчерская                         | 43,36  |  |
| 101.13   | Санузел диспетчерской                 | 2,75   |  |
| 101.14   | Служебное помещение                   | 4,59   |  |

|          |                         |       |  |
|----------|-------------------------|-------|--|
| Секция 3 |                         |       |  |
| 101.30   | Лестничная клетка Л1.3  | 7,51  |  |
| 101.30п  | Лестничная клетка Лп1.3 | 13,28 |  |
| 101.31   | Вестибюль               | 81,84 |  |
| 101.32   | ПУИ                     | 3,10  |  |
| 101.33   | Колясочная              | 9,66  |  |
| 101.34   | Универсальный санузел   | 5,20  |  |

502,17

| Экспликация МОП 1 этажа (корпус 2) |              |             |                |
|------------------------------------|--------------|-------------|----------------|
| Номер помещения                    | Наименование | Площадь, м² | Категория пом. |

|          |                         |        |  |
|----------|-------------------------|--------|--|
| Секция 1 |                         |        |  |
| 201.1    | Лестничная клетка Л2.1  | 13,16  |  |
| 201.1п   | Лестничная клетка Лп2.1 | 5,78   |  |
| 201.2    | Вестибюль               | 110,83 |  |
| 201.3    | Колясочная              | 7,18   |  |
| 201.4    | Универсальный санузел   | 5,99   |  |
| 201.5    | ПУИ                     | 4,24   |  |
| 201.6    | Лестничная клетка Л2.2  | 8,16   |  |
| 201.6п   | Лестничная клетка Лп2.2 | 10,91  |  |

166,25

#### Экспликация помещений общего назначения

| Номер помещения | Наименование | Площадь, м² | Категория пом. |
|-----------------|--------------|-------------|----------------|
|-----------------|--------------|-------------|----------------|

|          |                        |        |  |
|----------|------------------------|--------|--|
| Секция 1 |                        |        |  |
| 101.35   | БКТ(Офисные помещения) | 150,23 |  |
| 101.36   | ПУИ                    | 4,15   |  |
| 101.37   | Универсальный санузел  | 7,25   |  |

|          |                                 |        |  |
|----------|---------------------------------|--------|--|
| Секция 2 |                                 |        |  |
| 101.15   | БКТ(Офисные помещения)          | 124,67 |  |
| 101.16   | ПУИ                             | 3,05   |  |
| 101.17   | Универсальный санузел           | 5,41   |  |
| 101.18   | Тренажерный зал                 | 82,65  |  |
| 101.19   | Раздевалка                      | 7,98   |  |
| 101.20   | Душевая                         | 2,62   |  |
| 101.21   | С/у                             | 2,25   |  |
| 101.22   | Раздевалка                      | 5,64   |  |
| 101.23   | С/у                             | 2,19   |  |
| 101.24   | Душевая                         | 1,92   |  |
| 101.25   | Салон красоты                   | 39,51  |  |
| 101.26   | Салон красоты                   | 17,76  |  |
| 101.27   | С/у                             | 3,30   |  |
| 101.28   | С/у персонала                   | 2,61   |  |
| 101.29   | Помещение для досуговых занятий | 29,32  |  |

492,51

#### Экспликация помещений квартир 1 этажа (корпус 1)

| Номер помещения | Наименование              | Площадь, м² |
|-----------------|---------------------------|-------------|
| Секция 1        |                           |             |
| 1.1             | Холл                      | 23,49       |
| 1.2             | Кухня-ниша                | 26,43       |
| 1.3             | Гостиная                  | 25,55       |
| 1.4             | Спальня с гардеробной     | 27,41       |
| 1.5             | Спальня                   | 19,52       |
| 1.6             | Кабинет                   | 20,05       |
| 1.7             | С/у                       | 6,93        |
| 1.8             | С/у                       | 6,09        |
| 1.9             | С/у                       | 6,95        |
| 1.10            | Гардеробная               | 7,69        |
| 1.11            | Терраса (коэффициент 0,3) | 3,25        |
|                 |                           | 173,36      |
| Секция 2        |                           |             |
| 2.1             | Холл                      | 4,50        |
| 2.2             | Кухня-столовая            | 24,38       |
| 2.3             | Спальня с гардеробной     | 21,34       |
| 2.4             | С/у                       | 3,00        |
| 2.5             | С/у                       | 4,61        |
| 2.6             | Терраса (коэффициент 0,3) | 3,25        |
|                 |                           | 61,08       |
| Секция 3        |                           |             |
| 3.1             | Холл                      | 18,97       |
| 3.2             | Кухня-столовая            | 42,49       |
| 3.3             | Спальня                   | 18,87       |
| 3.4             | Спальня                   | 20,99       |
| 3.5             | Спальня с гардеробной     | 25,85       |
| 3.6             | С/у                       | 7,43        |
| 3.7             | С/у                       | 2,58        |
| 3.8             | С/у                       | 4,62        |
| 3.9             | Гардеробная               | 5,66        |
| 3.10            | Постирочная               | 7,73        |
| 3.11            | Холл                      | 8,17        |
| 3.12            | Терраса (коэффициент 0,3) | 3,15        |
|                 |                           | 166,51      |

#### Экспликация помещений квартир 1 этажа (корпус 1)


| Номер помещения | Наименование              | Площадь, м² |
|-----------------|---------------------------|-------------|
| Секция 1        |                           |             |
| 1.3.36          |                           |             |
| 1.11            |                           |             |
| 36.1            | Холл                      | 4,26        |
| 36.2            | Кухня-столовая            | 25,81       |
| 36.3            | Спальня с гардеробной     | 22,17       |
| 36.4            | С/у                       | 2,79        |
| 36.5            | С/у                       | 4,95        |
| 36.6            | Терраса (коэффициент 0,3) | 3,25        |
|                 |                           | 63,23       |
| Секция 2        |                           |             |
| 1.3.37          |                           |             |
| 37.1            | Холл                      | 10,18       |
| 37.2            | Кухня-столовая            | 36,21       |
| 37.3            | Спальня                   | 15,74       |
| 37.4            | Спальня с гардеробной     | 26,85       |
| 37.5            | С/у                       | 6,93        |
| 37.6            | С/у                       | 5,15        |
| 37.7            | Гардеробная               | 3,76        |
| 37.8            | Терраса (коэффициент 0,3) | 3,25        |
|                 |                           | 108,07      |
| Секция 3        |                           |             |
| 1.3.38          |                           |             |
| 38.1            | Холл                      | 6,25        |
| 38.2            | Кухня-столовая            | 21,92       |
| 38.3            | Спальня с гардеробной     | 19,44       |
| 38.4            | С/у                       | 5,91        |
| 38.5            | С/у                       | 4,09        |
|                 |                           | 57,61       |
|                 |                           | 629,86      |

#### Экспликация помещений квартир 1 этажа (корпус 2)

| Номер помещения | Наименование              | Площадь, м² |
|-----------------|---------------------------|-------------|
| Секция 1        |                           |             |
| 2.1.1           |                           |             |
| 1.1             | Холл                      | 9,54        |
| 1.2             | Кухня-столовая            | 26,20       |
| 1.3             | Спальня с гардеробной     | 19,93       |
| 1.4             | Спальня                   | 13,61       |
| 1.5             | Спальня с гардеробной     | 18,30       |
| 1.6             | Кабинет                   | 9,27        |
| 1.7             | С/у                       | 7,47        |
| 1.8             | С/у                       | 4,37        |
| 1.9             | С/у                       | 3,46        |
| 1.10            | Гардеробная               | 2,89        |
| 1.11            | Холл                      | 3,83        |
| 1.12            | Терраса (коэффициент 0,3) | 7,34        |
|                 |                           | 126,21      |
| Секция 2        |                           |             |
| 2.1.2           |                           |             |
| 2.1             | Холл                      | 7,65        |
| 2.2             | Кухня-столовая            | 31,38       |
| 2.3             | Спальня с гардеробной     | 21,78       |
| 2.4             | С/у                       | 6,13        |
| 2.5             | С/у                       | 4,15        |
| 2.6             | Терраса (коэффициент 0,3) | 7,62        |
|                 |                           | 78,71       |
| Секция 3        |                           |             |
| 2.1.3           |                           |             |
| 3.1             | Холл                      | 11,29       |
| 3.2             | Кухня-столовая            | 29,91       |
| 3.3             | Спальня с гардеробной     | 22,08       |
| 3.4             | Спальня                   | 15,23       |
| 3.5             | С/у                       | 5,84        |
| 3.6             | С/у                       | 4,49        |
| 3.7             | Гардеробная               | 4,52        |
| 3.8             | Терраса (коэффициент 0,3) | 9,82        |
|                 |                           | 103,18      |
|                 |                           | 308,10      |

Покрывте тип ПТ1 (покровие террасы по грунту)

|                                                                 |             |
|-----------------------------------------------------------------|-------------|
| Плитка из природного камня                                      | -20 мм      |
| Прослойка и заполнение швов из цементно-песчаного раствора М100 | -10 мм      |
| Стяжка цементно-песчаная М150, армированная 4Вр1100х100         | -30...90 мм |
| Гидроизол на битумной мастике (см. черт. КР)                    | -5 мм       |
| Стяжка выравнивающая из цементно-песчаного раствора М100        | -30 мм      |
| Подстилающий слой из бетона В7,5                                | -100 мм     |
| Уплотненный со щебнем грунт                                     |             |

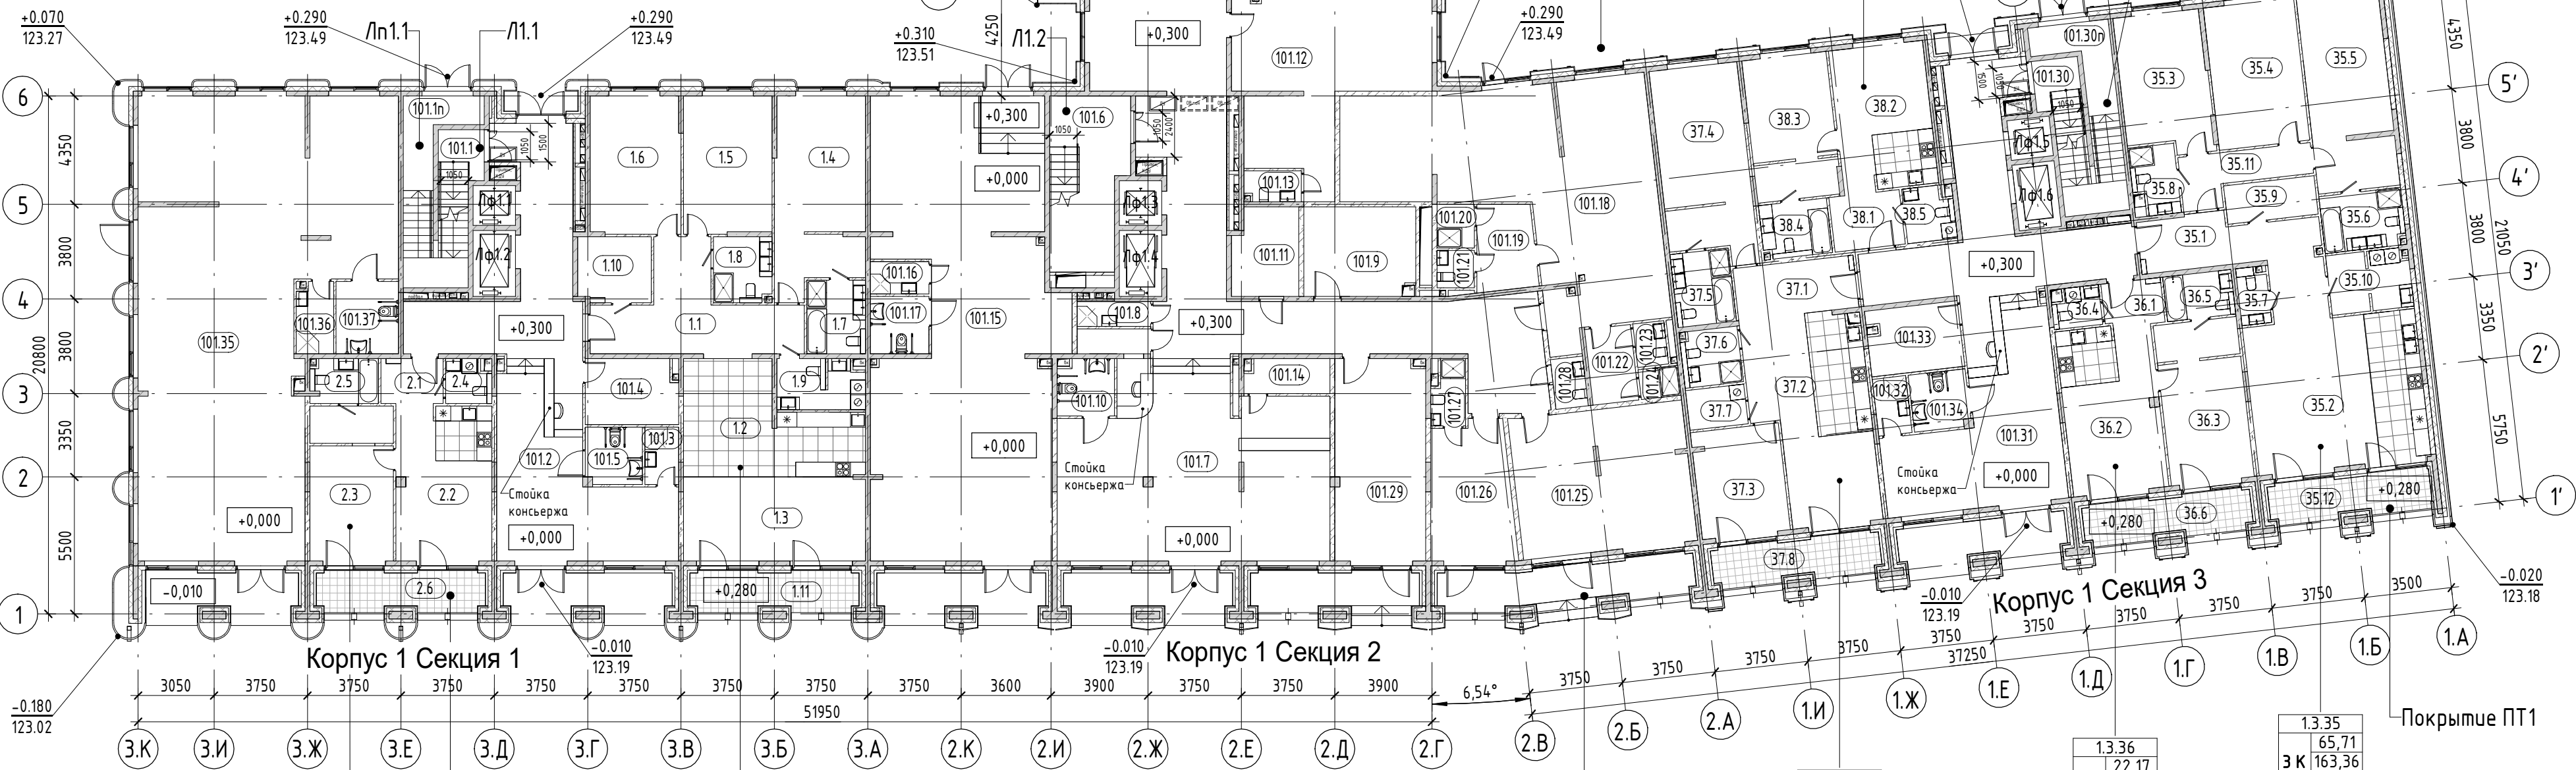

#### УСЛОВНЫЕ ОБОЗНАЧЕНИЯ

- железобетонные конструкции
- стена из газобетонных блоков толщ. 200 мм
- перегородка из газобетонных блоков толщ. 100 мм
- маркировка помещений квартиры
- маркировка помещений общего пользования

номер квартиры  
номер помещения  
номер корпуса  
этаж  
номер помещения

#### Марка квартиры:

|       |                                                           |
|-------|-----------------------------------------------------------|
| 33    | Номер квартиры                                            |
| 42.32 | Жилая площадь квартиры                                    |
| 82.58 | Общая площадь квартиры без учета неоплачиваемых помещений |
| 85.65 | Общая площадь квартиры с учетом понижающих коэффициентов  |
| К     | Код типа планировки                                       |
| 1     | Количество жилых комнат в квартире                        |

|              |        |           |        |                  |                                                                                         |                                       |                  |       |                                      |            |  |
|--------------|--------|-----------|--------|------------------|-----------------------------------------------------------------------------------------|---------------------------------------|------------------|-------|--------------------------------------|------------|--|
|              |        |           |        |                  | АА/БЗ-03-ДСЗ - АР1                                                                      |                                       |                  |       |                                      |            |  |
|              |        |           |        |                  | "Жилой комплекс", расположенный по адресу: г. Москва, ЦАО, Садовническая ул., вл. 76/71 |                                       |                  |       |                                      |            |  |
| Изм.         | Жол.ч. | Лист      | № док. | Подп.            | Дата                                                                                    |                                       |                  |       |                                      |            |  |
| Разработал   |        | Карасёв   |        | <i>Карасёв</i>   | 08.24                                                                                   | Часть 1. Архитектурные решения. Планы | Стация           | Лист  | Листов                               |            |  |
| Разработал   |        | Задорина  |        | <i>Задорина</i>  | 08.24                                                                                   |                                       | П                | 4     |                                      |            |  |
| Проверил     |        | Добрякова |        | <i>Добрякова</i> | 08.24                                                                                   |                                       |                  |       |                                      |            |  |
| Норм. контр. |        |           |        |                  |                                                                                         | Добрякова                             | <i>Добрякова</i> | 08.24 | Корпуса 1, 2. План 1 этажа. М 1_200. |            |  |
|              |        |           |        |                  |                                                                                         | АРХИТЕКТУРА                           |                  |       |                                      | Формат А1А |  |



Экспликация МОП 2 этажа (корпус 1)

| Номер помещения | Наименование           | Площадь, м² | Категория пом. |
|-----------------|------------------------|-------------|----------------|
| Секция 1        |                        |             |                |
| 102.1           | Лестничная клетка Л1.1 | 22,23       |                |
| 102.2           | Коридор                | 35,03       |                |
| Секция 2        |                        |             |                |
| 102.3           | Лестничная клетка Л1.2 | 22,10       |                |
| 102.4           | Коридор                | 45,22       |                |
| Секция 3        |                        |             |                |
| 102.5           | Лестничная клетка Л1.3 | 22,23       |                |
| 102.6           | Коридор                | 47,00       |                |
|                 |                        | 193,81      |                |

Экспликация МОП 2 этажа (корпус 2)

| Номер помещения | Наименование           | Площадь, м² | Категория пом. |
|-----------------|------------------------|-------------|----------------|
| Секция 1        |                        |             |                |
| 202.1           | Лестничная клетка Л2.1 | 20,18       |                |
| 202.2           | Коридор                | 18,51       |                |
| Секция 2        |                        |             |                |
| 202.3           | Лестничная клетка Л2.2 | 20,18       |                |
| 202.4           | Коридор                | 18,09       |                |
|                 |                        | 76,96       |                |

Экспликация помещений квартир 2 этажа (корпус 1)

| Номер помещения | Наименование          | Площадь, м2 |
|-----------------|-----------------------|-------------|
| Секция 1        |                       |             |
| 1.1.3           |                       |             |
| 3.1             | Холл                  | 23,10       |
| 3.2             | Кухня-ниша            | 27,11       |
| 3.3             | Гостиная              | 39,42       |
| 3.4             | Спальня               | 20,05       |
| 3.5             | Спальня               | 19,52       |
| 3.6             | Спальня с гардеробной | 27,26       |
| 3.7             | С/у                   | 6,93        |
| 3.8             | С/у                   | 6,49        |
| 3.9             | С/у                   | 5,88        |
| 3.10            | Гардеробная           | 7,56        |
|                 |                       | 183,32      |
| 1.1.4           |                       |             |
| 4.1             | Холл                  | 4,50        |
| 4.2             | Кухня-столовая        | 32,08       |
| 4.3             | Спальня с гардеробной | 27,97       |
| 4.4             | С/у                   | 4,77        |
| 4.5             | С/у                   | 3,00        |
|                 |                       | 72,32       |

Экспликация помещений квартир 2 этажа (корпус 1)

| Номер помещения | Наименование          | Площадь, м2 |
|-----------------|-----------------------|-------------|
| 1.1.5           |                       |             |
| 5.1             | Холл                  | 4,50        |
| 5.2             | Кухня-столовая        | 32,08       |
| 5.3             | Спальня с гардеробной | 27,97       |
| 5.4             | С/у                   | 4,35        |
| 5.5             | С/у                   | 2,52        |
|                 |                       | 71,42       |
| 1.1.6           |                       |             |
| 6.1             | Холл                  | 17,61       |
| 6.2             | Кухня-ниша            | 17,27       |
| 6.3             | Гостиная              | 39,37       |
| 6.4             | Спальня               | 23,59       |
| 6.5             | Спальня               | 28,47       |
| 6.6             | Спальня с гардеробной | 20,46       |
| 6.7             | С/у                   | 7,35        |
| 6.8             | С/у                   | 5,49        |
| 6.9             | С/у                   | 4,55        |
| 6.10            | Холл                  | 7,73        |
|                 |                       | 171,89      |

Экспликация помещений квартир 2 этажа (корпус 1)


| Номер помещения | Наименование          | Площадь, м2 |
|-----------------|-----------------------|-------------|
| Секция 2        |                       |             |
| 12.18           |                       |             |
| 18.1            | Холл                  | 15,71       |
| 18.2            | Кухня-столовая        | 45,18       |
| 18.3            | Спальня               | 21,37       |
| 18.4            | Спальня               | 22,38       |
| 18.5            | Спальня               | 22,01       |
| 18.6            | С/у                   | 7,14        |
| 18.7            | С/у                   | 2,92        |
| 18.8            | С/у                   | 9,63        |
| 18.9            | Гардеробная           | 8,49        |
| 18.10           | Гардеробная           | 9,51        |
| 18.11           | Гардеробная           | 6,09        |
| 18.12           | Постирочная           | 3,68        |
| 18.13           | Холл                  | 7,24        |
|                 |                       | 181,35      |
| 12.19           |                       |             |
| 19.1            | Холл                  | 7,65        |
| 19.2            | Кухня-столовая        | 52,53       |
| 19.3            | Спальня               | 18,81       |
| 19.4            | Спальня с гардеробной | 28,98       |
| 19.5            | С/у                   | 7,23        |
| 19.6            | С/у                   | 8,70        |
| 19.7            | Гардеробная           | 4,72        |
|                 |                       | 128,62      |
| 12.20           |                       |             |
| 20.1            | Холл                  | 4,14        |
| 20.2            | Кухня-столовая        | 32,14       |
| 20.3            | Спальня с гардеробной | 27,97       |
| 20.4            | С/у                   | 4,71        |
| 20.5            | С/у                   | 3,36        |
|                 |                       | 72,32       |
| 12.21           |                       |             |
| 21.1            | Холл                  | 4,14        |
| 21.2            | Кухня-столовая        | 32,14       |
| 21.3            | Спальня с гардеробной | 27,97       |
| 21.4            | С/у                   | 3,36        |
| 21.5            | С/у                   | 4,81        |
|                 |                       | 72,42       |
| 12.22           |                       |             |
| 22.1            | Холл                  | 19,41       |
| 22.2            | Кухня-столовая        | 44,67       |
| 22.3            | Спальня               | 15,80       |
| 22.4            | Спальня с гардеробной | 24,19       |
| 22.5            | Спальня               | 17,82       |
| 22.6            | С/у                   | 5,07        |
| 22.7            | С/у                   | 6,93        |
| 22.8            | С/у                   | 4,90        |
| 22.9            | Гардеробная           | 7,85        |
|                 |                       | 146,64      |

Экспликация помещений квартир 2 этажа (корпус 1)

| Номер помещения | Наименование          | Площадь, м2 |
|-----------------|-----------------------|-------------|
| Секция 3        |                       |             |
| 13.39           |                       |             |
| 39.1            | Холл                  | 10,18       |
| 39.2            | Кухня-столовая        | 31,39       |
| 39.3            | Спальня               | 17,77       |
| 39.4            | Спальня с гардеробной | 25,85       |
| 39.5            | С/у                   | 7,10        |
| 39.6            | С/у                   | 4,62        |
| 39.7            | Гардеробная           | 4,00        |
|                 |                       | 100,91      |
| 13.40           |                       |             |
| 40.1            | Холл                  | 8,21        |
| 40.2            | Кухня-столовая        | 43,46       |
| 40.3            | Спальня               | 17,77       |
| 40.4            | Спальня               | 22,19       |
| 40.5            | Спальня с гардеробной | 26,73       |
| 40.6            | С/у                   | 7,03        |
| 40.7            | С/у                   | 4,60        |
| 40.8            | С/у                   | 2,76        |
| 40.9            | Гардеробная           | 4,80        |
| 40.10           | Холл                  | 6,50        |
|                 |                       | 144,05      |
| 13.41           |                       |             |
| 41.1            | Холл                  | 5,45        |
| 41.2            | Кухня-столовая        | 31,12       |
| 41.3            | Спальня с гардеробной | 28,81       |
| 41.4            | С/у                   | 4,70        |
| 41.5            | С/у                   | 3,87        |
|                 |                       | 73,95       |
| 13.42           |                       |             |
| 42.1            | Холл                  | 10,19       |
| 42.2            | Кухня-столовая        | 44,17       |
| 42.3            | Спальня               | 20,06       |
| 42.4            | Спальня с гардеробной | 26,85       |
| 42.5            | С/у                   | 6,93        |
| 42.6            | С/у                   | 4,71        |
| 42.7            | Гардеробная           | 5,59        |
|                 |                       | 118,50      |
| 13.43           |                       |             |
| 43.1            | Холл                  | 6,36        |
| 43.2            | Кухня-столовая        | 22,38       |
| 43.3            | Спальня с гардеробной | 18,98       |
| 43.4            | С/у                   | 5,61        |
| 43.5            | С/у                   | 3,73        |
|                 |                       | 57,06       |
|                 |                       | 1594,77     |

Экспликация помещений квартир 2 этажа (корпус 2)

| Номер помещения | Наименование          | Площадь, м2 |
|-----------------|-----------------------|-------------|
| Секция 1        |                       |             |
| 2.1.4           |                       |             |
| 4.1             | Холл                  | 16,63       |
| 4.2             | Кухня-столовая        | 33,43       |
| 4.3             | Спальня               | 18,42       |
| 4.4             | Спальня с гардеробной | 20,87       |
| 4.5             | С/у                   | 6,44        |
| 4.6             | С/у                   | 4,71        |
| 4.7             | Гардеробная           | 5,13        |
|                 |                       | 105,63      |
| 2.1.5           |                       |             |
| 5.1             | Холл                  | 4,74        |
| 5.2             | Кухня-столовая        | 22,55       |
| 5.3             | Спальня с гардеробной | 20,28       |
| 5.4             | С/у                   | 5,26        |
| 5.5             | С/у                   | 2,82        |
|                 |                       | 55,65       |
| 2.1.6           |                       |             |
| 6.1             | Холл                  | 16,40       |
| 6.2             | Кухня-столовая        | 33,11       |
| 6.3             | Спальня с гардеробной | 21,76       |
| 6.4             | Спальня               | 18,46       |
| 6.5             | С/у                   | 4,87        |
| 6.6             | С/у                   | 6,84        |
| 6.7             | Гардеробная           | 5,23        |
|                 |                       | 106,67      |
| Секция 2        |                       |             |
| 2.2.15          |                       |             |
| 15.1            | Холл                  | 12,77       |
| 15.2            | Кухня-столовая        | 25,96       |
| 15.3            | Спальня с гардеробной | 19,93       |
| 15.4            | Спальня               | 16,79       |
| 15.5            | Спальня               | 12,41       |
| 15.6            | С/у                   | 4,54        |
| 15.7            | С/у                   | 2,38        |
| 15.8            | С/у                   | 7,49        |
| 15.9            | Гардеробная           | 3,68        |
|                 |                       | 105,95      |
| 2.2.16          |                       |             |
| 16.1            | Холл                  | 4,93        |
| 16.2            | Кухня-столовая        | 24,52       |
| 16.3            | Спальня с гардеробной | 18,20       |
| 16.4            | С/у                   | 4,59        |
| 16.5            | С/у                   | 3,80        |
|                 |                       | 56,04       |
| 2.2.17          |                       |             |
| 17.1            | Холл                  | 16,75       |
| 17.2            | Кухня-столовая        | 33,60       |
| 17.3            | Спальня с гардеробной | 21,18       |
| 17.4            | Спальня               | 18,43       |
| 17.5            | С/у                   | 4,71        |
| 17.6            | С/у                   | 6,59        |
| 17.7            | Гардеробная           | 5,23        |
|                 |                       | 106,49      |
|                 |                       | 536,43      |

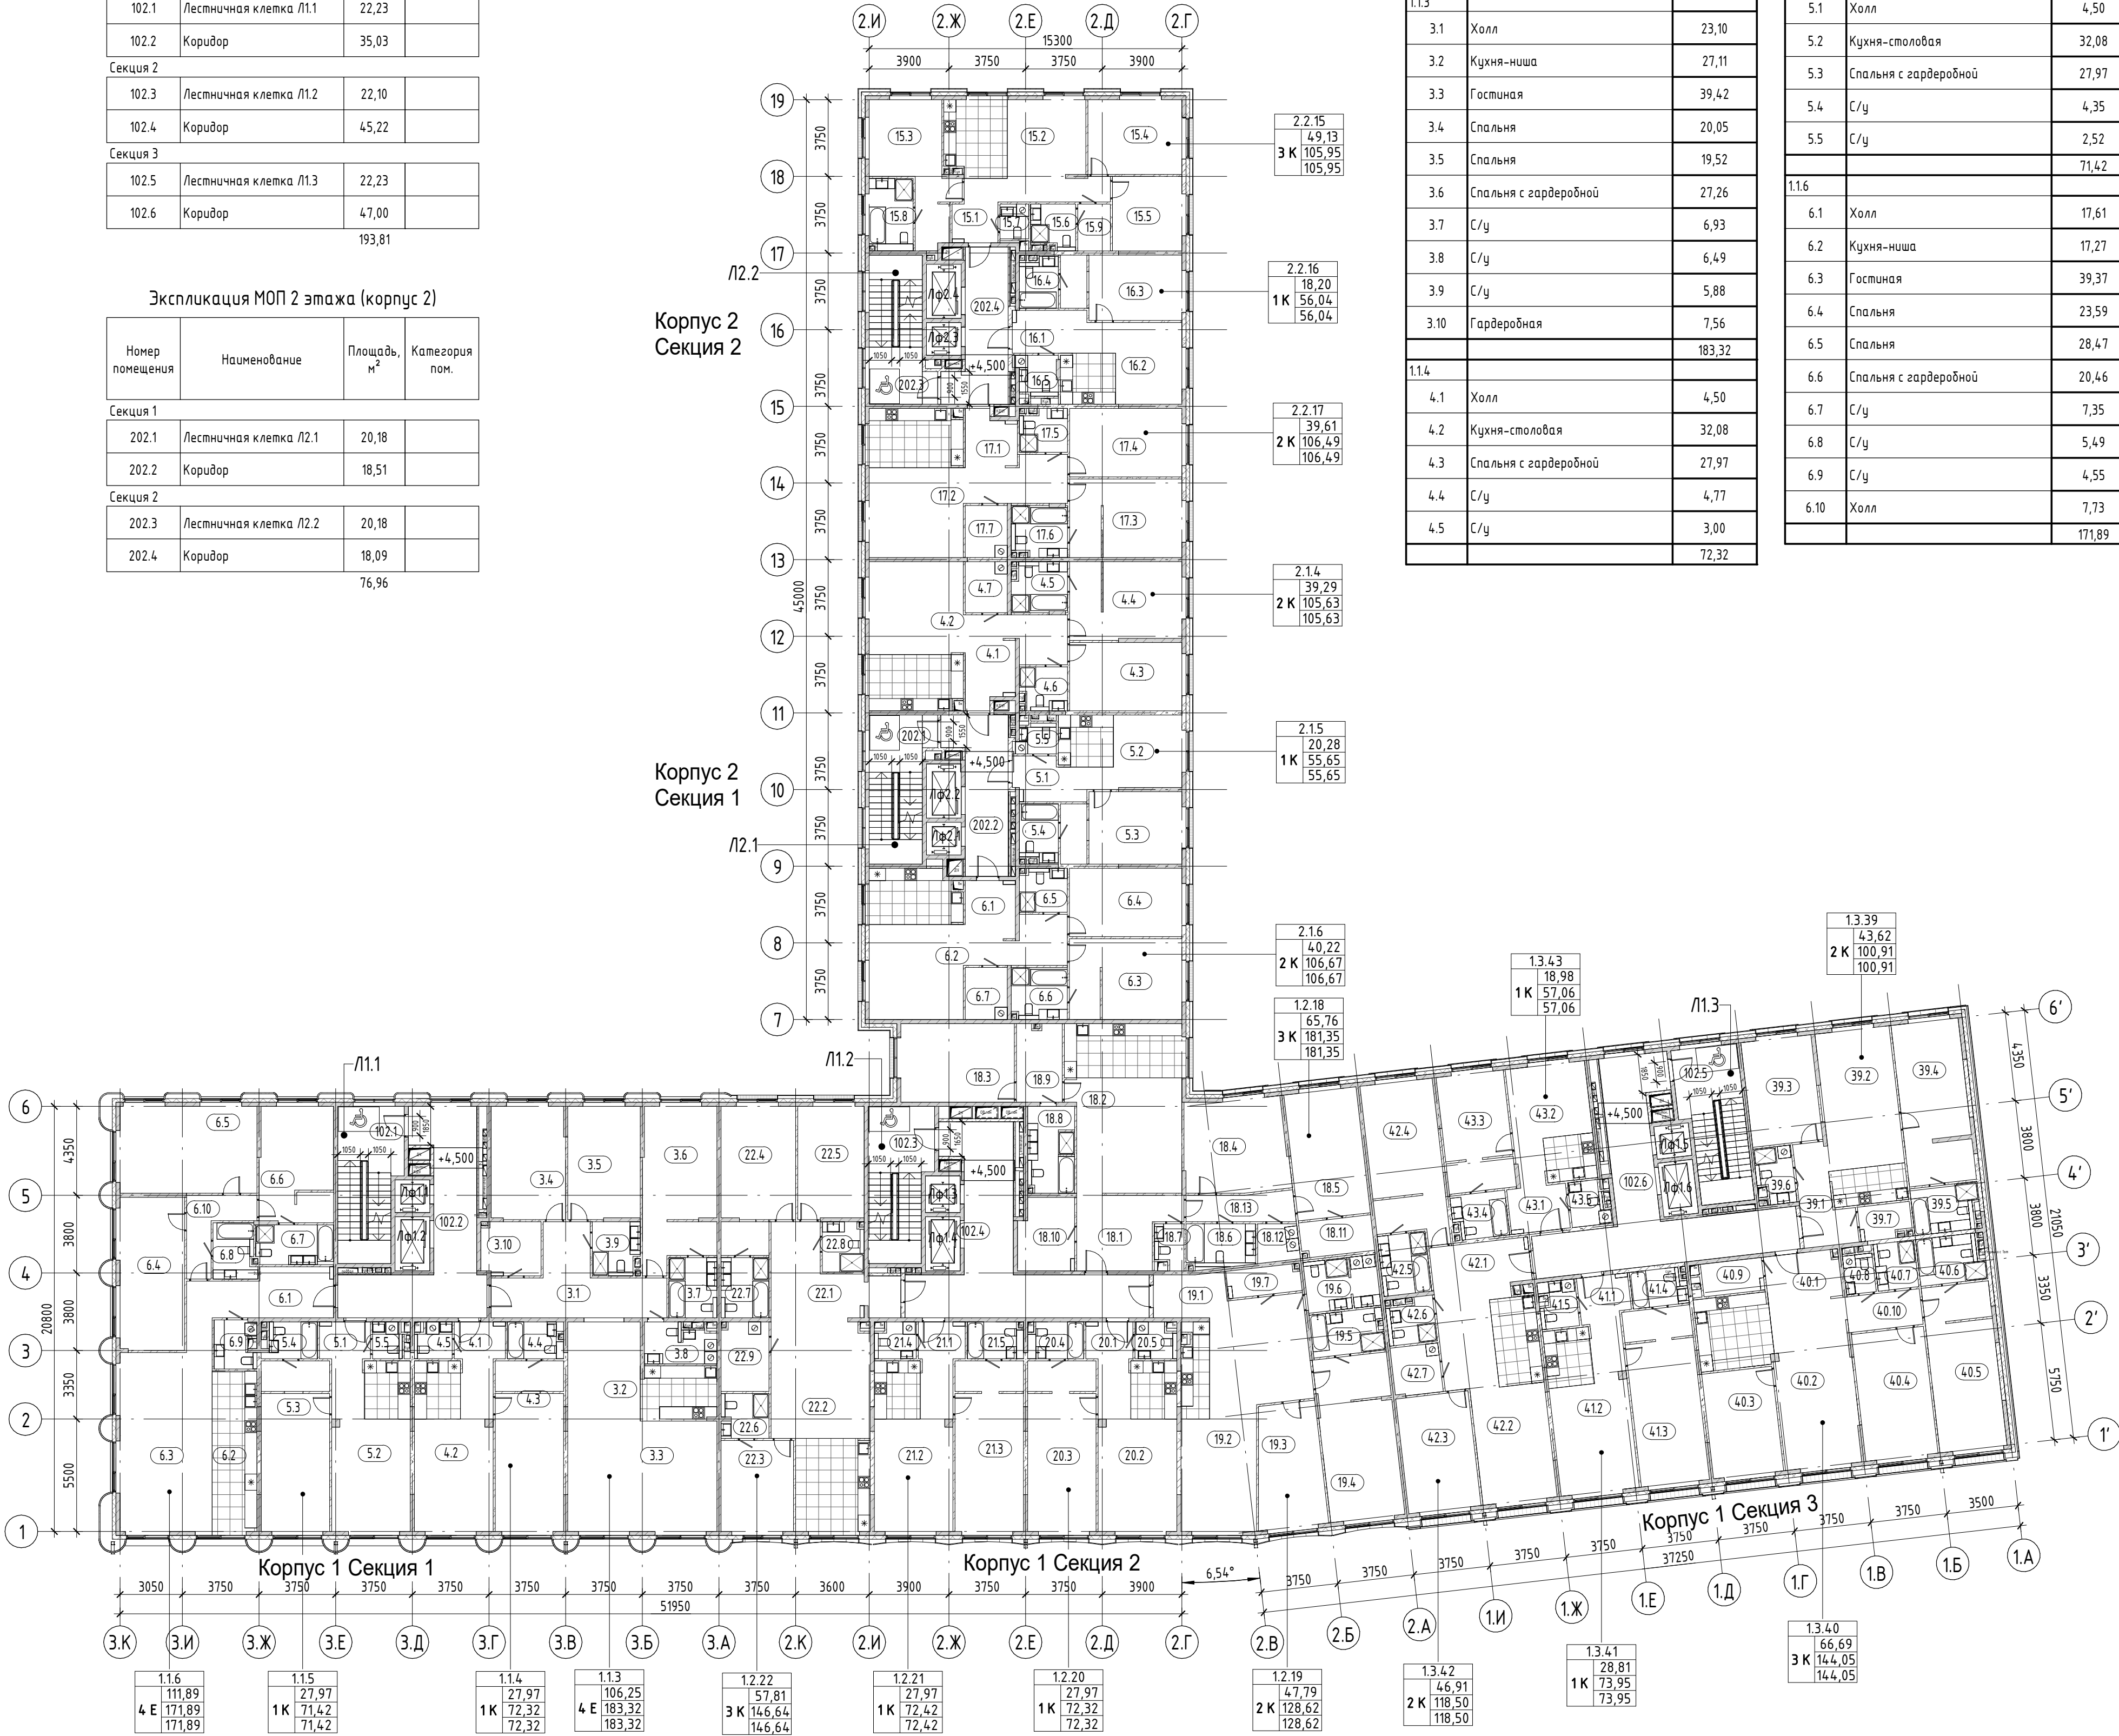


УСЛОВНЫЕ ОБОЗНАЧЕНИЯ

- железобетонные конструкции
- стена из газобетонных блоков толщ. 200 мм
- перегородка из газобетонных блоков толщ. 100 мм
- маркировка помещений квартиры
- маркировка помещений общего пользования

Марка квартиры:

|       |                                                             |
|-------|-------------------------------------------------------------|
| 33    | — номер квартиры                                            |
| 42.32 | — жилая площадь квартиры                                    |
| 82.58 | — общая площадь квартиры без учета неотапливаемых помещений |
| 85.65 | — общая площадь квартиры с учетом понижающих коэффициентов  |
| К     | — код типа планировки                                       |
| 1     | — количество жилых комнат в квартире                        |

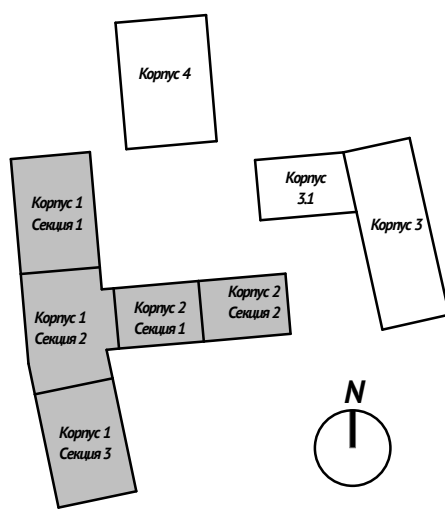



| Экспликация МОП 3 этажа (корпус 1) |                        |             |                |
|------------------------------------|------------------------|-------------|----------------|
| Номер помещения                    | Наименование           | Площадь, м² | Категория пом. |
| Секция 1                           |                        |             |                |
| 103.1                              | Лестничная клетка Л1.1 | 22,23       |                |
| 103.2                              | Коридор                | 35,03       |                |
| Секция 2                           |                        |             |                |
| 103.3                              | Лестничная клетка Л1.2 | 22,10       |                |
| 103.4                              | Коридор                | 45,22       |                |
| Секция 3                           |                        |             |                |
| 103.5                              | Лестничная клетка Л1.3 | 22,23       |                |
| 103.6                              | Коридор                | 47,02       |                |
|                                    |                        | 193,83      |                |

| Экспликация МОП 3 этажа (корпус 2) |                        |             |                |
|------------------------------------|------------------------|-------------|----------------|
| Номер помещения                    | Наименование           | Площадь, м² | Категория пом. |
| Секция 1                           |                        |             |                |
| 203.1                              | Лестничная клетка Л2.1 | 20,18       |                |
| 203.2                              | Коридор                | 18,51       |                |
| Секция 2                           |                        |             |                |
| 203.3                              | Лестничная клетка Л2.2 | 20,18       |                |
| 203.4                              | Коридор                | 18,09       |                |
|                                    |                        | 76,96       |                |

Корпус 2  
Секция 2  
Л2.2

Корпус 2  
Секция 1  
Л2.1



| Экспликация помещений квартир 3 этажа (корпус 1) |                       |             |
|--------------------------------------------------|-----------------------|-------------|
| Номер помещения                                  | Наименование          | Площадь, м² |
| Секция 1                                         |                       |             |
| 1.1.7                                            |                       |             |
| 7.1                                              | Холл                  | 23,10       |
| 7.2                                              | Кухня-ниша            | 27,11       |
| 7.3                                              | Гостиная              | 39,42       |
| 7.4                                              | Спальня               | 20,05       |
| 7.5                                              | Спальня               | 19,52       |
| 7.6                                              | Спальня с гардеробной | 27,42       |
| 7.7                                              | С/у                   | 6,93        |
| 7.8                                              | С/у                   | 6,49        |
| 7.9                                              | С/у                   | 5,88        |
| 7.10                                             | Гардеробная           | 7,56        |
|                                                  |                       | 183,48      |
| Секция 2                                         |                       |             |
| 8.1                                              | Холл                  | 4,50        |
| 8.2                                              | Кухня-столовая        | 32,08       |
| 8.3                                              | Спальня с гардеробной | 27,97       |
| 8.4                                              | С/у                   | 4,60        |
| 8.5                                              | С/у                   | 2,52        |
|                                                  |                       | 71,67       |

| Экспликация помещений квартир 3 этажа (корпус 1) |                       |             |
|--------------------------------------------------|-----------------------|-------------|
| Номер помещения                                  | Наименование          | Площадь, м² |
| Секция 1                                         |                       |             |
| 1.1.9                                            |                       |             |
| 9.1                                              | Холл                  | 4,50        |
| 9.2                                              | Кухня-столовая        | 32,08       |
| 9.3                                              | Спальня с гардеробной | 27,97       |
| 9.4                                              | С/у                   | 4,35        |
| 9.5                                              | С/у                   | 2,52        |
|                                                  |                       | 71,42       |
| Секция 2                                         |                       |             |
| 10.1                                             | Холл                  | 17,61       |
| 10.2                                             | Кухня-ниша            | 17,27       |
| 10.3                                             | Гостиная              | 39,37       |
| 10.4                                             | Спальня               | 23,59       |
| 10.5                                             | Спальня               | 28,47       |
| 10.6                                             | Спальня с гардеробной | 20,46       |
| 10.7                                             | С/у                   | 7,35        |
| 10.8                                             | С/у                   | 5,25        |
| 10.9                                             | С/у                   | 4,16        |
| 10.10                                            | Холл                  | 7,73        |
|                                                  |                       | 171,26      |

| Экспликация помещений квартир 3 этажа (корпус 1) |                       |             |
|--------------------------------------------------|-----------------------|-------------|
| Номер помещения                                  | Наименование          | Площадь, м² |
| Секция 2                                         |                       |             |
| 12.23                                            |                       |             |
| 23.1                                             | Холл                  | 15,71       |
| 23.2                                             | Кухня-столовая        | 45,18       |
| 23.3                                             | Спальня               | 21,37       |
| 23.4                                             | Спальня               | 22,38       |
| 23.5                                             | Спальня               | 22,01       |
| 23.6                                             | С/у                   | 7,14        |
| 23.7                                             | С/у                   | 2,54        |
| 23.8                                             | С/у                   | 9,30        |
| 23.9                                             | Гардеробная           | 8,16        |
| 23.10                                            | Гардеробная           | 9,51        |
| 23.11                                            | Гардеробная           | 6,09        |
| 23.12                                            | Постирочная           | 3,38        |
| 23.13                                            | Холл                  | 7,24        |
|                                                  |                       | 180,01      |
| Секция 3                                         |                       |             |
| 24.1                                             | Холл                  | 7,65        |
| 24.2                                             | Кухня-столовая        | 52,26       |
| 24.3                                             | Спальня               | 18,81       |
| 24.4                                             | Спальня с гардеробной | 28,98       |
| 24.5                                             | С/у                   | 7,23        |
| 24.6                                             | С/у                   | 8,42        |
| 24.7                                             | Гардеробная           | 4,39        |
|                                                  |                       | 127,74      |
| Секция 4                                         |                       |             |
| 25.1                                             | Холл                  | 4,14        |
| 25.2                                             | Кухня-столовая        | 32,14       |
| 25.3                                             | Спальня с гардеробной | 27,97       |
| 25.4                                             | С/у                   | 4,49        |
| 25.5                                             | С/у                   | 2,95        |
|                                                  |                       | 71,69       |
| Секция 5                                         |                       |             |
| 26.1                                             | Холл                  | 4,14        |
| 26.2                                             | Кухня-столовая        | 32,14       |
| 26.3                                             | Спальня с гардеробной | 27,97       |
| 26.4                                             | С/у                   | 2,95        |
| 26.5                                             | С/у                   | 4,62        |
|                                                  |                       | 71,82       |
| Секция 6                                         |                       |             |
| 27.1                                             | Холл                  | 19,41       |
| 27.2                                             | Кухня-столовая        | 44,40       |
| 27.3                                             | Спальня               | 15,80       |
| 27.4                                             | Спальня с гардеробной | 24,19       |
| 27.5                                             | Спальня               | 17,82       |
| 27.6                                             | С/у                   | 5,07        |
| 27.7                                             | С/у                   | 6,93        |
| 27.8                                             | С/у                   | 4,68        |
| 27.9                                             | Гардеробная           | 7,40        |
|                                                  |                       | 145,70      |

| Экспликация помещений квартир 3 этажа (корпус 1) |                       |             |
|--------------------------------------------------|-----------------------|-------------|
| Номер помещения                                  | Наименование          | Площадь, м² |
| Секция 3                                         |                       |             |
| 13.44                                            |                       |             |
| 44.1                                             | Холл                  | 10,18       |
| 44.2                                             | Кухня-столовая        | 31,39       |
| 44.3                                             | Спальня               | 17,77       |
| 44.4                                             | Спальня с гардеробной | 25,85       |
| 44.5                                             | С/у                   | 7,09        |
| 44.6                                             | С/у                   | 4,62        |
| 44.7                                             | Гардеробная           | 3,82        |
|                                                  |                       | 100,72      |
| Секция 4                                         |                       |             |
| 45.1                                             | Холл                  | 8,21        |
| 45.2                                             | Кухня-столовая        | 43,46       |
| 45.3                                             | Спальня               | 17,77       |
| 45.4                                             | Спальня с гардеробной | 22,19       |
| 45.5                                             | Спальня с гардеробной | 26,73       |
| 45.6                                             | С/у                   | 7,03        |
| 45.7                                             | С/у                   | 4,60        |
| 45.8                                             | С/у                   | 2,76        |
| 45.9                                             | Гардеробная           | 4,80        |
| 45.10                                            | Холл                  | 6,50        |
|                                                  |                       | 144,05      |
| Секция 5                                         |                       |             |
| 46.1                                             | Холл                  | 5,45        |
| 46.2                                             | Кухня-столовая        | 31,12       |
| 46.3                                             | Спальня с гардеробной | 28,81       |
| 46.4                                             | С/у                   | 4,55        |
| 46.5                                             | С/у                   | 3,57        |
|                                                  |                       | 73,50       |
| Секция 6                                         |                       |             |
| 47.1                                             | Холл                  | 10,19       |
| 47.2                                             | Кухня-столовая        | 44,17       |
| 47.3                                             | Спальня               | 20,06       |
| 47.4                                             | Спальня с гардеробной | 26,85       |
| 47.5                                             | С/у                   | 6,93        |
| 47.6                                             | С/у                   | 4,71        |
| 47.7                                             | Гардеробная           | 5,59        |
|                                                  |                       | 118,50      |
| Секция 7                                         |                       |             |
| 48.1                                             | Холл                  | 6,36        |
| 48.2                                             | Кухня-столовая        | 22,38       |
| 48.3                                             | Спальня с гардеробной | 18,98       |
| 48.4                                             | С/у                   | 5,61        |
| 48.5                                             | С/у                   | 3,73        |
|                                                  |                       | 57,06       |
|                                                  |                       | 1588,62     |


| Экспликация помещений квартир 3 этажа (корпус 2) |                       |             |
|--------------------------------------------------|-----------------------|-------------|
| Номер помещения                                  | Наименование          | Площадь, м² |
| Секция 1                                         |                       |             |
| 2.1.7                                            |                       |             |
| 7.1                                              | Холл                  | 7,82        |
| 7.2                                              | Кухня-столовая        | 41,50       |
| 7.3                                              | Спальня               | 15,94       |
| 7.4                                              | Спальня               | 14,35       |
| 7.5                                              | Спальня с гардеробной | 25,33       |
| 7.6                                              | С/у                   | 6,46        |
| 7.7                                              | С/у                   | 3,18        |
| 7.8                                              | С/у                   | 5,13        |
| 7.9                                              | Гардеробная           | 4,10        |
| 7.10                                             | Гардеробная           | 2,79        |
| 7.11                                             | Холл                  | 7,09        |
|                                                  |                       | 133,69      |
| Секция 2                                         |                       |             |
| 2.1.8                                            |                       |             |
| 8.1                                              | Холл                  | 7,23        |
| 8.2                                              | Кухня-столовая        | 41,95       |
| 8.3                                              | Спальня               | 16,36       |
| 8.4                                              | Спальня               | 14,66       |
| 8.5                                              | Спальня с гардеробной | 25,09       |
| 8.6                                              | С/у                   | 6,04        |
| 8.7                                              | С/у                   | 3,07        |
| 8.8                                              | С/у                   | 5,16        |
| 8.9                                              | Гардеробная           | 2,79        |
| 8.10                                             | Гардеробная           | 4,33        |
| 8.11                                             | Холл                  | 7,28        |
|                                                  |                       | 133,96      |
| Секция 3                                         |                       |             |
| 2.2.18                                           |                       |             |
| 18.1                                             | Холл                  | 4,24        |
| 18.2                                             | Кухня-столовая        | 31,31       |
| 18.3                                             | Спальня с гардеробной | 19,93       |
| 18.4                                             | Спальня               | 16,79       |
| 18.5                                             | Спальня               | 12,44       |
| 18.6                                             | Спальня с гардеробной | 21,30       |
| 18.7                                             | С/у                   | 6,52        |
| 18.8                                             | С/у                   | 6,00        |
| 18.9                                             | С/у                   | 7,49        |
| 18.10                                            | Гардеробная           | 2,98        |
| 18.11                                            | Холл                  | 5,28        |
|                                                  |                       | 134,28      |
| Секция 4                                         |                       |             |
| 2.2.19                                           |                       |             |
| 19.1                                             | Холл                  | 5,43        |
| 19.2                                             | Кухня-столовая        | 42,41       |
| 19.3                                             | Спальня               | 15,94       |
| 19.4                                             | Спальня               | 14,66       |
| 19.5                                             | Спальня с гардеробной | 24,21       |
| 19.6                                             | С/у                   | 6,50        |
| 19.7                                             | С/у                   | 3,34        |
| 19.8                                             | С/у                   | 5,25        |
| 19.9                                             | Гардеробная           | 4,18        |
| 19.10                                            | Гардеробная           | 4,08        |
| 19.11                                            | Холл                  | 7,50        |
|                                                  |                       | 133,50      |
|                                                  |                       | 535,43      |

#### УСЛОВНЫЕ ОБОЗНАЧЕНИЯ

- железобетонные конструкции
- стена из газобетонных блоков толщ. 200 мм
- перегородка из газобетонных блоков толщ. 100 мм
- маркировка помещений квартир
- маркировка помещений общего пользования

#### Марка квартиры:

- 33 — Номер квартиры
- 42.32 — Жилая площадь квартиры
- 82.58 — Общая площадь квартиры без учета неоплачиваемых помещений
- 85.65 — Общая площадь квартиры с учетом понижающих коэффициентов
- Код типа планировки
- Количество жилых комнат в квартире

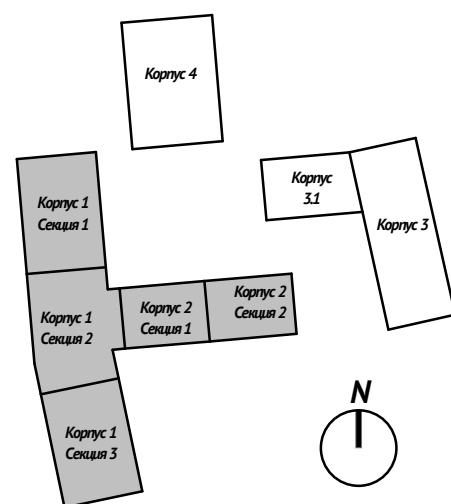

|              |           |      |        |       |        |                                                                                         |                   |      |        |
|--------------|-----------|------|--------|-------|--------|-----------------------------------------------------------------------------------------|-------------------|------|--------|
|              |           |      |        |       |        | АА/БЗ-03-ДС3 - АР1                                                                      |                   |      |        |
|              |           |      |        |       |        | "Жилой комплекс", расположенный по адресу: г. Москва, ЦАО, Садовническая ул., вл. 76/71 |                   |      |        |
| Изм.         | Жолуч     | Лист | № док. | Подп. | Дата   | Часть 1. Архитектурные решения. Планы                                                   | Стация            | Лист | Листов |
| Разработал   | Карасев   |      |        |       | 08.24. |                                                                                         | П                 | 6    |        |
| Разработал   | Задорина  |      |        |       | 08.24. |                                                                                         |                   |      |        |
| Проверил     | Добрякова |      |        |       | 08.24. |                                                                                         |                   |      |        |
| Норм. контр. | Добрякова |      |        |       | 08.24. | Корпуса 1, 2. План 3 этажа. М1_200.                                                     | A R C H I T E K T |      |        |



Экспликация МОП 4 этажа (корпус 1)

| Номер помещения | Наименование           | Площадь, м² | Категория пом. |
|-----------------|------------------------|-------------|----------------|
| Секция 1        |                        |             |                |
| 104.1           | Лестничная клетка Л1.1 | 22,23       |                |
| 104.2           | Коридор                | 35,03       |                |
| Секция 2        |                        |             |                |
| 104.3           | Лестничная клетка Л1.2 | 22,10       |                |
| 104.4           | Коридор                | 45,21       |                |
| Секция 3        |                        |             |                |
| 104.5           | Лестничная клетка Л1.3 | 22,23       |                |
| 104.6           | Коридор                | 47,00       |                |
|                 |                        | 193,80      |                |

Экспликация МОП 4 этажа (корпус 2)

| Номер помещения | Наименование           | Площадь, м² | Категория пом. |
|-----------------|------------------------|-------------|----------------|
| Секция 1        |                        |             |                |
| 204.1           | Лестничная клетка Л2.1 | 20,18       |                |
| 204.2           | Коридор                | 18,51       |                |
| Секция 2        |                        |             |                |
| 204.3           | Лестничная клетка Л2.2 | 20,18       |                |
| 204.4           | Коридор                | 18,09       |                |
|                 |                        | 76,96       |                |

Экспликация помещений квартир 4 этажа (корпус 1)

| Номер помещения | Наименование          | Площадь, м2 |
|-----------------|-----------------------|-------------|
| Секция 1        |                       |             |
| 11.11           |                       |             |
| 11.1            | Холл                  | 23,10       |
| 11.2            | Кухня-ниша            | 27,11       |
| 11.3            | Гостиная              | 39,42       |
| 11.4            | Спальня               | 20,05       |
| 11.5            | Спальня               | 19,52       |
| 11.6            | Спальня с гардеробной | 27,42       |
| 11.7            | С/у                   | 6,93        |
| 11.8            | С/у                   | 6,49        |
| 11.9            | С/у                   | 5,88        |
| 11.10           | Гардеробная           | 7,56        |
|                 |                       | 183,48      |
| 11.12           |                       |             |
| 12.1            | Холл                  | 4,50        |
| 12.2            | Кухня-столовая        | 32,08       |
| 12.3            | Спальня с гардеробной | 27,97       |
| 12.4            | С/у                   | 4,60        |
| 12.5            | С/у                   | 2,52        |
|                 |                       | 71,67       |

Экспликация помещений квартир 4 этажа (корпус 1)

| Номер помещения | Наименование          | Площадь, м2 |
|-----------------|-----------------------|-------------|
| 1.1.13          |                       |             |
| 13.1            | Холл                  | 4,50        |
| 13.2            | Кухня-столовая        | 32,08       |
| 13.3            | Спальня с гардеробной | 27,97       |
| 13.4            | С/у                   | 4,35        |
| 13.5            | С/у                   | 2,52        |
|                 |                       | 71,42       |
| 1.1.14          |                       |             |
| 14.1            | Холл                  | 17,61       |
| 14.2            | Кухня-ниша            | 17,27       |
| 14.3            | Гостиная              | 39,37       |
| 14.4            | Спальня               | 23,59       |
| 14.5            | Спальня               | 28,47       |
| 14.6            | Спальня с гардеробной | 20,46       |
| 14.7            | С/у                   | 7,35        |
| 14.8            | С/у                   | 5,25        |
| 14.9            | С/у                   | 4,16        |
| 14.10           | Холл                  | 7,73        |
|                 |                       | 171,26      |

Экспликация помещений квартир 4 этажа (корпус 1)


| Номер помещения | Наименование          | Площадь, м2 |
|-----------------|-----------------------|-------------|
| Секция 2        |                       |             |
| 12.28           |                       |             |
| 28.1            | Холл                  | 15,71       |
| 28.2            | Кухня-столовая        | 45,18       |
| 28.3            | Спальня               | 21,37       |
| 28.4            | Спальня               | 22,38       |
| 28.5            | Спальня               | 22,01       |
| 28.6            | С/у                   | 7,14        |
| 28.7            | С/у                   | 2,54        |
| 28.8            | С/у                   | 9,30        |
| 28.9            | Гардеробная           | 8,16        |
| 28.10           | Гардеробная           | 9,51        |
| 28.11           | Гардеробная           | 6,09        |
| 28.12           | Постирочная           | 3,38        |
| 28.13           | Холл                  | 7,24        |
|                 |                       | 180,01      |
| 12.29           |                       |             |
| 29.1            | Холл                  | 7,65        |
| 29.2            | Кухня-столовая        | 52,26       |
| 29.3            | Спальня               | 18,81       |
| 29.4            | Спальня с гардеробной | 28,98       |
| 29.5            | С/у                   | 7,23        |
| 29.6            | С/у                   | 8,42        |
| 29.7            | Гардеробная           | 4,39        |
|                 |                       | 127,74      |
| 12.30           |                       |             |
| 30.1            | Холл                  | 4,14        |
| 30.2            | Кухня-столовая        | 32,14       |
| 30.3            | Спальня с гардеробной | 27,97       |
| 30.4            | С/у                   | 4,49        |
| 30.5            | С/у                   | 2,95        |
|                 |                       | 71,69       |
| 12.31           |                       |             |
| 31.1            | Холл                  | 4,14        |
| 31.2            | Кухня-столовая        | 32,14       |
| 31.3            | Спальня с гардеробной | 27,97       |
| 31.4            | С/у                   | 2,95        |
| 31.5            | С/у                   | 4,62        |
|                 |                       | 71,82       |
| 12.32           |                       |             |
| 32.1            | Холл                  | 19,41       |
| 32.2            | Кухня-столовая        | 44,40       |
| 32.3            | Спальня               | 15,80       |
| 32.4            | Спальня с гардеробной | 24,19       |
| 32.5            | Спальня               | 17,82       |
| 32.6            | С/у                   | 5,07        |
| 32.7            | С/у                   | 6,93        |
| 32.8            | С/у                   | 4,68        |
| 32.9            | Гардеробная           | 7,40        |
|                 |                       | 145,70      |

Экспликация помещений квартир 4 этажа (корпус 1)

| Номер помещения | Наименование          | Площадь, м2 |
|-----------------|-----------------------|-------------|
| Секция 3        |                       |             |
| 13.49           |                       |             |
| 49.1            | Холл                  | 10,18       |
| 49.2            | Кухня-столовая        | 31,39       |
| 49.3            | Спальня               | 17,77       |
| 49.4            | Спальня с гардеробной | 25,85       |
| 49.5            | С/у                   | 7,09        |
| 49.6            | С/у                   | 4,62        |
| 49.7            | Гардеробная           | 3,82        |
|                 |                       | 100,72      |
| 13.50           |                       |             |
| 50.1            | Холл                  | 8,21        |
| 50.2            | Кухня-столовая        | 43,46       |
| 50.3            | Спальня               | 17,77       |
| 50.4            | Спальня               | 22,19       |
| 50.5            | Спальня с гардеробной | 26,73       |
| 50.6            | С/у                   | 7,03        |
| 50.7            | С/у                   | 4,60        |
| 50.8            | С/у                   | 2,76        |
| 50.9            | Гардеробная           | 4,80        |
| 50.10           | Холл                  | 6,50        |
|                 |                       | 144,05      |
| 13.51           |                       |             |
| 51.1            | Холл                  | 5,45        |
| 51.2            | Кухня-столовая        | 31,12       |
| 51.3            | Спальня с гардеробной | 28,81       |
| 51.4            | С/у                   | 4,55        |
| 51.5            | С/у                   | 3,57        |
|                 |                       | 73,50       |
| 13.52           |                       |             |
| 52.1            | Холл                  | 10,19       |
| 52.2            | Кухня-столовая        | 44,17       |
| 52.3            | Спальня               | 20,06       |
| 52.4            | Спальня с гардеробной | 26,85       |
| 52.5            | С/у                   | 6,93        |
| 52.6            | С/у                   | 4,71        |
| 52.7            | Гардеробная           | 5,59        |
|                 |                       | 118,50      |
| 13.53           |                       |             |
| 53.1            | Холл                  | 6,36        |
| 53.2            | Кухня-столовая        | 22,38       |
| 53.3            | Спальня с гардеробной | 18,98       |
| 53.4            | С/у                   | 5,61        |
| 53.5            | С/у                   | 3,73        |
|                 |                       | 57,06       |
|                 |                       | 1588,62     |

Экспликация помещений квартир 4 этажа (корпус 2)

| Номер помещения | Наименование          | Площадь, м2 |
|-----------------|-----------------------|-------------|
| Секция 1        |                       |             |
| 2.1.9           |                       |             |
| 9.1             | Холл                  | 7,82        |
| 9.2             | Кухня-столовая        | 41,50       |
| 9.3             | Спальня               | 15,94       |
| 9.4             | Спальня               | 14,35       |
| 9.5             | Спальня с гардеробной | 25,33       |
| 9.6             | С/у                   | 6,46        |
| 9.7             | С/у                   | 3,18        |
| 9.8             | С/у                   | 5,13        |
| 9.9             | Гардеробная           | 4,10        |
| 9.10            | Гардеробная           | 2,79        |
| 9.11            | Холл                  |             |
|                 |                       | 133,69      |
| 2.1.10          |                       |             |
| 10.1            | Холл                  | 7,23        |
| 10.2            | Кухня-столовая        | 41,95       |
| 10.3            | Спальня               | 16,36       |
| 10.4            | Спальня               | 14,66       |
| 10.5            | Спальня с гардеробной | 25,09       |
| 10.6            | С/у                   | 5,92        |
| 10.7            | С/у                   | 3,07        |
| 10.8            | С/у                   | 5,16        |
| 10.9            | Гардеробная           | 2,79        |
| 10.10           | Гардеробная           | 4,33        |
| 10.11           | Холл                  | 7,28        |
|                 |                       | 133,84      |
| Секция 2        |                       |             |
| 2.2.20          |                       |             |
| 20.1            | Холл                  | 4,24        |
| 20.2            | Кухня-столовая        | 31,31       |
| 20.3            | Спальня с гардеробной | 19,93       |
| 20.4            | Спальня               | 16,79       |
| 20.5            | Спальня               | 12,44       |
| 20.6            | Спальня с гардеробной | 21,30       |
| 20.7            | С/у                   | 6,52        |
| 20.8            | С/у                   | 6,00        |
| 20.9            | С/у                   | 7,49        |
| 20.10           | Гардеробная           | 2,98        |
| 20.11           | Холл                  | 5,28        |
|                 |                       | 134,28      |
| 2.2.21          |                       |             |
| 21.1            | Холл                  | 5,43        |
| 21.2            | Кухня-столовая        | 42,41       |
| 21.3            | Спальня               | 15,94       |
| 21.4            | Спальня               | 14,66       |
| 21.5            | Спальня с гардеробной | 24,21       |
| 21.6            | С/у                   | 6,50        |
| 21.7            | С/у                   | 3,34        |
| 21.8            | С/у                   | 5,25        |
| 21.9            | Гардеробная           | 4,18        |
| 21.10           | Гардеробная           | 4,08        |
| 21.11           | Холл                  | 7,50        |
|                 |                       | 133,50      |
|                 |                       | 535,31      |

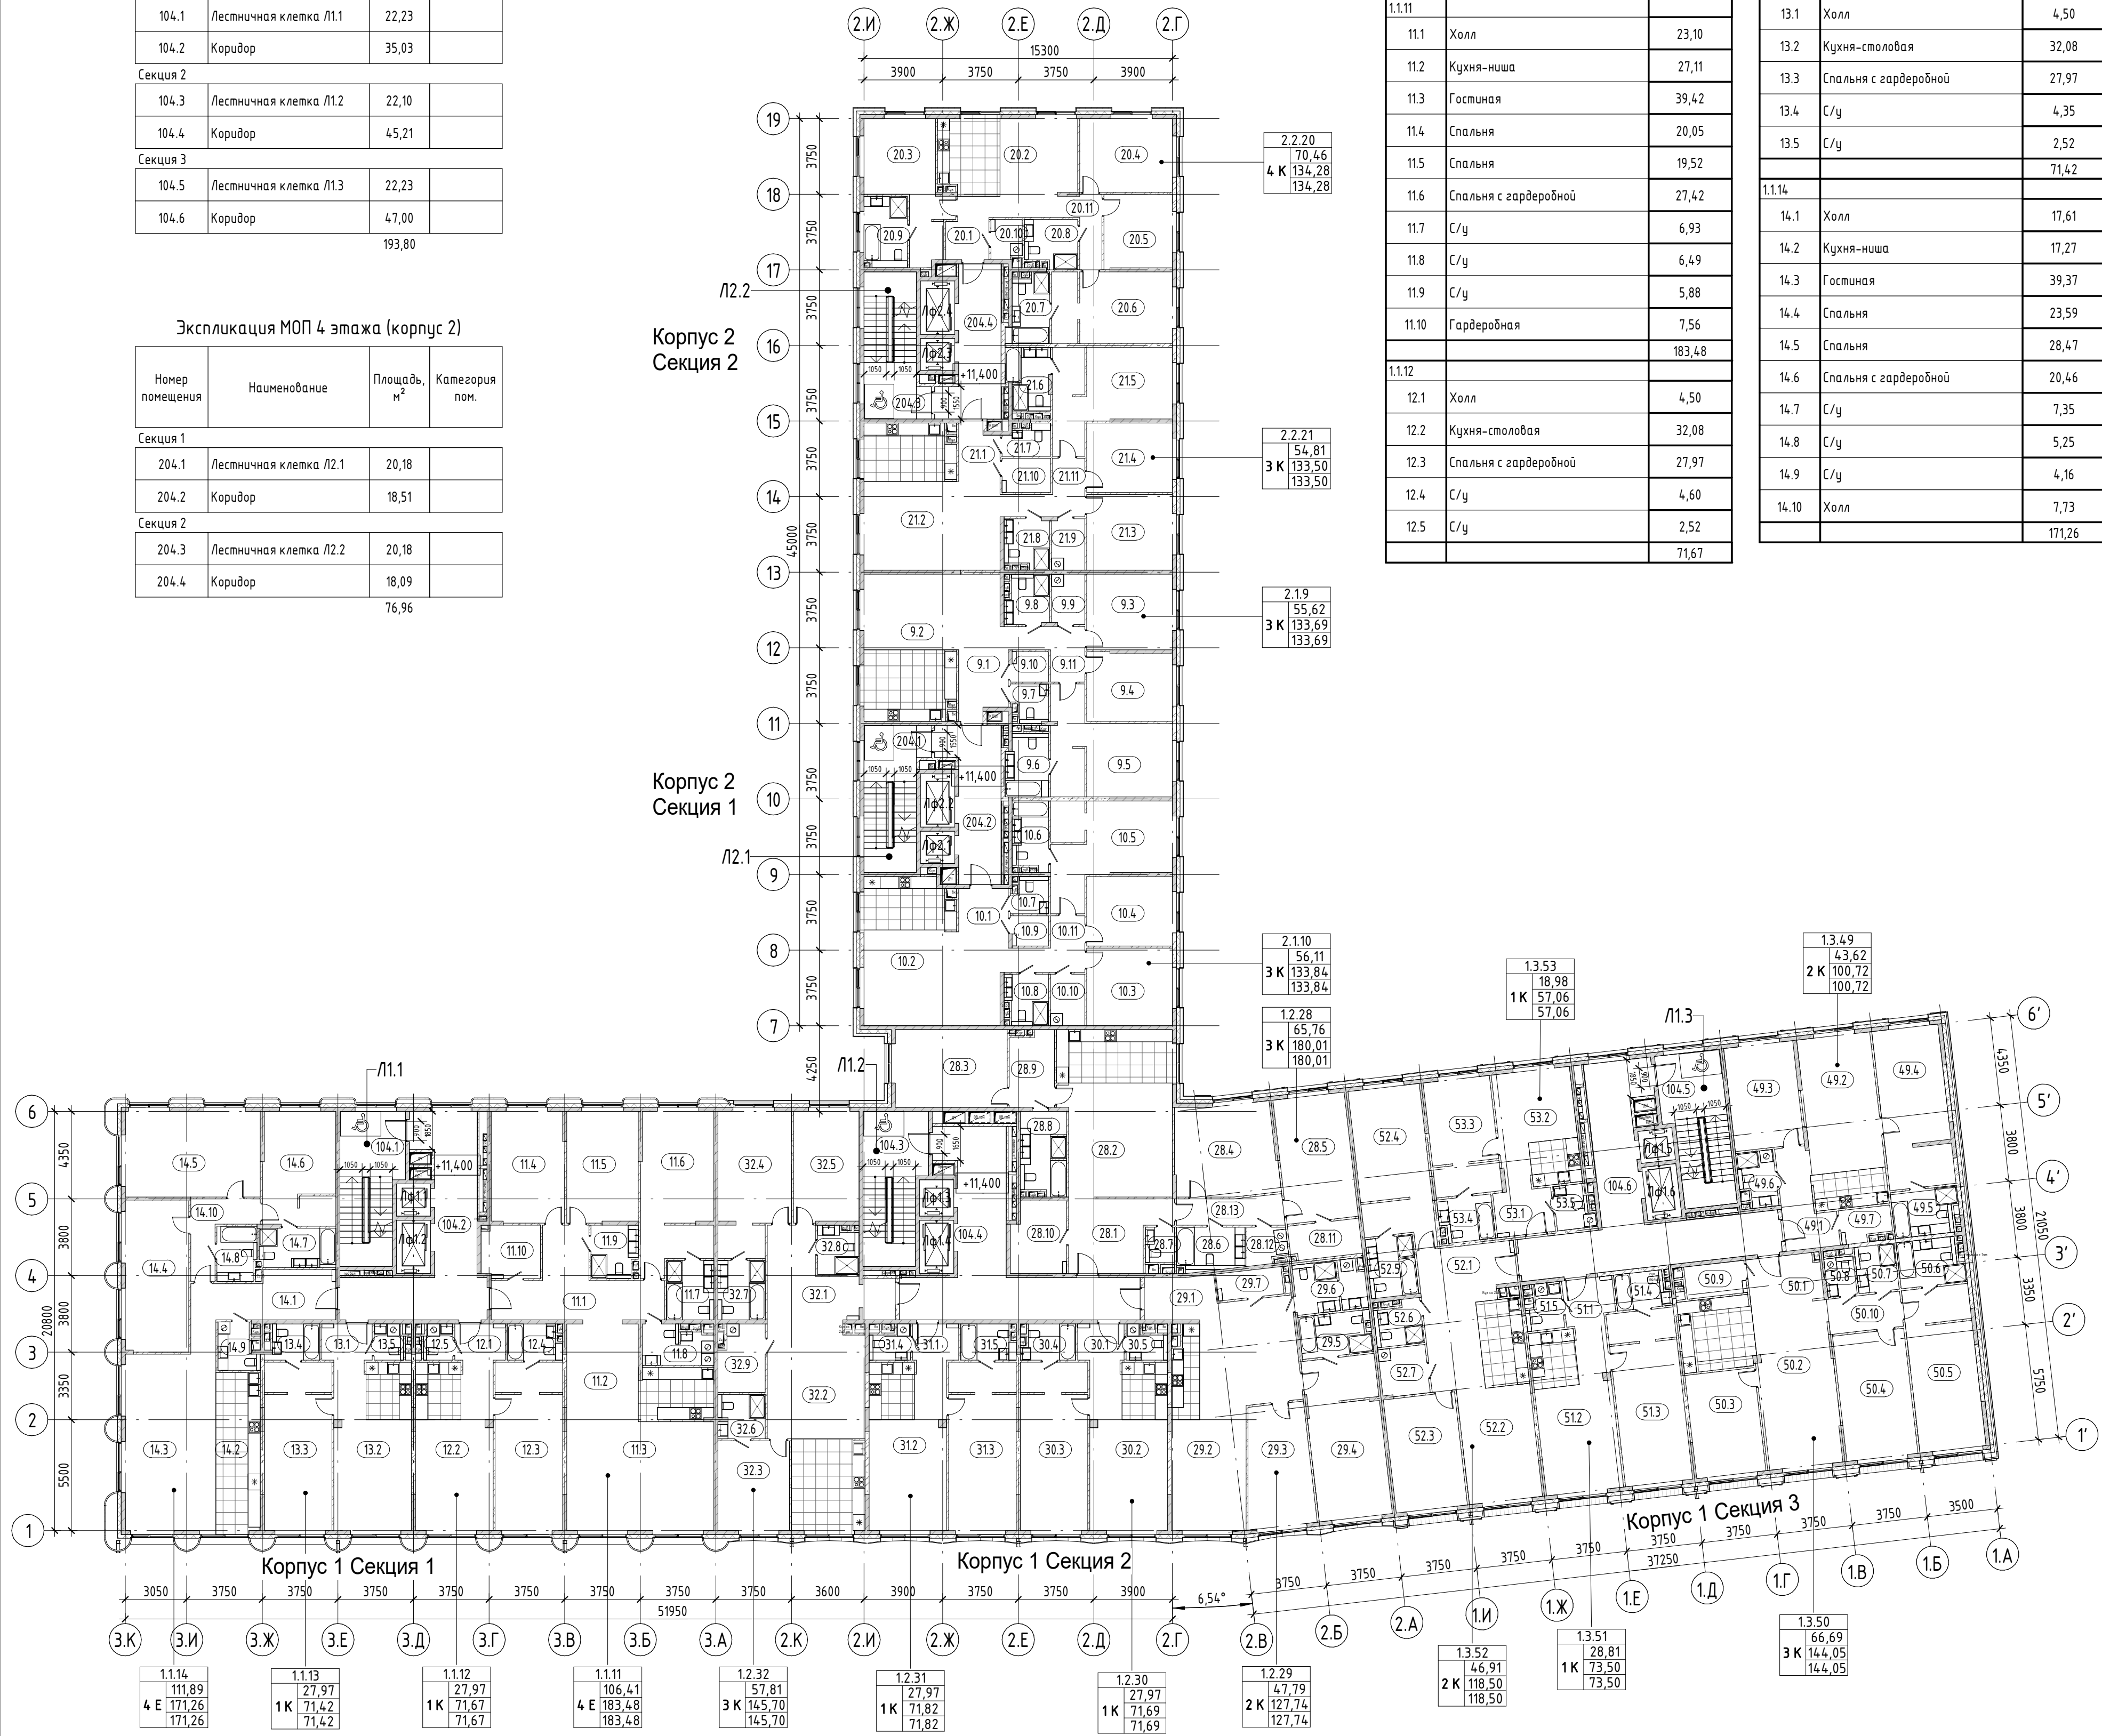


УСЛОВНЫЕ ОБОЗНАЧЕНИЯ

- железобетонные конструкции
- стена из газобетонных блоков толщ. 200 мм
- перегородка из газобетонных блоков толщ. 100 мм
- маркировка помещений квартиры
- маркировка помещений общего пользования

Марка квартиры:

|                                      |                                                             |
|--------------------------------------|-------------------------------------------------------------|
| 33                                   | — номер квартиры                                            |
| 42.32                                | — жилая площадь квартиры                                    |
| 82.58                                | — общая площадь квартиры без учета неоплачиваемых помещений |
| 85.65                                | — общая площадь квартиры с учетом понижающих коэффициентов  |
| — код типа планировки                |                                                             |
| — количество жилых комнат в квартире |                                                             |

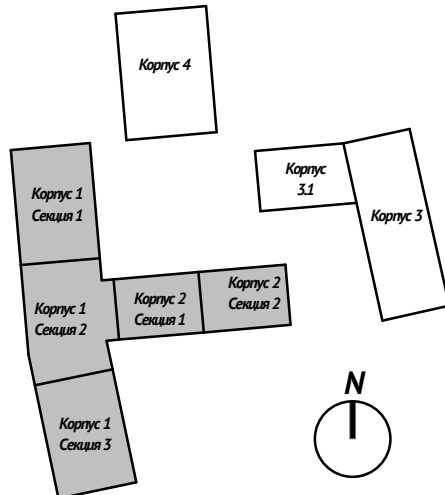



| Экспликация МОП 5 этажа (корпус 1) |                        |             |                |
|------------------------------------|------------------------|-------------|----------------|
| Номер помещения                    | Наименование           | Площадь, м² | Категория пом. |
| Секция 1                           |                        |             |                |
| 105.1                              | Лестничная клетка Л1.1 | 22,23       |                |
| 105.2                              | Коридор                | 31,25       |                |
| Секция 2                           |                        |             |                |
| 105.3                              | Лестничная клетка Л1.2 | 22,10       |                |
| 105.4                              | Коридор                | 31,25       |                |
| Секция 3                           |                        |             |                |
| 105.5                              | Коридор                | 30,20       |                |
| 105.6                              | Лестничная клетка Л1.3 | 22,23       |                |
|                                    |                        | 159,26      |                |

| Экспликация МОП 5 этажа (корпус 2) |                        |             |                |
|------------------------------------|------------------------|-------------|----------------|
| Номер помещения                    | Наименование           | Площадь, м² | Категория пом. |
| Секция 1                           |                        |             |                |
| 205.1                              | Лестничная клетка Л2.1 | 20,18       |                |
| 205.2                              | Коридор                | 18,51       |                |
| Секция 2                           |                        |             |                |
| 205.3                              | Лестничная клетка Л2.2 | 20,18       |                |
| 205.4                              | Коридор                | 18,09       |                |
|                                    |                        | 76,96       |                |

Экспликация помещений квартир 5 этажа (корпус 1)

| Номер помеще-ния | Наименование              | Площадь, м2 |
|------------------|---------------------------|-------------|
| Секция 1         |                           |             |
| 1.1.15           |                           |             |
| 15.1             | Холл                      | 5,88        |
| 15.2             | Кухня-ниша                | 7,10        |
| 15.3             | Гостиная                  | 44,32       |
| 15.4             | Спальня                   | 11,89       |
| 15.5             | Спальня                   | 20,05       |
| 15.6             | Спальня                   | 19,52       |
| 15.7             | Спальня с гардеробной     | 29,86       |
| 15.8             | С/у                       | 7,82        |
| 15.9             | С/у                       | 5,35        |
| 15.10            | С/у                       | 4,62        |
| 15.11            | Гардеробная               | 6,94        |
| 15.12            | Постирочная               | 4,61        |
| 15.13            | Холл                      | 10,22       |
| 15.14            | Терраса (коэффициент 0,3) | 23,67       |
|                  |                           | 201,85      |
| 1.1.16           |                           |             |
| 16.1             | Холл                      | 3,51        |
| 16.2             | Кухня-столовая            | 16,92       |
| 16.3             | Гостиная                  | 90,96       |
| 16.4             | Спальня                   | 13,39       |
| 16.5             | Кабинет                   | 10,69       |
| 16.6             | Спальня с гардеробной     | 20,19       |
| 16.7             | С/у                       | 4,83        |
| 16.8             | С/у                       | 6,94        |
| 16.9             | С/у                       | 2,40        |
| 16.10            | Гардеробная               | 2,91        |
| 16.11            | Терраса (коэффициент 0,3) | 21,71       |
|                  |                           | 194,45      |

Экспликация помещений квартир 5 этажа (корпус 1)

| Номер помеще-ния | Наименование              | Площадь, м2 |
|------------------|---------------------------|-------------|
| Секция 2         |                           |             |
| 1.2.33           |                           |             |
| 33.1             | Холл                      | 19,21       |
| 33.2             | Кухня-столовая            | 59,21       |
| 33.3             | Спальня с гардеробной     | 20,21       |
| 33.4             | Спальня с гардеробной     | 31,91       |
| 33.5             | Спальня с гардеробной     | 29,15       |
| 33.6             | Спальня                   | 22,10       |
| 33.7             | Спальня                   | 21,40       |
| 33.8             | С/у                       | 4,67        |
| 33.9             | С/у                       | 9,30        |
| 33.10            | С/у                       | 2,42        |
| 33.11            | С/у                       | 5,60        |
| 33.12            | С/у                       | 4,23        |
| 33.13            | Гардеробная               | 9,43        |
| 33.14            | Холл                      | 4,32        |
| 33.15            | Холл                      | 4,72        |
| 33.16            | Терраса (коэффициент 0,3) | 17,28       |
|                  |                           | 265,16      |
| 1.2.34           |                           |             |
| 34.1             | Холл                      | 6,72        |
| 34.2             | Кухня-столовая            | 58,25       |
| 34.3             | Спальня                   | 16,74       |
| 34.4             | Спальня                   | 23,46       |
| 34.5             | Спальня с гардеробной     | 27,69       |
| 34.6             | Спальня с гардеробной     | 18,39       |
| 34.7             | С/у                       | 6,09        |
| 34.8             | С/у                       | 8,52        |
| 34.9             | С/у                       | 3,28        |
| 34.10            | С/у                       | 4,93        |
| 34.11            | Гардеробная               | 4,41        |
| 34.12            | Постирочная               | 4,76        |
| 34.13            | Холл                      | 8,32        |
| 34.14            | Терраса (коэффициент 0,3) | 33,95       |
|                  |                           | 225,51      |

Экспликация помещений квартир 5 этажа (корпус 1)

| Номер помеще-ния | Наименование              | Площадь, м2 |
|------------------|---------------------------|-------------|
| Секция 3         |                           |             |
| 1.3.54           |                           |             |
| 54.1             | Холл                      | 10,44       |
| 54.2             | Кухня-столовая            | 50,51       |
| 54.3             | Спальня                   | 12,56       |
| 54.4             | Спальня с гардеробной     | 22,09       |
| 54.5             | Спальня с гардеробной     | 23,42       |
| 54.6             | Спальня с гардеробной     | 25,85       |
| 54.7             | С/у                       | 3,66        |
| 54.8             | С/у                       | 4,63        |
| 54.9             | С/у                       | 7,09        |
| 54.10            | Гардеробная               | 4,16        |
| 54.11            | Постирочная               | 2,16        |
| 54.12            | Холл                      | 8,30        |
| 54.13            | Терраса (коэффициент 0,3) | 23,05       |
|                  |                           | 197,92      |
| 1.3.55           |                           |             |
| 55.1             | Холл                      | 7,04        |
| 55.2             | Кухня-столовая            | 55,47       |
| 55.3             | Спальня с гардеробной     | 26,63       |
| 55.4             | Спальня                   | 19,66       |
| 55.5             | Спальня                   | 21,85       |
| 55.6             | Спальня                   | 12,56       |
| 55.7             | С/у                       | 8,61        |
| 55.8             | С/у                       | 5,36        |
| 55.9             | С/у                       | 3,89        |
| 55.10            | Гардеробная               | 5,89        |
| 55.11            | Постирочная               | 2,31        |
| 55.12            | Холл                      | 9,95        |
| 55.13            | Терраса (коэффициент 0,3) | 24,04       |
|                  |                           | 203,26      |
|                  |                           | 1288,15     |

Экспликация помещений квартир 5 этажа (корпус 2)

| Номер помеще-ния | Наименование          | Площадь, м2 |
|------------------|-----------------------|-------------|
| Секция 1         |                       |             |
| 2.1.11           |                       |             |
| 11.1             | Холл                  | 7,82        |
| 11.2             | Кухня-столовая        | 41,50       |
| 11.3             | Спальня               | 15,94       |
| 11.4             | Спальня               | 14,35       |
| 11.5             | Спальня с гардеробной | 25,33       |
| 11.6             | С/у                   | 6,46        |
| 11.7             | С/у                   | 3,18        |
| 11.8             | С/у                   | 5,13        |
| 11.9             | Гардеробная           | 4,10        |
| 11.10            | Гардеробная           | 2,79        |
| 11.11            | Холл                  | 7,09        |
|                  |                       | 133,69      |
| 2.1.12           |                       |             |
| 12.1             | Холл                  | 7,23        |
| 12.2             | Кухня-столовая        | 41,95       |
| 12.3             | Спальня               | 16,36       |
| 12.4             | Спальня               | 14,66       |
| 12.5             | Спальня с гардеробной | 25,09       |
| 12.6             | С/у                   | 5,92        |
| 12.7             | С/у                   | 3,07        |
| 12.8             | С/у                   | 5,16        |
| 12.9             | Гардеробная           | 2,79        |
| 12.10            | Гардеробная           | 4,33        |
| 12.11            | Холл                  | 7,28        |
|                  |                       | 133,84      |
| Секция 2         |                       |             |
| 2.2.22           |                       |             |
| 22.1             | Холл                  | 4,24        |
| 22.2             | Кухня-столовая        | 31,31       |
| 22.3             | Спальня с гардеробной | 19,93       |
| 22.4             | Спальня               | 16,79       |
| 22.5             | Спальня               | 12,44       |
| 22.6             | Спальня с гардеробной | 21,30       |
| 22.7             | С/у                   | 6,52        |
| 22.8             | С/у                   | 6,00        |
| 22.9             | С/у                   | 7,49        |
| 22.10            | Гардеробная           | 2,98        |
| 22.11            | Холл                  | 5,28        |
|                  |                       | 134,28      |
| 2.2.23           |                       |             |
| 23.1             | Холл                  | 5,43        |
| 23.2             | Кухня-столовая        | 42,41       |
| 23.3             | Спальня               | 15,94       |
| 23.4             | Спальня               | 14,66       |
| 23.5             | Спальня с гардеробной | 24,21       |
| 23.6             | С/у                   | 6,50        |
| 23.7             | С/у                   | 3,34        |
| 23.8             | С/у                   | 5,25        |
| 23.9             | Гардеробная           | 4,18        |
| 23.10            | Гардеробная           | 4,08        |
| 23.11            | Холл                  | 7,50        |
|                  |                       | 133,50      |
|                  |                       | 535,31      |



УСЛОВНЫЕ ОБОЗНАЧЕНИЯ

- железобетонные конструкции
- стена из газобетонных блоков толщ. 200 мм
- перегородка из газобетонных блоков толщ. 100 мм

- 57 — маркировка помещений квартиры
- 1015 — маркировка помещений общего пользования

Марка квартиры:

- 33 — Номер квартиры
- 4232 — Жилая площадь квартиры
- 8258 — Общая площадь квартиры без учета неоплачиваемых помещений
- 8565 — Общая площадь квартиры с учетом планижаемых коэффициентов
- Код типа планировки
- Количество жилых комнат в квартире





|              |        |      |        |           |       |                                                                                         |             |      |        |
|--------------|--------|------|--------|-----------|-------|-----------------------------------------------------------------------------------------|-------------|------|--------|
|              |        |      |        |           |       | AA/БЗ-03-ДС3 - AP1                                                                      |             |      |        |
|              |        |      |        |           |       | "Жилой комплекс", расположенный по адресу: г. Москва, ЦАО, Садовническая ул., вл. 76/71 |             |      |        |
| Изм.         | Жол.ч. | Лист | № док. | Подп.     | Дата  | Часть 1. Архитектурные решения, Планы                                                   | Стация      | Лист | Листов |
| Разработал   |        |      |        | Карасёв   | 08.24 |                                                                                         | П           | 8    |        |
| Разработал   |        |      |        | Задорина  | 08.24 |                                                                                         |             |      |        |
| Проверил     |        |      |        | Добрякова | 08.24 |                                                                                         |             |      |        |
| Норм. контр. |        |      |        | Добрякова | 08.24 | Корпуса 1, 2. План 5 этажа. М 1_200.                                                    | АРХИТЕКТУРА |      |        |



| Номер помещения | Наименование            | Площадь, м <sup>2</sup> | Категория пом. |
|-----------------|-------------------------|-------------------------|----------------|
| Секция 1        |                         |                         |                |
| 206.1           | Лестничная клетка Л/2.1 | 20,18                   |                |
| 206.2           | Коридор                 | 18,51                   |                |
|                 |                         | 38,69                   |                |

| Номер помещения | Наименование            | Площадь, м² | Категория пом. |
|-----------------|-------------------------|-------------|----------------|
| <b>Секция 1</b> |                         |             |                |
| 206.1           | Лестничная клетка /12.1 | 20,18       |                |
| 206.2           | Коридор                 | 18,51       |                |
|                 |                         | 38,69       |                |

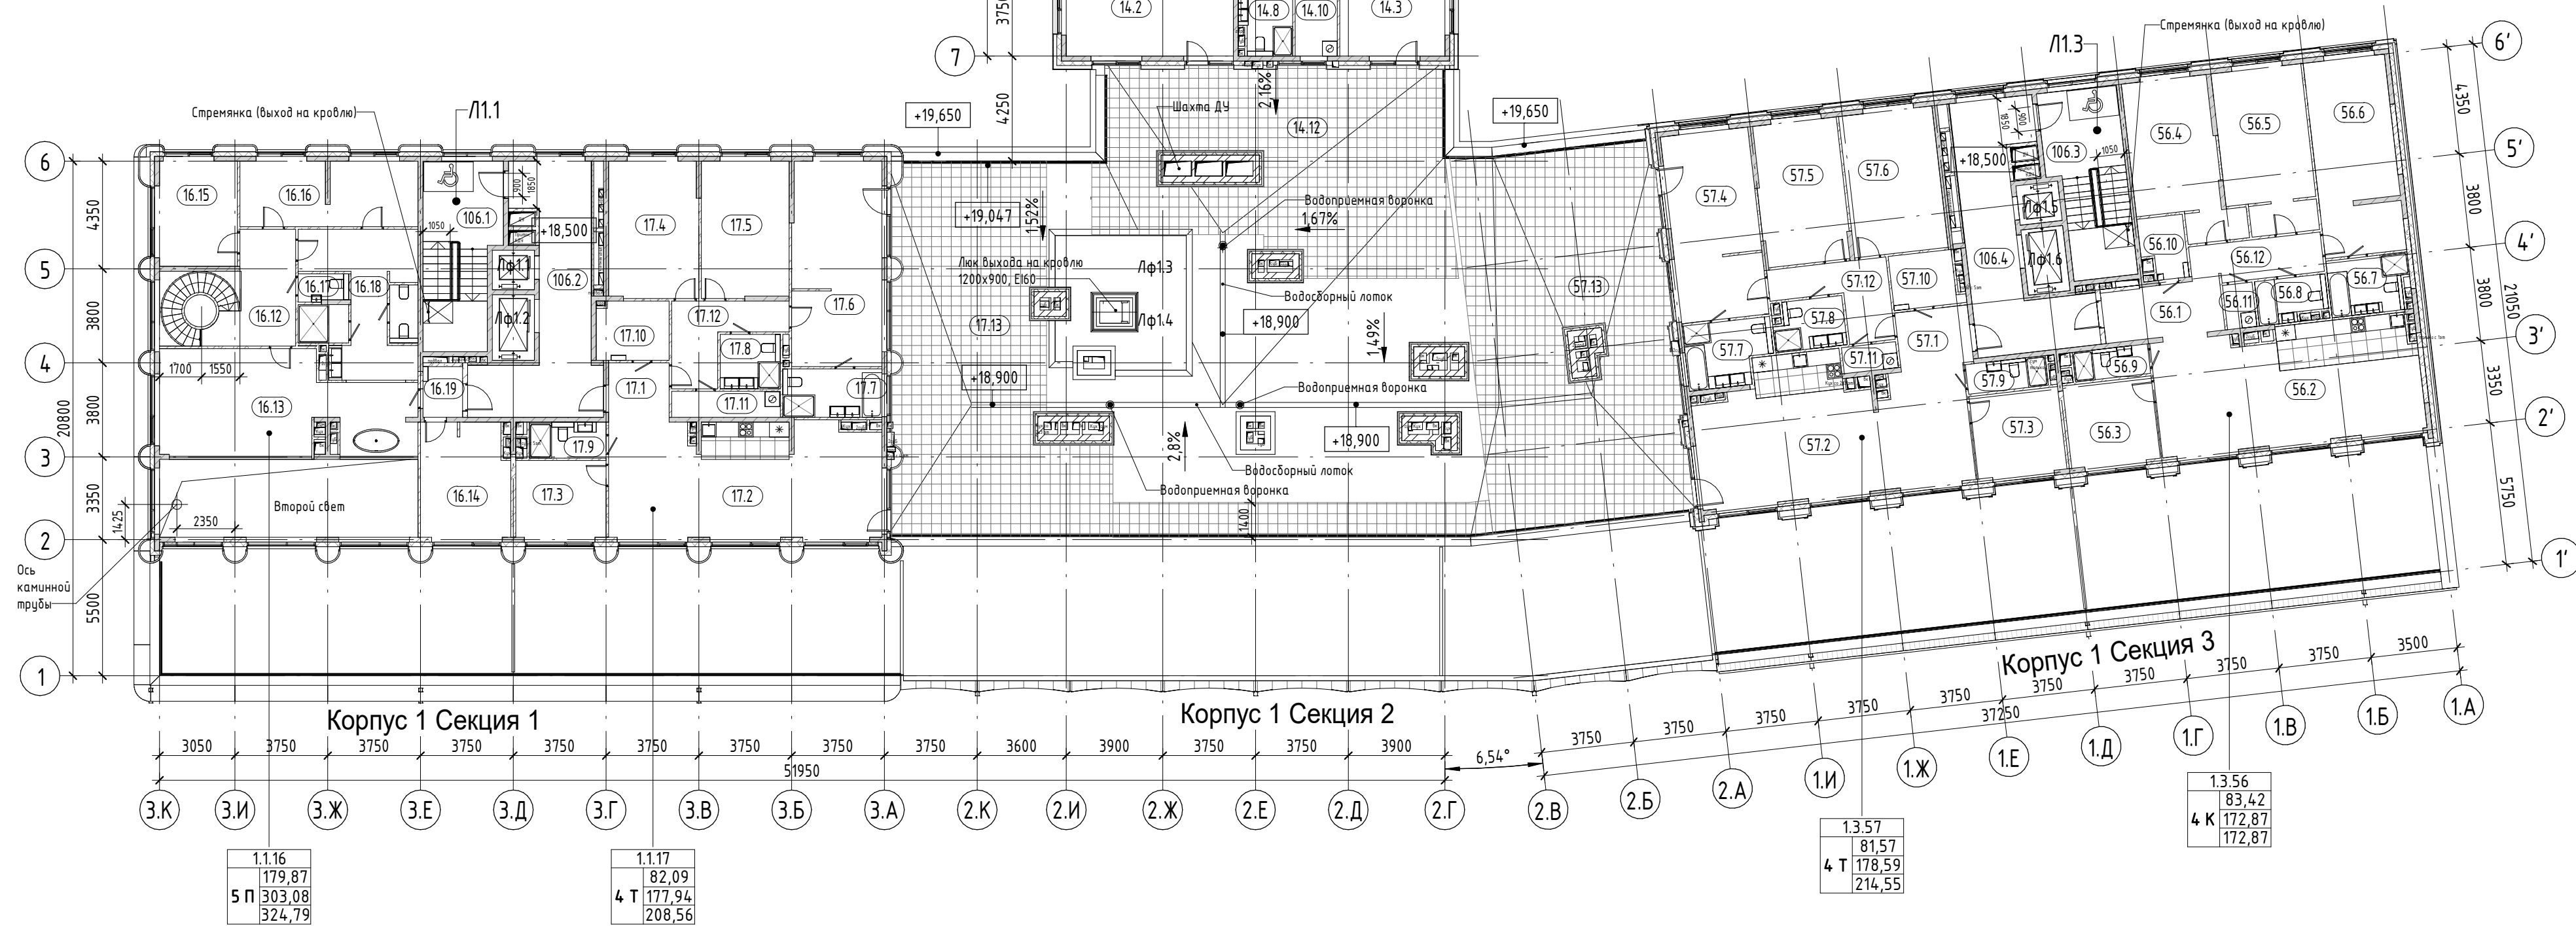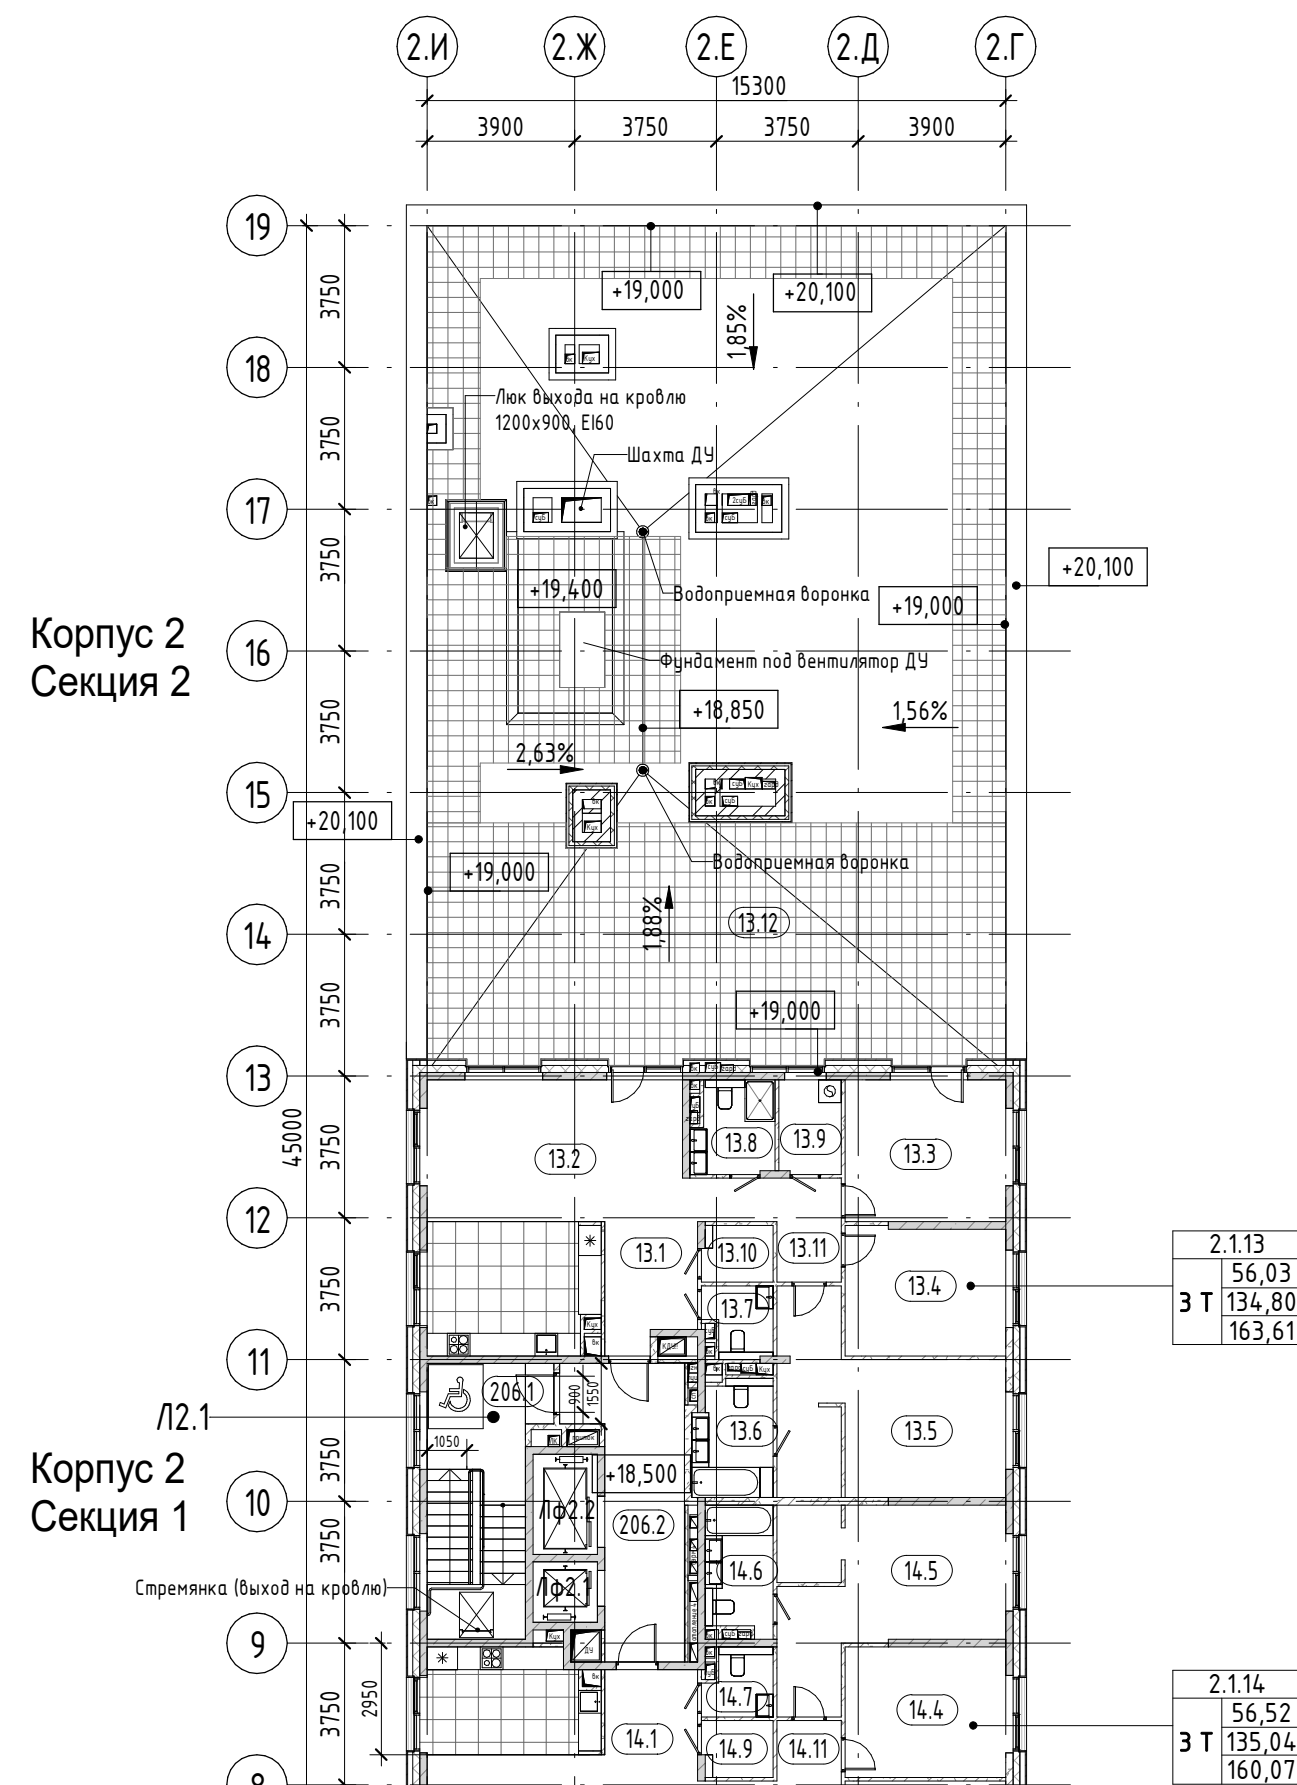

| Номер помеще-ния | Наименование              | Площадь, м2 |
|------------------|---------------------------|-------------|
| Секция 1         |                           |             |
| 11.16            |                           |             |
| 16.12            | Холл                      | 12,53       |
| 16.13            | Спальня с гардеробной     | 38,98       |
| 16.14            | Спальня                   | 16,35       |
| 16.15            | Кабинет                   | 13,39       |
| 16.16            | Кабинет                   | 18,73       |
| 16.17            | С/у                       | 2,24        |
| 16.18            | С/у                       | 24,84       |
| 16.19            | Гардеробная               | 3,28        |
|                  |                           | 130,34      |
| 11.17            |                           |             |
| 17.1             | Холл                      | 5,88        |
| 17.2             | Кухня-столовая            | 50,53       |
| 17.3             | Спальня                   | 11,32       |
| 17.4             | Спальня                   | 20,05       |
| 17.5             | Спальня                   | 19,52       |
| 17.6             | Спальня с гардеробной     | 31,20       |
| 17.7             | С/у                       | 7,82        |
| 17.8             | С/у                       | 5,35        |
| 17.9             | С/у                       | 4,50        |
| 17.10            | Гардеробная               | 6,94        |
| 17.11            | Постирочная               | 4,61        |
| 17.12            | Холл                      | 10,22       |
| 17.13            | Терраса (коэффициент 0,3) | 30,62       |
|                  |                           | 208,56      |

| Номер помеще-<br>ния | Наименование              | Площадь, м2 |
|----------------------|---------------------------|-------------|
| Секция 1             |                           |             |
| 11.16                |                           |             |
| 16.12                | Холл                      | 12,53       |
| 16.13                | Спальня с гардеробной     | 38,98       |
| 16.14                | Спальня                   | 16,35       |
| 16.15                | Кабинет                   | 13,39       |
| 16.16                | Кабинет                   | 18,73       |
| 16.17                | С/у                       | 2,24        |
| 16.18                | С/у                       | 24,84       |
| 16.19                | Гардеробная               | 3,28        |
|                      |                           | 130,34      |
| 11.17                |                           |             |
| 17.1                 | Холл                      | 5,88        |
| 17.2                 | Кухня-столовая            | 50,53       |
| 17.3                 | Спальня                   | 11,32       |
| 17.4                 | Спальня                   | 20,05       |
| 17.5                 | Спальня                   | 19,52       |
| 17.6                 | Спальня с гардеробной     | 31,20       |
| 17.7                 | С/у                       | 7,82        |
| 17.8                 | С/у                       | 5,35        |
| 17.9                 | С/у                       | 4,50        |
| 17.10                | Гардеробная               | 6,94        |
| 17.11                | Пастирочная               | 4,61        |
| 17.12                | Холл                      | 10,22       |
| 17.13                | Терраса (коэффициент 0,3) | 30,62       |
|                      |                           | 208,56      |

| Номер помеще-ния | Наименование              | Площадь, м2 |
|------------------|---------------------------|-------------|
| Секция 3         |                           |             |
| 13.56            |                           |             |
| 56.1             | Холл                      | 10,44       |
| 56.2             | Кухня-столовая            | 49,01       |
| 56.3             | Спальня                   | 12,06       |
| 56.4             | Спальня с гардеробной     | 22,09       |
| 56.5             | Спальня с гардеробной     | 23,42       |
| 56.6             | Спальня с гардеробной     | 25,85       |
| 56.7             | С/у                       | 7,09        |
| 56.8             | С/у                       | 4,63        |
| 56.9             | С/у                       | 3,66        |
| 56.10            | Гардеробная               | 4,16        |
| 56.11            | Постирочная               | 2,16        |
| 56.12            | Холл                      | 8,30        |
|                  |                           | 172,87      |
| 13.57            |                           |             |
| 57.1             | Холл                      | 7,04        |
| 57.2             | Кухня-столовая            | 54,46       |
| 57.3             | Спальня                   | 12,06       |
| 57.4             | Спальня с гардеробной     | 28,00       |
| 57.5             | Спальня                   | 19,66       |
| 57.6             | Спальня                   | 21,85       |
| 57.7             | С/у                       | 8,26        |
| 57.8             | С/у                       | 5,36        |
| 57.9             | С/у                       | 3,89        |
| 57.10            | Гардеробная               | 5,75        |
| 57.11            | Постирочная               | 2,31        |
| 57.12            | Холл                      | 9,95        |
| 57.13            | Терраса (коэффициент 0,3) | 35,56       |
|                  |                           | 214,55      |
|                  |                           | 726,32      |

| Номер помеще-<br>ния | Наименование              | Площадь, м2 |
|----------------------|---------------------------|-------------|
| Секция 3             |                           |             |
| 13.56                |                           |             |
| 56.1                 | Холл                      | 10,44       |
| 56.2                 | Кухня-столовая            | 49,01       |
| 56.3                 | Спальня                   | 12,06       |
| 56.4                 | Спальня с гардеробной     | 22,09       |
| 56.5                 | Спальня с гардеробной     | 23,42       |
| 56.6                 | Спальня с гардеробной     | 25,85       |
| 56.7                 | С/у                       | 7,09        |
| 56.8                 | С/у                       | 4,63        |
| 56.9                 | С/у                       | 3,66        |
| 56.10                | Гардеробная               | 4,16        |
| 56.11                | Постирочная               | 2,16        |
| 56.12                | Холл                      | 8,30        |
|                      |                           | 172,87      |
| 13.57                |                           |             |
| 57.1                 | Холл                      | 7,04        |
| 57.2                 | Кухня-столовая            | 54,46       |
| 57.3                 | Спальня                   | 12,06       |
| 57.4                 | Спальня с гардеробной     | 28,00       |
| 57.5                 | Спальня                   | 19,66       |
| 57.6                 | Спальня                   | 21,85       |
| 57.7                 | С/у                       | 8,26        |
| 57.8                 | С/у                       | 5,36        |
| 57.9                 | С/у                       | 3,89        |
| 57.10                | Гардеробная               | 5,75        |
| 57.11                | Постирочная               | 2,31        |
| 57.12                | Холл                      | 9,95        |
| 57.13                | Терраса (коэффициент 0,3) | 35,96       |
|                      |                           | 214,55      |
|                      |                           | 126,32      |

| Номер помеще-<br>ния | Наименование              | Площадь, м2 |
|----------------------|---------------------------|-------------|
| Секция 1             |                           |             |
| 2.1.13               |                           |             |
| 13.1                 | Холл                      | 7,82        |
| 13.2                 | Кухня-столовая            | 42,31       |
| 13.3                 | Спальня                   | 16,35       |
| 13.4                 | Спальня                   | 14,35       |
| 13.5                 | Спальня с гардеробной     | 25,33       |
| 13.6                 | С/у                       | 6,35        |
| 13.7                 | С/у                       | 3,18        |
| 13.8                 | С/у                       | 5,13        |
| 13.9                 | Гардеробная               | 4,10        |
| 13.10                | Гардеробная               | 2,79        |
| 13.11                | Холл                      | 7,09        |
| 13.12                | Терраса (коэффициент 0,3) | 28,81       |
|                      |                           | 163,61      |
| 2.1.14               |                           |             |
| 14.1                 | Холл                      | 5,51        |
| 14.2                 | Кухня-столовая            | 44,46       |
| 14.3                 | Спальня                   | 16,77       |
| 14.4                 | Спальня                   | 14,66       |
| 14.5                 | Спальня с гардеробной     | 25,09       |
| 14.6                 | С/у                       | 5,92        |
| 14.7                 | С/у                       | 3,07        |
| 14.8                 | С/у                       | 5,16        |
| 14.9                 | Гардеробная               | 2,79        |
| 14.10                | Гардеробная               | 4,33        |
| 14.11                | Холл                      | 7,28        |
| 14.12                | Терраса (коэффициент 0,3) | 25,03       |
|                      |                           | 160,07      |
|                      |                           | 323,68      |

| Номер помеще-ния | Наименование              | Площадь, м2 |
|------------------|---------------------------|-------------|
| Секция 1         |                           |             |
| 2.1.13           |                           |             |
| 13.1             | Холл                      | 7,82        |
| 13.2             | Кухня-столовая            | 42,31       |
| 13.3             | Спальня                   | 16,35       |
| 13.4             | Спальня                   | 14,35       |
| 13.5             | Спальня с гардеробной     | 25,33       |
| 13.6             | С/у                       | 6,35        |
| 13.7             | С/у                       | 3,18        |
| 13.8             | С/у                       | 5,13        |
| 13.9             | Гардеробная               | 4,10        |
| 13.10            | Гардеробная               | 2,79        |
| 13.11            | Холл                      | 7,09        |
| 13.12            | Терраса (коэффициент 0,3) | 28,81       |
|                  |                           | 163,61      |
| 2.1.14           |                           |             |
| 14.1             | Холл                      | 5,51        |
| 14.2             | Кухня-столовая            | 44,46       |
| 14.3             | Спальня                   | 16,77       |
| 14.4             | Спальня                   | 14,66       |
| 14.5             | Спальня с гардеробной     | 25,09       |
| 14.6             | С/у                       | 5,92        |
| 14.7             | С/у                       | 3,07        |
| 14.8             | С/у                       | 5,16        |
| 14.9             | Гардеробная               | 2,79        |
| 14.10            | Гардеробная               | 4,33        |
| 14.11            | Холл                      | 7,28        |
| 14.12            | Терраса (коэффициент 0,3) | 25,03       |
|                  |                           | 160,07      |
|                  |                           | 323,68      |


### УСЛОВНЫЕ ОБОЗНАЧЕНИЯ

-  - железобетонные конструкции  
 - стена из газобетонных блоков толщ. 200 мм  
 - перегородка из газобетонных блоков толщ. 100 мм  
 - маркировка помещений квартиры  
 - маркировка помещений общего пользования

Марка квартиры

Diagram illustrating the structure of a 5-digit apartment number (3342328565) and its components:

- 33**: Номер квартиры (Apartment number)
- 4232**: Жилая площадь квартиры (Residential area of the apartment)
- 8258**: Общая площадь квартиры без учета неотапливаемых помещений (Total area of the apartment excluding unheated areas)
- 8565**: Общая площадь квартиры с учетом понижающих коэффициентов (Total area of the apartment with discount coefficients)
- NT**: Код типа планировки (Layout type code)
- 4**: Количество жилых комнат в квартире (Number of living rooms in the apartment)

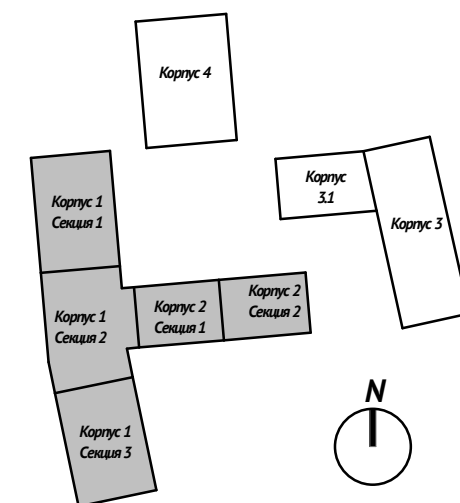


|              |           |      |        |       |       |                                                                                       |                   |      |        |
|--------------|-----------|------|--------|-------|-------|---------------------------------------------------------------------------------------|-------------------|------|--------|
|              |           |      |        |       |       | AA/БЗ-03-ДСЗ - АР1                                                                    |                   |      |        |
|              |           |      |        |       |       | "Жилой комплекс", расположенный по адресу: г. Москва, ЦАО, Садовническая ул., 8/76/71 |                   |      |        |
| Изм.         | Колуч.    | Лист | № док. | Подп. | Дата  | Часть 1. Архитектурные решения. Планы                                                 | Стадия            | Лист | Листов |
| Разработал   | Карасев   |      |        |       | 08.24 |                                                                                       | П                 | 9    |        |
| Разработал   | Заборова  |      |        |       | 08.24 |                                                                                       |                   |      |        |
| Проверил     | Добрякова |      |        |       | 08.24 |                                                                                       |                   |      |        |
| Норм. контр. | Добрякова |      |        |       | 08.24 | Корпус 1, 2. План 6 этажа. М1_200.                                                    | A R C H I T E C T |      |        |



|                                                                |              |
|----------------------------------------------------------------|--------------|
| Кровля тип КЗ (толщ. 350-550мм)                                |              |
| Гравий промытый                                                | -50 мм       |
| Дренажная мембрана ВИЛЛАДРЕЙН или аналог                       | -8 мм        |
| Геотекстиль ИКОПАЛ 300                                         |              |
| Гидроизоляция ИКОПАЛ Ультра В, 1 слой или аналог               | -5 мм        |
| Гидроизоляция ИКОПАЛ Ультра Н, 1 слой или аналог               | -5 мм        |
| Цементно-песчаная стяжка М150, армированная сеткой 4Вр1100х100 | -40 мм       |
| Уклонообразующий слой из керамзитобетона                       | -30...230 мм |
| Полиэтиленовая пленка 2 слоя                                   |              |
| Минераловатный утеплитель из каменного волокна 180 кг/м3       | -50 мм       |
| Минераловатный утеплитель из каменного волокна НГ 80-125 кг/м3 | -150 мм      |
| Пароизоляционная пленка                                        |              |
| Праймер СБС ИКОПАЛ                                             |              |
| Выравнивающая стяжка из цементно-песчаного раствора М150       | -12 мм       |
| Железобетонная плита перекрытия (см. КР)                       |              |


|                                                                 |                       |              |
|-----------------------------------------------------------------|-----------------------|--------------|
| Кровля тип К5 (с лотками):                                      | Гравий промытый       | -50 мм       |
| Дренажная мембрана                                              | ВИЛЛАДРЕЙН или аналог | -8 мм        |
| Геотекстиль ИКОПАЛ 300                                          |                       |              |
| Гидроизоляция ИКОПАЛ Ультра В 1 слой или аналог                 |                       | -5 мм        |
| Гидроизоляция ИКОПАЛ Ультра Н 1 слой или аналог                 |                       | -5 мм        |
| Цементно-песчаная стяжка М150, армированная сеткой 4Вр1 100х100 |                       | -40 мм       |
| Уклонообразующий слой из керамзитобетона                        |                       | -40...190 мм |
| Цементно-песчаная стяжка М150, армированная сеткой 4Вр1 100х100 |                       | -40 мм       |
| Полиэтиленовая пленка 2 слоя                                    |                       |              |
| Минераловатный утеплитель из каменного волокна 180 кг/м3        |                       | -50 мм       |
| Минераловатный утеплитель из каменного волокна НГ 80-125 кг/м3  |                       | -150 мм      |
| Пароизоляционная пленка                                         |                       |              |
| Праймер СБС ИКОПАЛ                                              |                       |              |
| Выравнивающая стяжка из цементно-песчаного раствора М150        |                       | -12 мм       |
| Железобетонная плита перекрытия (см. КР)                        |                       |              |

|                                                                  |              |
|------------------------------------------------------------------|--------------|
| Покрывные тип ПТ2 (толщ. 260...350мм – террасы корп.1 этаж 5)    |              |
| Бетонная тротуар. плита с засыпкой швов мелким гравием (фр. 5мм) | -50 мм       |
| Дренажная мембрана ВИЛЛАДРЕЙН или аналог                         | -8 мм        |
| Геотекстиль ИКОПАЛ 300                                           |              |
| Гидроизоляция ИКОПАЛ Ультра В, 1 слой или аналог                 | -5 мм        |
| Гидроизоляция ИКОПАЛ Ультра Н, 1 слой или аналог                 | -5 мм        |
| Цементно-песчаная стяжка М150, армированная сеткой 4Вр1 100х100  | -30...120 мм |
| Утеплитель ЭППС 35                                               | -150 мм      |
| Пароизоляционная пленка                                          |              |
| Праймер СБС ИКОПАЛ                                               |              |
| Выравнивающая стяжка из цементно-песчаного раствора М150         | -12 мм       |
| Железобетонная плита перекрытия (см. КР)                         |              |

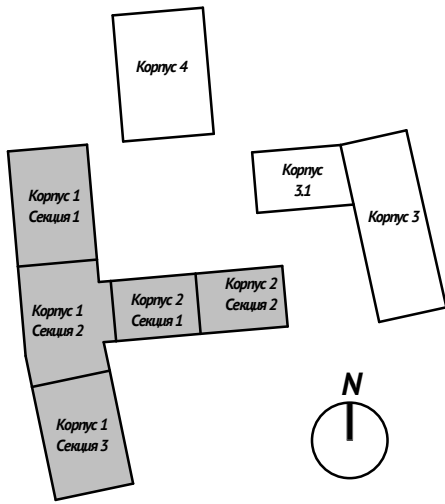

|              |           |      |       |       |       |                                                                                         |         |      |        |
|--------------|-----------|------|-------|-------|-------|-----------------------------------------------------------------------------------------|---------|------|--------|
|              |           |      |       |       |       | АА/БЗ-03-ДСЗ – АР1                                                                      |         |      |        |
|              |           |      |       |       |       | "Жилой комплекс", расположенный по адресу: г. Москва, ЦАО, Садовническая ул., вл. 76/71 |         |      |        |
| Изм.         | Колуч     | Лист | №вок. | Подп. | Дата  | Часть 1. Архитектурные решения. Планы                                                   | Стандия | Лист | Листов |
| Разработал   | Карасёв   |      |       |       | 08.24 |                                                                                         | П       | 10   |        |
| Разработал   | Задорина  |      |       |       | 08.24 |                                                                                         |         |      |        |
| Проверил     | Добрякова |      |       |       | 08.24 |                                                                                         |         |      |        |
| Норм. контр. | Добрякова |      |       |       | 08.24 | Корпуса 1, 2. План кровли. М 1_200.                                                     |         |      |        |
|              |           |      |       |       |       |    |         |      |        |



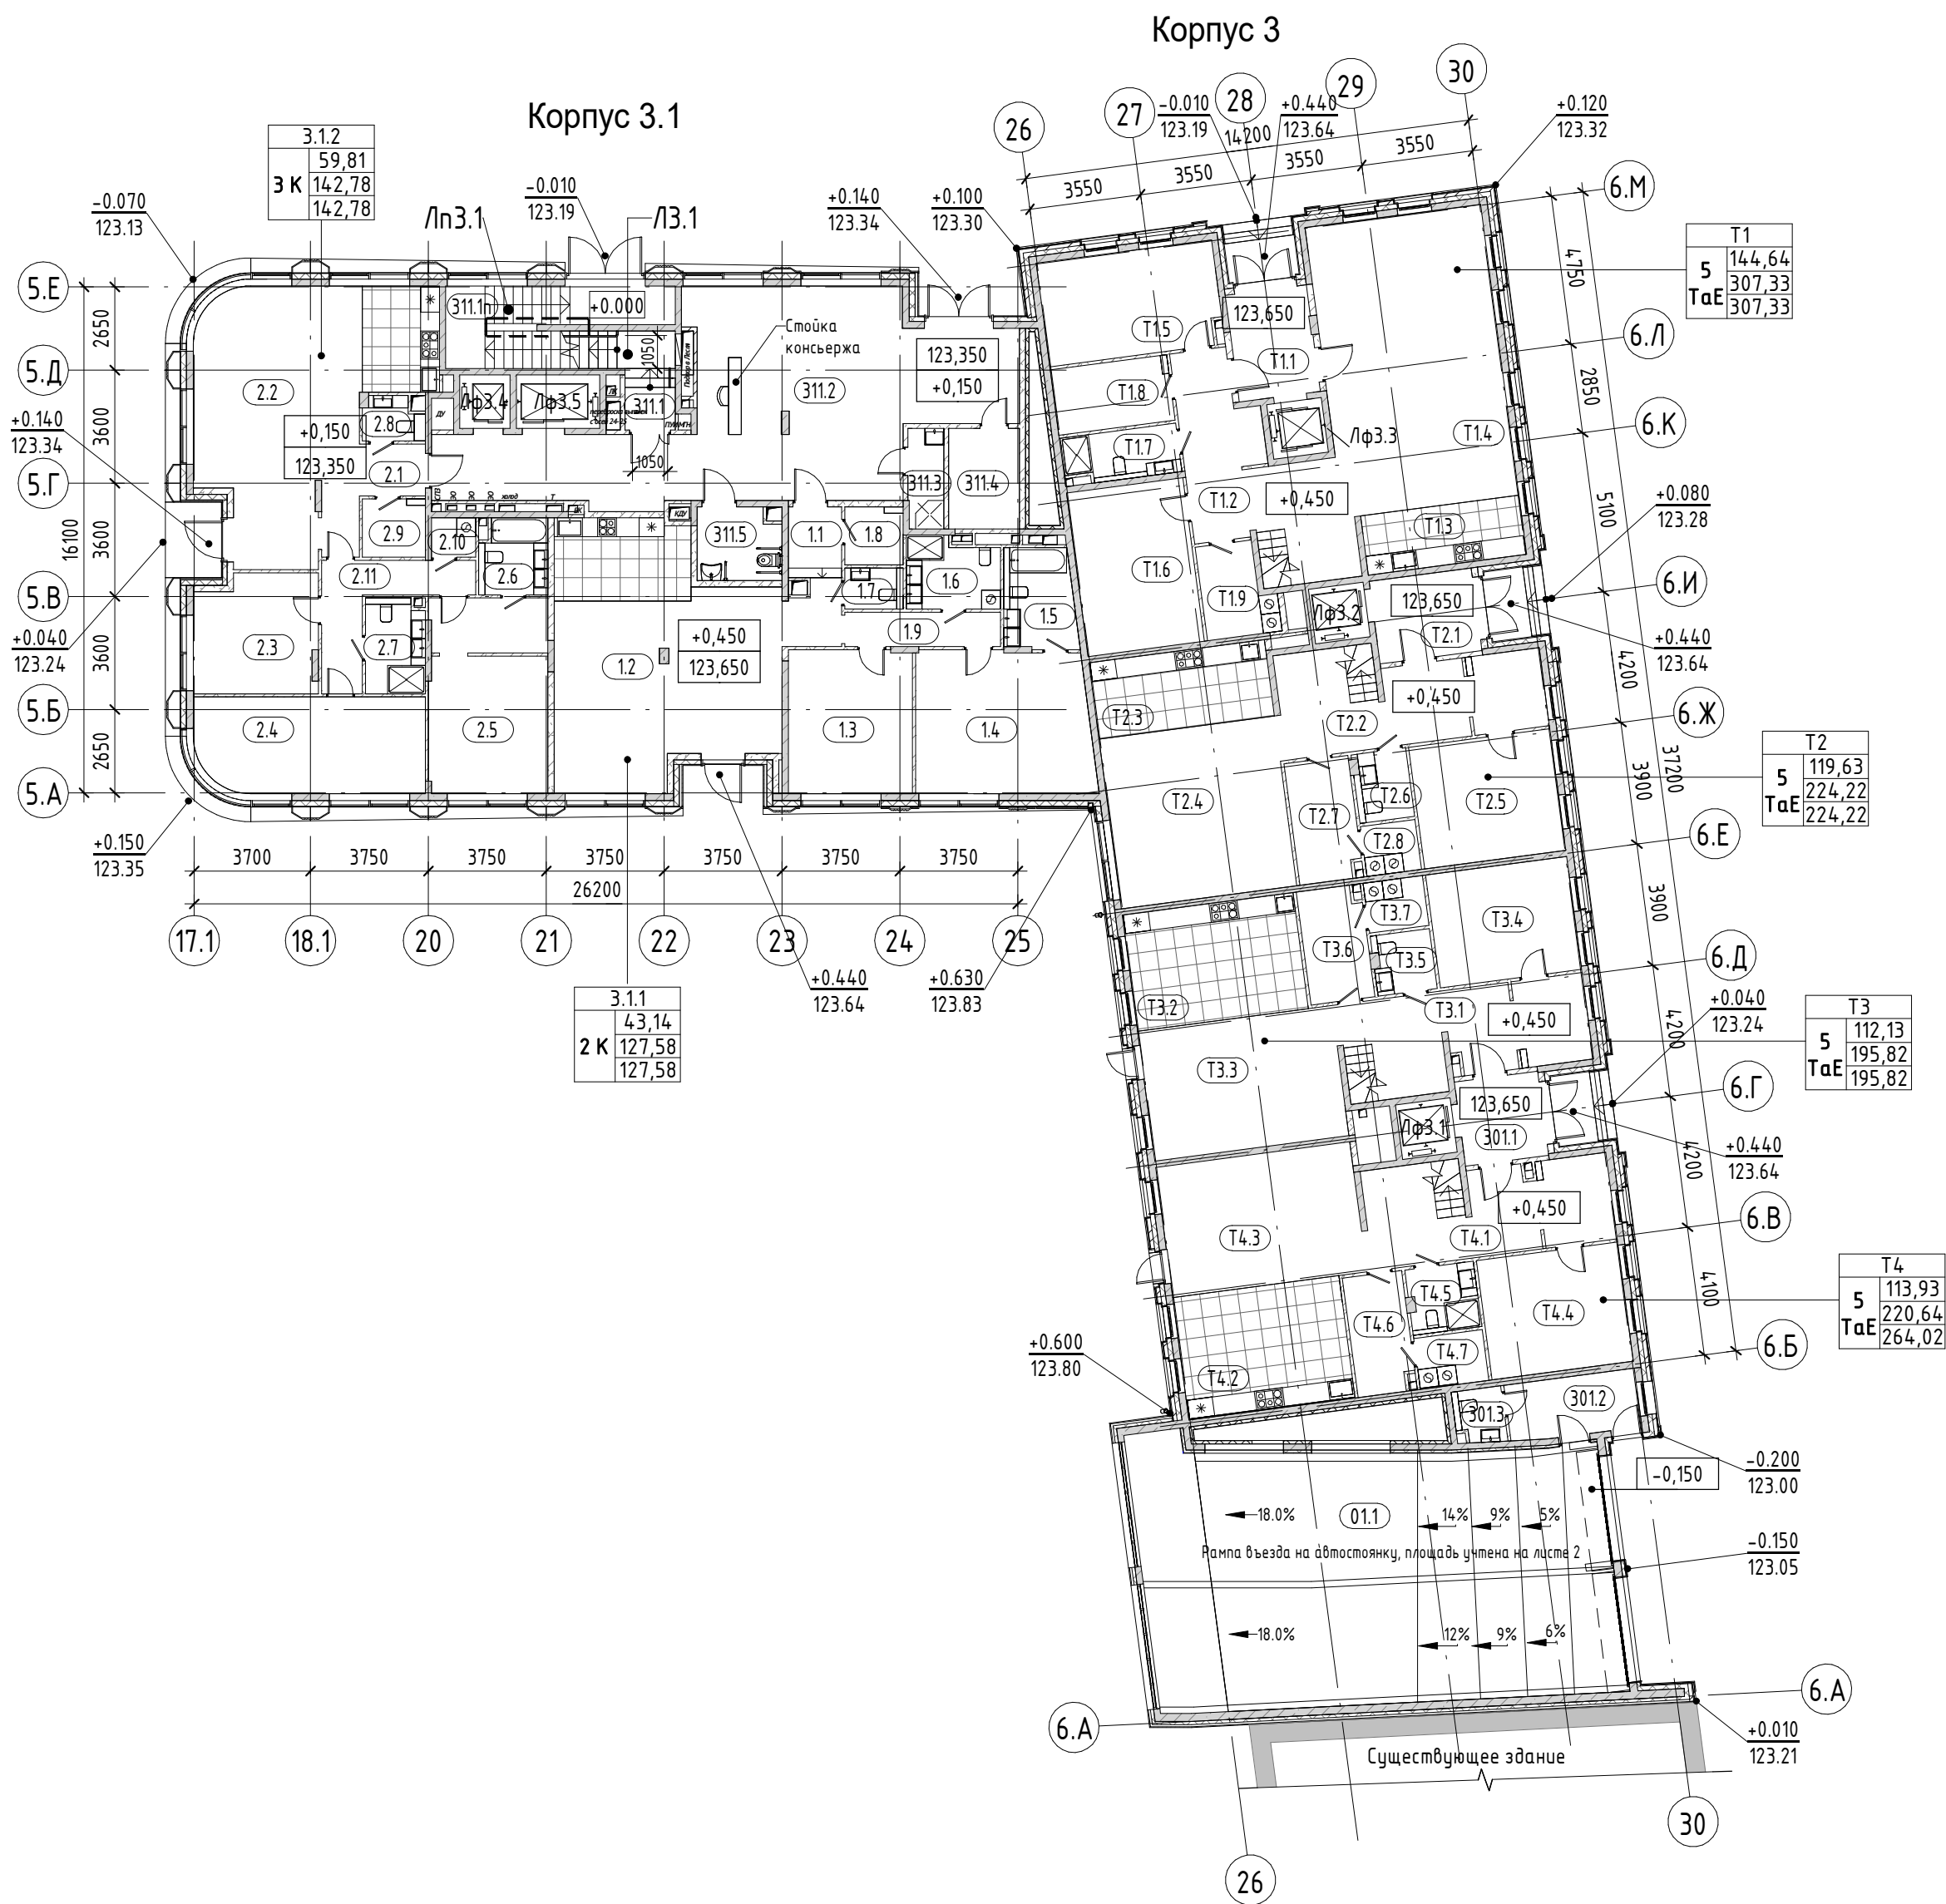

УСЛОВНЫЕ ОБОЗНАЧЕНИЯ

- железобетонные конструкции
- стена из газобетонных блоков толщ. 200 мм
- перегородка из газобетонных блоков толщ. 100 мм

- маркировка помещений квартиры
  - маркировка помещений общего пользования
- номер квартиры
- номер помещения
- номер корпуса
- этаж
- номер помещения

Марка квартиры:

- 33 - Номер квартиры
- 42.32 - Жилая площадь квартиры
- 82.58 - Общая площадь квартиры без учета неотапливаемых помещений
- 85.65 - Общая площадь квартиры с учетом понижающих коэффициентов
- Код типа планировки
- Количество жилых комнат в квартире

Экспликация помещений квартир 1 этажа (корпус 3)

| Номер помещения | Наименование       | Площадь, м2 |
|-----------------|--------------------|-------------|
| T1              |                    |             |
| T1.1            | Холл               | 8,86        |
| T1.2            | Холл               | 24,39       |
| T1.3            | Кухня-ниша         | 9,65        |
| T1.4            | Гостиная           | 52,53       |
| T1.5            | Гостевая комната   | 18,44       |
| T1.6            | Домашний кинотеатр | 19,58       |
| T1.7            | С/у                | 5,46        |
| T1.8            | Гардеробная        | 7,83        |
| T1.9            | Постирочная        | 6,12        |
|                 |                    | 152,86      |
| T2              |                    |             |
| T2.1            | Холл               | 8,67        |
| T2.2            | Холл               | 23,71       |
| T2.3            | Кухня-ниша         | 13,79       |
| T2.4            | Гостиная           | 30,68       |
| T2.5            | Гостевая комната   | 17,67       |
| T2.6            | С/у                | 3,75        |
| T2.7            | Гардеробная        | 7,78        |
| T2.8            | Постирочная        | 2,80        |
|                 |                    | 108,85      |
| T3              |                    |             |
| T3.1            | Холл               | 22,64       |
| T3.2            | Кухня-ниша         | 20,41       |
| T3.3            | Гостиная           | 26,01       |
| T3.4            | Гостевая комната   | 16,42       |
| T3.5            | С/у                | 3,56        |
| T3.6            | Гардеробная        | 7,22        |
| T3.7            | Постирочная        | 3,04        |
|                 |                    | 99,30       |
| T4              |                    |             |
| T4.1            | Холл               | 22,70       |
| T4.2            | Кухня-ниша         | 20,95       |
| T4.3            | Гостиная           | 26,01       |
| T4.4            | Гостевая комната   | 17,35       |
| T4.5            | С/у                | 4,52        |
| T4.6            | Гардеробная        | 7,06        |
| T4.7            | Постирочная        | 3,59        |
|                 |                    | 102,18      |
|                 |                    | 463,19      |

Экспликация МОП 1 этажа (корпус 3)

| Номер помещения | Наименование     | Площадь, м <sup>2</sup> |
|-----------------|------------------|-------------------------|
| 301.1           | Тамбур           | 7,21                    |
| 301.2           | Помещение охраны | 7,79                    |
| 301.3           | С/у              | 2,57                    |
|                 |                  | 17,57                   |

Экспликация помещений квартир 1 этажа (корпус 3.1)

| Номер помещения | Наименование          | Площадь, м2 |
|-----------------|-----------------------|-------------|
| 3.1.1           |                       |             |
| 1.1             | Холл                  | 7,42        |
| 1.2             | Кухня-столовая        | 52,24       |
| 1.3             | Спальня               | 18,02       |
| 1.4             | Спальня               | 25,12       |
| 1.5             | С/у                   | 7,13        |
| 1.6             | С/у                   | 6,39        |
| 1.7             | С/у                   | 2,40        |
| 1.8             | Гардеробная           | 3,42        |
| 1.9             | Холл                  | 5,44        |
|                 |                       | 127,58      |
| 3.1.2           |                       |             |
| 2.1             | Холл                  | 7,78        |
| 2.2             | Кухня-столовая        | 47,07       |
| 2.3             | Спальня               | 14,36       |
| 2.4             | Спальня               | 22,01       |
| 2.5             | Спальня с гардеробной | 23,44       |
| 2.6             | С/у                   | 5,07        |
| 2.7             | С/у                   | 5,62        |
| 2.8             | С/у                   | 2,49        |
| 2.9             | Гардеробная           | 3,70        |
| 2.10            | Постирочная           | 1,75        |
| 2.11            | Холл                  | 9,49        |
|                 |                       | 142,78      |
|                 |                       | 270,36      |

Экспликация МОП 1 этажа (корпус 3.1)

| Номер помещения | Наименование             | Площадь, м <sup>2</sup> | Категория пом. |
|-----------------|--------------------------|-------------------------|----------------|
| 311.1           | Лестничная клетка /ЛЗ.1  | 6,42                    |                |
| 311.1n          | Лестничная клетка /Лп3.1 | 15,18                   |                |
| 311.2           | Вестибюль                | 74,97                   |                |
| 311.3           | ПУИ                      | 3,64                    |                |
| 311.4           | Колясочная               | 7,20                    |                |
| 311.5           | Универсальный с/у        | 6,02                    |                |
|                 |                          | 113,43                  |                |

0.000=123,20

АА/БЗ-03-ДСЗ - АР1

"Жилой комплекс", расположенный по адресу: г. Москва, ЦАО, Садовническая ул., вл. 76/71

| Изм.         | Кол.уч.   | Лист | № док. | Подп. | Дата  | Часть 1. Архитектурные решения. Планы | Стадия | Лист | Листов |
|--------------|-----------|------|--------|-------|-------|---------------------------------------|--------|------|--------|
| Разработал   | Карасёв   |      |        |       | 08.24 |                                       | П      | 11   |        |
| Разработал   | Задорина  |      |        |       | 08.24 |                                       |        |      |        |
| Проверил     | Добрякова |      |        |       | 08.24 |                                       |        |      |        |
| Норм. контр. | Добрякова |      |        |       | 08.24 | Корпус 3, 3.1. План 1 этажа. М 1_200. |        |      |        |

ARTSL ARCHITECTS

Формат А2А





УСЛОВНЫЕ ОБОЗНАЧЕНИЯ

- железобетонные конструкции
- стена из газобетонных блоков толщ. 200 мм
- перегородка из газобетонных блоков толщ.100 мм
- 25.7

- маркировка помещений квартиры
- 101.5

- маркировка помещений общего пользования
- номер корпуса
- этаж
- номер помещения

Марка квартиры:

- 33

Номер квартиры
- 42.32

Жилая площадь квартиры
- 82.58

Общая площадь квартиры без учета неотапливаемых помещений
- 85.65

Общая площадь квартиры с учетом понижающих коэффициентов
- NT

Код типа планировки
- Количество жилых комнат в квартире

Экспликация помещений квартир 3 этажа  
(корпус 3.1)

| Номер помещения | Наименование              | Площадь, м2 |
|-----------------|---------------------------|-------------|
| 3.1.6           |                           |             |
| 6.1             | Холл                      | 5,93        |
| 6.2             | Кухня-столовая            | 60,44       |
| 6.3             | Спальня                   | 17,70       |
| 6.4             | Спальня с гардеробной     | 30,83       |
| 6.5             | Спальня                   | 14,74       |
| 6.6             | С/у                       | 6,82        |
| 6.7             | С/у                       | 3,69        |
| 6.8             | С/у                       | 4,93        |
| 6.9             | Гардеробная               | 5,16        |
| 6.10            | Холл                      | 6,70        |
| 6.11            | Терраса (коэффициент 0,3) | 31,22       |
|                 |                           | 188,16      |
| 3.1.7           |                           |             |
| 7.1             | Холл                      | 5,94        |
| 7.2             | Кухня-столовая            | 39,57       |
| 7.3             | Спальня                   | 15,63       |
| 7.4             | Спальня с гардеробной     | 31,97       |
| 7.5             | Спальня                   | 18,37       |
| 7.6             | Спальня                   | 16,98       |
| 7.7             | Спальня с гардеробной     | 33,57       |
| 7.8             | С/у                       | 2,86        |
| 7.9             | С/у                       | 5,90        |
| 7.10            | С/у                       | 8,50        |
| 7.11            | С/у                       | 6,77        |
| 7.12            | Гардеробная               | 2,50        |
| 7.13            | Постирочная               | 1,61        |
| 7.14            | Холл                      | 18,68       |
|                 |                           | 208,85      |
|                 |                           | 397,01      |

Экспликация помещений МОП 3 этажа  
(корпус 3.1)

| Номер помещения | Наименование           | Площадь, м² |
|-----------------|------------------------|-------------|
| 313.1           | Лестничная клетка ЛЗ.1 | 19,92       |
| 313.2           | Коридор                | 19,73       |
|                 |                        | 39,65       |

+0.000=123.200

АА/БЗ-03-ДСЗ – АР1

“Жилой комплекс”, расположенный по адресу: г. Москва, ЦАО, Садовническая ул., вл. 76/71

| Изм.         | Кол.уч.   | Лист  | №док. | Подп. | Дата | Часть 1. Архитектурные решения. Планы  | Стадия              | Лист | Листов |
|--------------|-----------|-------|-------|-------|------|----------------------------------------|---------------------|------|--------|
| Разработал   | Карасёв   | 08.24 |       |       |      |                                        | П                   | 13   |        |
| Разработал   | Задорина  | 08.24 |       |       |      | Корпуса 3, 3.1. План 3 этажа. М 1_200. | ARTSL<br>ARCHITECTS |      |        |
| Проверил     | Добрякова | 08.24 |       |       |      |                                        |                     |      |        |
| Норм. контр. | Добрякова | 08.24 |       |       |      |                                        |                     |      |        |

УСЛОВНЫЕ ОБОЗНАЧЕНИЯ

- железобетонные конструкции
- стена из газобетонных блоков толщ. 200 мм
- перегородка из газобетонных блоков толщ.100 мм

- 25.7

номер квартиры

101.5

номер помещения

номер этажа

номер помещения
- 101.5

маркировка помещений общего пользования

25.7

маркировка помещений квартиры

Марка квартиры:

- 33

42.32

82.58

85.65

•

—

—

—

—

—

Номер квартиры


Жилая площадь квартиры

Общая площадь квартиры без учета неотапливаемых помещений

Общая площадь квартиры с учетом понижающих коэффициентов

Код типа планировки

Количество жилых комнат в квартире

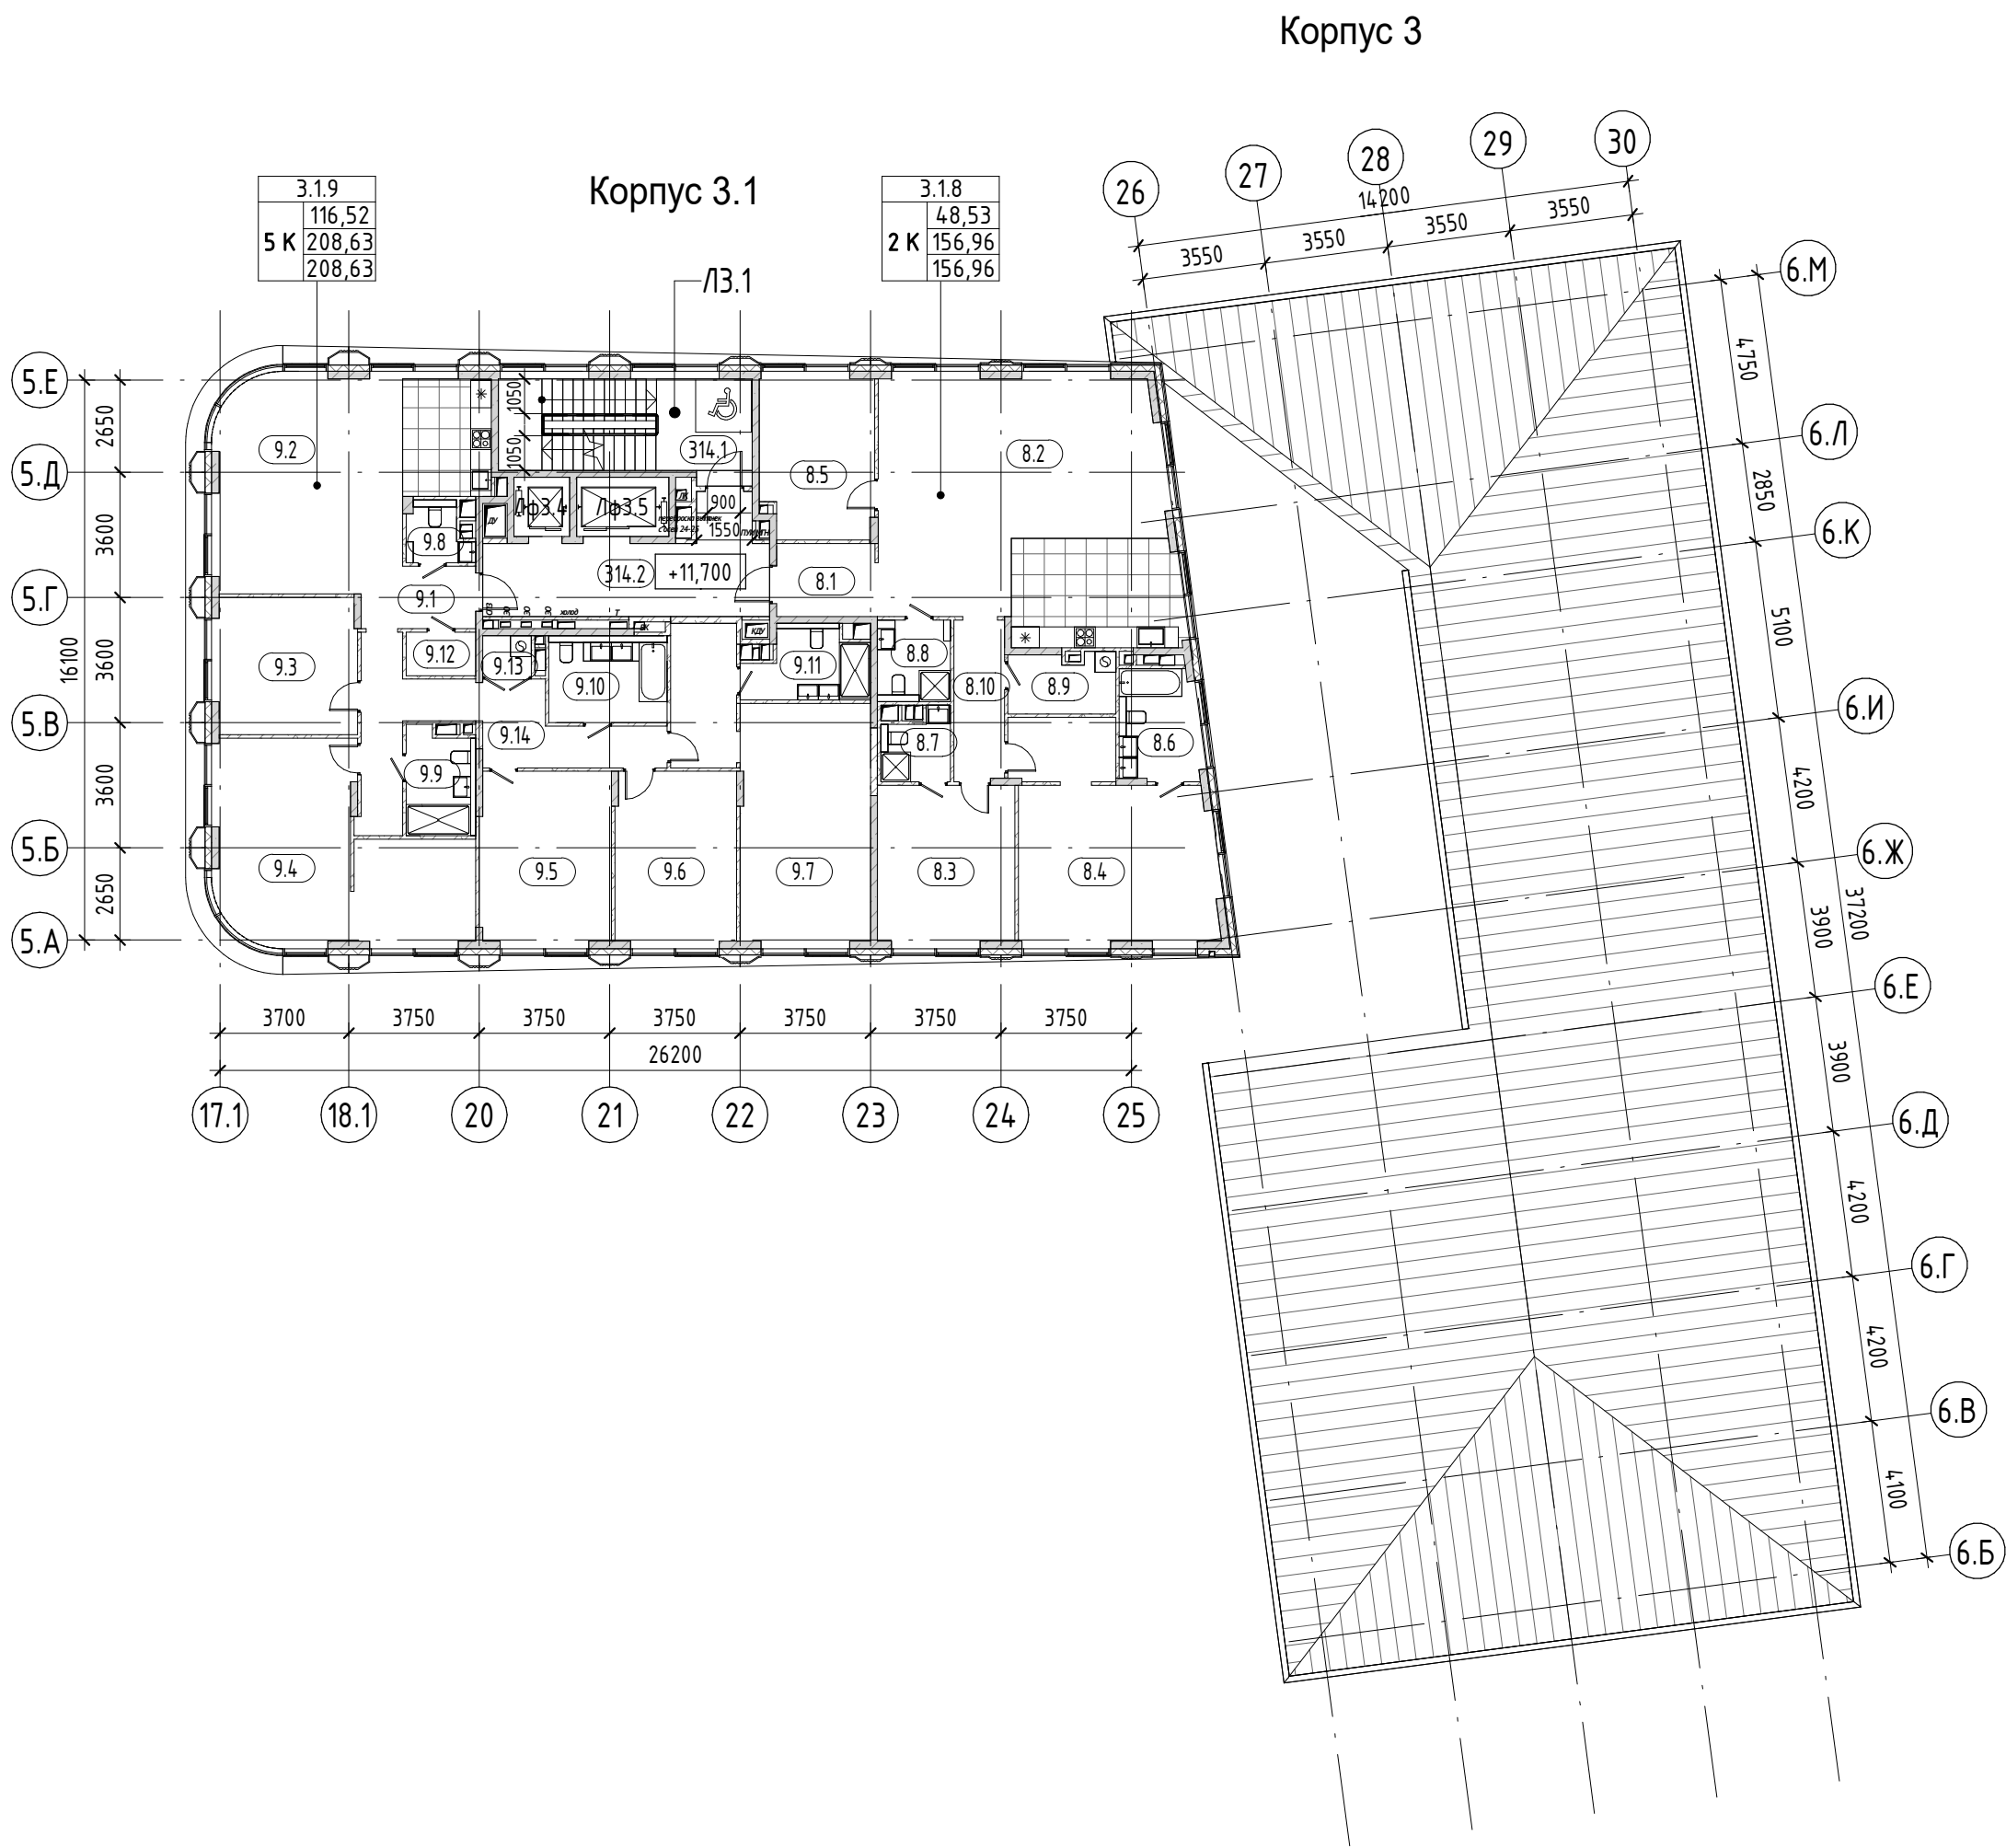


Экспликация помещений квартир 4 этажа  
(корпус 3.1)


| Номер помещения | Наименование          | Площадь, м2 |
|-----------------|-----------------------|-------------|
| 3.1.8           |                       |             |
| 8.1             | Холл                  | 5,93        |
| 8.2             | Кухня-столовая        | 60,44       |
| 8.3             | Спальня               | 17,70       |
| 8.4             | Спальня с гардеробной | 30,83       |
| 8.5             | Кабинет               | 14,74       |
| 8.6             | С/у                   | 6,82        |
| 8.7             | С/у                   | 3,69        |
| 8.8             | С/у                   | 4,94        |
| 8.9             | Гардеробная           | 5,17        |
| 8.10            | Холл                  | 6,70        |
|                 |                       | 156,96      |
| 3.1.9           |                       |             |
| 9.1             | Холл                  | 5,94        |
| 9.2             | Кухня-столовая        | 39,57       |
| 9.3             | Спальня               | 15,63       |
| 9.4             | Спальня с гардеробной | 31,97       |
| 9.5             | Спальня               | 18,37       |
| 9.6             | Спальня               | 16,98       |
| 9.7             | Спальня с гардеробной | 33,57       |
| 9.8             | С/у                   | 2,86        |
| 9.9             | С/у                   | 5,90        |
| 9.10            | С/у                   | 8,50        |
| 9.11            | С/у                   | 6,55        |
| 9.12            | Гардеробная           | 2,50        |
| 9.13            | Постирочная           | 1,61        |
| 9.14            | Холл                  | 18,68       |
|                 |                       | 208,63      |
|                 |                       | 365,59      |

Экспликация помещений МОП 4 этажа  
(корпус 3.1)

| Номер помещения | Наименование            | Площадь, м² |
|-----------------|-------------------------|-------------|
| 314.1           | Лестничная клетка /ЛЗ.1 | 19,92       |
| 314.2           | Коридор                 | 19,73       |
|                 |                         | 39,65       |

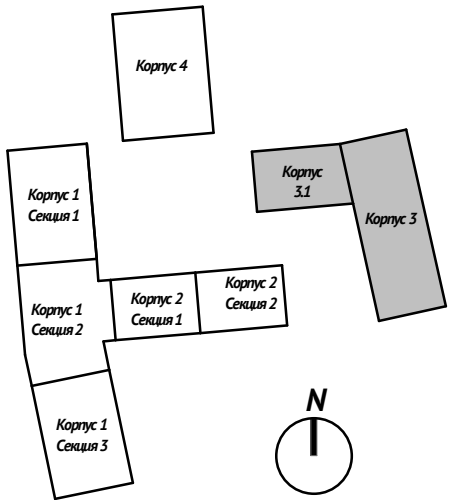

|              |           |       |        |       |       |                                                                                         |                                  |      |        |
|--------------|-----------|-------|--------|-------|-------|-----------------------------------------------------------------------------------------|----------------------------------|------|--------|
|              |           |       |        |       |       | +0.000=123.200                                                                          |                                  |      |        |
|              |           |       |        |       |       | АА/БЗ-03-ДСЗ - АР1                                                                      |                                  |      |        |
|              |           |       |        |       |       | "Жилой комплекс", расположенный по адресу: г. Москва, ЦАО, Садовническая ул., вл. 76/71 |                                  |      |        |
| Изм.         | Кол.уч.   | Лист  | № док. | Подп. | Дата  | Часть 1. Архитектурные решения. Планы                                                   | Стадия                           | Лист | Листов |
| Разработал   | Карасёв   | 08.24 |        |       | 08.24 |                                                                                         | П                                | 14   |        |
| Разработал   | Задорина  | 08.24 |        |       | 08.24 |                                                                                         |                                  |      |        |
| Проверил     | Добрякова |       |        |       |       | Корпуса 3, 3.1. План 4 этажа. М 1_200.                                                  | A R T E L<br>A R C H I T E C T S |      |        |
| Норм. контр. | Добрякова |       |        |       | 08.24 |                                                                                         | Формат А2А                       |      |        |

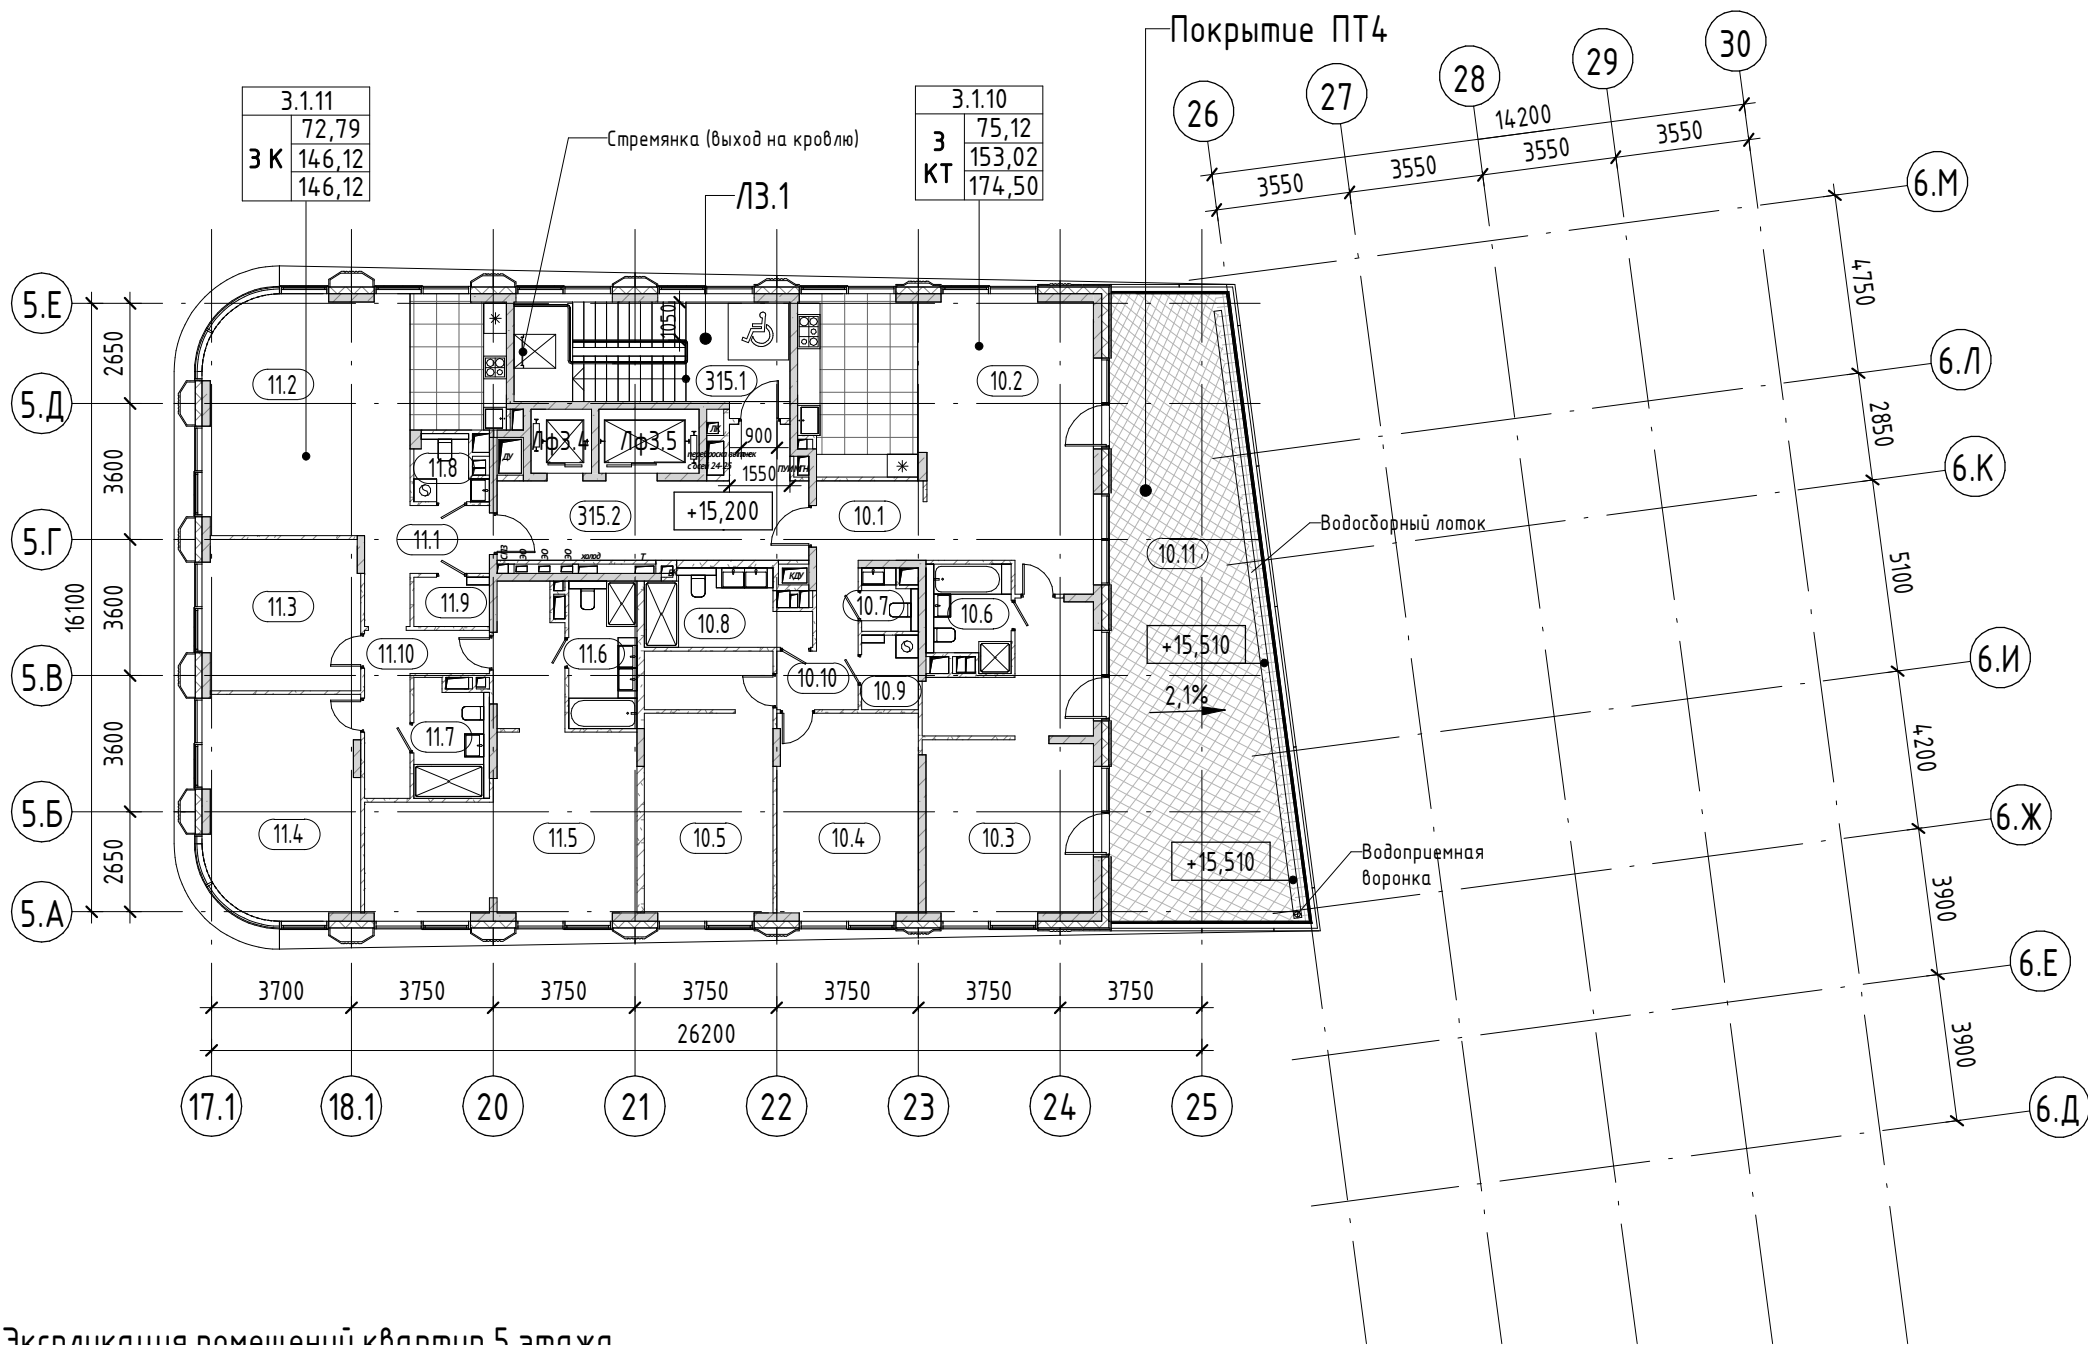

Экспликация помещений квартир 5 этажа  
(корпус 3.1)


| Номер помещения | Наименование              | Площадь, м2 |
|-----------------|---------------------------|-------------|
| 3.1.10          |                           |             |
| 10.1            | Холл                      | 8,57        |
| 10.2            | Кухня-столовая            | 47,26       |
| 10.3            | Спальня с гардеробной     | 31,86       |
| 10.4            | Спальня                   | 19,70       |
| 10.5            | Спальня с гардеробной     | 23,56       |
| 10.6            | С/у                       | 5,75        |
| 10.7            | С/у                       | 2,19        |
| 10.8            | С/у                       | 7,84        |
| 10.9            | Гардеробная               | 2,96        |
| 10.10           | Холл                      | 3,33        |
| 10.11           | Терраса (коэффициент 0,3) | 21,48       |
|                 |                           | 174,50      |
| 3.1.11          |                           |             |
| 11.1            | Холл                      | 7,62        |
| 11.2            | Кухня-столовая            | 39,57       |
| 11.3            | Спальня                   | 15,83       |
| 11.4            | Спальня с гардеробной     | 22,09       |
| 11.5            | Спальня с гардеробной     | 34,87       |
| 11.6            | С/у                       | 7,02        |
| 11.7            | С/у                       | 5,90        |
| 11.8            | С/у                       | 2,86        |
| 11.9            | Гардеробная               | 2,60        |
| 11.10           | Холл                      | 7,76        |
|                 |                           | 146,12      |
|                 |                           | 320,62      |

УСЛОВНЫЕ ОБОЗНАЧЕНИЯ

- железобетонные конструкции
- стена из газобетонных блоков толщ. 200 мм
- перегородка из газобетонных блоков толщ. 100 мм
- маркировка помещений квартиры
- маркировка помещений общего пользования
- номер квартиры
- номер помещения
- номер корпуса
- этаж
- номер помещения

Марка квартиры:

- Номер квартиры
- Жилая площадь квартиры
- Общая площадь квартиры без учета неотапливаемых помещений
- Общая площадь квартиры с учетом понижающих коэффициентов
- Код типа планировки
- Количество жилых комнат в квартире

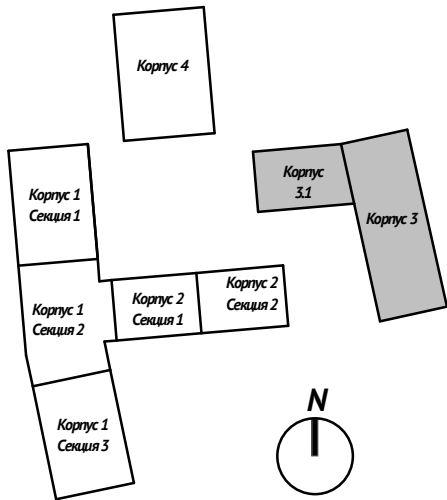


Экспликация помещений МОП 5 этажа  
(корпус 3.1)

| Номер помещения | Наименование           | Площадь, м² |
|-----------------|------------------------|-------------|
| 315.1           | Лестничная клетка ЛЗ.1 | 19,92       |
| 315.2           | Коридор                | 19,72       |
|                 |                        | 39,64       |

|              |           |      |        |                                                                                       |       |                                                                                         |                                                                                       |      |        |
|--------------|-----------|------|--------|---------------------------------------------------------------------------------------|-------|-----------------------------------------------------------------------------------------|---------------------------------------------------------------------------------------|------|--------|
|              |           |      |        |                                                                                       |       | АА/БЗ-03-ДСЗ - АР1                                                                      |                                                                                       |      |        |
|              |           |      |        |                                                                                       |       | "Жилой комплекс", расположенный по адресу: г. Москва, ЦАО, Садовническая ул., вл. 76/71 |                                                                                       |      |        |
| Изм.         | Кол.уч.   | Лист | № док. | Подп.                                                                                 | Дата  |                                                                                         |                                                                                       |      |        |
| Разработал   | Карасёв   |      |        |  | 08.24 | Часть 1. Архитектурные решения. Планы.                                                  | Стадия                                                                                | Лист | Листов |
| Разработал   | Задорина  |      |        |  | 08.24 |                                                                                         | П                                                                                     | 15   |        |
| Проверил     | Добрякова |      |        |  | 08.24 |                                                                                         |                                                                                       |      |        |
|              |           |      |        |                                                                                       |       | Корпуса 3, 3.1. План 5 этажа. М1_200.                                                   |  |      |        |
| Норм. контр. | Добрякова |      |        |  | 08.24 |                                                                                         |                                                                                       |      |        |



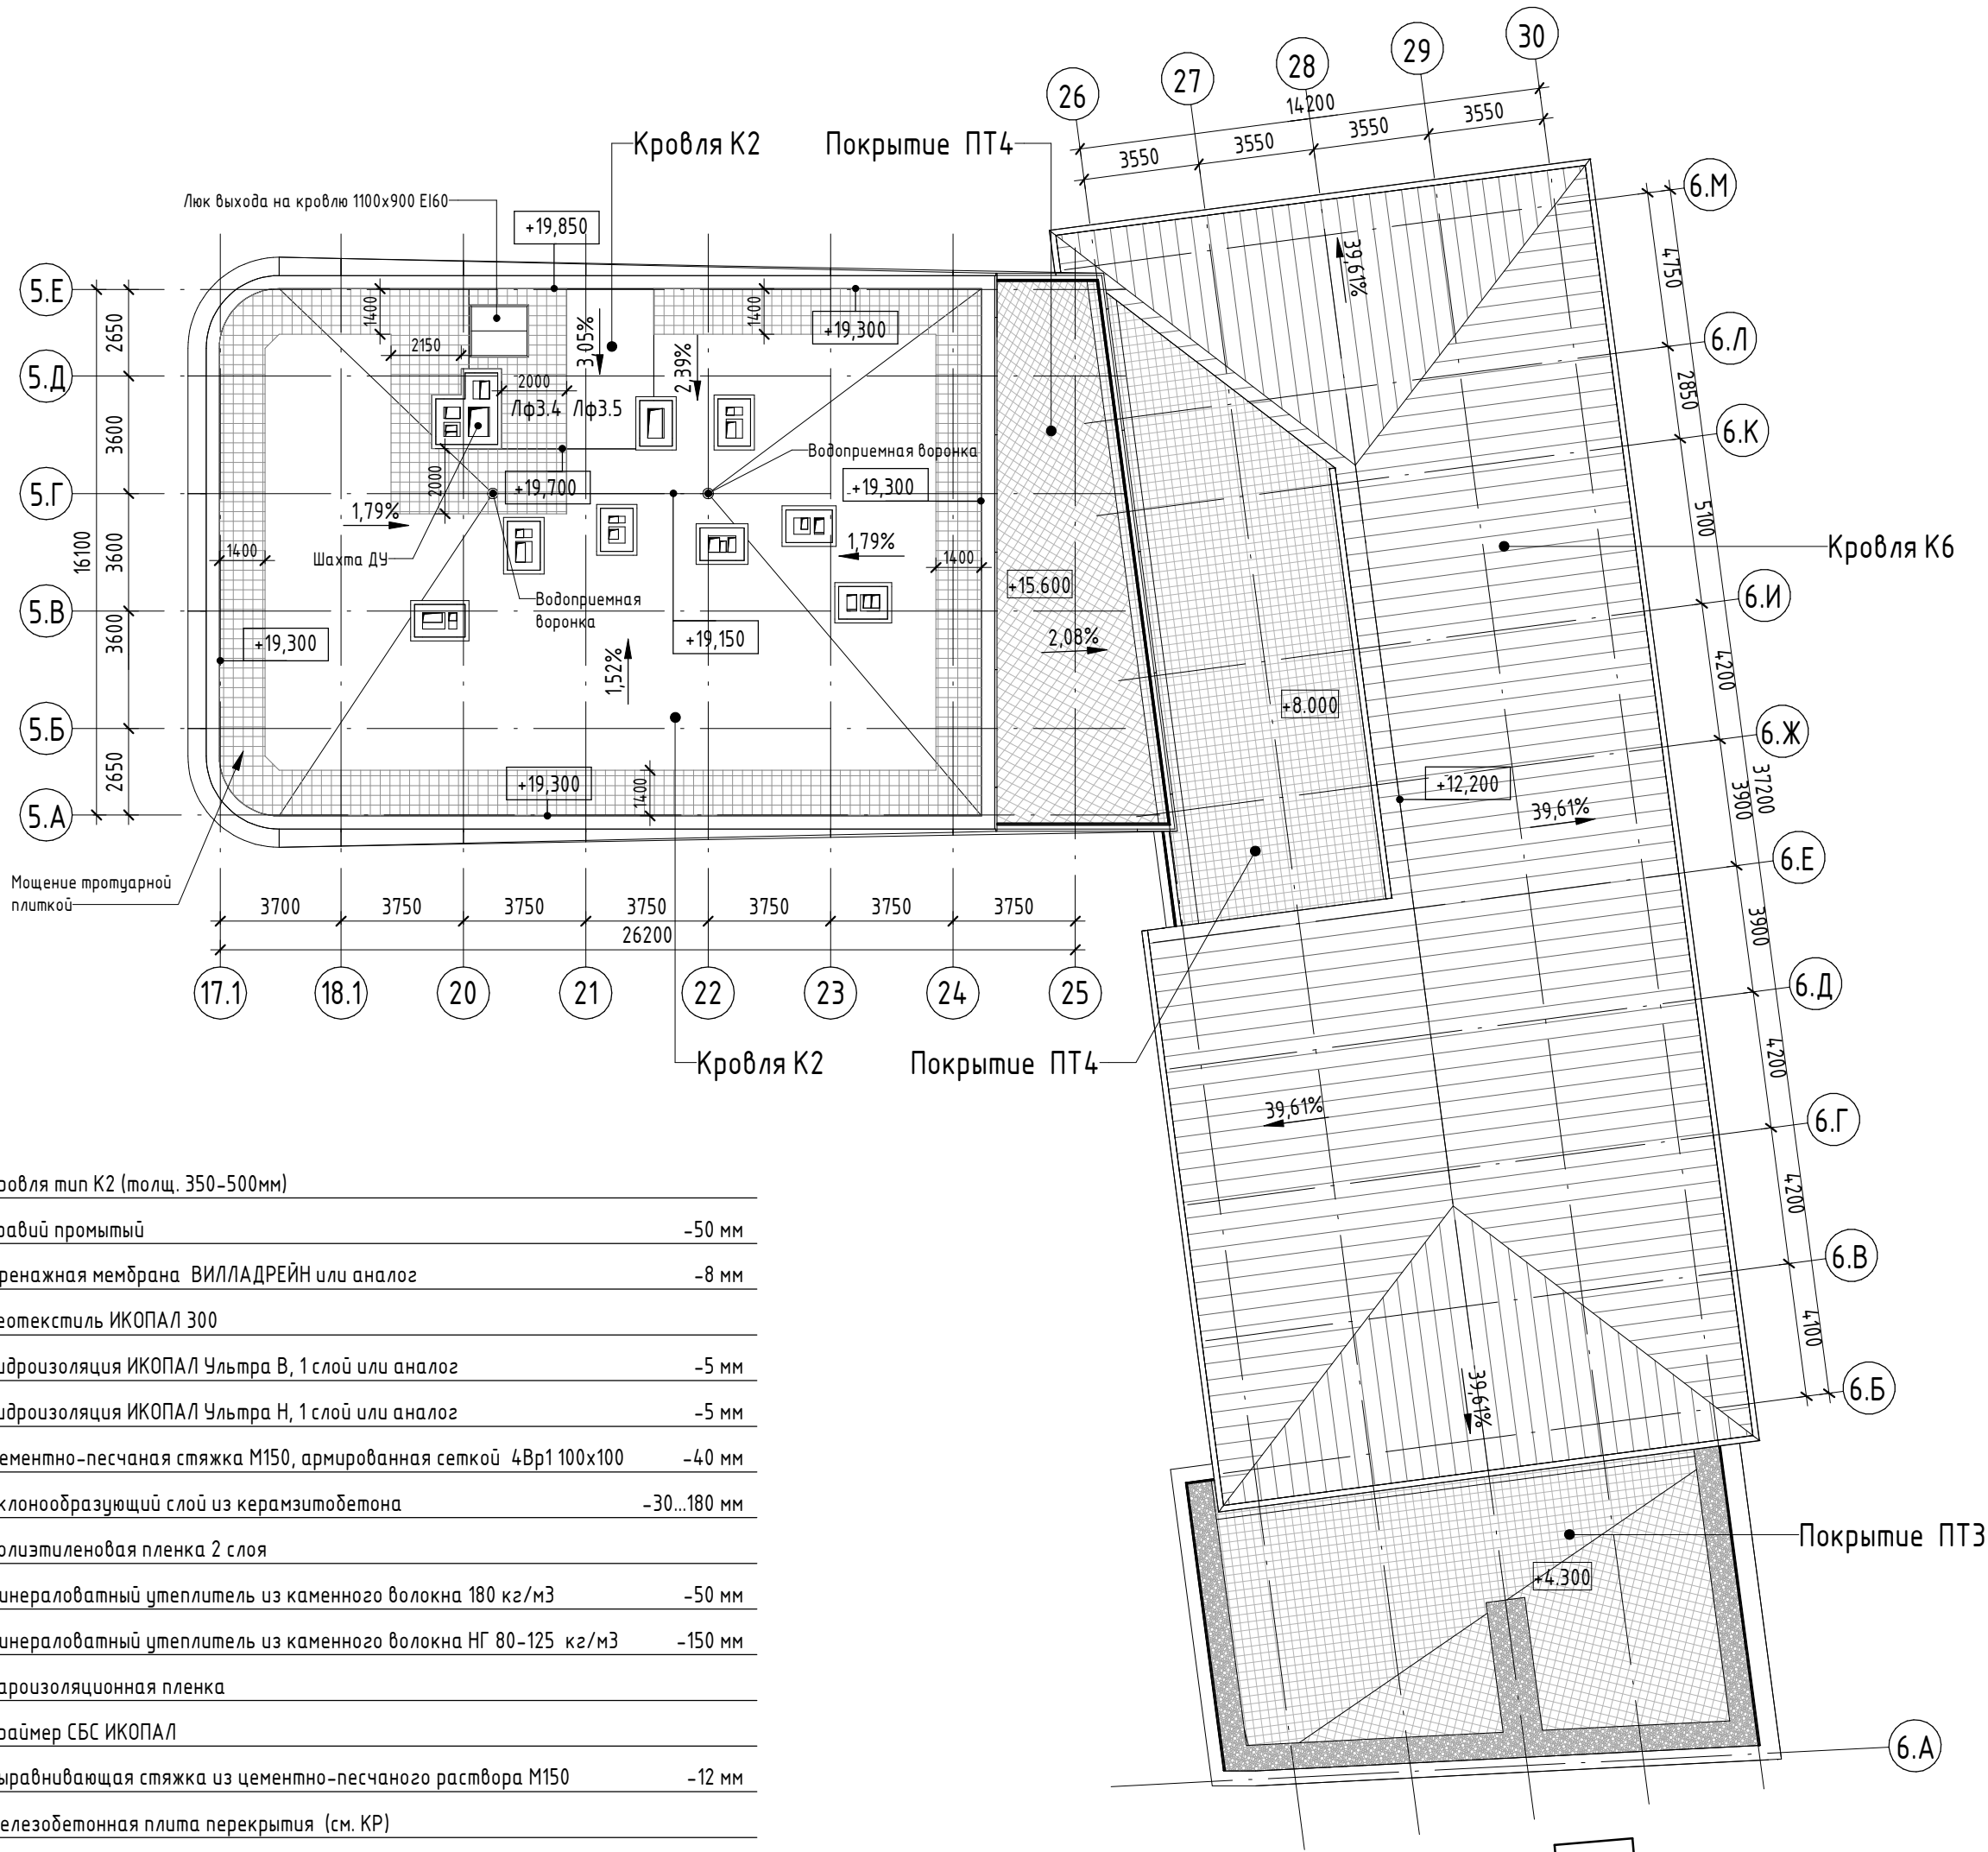


Кровля тип К2 (толщ. 350–500мм)

|                                                                 |              |
|-----------------------------------------------------------------|--------------|
| Гравий промытый                                                 | –50 мм       |
| Дренажная мембрана ВИЛЛАДРЕЙН или аналог                        | –8 мм        |
| Геотекстиль ИКОПАЛ 300                                          |              |
| Гидроизоляция ИКОПАЛ Ультра В, 1 слой или аналог                | –5 мм        |
| Гидроизоляция ИКОПАЛ Ультра Н, 1 слой или аналог                | –5 мм        |
| Цементно-песчаная стяжка М150, армированная сеткой 4Вр1 100х100 | –40 мм       |
| Уклонообразующий слой из керамзитобетона                        | –30...180 мм |
| Полиэтиленовая пленка 2 слоя                                    |              |
| Минераловатный утеплитель из каменного волокна 180 кг/м3        | –50 мм       |
| Минераловатный утеплитель из каменного волокна НГ 80–125 кг/м3  | –150 мм      |
| Пароизоляционная пленка                                         |              |
| Праймер СБС ИКОПАЛ                                              |              |
| Выравнивающая стяжка из цементно-песчаного раствора М150        | –12 мм       |
| Железобетонная плита перекрытия (см. КР)                        |              |

Кровля тип К6 (скатная)

|   |         |
|---|---------|
| Фальцевая медная кровля                                                                                 | –0.8 мм |
| Подстилающий слой (рубероид, изол ,гидроизол или аналог)                                                |         |
| Сплошной настил из досок хвойных пород                                                                  | –22 мм  |
| Контробрешетка (50х50) по брусу и воздушный зазор                                                       | –50 мм  |
| Гидроветрозащитная паропроницаемая мембрана                                                             |         |
| Минераловатный утеплитель из каменного волокна НГ 80–125 кг/м3                                          |         |
| между деревянными антипирированными брусками (50х150, шаг 600)                                          | –150 мм |
| Пароизоляционная пленка                                                                                 |         |
| Контрутепление между деревянными антипирированными брусками (50х50, шаг 600) –минераловатный утеплитель |         |
| из каменного волокна НГ 80–125 кг/м3                                                                    | –50 мм  |
| 2 слоя ГВЛВ по 12.5 мм                                                                                  | –25 мм  |

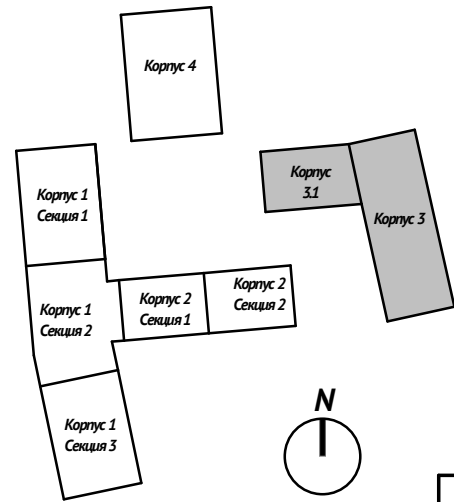

+0.000=123.200

|              |           |      |        |                                                                                       |       |                                                                                         |                     |      |        |
|--------------|-----------|------|--------|---------------------------------------------------------------------------------------|-------|-----------------------------------------------------------------------------------------|---------------------|------|--------|
|              |           |      |        |                                                                                       |       | АА/БЗ-03-ДСЗ - АР1                                                                      |                     |      |        |
|              |           |      |        |                                                                                       |       | "Жилой комплекс", расположенный по адресу: г. Москва, ЦАО, Садовническая ул., вл. 76/71 |                     |      |        |
| Изм.         | Кол.уч.   | Лист | № док. | Подп.                                                                                 | Дата  | Часть 1. Архитектурные решения. Планы                                                   | Стадия              | Лист | Листов |
| Разработал   | Карасёв   |      |        |  | 08.24 |                                                                                         | П                   | 16   |        |
| Разработал   | Задорина  |      |        |  | 08.24 |                                                                                         |                     |      |        |
| Проверил     | Добрякова |      |        |  | 08.24 |                                                                                         |                     |      |        |
|              |           |      |        |                                                                                       |       | Корпуса 3, 3.1. План кровли. М 1_200.                                                   | A R C H I T E C T S |      |        |
| Норм. контр. | Добрякова |      |        |  | 08.24 |                                                                                         |                     |      |        |

УСЛОВНЫЕ ОБОЗНАЧЕНИЯ

- железобетонные конструкции
- стена из газобетонных блоков толщ. 200 мм
- перегородка из газобетонных блоков толщ.100 мм

- 25.7

номер квартиры
- 1015

номер помещения
- номер корпуса
- этаж
- номер помещения

Марка квартиры:

- 1.11



Номер квартиры
- 22.22

Жилая площадь квартиры
- 33.33

Общая площадь квартиры без учета неотапливаемых помещений
- 44.44

Общая площадь квартиры с учетом понижающих коэффициентов
- 3 К

Код типа планировки
- Количество жилых комнат в квартире

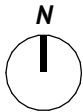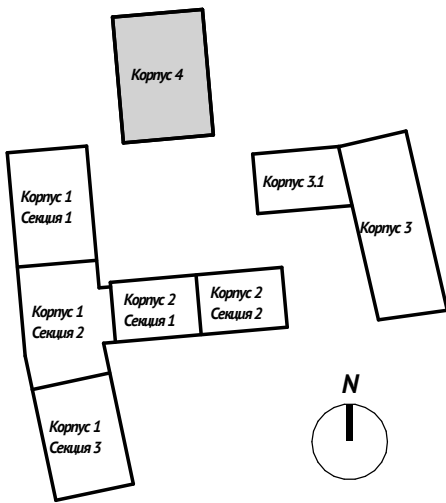

Экспликация помещений квартир 1 этажа

| Номер помещения | Наименование          | Площадь, м2 |
|-----------------|-----------------------|-------------|
| 4.1             |                       |             |
| 1.1             | Холл                  | 15,76       |
| 1.2             | Кухня-столовая        | 58,18       |
| 1.3             | Спальня с гардеробной | 24,31       |
| 1.4             | Спальня с гардеробной | 24,41       |
| 1.5             | Спальня с гардеробной | 20,80       |
| 1.6             | С/у                   | 4,08        |
| 1.7             | С/у                   | 5,98        |
| 1.8             | С/у                   | 4,39        |
| 1.9             | Гардеробная           | 5,46        |
|                 |                       | 163,37      |
| 4.2             |                       |             |
| 2.1             | Холл                  | 16,96       |
| 2.2             | Кухня-столовая        | 50,84       |
| 2.3             | Спальня               | 18,93       |
| 2.4             | Спальня с гардеробной | 22,16       |
| 2.5             | Спальня               | 14,97       |
| 2.6             | С/у                   | 3,28        |
| 2.7             | С/у                   | 5,01        |
| 2.8             | С/у                   | 7,03        |
| 2.9             | Гардеробная           | 3,94        |
|                 |                       | 143,12      |

Экспликация помещений квартир 1 этажа

| Номер помещения | Наименование          | Площадь, м2 |
|-----------------|-----------------------|-------------|
| 4.3             |                       |             |
| 3.1             | Холл                  | 17,94       |
| 3.2             | Кухня-столовая        | 31,39       |
| 3.3             | Спальня               | 15,28       |
| 3.4             | Спальня с гардеробной | 27,04       |
| 3.5             | С/у                   | 4,09        |
| 3.6             | С/у                   | 8,34        |
| 3.7             | Постирочная           | 2,55        |
| 3.8             | Холл                  | 3,84        |
|                 |                       | 110,47      |
| 4.4             |                       |             |
| 4.1             | Холл                  | 23,09       |
| 4.2             | Кухня-ниша            | 8,14        |
| 4.3             | Гостиная              | 31,71       |
| 4.4             | Спальня               | 12,80       |
| 4.5             | Спальня с гардеробной | 19,37       |
| 4.6             | С/у                   | 3,79        |
| 4.7             | С/у                   | 5,20        |
| 4.8             | Гардеробная           | 3,57        |
|                 |                       | 107,67      |
|                 |                       | 524,63      |

Экспликация МОП 1 этажа

| Номер помещения | Наименование          | Площадь, м² | Категория пом. |
|-----------------|-----------------------|-------------|----------------|
| 401.1           | Вестибюль             | 82,78       |                |
| 401.2           | Лестничная клетка Л4  | 19,45       |                |
| 401.3           | Универсальный санузел | 5,29        |                |
| 401.4           | ПУИ                   | 2,64        |                |
| 401.5           | Лестничная клетка Лп4 | 3,94        |                |
| 401.6           | Колясочная            | 6,98        |                |
|                 |                       | 121,08      |                |

0.000=123,20

|              |           |      |        |                                                                                       |       |                                                                                         |                                                                                       |      |        |
|--------------|-----------|------|--------|---------------------------------------------------------------------------------------|-------|-----------------------------------------------------------------------------------------|---------------------------------------------------------------------------------------|------|--------|
|              |           |      |        |                                                                                       |       | АА/БЗ-03-ДСЗ - АР1                                                                      |                                                                                       |      |        |
|              |           |      |        |                                                                                       |       | "Жилой комплекс", расположенный по адресу: г. Москва, ЦАО, Садовническая ул., вл. 76/71 |                                                                                       |      |        |
| Изм.         | Кол.уч.   | Лист | № док. | Подп.                                                                                 | Дата  | Часть 1. Архитектурные решения.<br>Планы.                                               | Стадия                                                                                | Лист | Листов |
| Разработал   | Карасёв   |      |        |  | 08.24 |                                                                                         | П                                                                                     | 17   |        |
| Разработал   | Задорина  |      |        |  | 08.24 |                                                                                         |                                                                                       |      |        |
| Проверил     | Добрякова |      |        |  | 08.24 |                                                                                         |                                                                                       |      |        |
|              |           |      |        |                                                                                       |       | Корпус 4. План 1 этажа. М 1_200.                                                        |  |      |        |
| Норм. контр. | Добрякова |      |        |  | 08.24 |                                                                                         |                                                                                       |      |        |

УСЛОВНЫЕ ОБОЗНАЧЕНИЯ

- железобетонные конструкции
- стена из газобетонных блоков толщ. 200 мм
- перегородка из газобетонных блоков толщ. 100 мм

- 25.7

номер квартиры
- 101.5

номер помещения
- номер корпуса
- этаж
- номер помещения
- 101.5

- маркировка помещений общего пользования

Марка квартиры:

- 1.11

Номер квартиры
- 22.22


Жилая площадь квартиры
- 33.33

Общая площадь квартиры без учета неотапливаемых помещений
- 44.44

Общая площадь квартиры с учетом понижающих коэффициентов
- 3 К

Код типа планировки
- 3 К

Количество жилых комнат в квартире

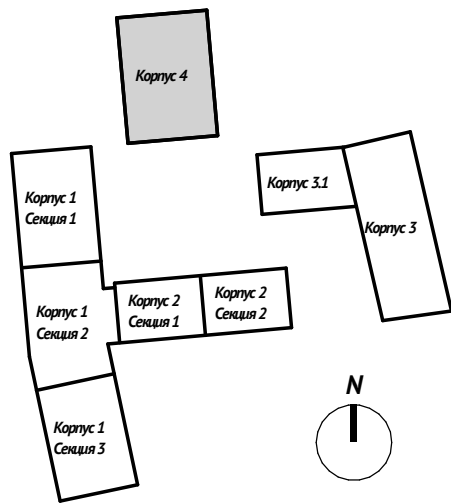

Экспликация помещений квартир 2 этажа

| Номер помещения | Наименование          | Площадь, м2 |
|-----------------|-----------------------|-------------|
| 4.5             |                       |             |
| 5.1             | Холл                  | 14,29       |
| 5.2             | Кухня-столовая        | 54,37       |
| 5.3             | Спальня с гардеробной | 23,26       |
| 5.4             | Спальня               | 12,47       |
| 5.5             | Спальня               | 17,34       |
| 5.6             | С/у                   | 6,01        |
| 5.7             | С/у                   | 2,55        |
| 5.8             | С/у                   | 3,97        |
| 5.9             | Гардеробная           | 3,46        |
| 5.10            | Холл                  | 2,68        |
|                 |                       | 140,40      |
| 4.6             |                       |             |
| 6.1             | Холл                  | 14,49       |
| 6.2             | Кухня-столовая        | 54,43       |
| 6.3             | Спальня с гардеробной | 22,16       |
| 6.4             | Спальня с гардеробной | 22,67       |
| 6.5             | Спальня               | 18,29       |
| 6.6             | Спальня               | 15,87       |
| 6.7             | С/у                   | 7,03        |
| 6.8             | С/у                   | 4,74        |
| 6.9             | С/у                   | 5,01        |
| 6.10            | Гардеробная           | 3,23        |
| 6.11            | Постирочная           | 1,53        |
|                 |                       | 169,45      |

Экспликация помещений квартир 2 этажа

| Номер помещения | Наименование          | Площадь, м2 |
|-----------------|-----------------------|-------------|
| 4.7             |                       |             |
| 7.1             | Холл                  | 13,56       |
| 7.2             | Кухня-столовая        | 54,42       |
| 7.3             | Спальня с гардеробной | 22,16       |
| 7.4             | Спальня с гардеробной | 22,80       |
| 7.5             | Спальня               | 19,01       |
| 7.6             | Спальня               | 16,48       |
| 7.7             | С/у                   | 7,03        |
| 7.8             | С/у                   | 5,15        |
| 7.9             | С/у                   | 5,01        |
| 7.10            | Гардеробная           | 3,23        |
| 7.11            | Постирочная           | 1,53        |
|                 |                       | 170,38      |
| 4.8             |                       |             |
| 8.1             | Холл                  | 15,53       |
| 8.2             | Кухня-ниша            | 10,53       |
| 8.3             | Гостиная              | 43,84       |
| 8.4             | Спальня с гардеробной | 23,26       |
| 8.5             | Спальня               | 12,47       |
| 8.6             | Спальня               | 17,34       |
| 8.7             | С/у                   | 6,01        |
| 8.8             | С/у                   | 2,55        |
| 8.9             | С/у                   | 3,97        |
| 8.10            | Гардеробная           | 3,46        |
| 8.11            | Холл                  | 2,68        |
|                 |                       | 141,64      |
|                 |                       | 621,87      |

Экспликация МОП 2 этажа

| Номер помещения | Наименование         | Площадь, м <sup>2</sup> |
|-----------------|----------------------|-------------------------|
| 402.1           | Лифтовый холл ПБЗ    | 13,14                   |
| 402.2           | Лестничная клетка Л4 | 17,40                   |
| 402.3           | Коридор              | 8,45                    |
| 402.4           | Коридор              | 8,45                    |
|                 |                      | 47,44                   |


0.000=123,20

|              |           |      |        |                                                                                       |       |                                                                                         |                                                                                       |      |        |
|--------------|-----------|------|--------|---------------------------------------------------------------------------------------|-------|-----------------------------------------------------------------------------------------|---------------------------------------------------------------------------------------|------|--------|
|              |           |      |        |                                                                                       |       | АА/БЗ-03-ДСЗ - АР1                                                                      |                                                                                       |      |        |
|              |           |      |        |                                                                                       |       | "Жилой комплекс", расположенный по адресу: г. Москва, ЦАО, Садовническая ул., вл. 76/71 |                                                                                       |      |        |
| Изм.         | Кол.уч.   | Лист | № док. | Подп.                                                                                 | Дата  | Часть 1. Архитектурные решения.<br>Планы.                                               | Стадия                                                                                | Лист | Листов |
| Разработал   | Карасёв   |      |        |  | 08.24 |                                                                                         | П                                                                                     | 18   |        |
| Разработал   | Задорина  |      |        |  | 08.24 |                                                                                         |                                                                                       |      |        |
| Проверил     | Добрякова |      |        |  | 08.24 |                                                                                         |                                                                                       |      |        |
|              |           |      |        |                                                                                       |       | Корпус 4. План 2 этажа. М 1_200.                                                        |  |      |        |
| Норм. контр. | Добрякова |      |        |  | 08.24 |                                                                                         |                                                                                       |      |        |

Формат А2А



| Инв. № подл. | Подп. и дата | Взам. инв. № |
|--------------|--------------|--------------|
|              |              |              |

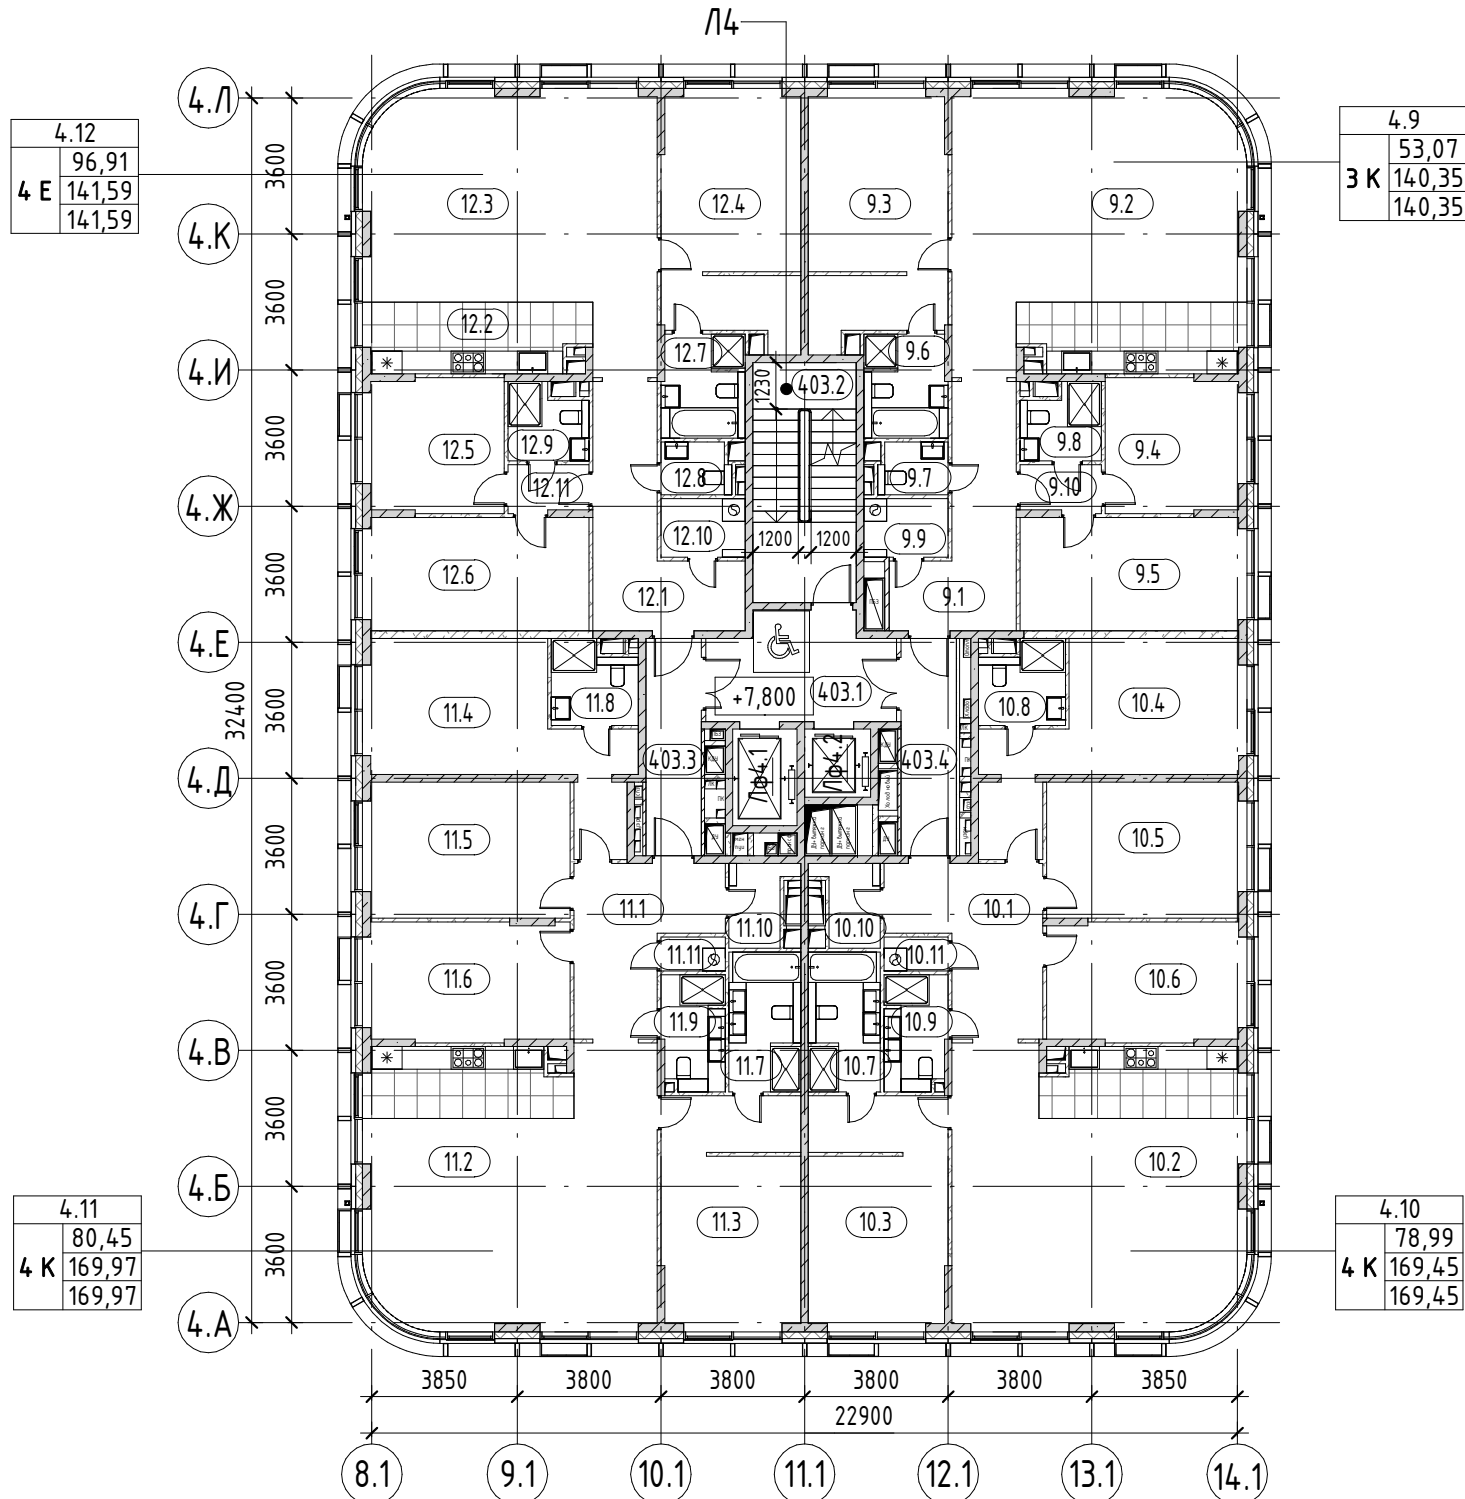

## УСЛОВНЫЕ ОБОЗНАЧЕНИЯ

-  - железобетонные конструкции
-  - стена из газобетонных блоков толщ. 200 мм
-  - перегородка из газобетонных блоков толщ. 100 мм


- маркировка помещений квартиры  
 номер квартиры  
 номер помещения

1015 - маркировка помещений общего пользования

номер корпуса —  
этаж —  
номер помещения —

Марка квартиры:

|    |       |                                                           |
|----|-------|-----------------------------------------------------------|
| ЭК | 1.11  | Номер квартиры                                            |
|    | 22.22 | Жилая площадь квартиры                                    |
|    | 33.33 | Общая площадь квартиры без учета неоплачиваемых помещений |
|    | 44.44 | Общая площадь квартиры с учетом понижающих коэффициентов  |
|    |       | Код типа планировки                                       |
|    |       | Количество жилых комнат в квартире                        |

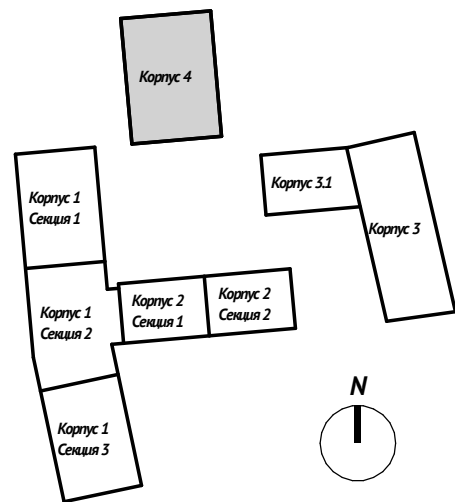

### Экспликация помещений квартир типового этажа (3-15)

| Номер помещения | Наименование          | Площадь, м2 |
|-----------------|-----------------------|-------------|
| 4.9             |                       |             |
| 9.1             | Холл                  | 14,29       |
| 9.2             | Кухня-столовая        | 54,37       |
| 9.3             | Спальня с гардеробной | 23,26       |
| 9.4             | Спальня               | 12,47       |
| 9.5             | Спальня               | 17,34       |
| 9.6             | С/у                   | 6,01        |
| 9.7             | С/у                   | 2,50        |
| 9.8             | С/у                   | 3,97        |
| 9.9             | Гардеробная           | 3,46        |
| 9.10            | Холл                  | 2,68        |
|                 |                       | 140,35      |
| 4.10            |                       |             |
| 10.1            | Холл                  | 14,49       |
| 10.2            | Кухня-столовая        | 54,43       |
| 10.3            | Спальня с гардеробной | 22,16       |
| 10.4            | Спальня с гардеробной | 22,67       |
| 10.5            | Спальня               | 18,29       |
| 10.6            | Спальня               | 15,87       |
| 10.7            | С/у                   | 7,03        |
| 10.8            | С/у                   | 4,74        |
| 10.9            | С/у                   | 5,01        |
| 10.10           | Гардеробная           | 3,23        |
| 10.11           | Постирочная           | 1,53        |
|                 |                       | 169,45      |

### Экспликация помещений квартир типового этажа (3-15)

| Номер помещения | Наименование          | Площадь, м2 |
|-----------------|-----------------------|-------------|
| 4.11            |                       |             |
| 11.1            | Холл                  | 13,56       |
| 11.2            | Кухня-столовая        | 54,42       |
| 11.3            | Спальня с гардеробной | 22,16       |
| 11.4            | Спальня с гардеробной | 22,80       |
| 11.5            | Спальня               | 19,01       |
| 11.6            | Спальня               | 16,48       |
| 11.7            | С/у                   | 7,03        |
| 11.8            | С/у                   | 4,74        |
| 11.9            | С/у                   | 5,01        |
| 11.10           | Гардеробная           | 3,23        |
| 11.11           | Постирочная           | 1,53        |
|                 |                       | 169,97      |
| 4.12            |                       |             |
| 12.1            | Холл                  | 15,53       |
| 12.2            | Кухня-ниша            | 10,53       |
| 12.3            | Гостиная              | 43,84       |
| 12.4            | Спальня с гардеробной | 23,26       |
| 12.5            | Спальня               | 12,47       |
| 12.6            | Спальня               | 17,34       |
| 12.7            | С/у                   | 6,01        |
| 12.8            | С/у                   | 2,50        |
| 12.9            | С/у                   | 3,97        |
| 12.10           | Гардеробная           | 3,46        |
| 12.11           | Холл                  | 2,68        |
|                 |                       | 141,59      |
|                 |                       | 621,36      |

### Экспликация МОП типового этажа (3-15)

| Номер помещения | Наименование         | Площадь, м <sup>2</sup> |
|-----------------|----------------------|-------------------------|
| 403.1           | Лифтовый холл ПБЗ    | 13,14                   |
| 403.2           | Лестничная клетка Л4 | 17,40                   |
| 403.3           | Коридор              | 8,45                    |
| 403.4           | Коридор              | 8,45                    |
|                 |                      | 47,44                   |


ПРИМЕЧАНИЕ:

1. Типовой этаж представлен планом 3 этажа.

|              |           |      |        |                                                                                       |       |                                                                                         |                                                                                       |      |        |
|--------------|-----------|------|--------|---------------------------------------------------------------------------------------|-------|-----------------------------------------------------------------------------------------|---------------------------------------------------------------------------------------|------|--------|
|              |           |      |        |                                                                                       |       | АА/БЗ-03-ДСЗ - АР1                                                                      |                                                                                       |      |        |
|              |           |      |        |                                                                                       |       | "Жилой комплекс", расположенный по адресу: г. Москва, ЦАО, Садовническая ул., вл. 76/71 |                                                                                       |      |        |
| Изм.         | Кол.уч.   | Лист | № док. | Подп.                                                                                 | Дата  | Часть 1. Архитектурные решения.<br>Планы.                                               | Стадия                                                                                | Лист | Листов |
| Разработал   | Карасёв   |      |        |  | 08.24 |                                                                                         | П                                                                                     | 19   |        |
| Разработал   | Задорина  |      |        |  | 08.24 |                                                                                         |                                                                                       |      |        |
| Проверил     | Добрякова |      |        |  | 08.24 |                                                                                         |                                                                                       |      |        |
|              |           |      |        |                                                                                       |       | Корпус 4. План 3-15 этажей. М 1_200.                                                    |  |      |        |
| Норм. контр. | Добрякова |      |        |  | 08.24 |                                                                                         |                                                                                       |      |        |

Формат A2A

|                                                                   |              |  |
|-------------------------------------------------------------------|--------------|--|
| Покрытие тип ПТ5 (террасы корп. 4)                                |              |  |
| Бетонная тротуар. плитка с засыпкой швов мелким грабием (фр. 5мм) | -50 мм       |  |
| Дренажная мембрана ВИЛЛАДРЕЙН или аналог                          | -8 мм        |  |
| Геотекстиль ИКОПАЛ 300                                            |              |  |
| Гидроизоляция ИКОПАЛ Ультра В, 1 слой или аналог                  | -5 мм        |  |
| Гидроизоляция ИКОПАЛ Ультра Н, 1 слой или аналог                  | -5 мм        |  |
| Цементно-песчаная стяжка М150, армированная сеткой 4Вр1 100х100   | -40 мм       |  |
| Уклонообразующий слой из керамзитобетона                          | -30...130 мм |  |
| Утеплитель ЭППС 35                                                | -150 мм      |  |
| Пароизоляционная пленка                                           |              |  |
| Праймер СБС ИКОПАЛ                                                |              |  |
| Выравнивающая стяжка из цементно-песчаного раствора М150          | -12 мм       |  |
| Железобетонная плита перекрытия (см. КР)                          |              |  |

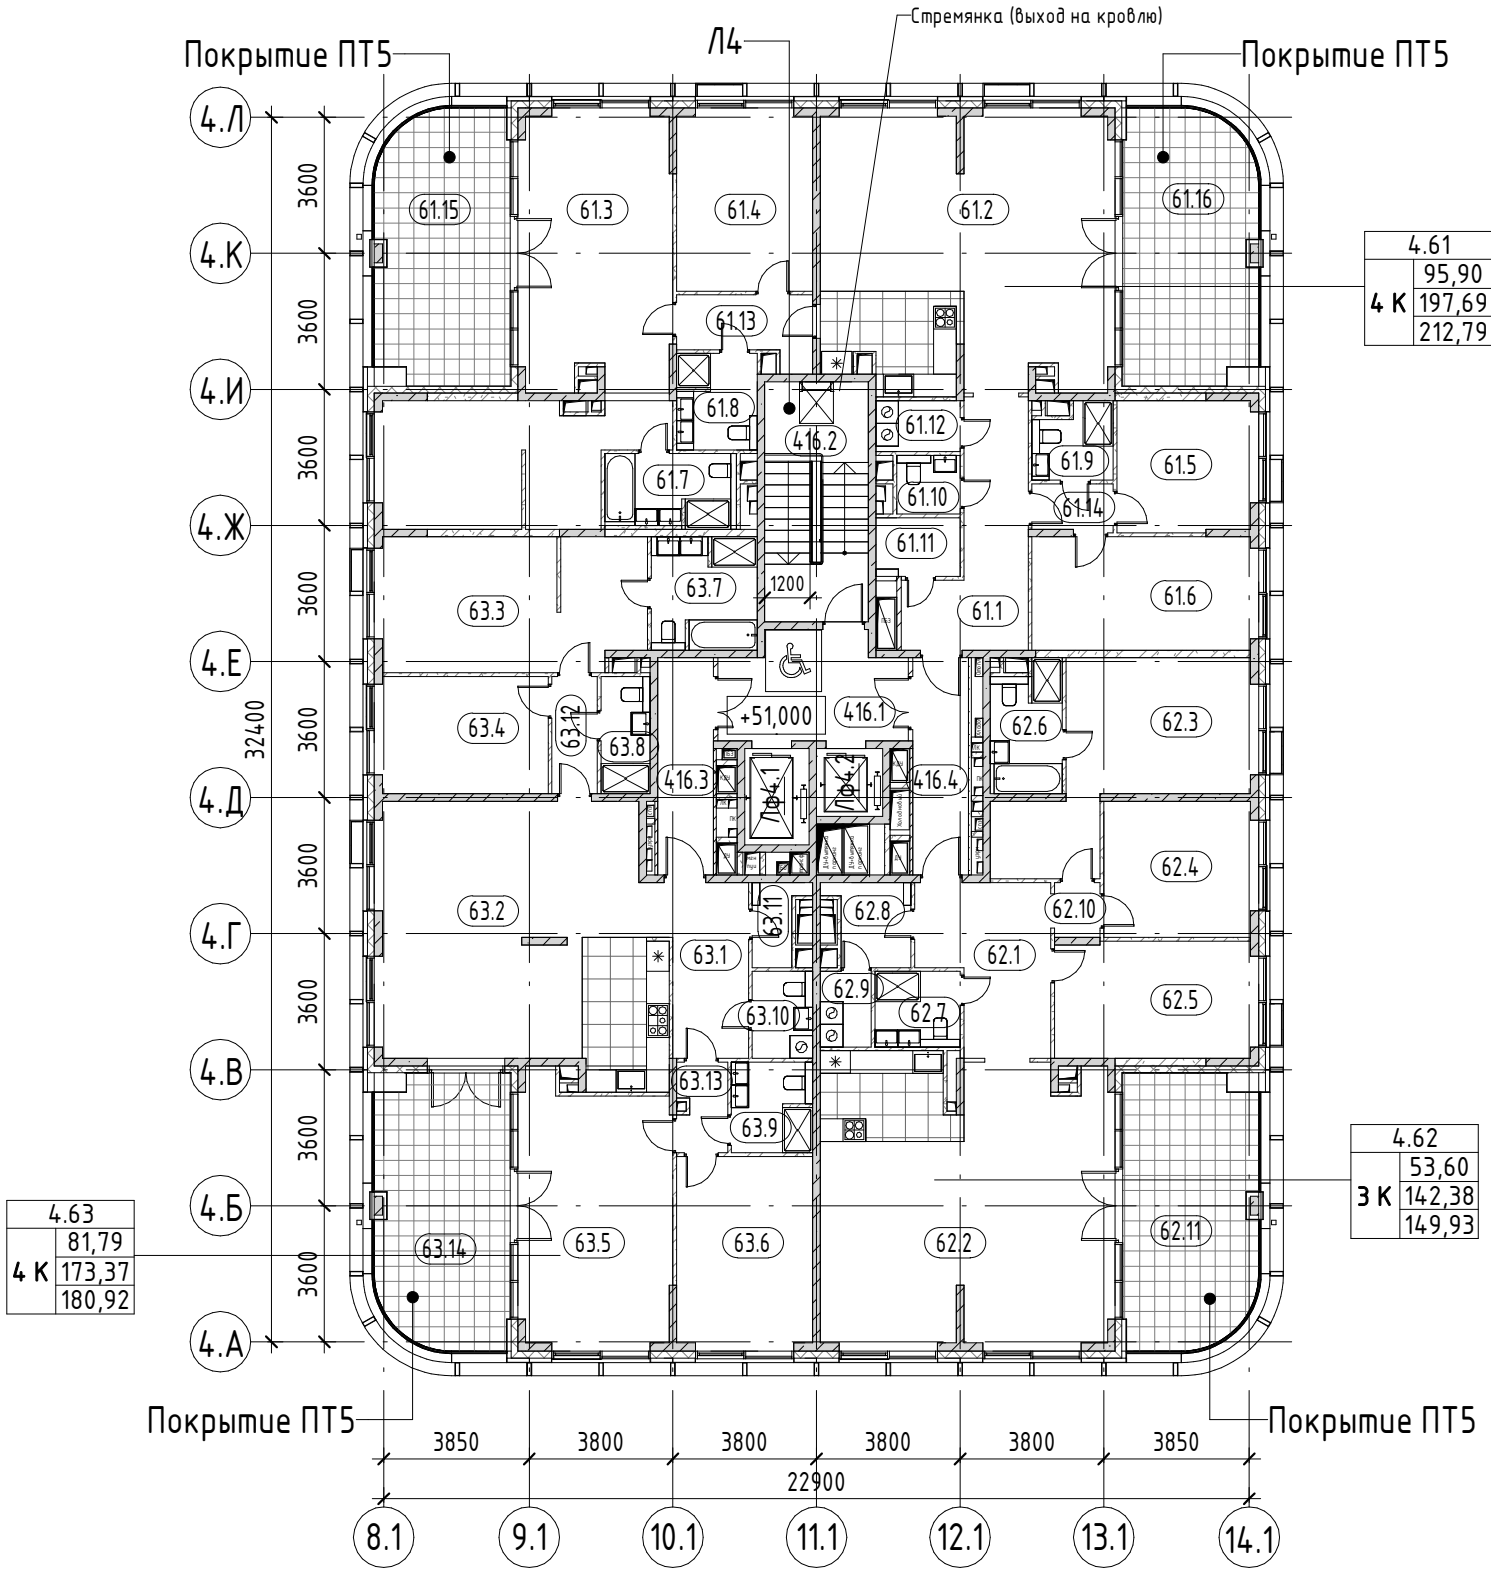

Экспликация помещений квартир 16 этажа

| Номер помещения | Наименование              | Площадь, м2 |
|-----------------|---------------------------|-------------|
| 4.61            |                           |             |
| 61.1            | Холл                      | 14,46       |
| 61.2            | Кухня-столовая            | 53,62       |
| 61.3            | Спальня с гардеробной     | 49,65       |
| 61.4            | Спальня                   | 16,67       |
| 61.5            | Спальня                   | 12,24       |
| 61.6            | Спальня                   | 17,34       |
| 61.7            | С/у                       | 6,76        |
| 61.8            | С/у                       | 5,43        |
| 61.9            | С/у                       | 3,97        |
| 61.10           | С/у                       | 2,60        |
| 61.11           | Гардеробная               | 3,46        |
| 61.12           | Постирочная               | 3,01        |
| 61.13           | Холл                      | 5,79        |
| 61.14           | Холл                      | 2,69        |
| 61.15           | Терраса (коэффициент 0,3) | 7,55        |
| 61.16           | Терраса (коэффициент 0,3) | 7,55        |
|                 |                           | 212,79      |
| 4.62            |                           |             |
| 62.1            | Холл                      | 13,62       |
| 62.2            | Кухня-столовая            | 55,58       |
| 62.3            | Спальня с гардеробной     | 23,69       |
| 62.4            | Спальня                   | 13,97       |
| 62.5            | Спальня                   | 15,94       |
| 62.6            | С/у                       | 6,29        |
| 62.7            | С/у                       | 4,50        |
| 62.8            | Гардеробная               | 4,35        |
| 62.9            | Постирочная               | 2,70        |

Экспликация помещений квартир 16 этажа

| Номер помещения | Наименование              | Площадь, м2 |
|-----------------|---------------------------|-------------|
| 62.10           | Холл                      | 1,74        |
| 62.11           | Терраса (коэффициент 0,3) | 7,55        |
|                 |                           | 149,93      |
| 4.63            |                           |             |
| 63.1            | Холл                      | 10,17       |
| 63.2            | Кухня-столовая            | 50,79       |
| 63.3            | Спальня с гардеробной     | 24,56       |
| 63.4            | Спальня                   | 13,58       |
| 63.5            | Спальня                   | 25,90       |
| 63.6            | Спальня                   | 17,75       |
| 63.7            | С/у                       | 8,40        |
| 63.8            | С/у                       | 4,03        |
| 63.9            | С/у                       | 5,16        |
| 63.10           | С/у                       | 3,68        |
| 63.11           | Гардеробная               | 2,55        |
| 63.12           | Холл                      | 3,72        |
| 63.13           | Холл                      | 3,08        |
| 63.14           | Терраса (коэффициент 0,3) | 7,55        |
|                 |                           | 180,92      |
|                 |                           | 543,64      |

Экспликация МОП 16 этажа

| Номер помещения | Наименование         | Площадь, м² |
|-----------------|----------------------|-------------|
| 416.1           | Лифтовый холл ПБЗ    | 13,14       |
| 416.2           | Лестничная клетка Л4 | 17,40       |
| 416.3           | Коридор              | 8,45        |
| 416.4           | Коридор              | 8,45        |
|                 |                      | 47,44       |


УСЛОВНЫЕ ОБОЗНАЧЕНИЯ

- железобетонные конструкции
- стена из газобетонных блоков толщ. 200 мм
- перегородка из газобетонных блоков толщ.100 мм


- маркировка помещений квартиры
  - маркировка помещений общего пользования
- номер квартиры
- номер помещения
- номер корпуса
- этаж
- номер помещения

Марка квартиры:

|       |                                                           |
|-------|-----------------------------------------------------------|
| 1.11  | Номер квартиры                                            |
| 22.22 | Жилая площадь квартиры                                    |
| 33.33 | Общая площадь квартиры без учета неотапливаемых помещений |
| 44.44 | Общая площадь квартиры с учетом понижающих коэффициентов  |
|       | Код типа планировки                                       |
|       | Количество жилых комнат в квартире                        |

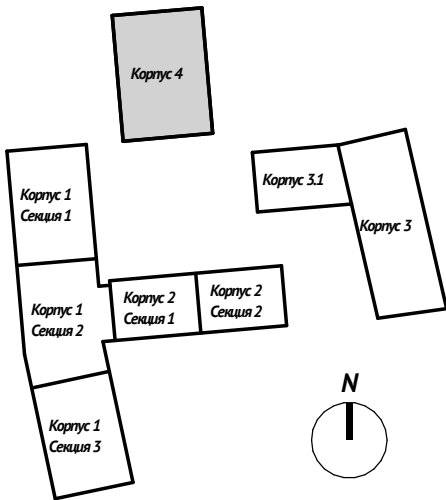


|              |           |      |        |                                                                                       |       |                                                                                         |                                                                                       |      |        |
|--------------|-----------|------|--------|---------------------------------------------------------------------------------------|-------|-----------------------------------------------------------------------------------------|---------------------------------------------------------------------------------------|------|--------|
|              |           |      |        |                                                                                       |       | АА/БЗ-03-ДСЗ - АР1                                                                      |                                                                                       |      |        |
|              |           |      |        |                                                                                       |       | "Жилой комплекс", расположенный по адресу: г. Москва, ЦАО, Садовническая ул., вл. 76/71 |                                                                                       |      |        |
| Изм.         | Кол.уч.   | Лист | № док. | Подп.                                                                                 | Дата  | Часть 1. Архитектурные решения.<br>Планы.                                               | Стадия                                                                                | Лист | Листов |
| Разработал   | Карасёв   |      |        |  | 08.24 |                                                                                         | П                                                                                     | 20   |        |
| Разработал   | Задорина  |      |        |  | 08.24 |                                                                                         |                                                                                       |      |        |
| Проверил     | Добрякова |      |        |  | 08.24 |                                                                                         |                                                                                       |      |        |
|              |           |      |        |                                                                                       |       | Корпус 4. План 16 этажа. М 1_200.                                                       |  |      |        |
| Норм. контр. | Добрякова |      |        |  | 08.24 |                                                                                         |                                                                                       |      |        |

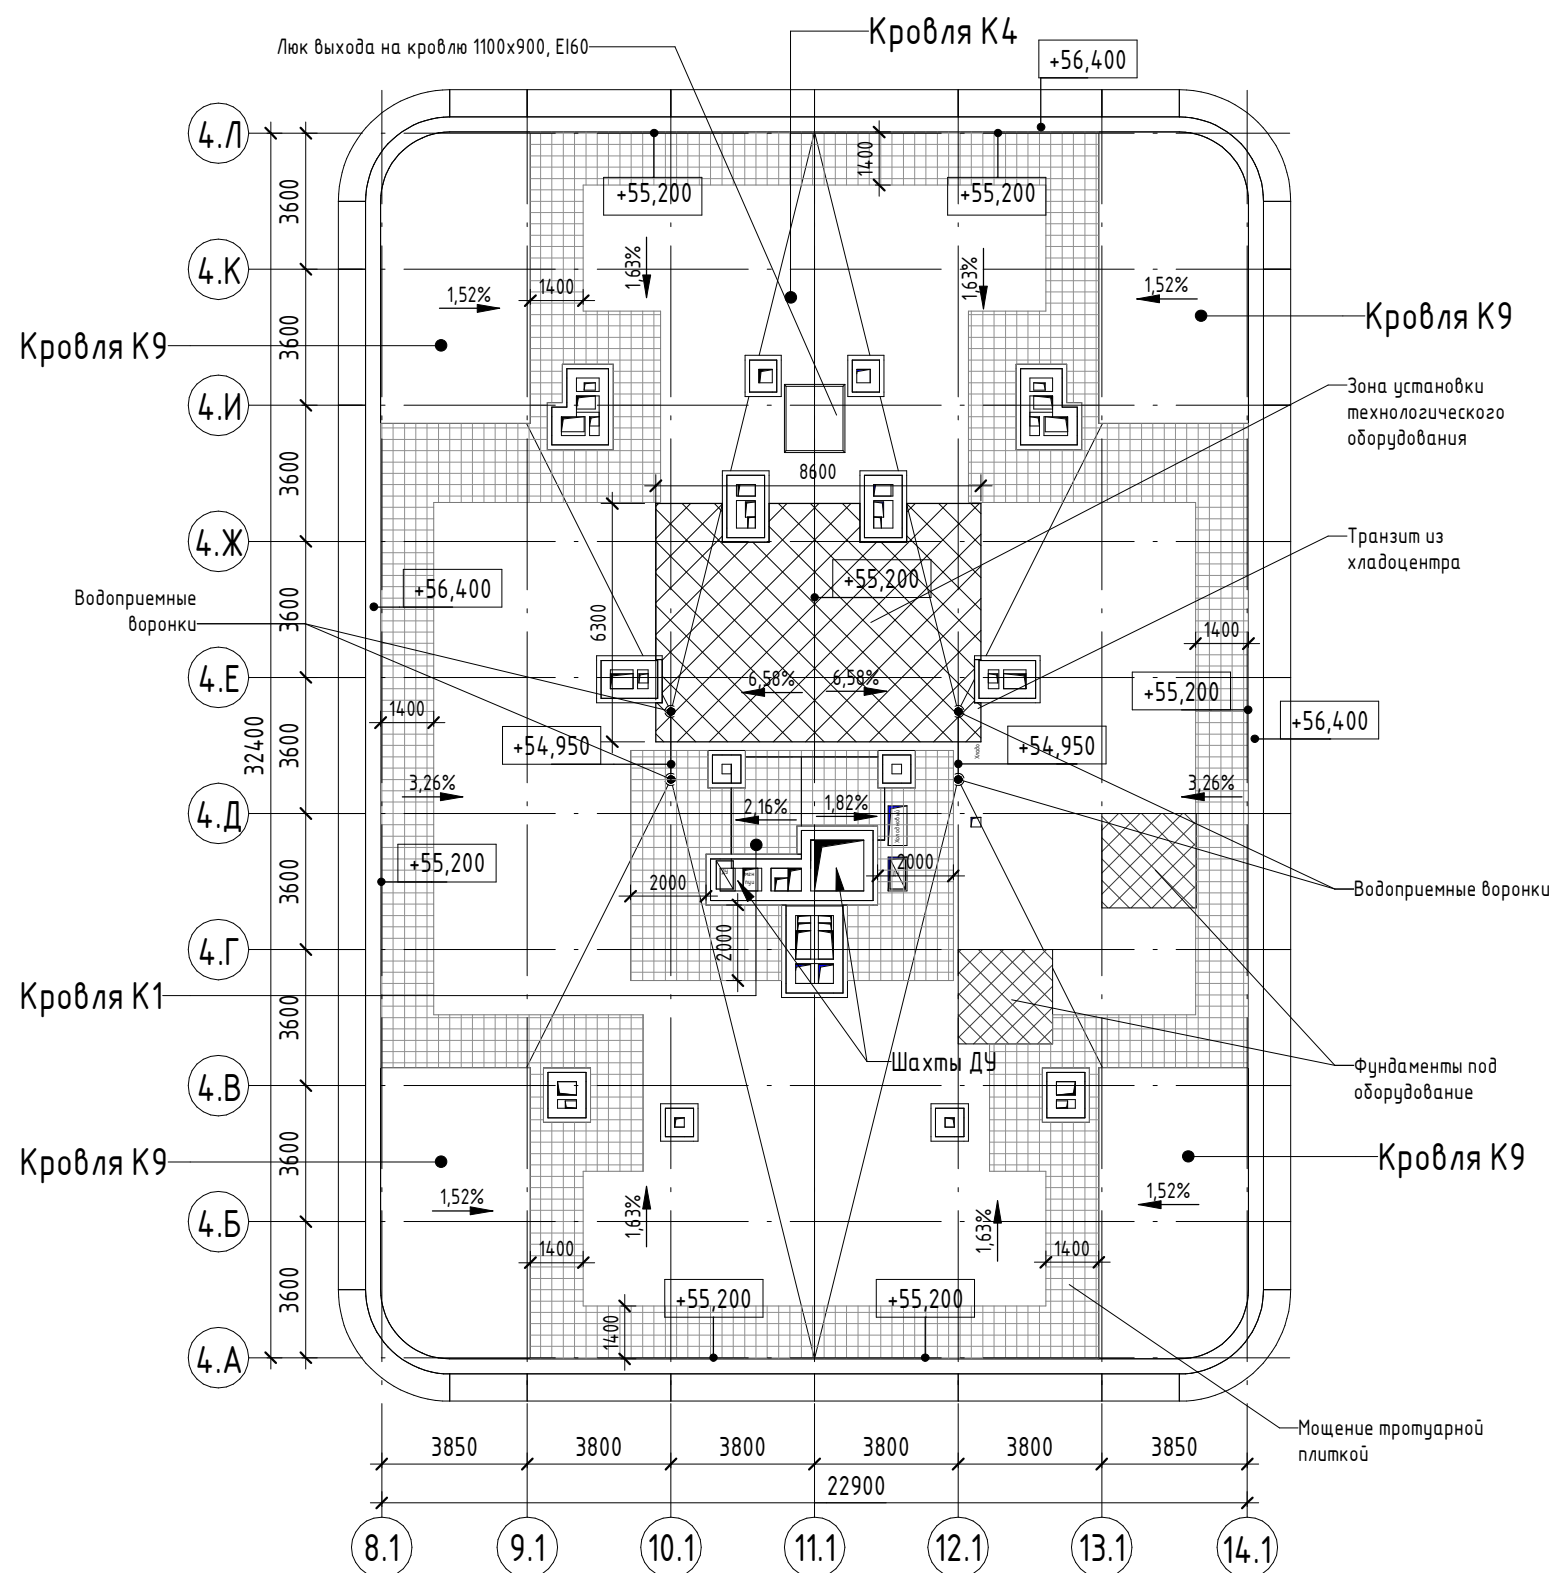

|                                                                 |             |
|-----------------------------------------------------------------|-------------|
| Кровля тип К1 (толщ. 350-400мм)                                 |             |
| Гравий промытый                                                 | -50 мм      |
| Дренажная мембрана ВИЛЛАДРЕЙН или аналог                        | -8 мм       |
| Геотекстиль ИКОПАЛ 300                                          |             |
| Гидроизоляция ИКОПАЛ Ультра В, 1 слой или аналог                | -5 мм       |
| Гидроизоляция ИКОПАЛ Ультра Н, 1 слой или аналог                | -5 мм       |
| Цементно-песчаная стяжка М150, армированная сеткой 4Вр1 100х100 | -40 мм      |
| Уклонообразующий слой из керамзитобетона                        | -30...80 мм |
| Полиэтиленовая пленка 2 слоя                                    |             |
| Минераловатный утеплитель из каменного волокна 180 кг/м3        | -50 мм      |
| Минераловатный утеплитель из каменного волокна НГ 80-125 кг/м3  | -150 мм     |
| Пароизоляционная пленка                                         |             |
| Праймер СБС ИКОПАЛ                                              |             |
| Выравнивающая стяжка из цементно-песчаного раствора М150        | -12 мм      |
| Железобетонная плита перекрытия (см. КР)                        |             |

|                                                                 |              |
|-----------------------------------------------------------------|--------------|
| Кровля тип К4 (толщ. 350–600мм)                                 |              |
| Гравий промытый                                                 | –50 мм       |
| Дренажная мембрана ВИЛЛАДРЕЙН или аналог                        | –8 мм        |
| Геотекстиль ИКОПАЛ 300                                          |              |
| Гидроизоляция ИКОПАЛ Ультра В, 1 слой или аналог                | –5 мм        |
| Гидроизоляция ИКОПАЛ Ультра Н, 1 слой или аналог                | –5 мм        |
| Цементно-песчаная стяжка М150, армированная сеткой 4Вр1 100х100 | –40 мм       |
| Уклонообразующий слой из керамзитобетона                        | –30...280 мм |
| Полиэтиленовая пленка 2 слоя                                    |              |
| Минераловатный утеплитель из каменного волокна 180 кг/м3        | –50 мм       |
| Минераловатный утеплитель из каменного волокна НГ 80–125 кг/м3  | –150 мм      |
| Пароизоляционная пленка                                         |              |
| Праймер СБС ИКОПАЛ                                              |              |
| Выравнивающая стяжка из цементно-песчаного раствора М150        | –12 мм       |
| Железобетонная плита перекрытия (см. КР)                        |              |

|                                                                |              |
|----------------------------------------------------------------|--------------|
| Кровля тип К9 (толщ. 160–220мм)                                |              |
| Гидроизоляция ИКОПАЛ Ультра В, 1 слой или аналог               | –5 мм        |
| Гидроизоляция ИКОПАЛ Ультра Н, 1 слой или аналог               | –5 мм        |
| Цем.-песч. стяжка М150 по уклону, армиров. сеткой 4Вр1 100х100 | –40...100 мм |
| Утеплитель ЭППС 35                                             | –100 мм      |
| Праймер СБС ИКОПАЛ                                             |              |
| Выравнивающая стяжка из цементно-песчаного раствора М150       | –10 мм       |
| Железобетонная плита перекрытия (см. КР)                       |              |

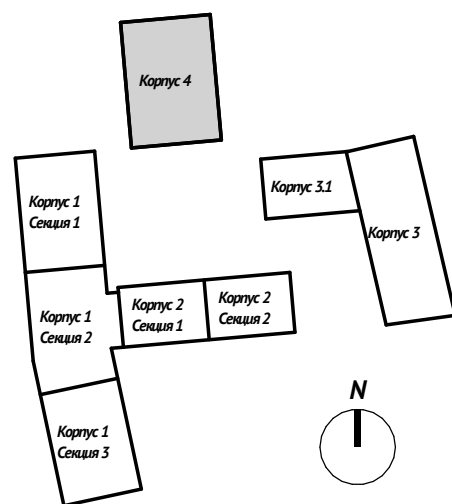

|              |         |           |        |                                                                                       |       |                                                                                         |        |      |        |
|--------------|---------|-----------|--------|---------------------------------------------------------------------------------------|-------|-----------------------------------------------------------------------------------------|--------|------|--------|
|              |         |           |        |                                                                                       |       | АА/БЗ-03-ДС - АР1                                                                       |        |      |        |
|              |         |           |        |                                                                                       |       | "Жилой комплекс", расположенный по адресу: г. Москва, ЦАО, Садовническая ул., вл. 76/71 |        |      |        |
| Изм.         | Кол.уч. | Лист      | № док. | Подп.                                                                                 | Дата  |                                                                                         |        |      |        |
| Разработал   |         | Карасёв   |        |  | 08.24 | Часть 1. Архитектурные решения.<br>Планы.                                               | Стадия | Лист | Листов |
| Разработал   |         | Задорина  |        |  | 08.24 |                                                                                         | П      | 21   |        |
| Проверил     |         | Добрякова |        |  | 08.24 |                                                                                         |        |      |        |
|              |         |           |        |                                                                                       |       | Корпус 4. План кровли. М 1_200.                                                         | ARTES  |      |        |
| Норм. контр. |         | Добрякова |        |  | 08.24 |                                                                                         |        |      |        |

| Инв. № подл. | Подп. и дата | Взам. инв. № |
|--------------|--------------|--------------|
|              |              |              |



|                                                                 |             |
|-----------------------------------------------------------------|-------------|
| Кровля тип К1 (толщ. 350-400мм)                                 |             |
| Гравий промытый                                                 | -50 мм      |
| Дренажная мембрана ВИЛЛАДРЕЙН или аналог                        | -8 мм       |
| Геотекстиль ИКОПАЛ 300                                          |             |
| Гидроизоляция ИКОПАЛ Ультра В, 1 слой или аналог                | -5 мм       |
| Гидроизоляция ИКОПАЛ Ультра Н, 1 слой или аналог                | -5 мм       |
| Цементно-песчаная стяжка М150, армированная сеткой 4Вр1 100х100 | -40 мм      |
| Уклонообразующий слой из керамзитобетона                        | -30...80 мм |
| Полэтиленовая пленка 2 слоя                                     |             |
| Минераловатный утеплитель из каменного волокна 180 кг/м3        | -50 мм      |
| Минераловатный утеплитель из каменного волокна НГ 80-125 кг/м3  | -150 мм     |
| Пароизоляционная пленка                                         |             |
| Праймер СБС ИКОПАЛ                                              |             |
| Выравнивающая стяжка из цементно-песчаного раствора М150        | -12 мм      |
| Железобетонная плита перекрытия (см. КР)                        |             |

|                                                                 |              |
|-----------------------------------------------------------------|--------------|
| Кровля тип К2 (толщ. 350-500мм)                                 |              |
| Гравий промытый                                                 | -50 мм       |
| Дренажная мембрана ВИЛЛАДРЕЙН или аналог                        | -8 мм        |
| Геотекстиль ИКОПАЛ 300                                          |              |
| Гидроизоляция ИКОПАЛ Ультра В, 1 слой или аналог                | -5 мм        |
| Гидроизоляция ИКОПАЛ Ультра Н, 1 слой или аналог                | -5 мм        |
| Цементно-песчаная стяжка М150, армированная сеткой 4Вр1 100х100 | -40 мм       |
| Уклонообразующий слой из керамзитобетона                        | -30...180 мм |
| Полэтиленовая пленка 2 слоя                                     |              |
| Минераловатный утеплитель из каменного волокна 180 кг/м3        | -50 мм       |
| Минераловатный утеплитель из каменного волокна НГ 80-125 кг/м3  | -150 мм      |
| Пароизоляционная пленка                                         |              |
| Праймер СБС ИКОПАЛ                                              |              |
| Выравнивающая стяжка из цементно-песчаного раствора М150        | -12 мм       |
| Железобетонная плита перекрытия (см. КР)                        |              |

|                                                                 |              |
|-----------------------------------------------------------------|--------------|
| Кровля тип К3 (толщ. 350-550мм)                                 |              |
| Гравий промытый                                                 | -50 мм       |
| Дренажная мембрана ВИЛЛАДРЕЙН или аналог                        | -8 мм        |
| Геотекстиль ИКОПАЛ 300                                          |              |
| Гидроизоляция ИКОПАЛ Ультра В, 1 слой или аналог                | -5 мм        |
| Гидроизоляция ИКОПАЛ Ультра Н, 1 слой или аналог                | -5 мм        |
| Цементно-песчаная стяжка М150, армированная сеткой 4Вр1 100х100 | -40 мм       |
| Уклонообразующий слой из керамзитобетона                        | -30...230 мм |
| Полэтиленовая пленка 2 слоя                                     |              |
| Минераловатный утеплитель из каменного волокна 180 кг/м3        | -50 мм       |
| Минераловатный утеплитель из каменного волокна НГ 80-125 кг/м3  | -150 мм      |
| Пароизоляционная пленка                                         |              |
| Праймер СБС ИКОПАЛ                                              |              |
| Выравнивающая стяжка из цементно-песчаного раствора М150        | -12 мм       |
| Железобетонная плита перекрытия (см. КР)                        |              |

|                                                                 |              |
|-----------------------------------------------------------------|--------------|
| Кровля тип К4 (толщ. 350-600мм)                                 |              |
| Гравий промытый                                                 | -50 мм       |
| Дренажная мембрана ВИЛЛАДРЕЙН или аналог                        | -8 мм        |
| Геотекстиль ИКОПАЛ 300                                          |              |
| Гидроизоляция ИКОПАЛ Ультра В, 1 слой или аналог                | -5 мм        |
| Гидроизоляция ИКОПАЛ Ультра Н, 1 слой или аналог                | -5 мм        |
| Цементно-песчаная стяжка М150, армированная сеткой 4Вр1 100х100 | -40 мм       |
| Уклонообразующий слой из керамзитобетона                        | -30...280 мм |
| Полэтиленовая пленка 2 слоя                                     |              |
| Минераловатный утеплитель из каменного волокна 180 кг/м3        | -50 мм       |
| Минераловатный утеплитель из каменного волокна НГ 80-125 кг/м3  | -150 мм      |
| Пароизоляционная пленка                                         |              |
| Праймер СБС ИКОПАЛ                                              |              |
| Выравнивающая стяжка из цементно-песчаного раствора М150        | -12 мм       |
| Железобетонная плита перекрытия (см. КР)                        |              |

Покрытие ТЕПЛОТРАССЫ тип ПТТ. 1 корпус

|                                                          |             |
|----------------------------------------------------------|-------------|
| Уплотненный со щебнем грунт                              |             |
| Мембрана ВИЛЛАДРЕЙН 8 Гео                                | -10 мм      |
| Гидроизоляция УЛЬТРАНАП, наплавлена                      | -5 мм       |
| Гидроизоляция ИКОПАЛ Н ЭПП, наплавлена                   | -5 мм       |
| Праймер СБС ИКОПАЛ                                       |             |
| Стяжка цементно-песчаная М200, армированная 4Вр1 100х100 | -40...80 мм |
| Полэтиленовая пленка                                     |             |
| Жесткий дорожный утеплитель Ravatherm XPS Standart 50    | -100 мм     |
| Изоляция УЛЬТРАДРАЙВ, наплавлена, 1 слой                 | -10 мм      |
| Праймер СБС ИКОПАЛ                                       |             |
| Железобетонная плита                                     |             |

|                                                                 |              |
|-----------------------------------------------------------------|--------------|
| Кровля тип К5 (с лотками): Гравий промытый                      | -50 мм       |
| Дренажная мембрана ВИЛЛАДРЕЙН или аналог                        | -8 мм        |
| Геотекстиль ИКОПАЛ 300                                          |              |
| Гидроизоляция ИКОПАЛ Ультра В, 1 слой или аналог                | -5 мм        |
| Гидроизоляция ИКОПАЛ Ультра Н, 1 слой или аналог                | -5 мм        |
| Цементно-песчаная стяжка М150, армированная сеткой 4Вр1 100х100 | -40 мм       |
| Уклонообразующий слой из керамзитобетона                        | -40...190 мм |
| Цементно-песчаная стяжка М150, армированная сеткой 4Вр1 100х100 | -40 мм       |
| Полэтиленовая пленка 2 слоя                                     |              |
| Минераловатный утеплитель из каменного волокна 180 кг/м3        | -50 мм       |
| Минераловатный утеплитель из каменного волокна НГ 80-125 кг/м3  | -150 мм      |
| Пароизоляционная пленка                                         |              |
| Праймер СБС ИКОПАЛ                                              |              |
| Выравнивающая стяжка из цементно-песчаного раствора М150        | -12 мм       |
| Железобетонная плита перекрытия (см. КР)                        |              |

|   |         |
|---|---------|
| Кровля тип К6 (скатная)                                                                                 |         |
| Фальцевая медная кровля                                                                                 | -0.8 мм |
| Подстилающий слой (руберойд, изол, гидроизол или аналог)                                                |         |
| Сплошной настил из досок хвойных пород                                                                  | -22 мм  |
| Контробрешетка (50х50) на брусу и воздушный зазор                                                       | -50 мм  |
| Гидроветрозащитная паропроницаемая мембрана                                                             |         |
| Минераловатный утеплитель из каменного волокна НГ 80-125 кг/м3                                          |         |
| между деревянными антипирированными брусками (50х150, шаг 600)                                          | -150 мм |
| Пароизоляционная пленка                                                                                 |         |
| Контрутепление между деревянными антипирированными брусками (50х50, шаг 600) -минераловатный утеплитель |         |
| из каменного волокна НГ 80-125 кг/м3                                                                    | -50 мм  |
| 2 слоя ГВЛВ по 12.5 мм                                                                                  | -25 мм  |

|                                                           |             |
|-----------------------------------------------------------|-------------|
| Кровля тип К7 (покрытие автостоянки)                      |             |
| Покрытие см. раздел ПЗУ                                   |             |
| Щебень фракции 5-20 мм                                    | -перем.     |
| Мембрана ВИЛЛАДРЕЙН 8 Гео                                 | -10 мм      |
| Гидроизоляция УЛЬТРАНАП, наплавлена                       | -5 мм       |
| Гидроизоляция ИКОПАЛ Н ЭПП, наплавлена                    | -5 мм       |
| Праймер СБС ИКОПАЛ                                        |             |
| Бетонная разгрузочная плита В25, армированная Вр1 100х100 | -150 мм     |
| Уклонообразующий слой из керамзитобетона 900 кг/м3        | -0...550 мм |
| Полэтиленовая пленка                                      |             |
| Жесткий дорожный утеплитель Ravatherm XPS Standart 50     | -50 мм      |
| Изоляция УЛЬТРАДРАЙВ, наплавлена, 1 слой                  | -10 мм      |
| Праймер СБС ИКОПАЛ                                        |             |
| Железобетонная плита                                      |             |

|                                                          |         |
|----------------------------------------------------------|---------|
| Кровля тип К8 (покрытие рамы по уклону)                  |         |
| Грунт - дренажный слой песчано-гравийной смеси           | -150 мм |
| Мембрана ВИЛЛАДРЕЙН 8 Гео                                | -10 мм  |
| Гидроизоляция УЛЬТРАНАП, наплавлена                      | -5 мм   |
| Гидроизоляция ИКОПАЛ Н ЭПП, наплавлена                   | -5 мм   |
| Праймер СБС ИКОПАЛ                                       |         |
| Стяжка цементно-песчаная М150, армированная 4Вр1 100х100 | -30 мм  |
| Полэтиленовая пленка                                     |         |
| Жесткий дорожный утеплитель Ravatherm XPS Standart 50+50 | -100 мм |
| Изоляция УЛЬТРАДРАЙВ, наплавлена, 1 слой                 | -5 мм   |
| Праймер СБС ИКОПАЛ                                       |         |
| Железобетонная плита                                     |         |

|                                                                 |              |
|-----------------------------------------------------------------|--------------|
| Кровля тип К9 (толщ. 160-220мм) 4 корпус над террасами 10 этажа |              |
| Гидроизоляция ИКОПАЛ Ультра В, 1 слой или аналог                | -5 мм        |
| Гидроизоляция ИКОПАЛ Ультра Н, 1 слой или аналог                | -5 мм        |
| Цем.-песч. стяжка М150 по уклону, армиров. сеткой 4Вр1 100х100  | -40...100 мм |
| Утеплитель ЭППС 35                                              | -100 мм      |
| Праймер СБС ИКОПАЛ                                              |              |
| Выравнивающая стяжка из цементно-песчаного раствора М150        | -10 мм       |
| Железобетонная плита перекрытия (см. КР)                        |              |

|                                                                 |             |
|-----------------------------------------------------------------|-------------|
| Покрытие тип ПТ1 (покрытие террасы по грунту)                   |             |
| Плитка из природного камня                                      | -20 мм      |
| Прослойка и заполнение швов из цементно-песчаного раствора М100 | -10 мм      |
| Стяжка цементно-песчаная М150, армированная 4Вр1 100х100        | -30...90 мм |
| Гидроизол на битумной мастике (см. черт. КР)                    | -5 мм       |
| Стяжка выравнивающая из цементно-песчаного раствора М100        | -30 мм      |
| Подстилающий слой из бетона В7.5                                | -100 мм     |
| Уплотненный со щебнем грунт                                     |             |

|                                                                   |              |
|-------------------------------------------------------------------|--------------|
| Покрытие тип ПТ2 (толщ. 260...350мм - террасы корп.1 этаж 5)      |              |
| Бетонная тротуар. плитка с засышкой швов мелким гравием (фр. 5мм) | -50 мм       |
| Дренажная мембрана ВИЛЛАДРЕЙН или аналог                          | -8 мм        |
| Геотекстиль ИКОПАЛ 300                                            |              |
| Гидроизоляция ИКОПАЛ Ультра В, 1 слой или аналог                  | -5 мм        |
| Гидроизоляция ИКОПАЛ Ультра Н, 1 слой или аналог                  | -5 мм        |
| Цементно-песчаная стяжка М150, армированная сеткой 4Вр1 100х100   | -30...120 мм |
| Утеплитель ЭППС 35                                                | -150 мм      |
| Пароизоляционная пленка                                           |              |
| Праймер СБС ИКОПАЛ                                                |              |
| Выравнивающая стяжка из цементно-песчаного раствора М150          | -12 мм       |
| Железобетонная плита перекрытия (см. КР)                          |              |

|                                                                   |              |
|-------------------------------------------------------------------|--------------|
| Покрытие тип ПТ3 (терраса над рамой, лоток)                       |              |
| Бетонная тротуар. плитка с засышкой швов мелким гравием (фр. 5мм) | -50 мм       |
| Дренажная мембрана ВИЛЛАДРЕЙН или аналог                          | -8 мм        |
| Геотекстиль ИКОПАЛ 300                                            |              |
| Гидроизоляция ИКОПАЛ Ультра В, 1 слой или аналог                  | -5 мм        |
| Гидроизоляция ИКОПАЛ Ультра Н, 1 слой или аналог                  | -5 мм        |
| Цементно-песчаная стяжка М150, армированная сеткой 4Вр1 100х100   | -40 мм       |
| Уклонообразующий слой из керамзитобетона                          | -40...180 мм |
| Утеплитель ЭППС 35                                                | -100 мм      |
| Пароизоляционная пленка                                           |              |
| Праймер СБС ИКОПАЛ                                                |              |
| Выравнивающая стяжка из цементно-песчаного раствора М150          | -12 мм       |
| Железобетонная плита перекрытия (см. КР)                          |              |

|                                                                   |              |
|-------------------------------------------------------------------|--------------|
| Покрытие тип ПТ4 (террасы корп. 3.1, лоток)                       |              |
| Бетонная тротуар. плитка с засышкой швов мелким гравием (фр. 5мм) | -50 мм       |
| Дренажная мембрана ВИЛЛАДРЕЙН или аналог                          | -8 мм        |
| Геотекстиль ИКОПАЛ 300                                            |              |
| Гидроизоляция ИКОПАЛ Ультра В, 1 слой или аналог                  | -5 мм        |
| Гидроизоляция ИКОПАЛ Ультра Н, 1 слой или аналог                  | -5 мм        |
| Цементно-песчаная стяжка М150, армированная сеткой 4Вр1 100х100   | -40 мм       |
| Уклонообразующий слой из керамзитобетона                          | -40...130 мм |
| Утеплитель ЭППС 35                                                | -150 мм      |
| Пароизоляционная пленка                                           |              |
| Праймер СБС ИКОПАЛ                                                |              |
| Выравнивающая стяжка из цементно-песчаного раствора М150          | -12 мм       |
| Железобетонная плита перекрытия (см. КР)                          |              |

|                                                                   |              |
|-------------------------------------------------------------------|--------------|
| Покрытие тип ПТ5 (террасы корп. 4)                                |              |
| Бетонная тротуар. плитка с засышкой швов мелким гравием (фр. 5мм) | -50 мм       |
| Дренажная мембрана ВИЛЛАДРЕЙН или аналог                          | -8 мм        |
| Геотекстиль ИКОПАЛ 300                                            |              |
| Гидроизоляция ИКОПАЛ Ультра В, 1 слой или аналог                  | -5 мм        |
| Гидроизоляция ИКОПАЛ Ультра Н, 1 слой или аналог                  | -5 мм        |
| Цементно-песчаная стяжка М150, армированная сеткой 4Вр1 100х100   | -40 мм       |
| Уклонообразующий слой из керамзитобетона                          | -30...130 мм |
| Утеплитель ЭППС 35                                                | -150 мм      |
| Пароизоляционная пленка                                           |              |
| Праймер СБС ИКОПАЛ                                                |              |
| Выравнивающая стяжка из цементно-песчаного раствора М150          | -12 мм       |
| Железобетонная плита перекрытия (см. КР)                          |              |

Покрытие АРКИ тип ПА. 2 корпус (совместно с черт. ГП)

|                                                             |              |
|-------------------------------------------------------------|--------------|
| Бетонная тротуарная плитка по ГОСТ 17608-2017               | -60 мм       |
| Сухая цементопесчаная смесь М100 по ГОСТ 31357-2007         | -40 мм       |
| Бетонная плита В25, армированная Вр1 100х100                | -80 мм       |
| Щебеночные смеси по ГОСТ 25607-2009 по уклону (см.черт. ГП) | -20...150 мм |
| Мембрана ВИЛЛАДРЕЙН 8 Гео                                   | -10 мм       |
| Гидроизоляция УЛЬТРАНАП, наплавлена                         | -5 мм        |
| Гидроизоляция ИКОПАЛ Н ЭПП, наплавлена                      | -5 мм        |
| Праймер СБС ИКОПАЛ                                          |              |
| Стяжка цементно-песчаная М200, армированная 4Вр1 100х100    | -40 мм       |
| Полэтиленовая пленка                                        |              |
| Жесткий дорожный утеплитель Ravatherm XPS Standart 50       | -100 мм      |
| Изоляция УЛЬТРАДРАЙВ, наплавлена, 1 слой                    | -10 мм       |
| Праймер СБС ИКОПАЛ                                          |              |
| Железобетонная плита                                        |              |

|                                                           |        |
|-----------------------------------------------------------|--------|
| Пол тип П1.1 (1 этаж МОП сухие)                           |        |
| Керамогранитная плитка с шероховатой поверхностью на клее | -20 мм |
| Грунтовка                                                 |        |
| Фиброцементная стяжка М150                                | -40 мм |
| Полэтиленовая пленка 2 слоя                               |        |
| Минераловатный утеплитель из каменного волокна 180 кг/м3  | -80 мм |
| Выравнивающий слой из бетона                              | -10 мм |
| Железобетонная плита перекрытия (см. КР)                  |        |

|                                                                  |        |
|------------------------------------------------------------------|--------|
| Пол тип П1.2 (1 этаж МОП мокрые)                                 |        |
| Керамогранитная плитка с шероховатой поверхностью на клее        | -20 мм |
| Грунтовка                                                        |        |
| Гидроизоляция Глимс Водостоп 2 слоя (завести на стены на 300 мм) | -5 мм  |
| Грунтовка                                                        |        |
| Фиброцементная стяжка М150                                       | -40 мм |
| Полэтиленовая пленка 2 слоя                                      |        |
| Минераловатный утеплитель из каменного волокна 180 кг/м3         | -80 мм |
| Выравнивающая затирка цементно-песчаным раствором                | -5 мм  |
| Железобетонная плита перекрытия (см. КР)                         |        |

|                                                          |        |
|----------------------------------------------------------|--------|
| Пол тип П1.3 (1 этаж квартиры сухие)                     |        |
| Финишное покрытие (выполняется собственником помещения)  | -20 мм |
| Грунтовка                                                |        |
| Фиброцементная стяжка М150                               | -40 мм |
| Полэтиленовая пленка 2 слоя                              |        |
| Минераловатный утеплитель из каменного волокна 180 кг/м3 | -80 мм |
| Выравнивающая затирка цементно-песчаным раствором        | -10 мм |
| Железобетонная плита перекрытия (см. КР)                 |        |

|                                                                  |        |
|------------------------------------------------------------------|--------|
| Пол тип П1.4 (1 этаж квартиры мокрые)                            |        |
| Финишное покрытие (выполняется собственником помещения)          | -20 мм |
| Грунтовка                                                        |        |
| Гидроизоляция Глимс Водостоп 2 слоя (завести на стены на 300 мм) | -5 мм  |
| Грунтовка                                                        |        |
| Фиброцементная стяжка М150                                       | -40 мм |
| Полэтиленовая пленка 2 слоя                                      |        |
| Минераловатный утеплитель из каменного волокна 180 кг/м3         | -80 мм |
| Выравнивающая затирка цементно-песчаным раствором                | -5 мм  |
| Железобетонная плита перекрытия (см. КР)                         |        |

|                                           |            |
|-------------------------------------------|------------|
| Фасад тип Ц1                              |            |
| Финишная облицовка                        |            |
| Воздушный зазор                           | -min 50 мм |
| Утеплитель - пеностекло плитное 120 кг/м3 | -180 мм    |
| Гидроизоляция подземной части (см. КР)    |            |
| Ж/В стена (см. КР)                        | -200 мм    |

|                                           |         |
|-------------------------------------------|---------|
| Фасад тип Ц2                              |         |
| Облицовка натуральным камнем              | -30 мм  |
| Кирпичная кладка                          | -120 мм |
| Утеплитель - пеностекло плитное 120 кг/м3 | -150 мм |
| Гидроизоляция подземной части (см. КР)    |         |
| Ж/В стена (см. КР)                        | -200 мм |

|                                                                |            |
|----------------------------------------------------------------|------------|
| Фасад тип Ф1                                                   |            |
| Облицовка глазурованной керамической плиткой                   | -15 мм     |
| Воздушный зазор                                                | -min 50 мм |
| Утеплитель минераловатный 90 кг/м3 (Вентил Баттс или аналог)   | -80 мм     |
| Утеплитель минераловатный 37 кг/м3 (Вентил Баттс Н или аналог) | -100 мм    |
| Газовентонные блоки D600/ Ж/В стена (см. КР)                   | -200 мм    |
| Цементно-песчаная штукатурка по сетке                          | -15 мм     |

|                                                                |         |
|----------------------------------------------------------------|---------|
| Фасад тип Ф2                                                   |         |
| Облицовка полимербетоном (СФБ)                                 | -20 мм  |
| Воздушный зазор                                                | -90 мм  |
| Утеплитель минераловатный 90 кг/м3 (Вентил Баттс или аналог)   | -80 мм  |
| Утеплитель минераловатный 37 кг/м3 (Вентил Баттс Н или аналог) | -100 мм |
| Ж/В стена (см. КР)                                             | -200 мм |
| Цементно-песчаная штукатурка по сетке                          | -15 мм  |

|                                                                |         |
|----------------------------------------------------------------|---------|
| Фасад тип Ф3                                                   |         |
| Облицовка натуральным камнем                                   | -20 мм  |
| Воздушный зазор                                                | -90 мм  |
| Утеплитель минераловатный 90 кг/м3 (Вентил Баттс или аналог)   | -80 мм  |
| Утеплитель минераловатный 37 кг/м3 (Вентил Баттс Н или аналог) | -100 мм |
| Ж/В стена (см. КР)                                             | -200 мм |
| Цементно-песчаная штукатурка по сетке                          | -15 мм  |

|                                                 |         |
|-------------------------------------------------|---------|
| Фасад тип Ф4                                    |         |
| Штукатурка цементно-песчаным раствором по сетке | -30 мм  |
| Кладка из полнотелого кирпича                   | -120 мм |
| Утеплитель минераловатные плиты НГ 125 кг/м3    | -150 мм |
| Ж/В стена (см. КР)                              | -200 мм |

|                                                                |         |
|----------------------------------------------------------------|---------|
| Фасад тип Ф5                                                   |         |
| Облицовка композитной фасадной панелью                         | -10 мм  |
| Воздушный зазор                                                | -90 мм  |
| Утеплитель минераловатный 90 кг/м3 (Вентил Баттс или аналог)   | -80 мм  |
| Утеплитель минераловатный 37 кг/м3 (Вентил Баттс Н или аналог) | -100 мм |
| Ж/В стена (см. КР)                                             | -200 мм |
| Цементно-песчаная штукатурка по сетке                          | -15 мм  |

|                                                                |            |
|----------------------------------------------------------------|------------|
| Фасад тип Ф6 (подшивка снизу)                                  |            |
| Ж/В перекрытие                                                 | -200 мм    |
| Утеплитель минераловатный 37 кг/м3 (Вентил Баттс Н или аналог) | -100 мм    |
| Утеплитель минераловатный 90 кг/м3 (Вентил Баттс или аналог)   | -100 мм    |
| Воздушный зазор                                                | -min 50 мм |
| Облицовка композитной фасадной панелью                         | -10 мм     |

|                                                                |         |
|----------------------------------------------------------------|---------|
| Фасад тип Ф7 (злужие участки витражей)                         |         |
| Однокамерный стеклопакет с тонированным стеклом                | -40 мм  |
| Воздушный зазор                                                | -50 мм  |
| Утеплитель минераловатный 90 кг/м3 (Вентил Баттс или аналог)   | -50 мм  |
| Утеплитель минераловатный 37 кг/м3 (Вентил Баттс Н или аналог) | -100 мм |
| Ж/В стена (см. КР)                                             |         |

|                                                           |        |
|-----------------------------------------------------------|--------|
| Стена внутренняя между помещением КПП и рампой (Корпус 3) |        |
| Ж/В стена (см. КР)                                        |        |
| Утеплитель минераловатные плиты плотность 180 кг/м3       | -80 мм |
| Цементно-песчаная штукатурка по сетке                     | -20 мм |