

**«Жилой комплекс» расположенный по адресу: г. Москва, ЦАО,
 Садовническая ул., вл 76/71**

ПРОЕКТНАЯ ДОКУМЕНТАЦИЯ

Раздел 2. Схема планировочной организации земельного участка

АА/БЭ- 03-ДСЗ-ПЗУ

Корректировка

Том 2

Инв. № подл. Инв.	Подп. и дата	Подп. и дата	Взам. инв. №Взам.

**«Жилой комплекс» расположенный по адресу: г. Москва, ЦАО,
Садовническая ул., вл 76/71**

ПРОЕКТНАЯ ДОКУМЕНТАЦИЯ

Раздел 2. Схема планировочной организации земельного участка

АА/БЭ- 03-ДСЗ-ПЗУ

Корректировка


Том 2

Главный архитектор



Е.Г. Ким

Главный инженер проекта

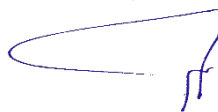

В.В. Остроумов

Главный архитектор проекта



А.В. Добрякова

инв. №

№ подл.

Москва, 2024

Содержание тома

№ п.п.	Наименование	№ стр.
	Обложка	
	Титульный лист	
	Содержание тома	2
	Текстовая часть	
	а) Характеристика земельного участка, предоставленного для размещения объекта капитального строительства	3
	б) Обоснование границ санитарно-защитных зон объектов капитального строительства в пределах границ земельного участка	4
	в) Обоснование планировочной организации земельного участка в соответствии с градостроительным и техническим регламентами либо документами об использовании земельного участка	4
	г) Техничко-экономические показатели земельного участка, предоставленного для размещения объекта капитального строительства	4-5
	д) Обоснование решений по инженерной подготовке территории, в том числе решений по инженерной защите территории и объектов капитального строительства от последствий опасных геологических процессов, паводковых, поверхностных и грунтовых вод	5
	е) Описание организации рельефа вертикальной планировкой	6
	ж) Описание решений по благоустройству территории	6
	и) Обоснование схем транспортных коммуникаций, обеспечивающих внешний и внутренний подъезд к объекту капитального строительства	6-11
	Графическая часть	
1	Ситуационный план. М1:2000	12
2	Схема планировочной организации земельного участка. М1:500	13
3	План организации рельефа. М1:500	14
4	План земляных масс. М1:500	15
5	План дорожных покрытий. М1:500	16
6	Конструкции дорожных покрытий.	17
7	План благоустройства и озеленения территории. М1:500	18
8	Сводный план инженерных сетей. М1:500	19

Согласовано:

Взам. инв. №

Подпись и дата

Инв. № подл.

АА/БЭ-03-ДС3-ПЗУ

Изм.	Кол.уч	Лист	№ док.	Подпись	Дата	Схема планировочной организации земельного участка. Содержание тома			Стадия	Лист	Листов
Разработал	Кузнецова				09.09.24				П	1	1
						ООО «Артел Архитектс»					

Введение

Корректировка проектной документации объекта «Жилого комплекса» расположен по адресу: г. Москва, ЦАО, Садовническая ул., вл. 76/71. Территория состоит из участка с кадастровым номером 77:01:0002014:6383 площадью 9856 м², выполнена на основании:

- Положительного заключения экспертизы №77-2-1-3-047721-2024 от 19.08.2024 года;
- Градостроительный план земельного участка № РФ-77-4-53-3-76-2024-0641-0 от 09.02.2024 подготовленный Комитетом по архитектуре и градостроительству города Москвы.
- Инженерно-топографических планов, выполненных ГБУ «Мосгоргеотрест» по заказу № 3/5624-22 от 02.11.2022 согласованных в ГБУ «Мосгоргеотрест»;
- Технического отчета об инженерно-геологических изысканиях;
- Технических условий на подключение сетей;
- Дополнительное соглашение №3 к договору АА/БЭ-03 от 24.05.2024г.

Проектные документация разработана в соответствии с требованиями технических регламентов, а также действующих нормативных документов:

- Постановление «О составе разделов проектной документации и требованиях к их содержанию» от 16 февраля 2008 года N 87 (с изм. на 01 декабря 2021 года);
- Постановление правительства РФ от 28 мая 2021 года N 815 «Об утверждении перечня национальных стандартов и сводов правил (частей таких стандартов и сводов правил), в результате применения которых на обязательной основе обеспечивается соблюдение требований Федерального закона "Технический регламент о безопасности зданий и сооружений"».

Корректировкой проекта предусмотрено уточнение:

- Актуализирован ГПЗУ No РФ-77-4-59-3-23-2024-6611-0 от 15.08.2024 в связи с изменением площади участка и предельных максимальных параметров разрешенного строительства (уч. изм. 1.1);
- Увеличена этажность корпуса 4 с 10 до 16 этажей (уч. изм. 1.2);
- Размещено здание общественного питания для проектирования на втором этапе (уч. изм 1.3).
- Уточнены номера технических условий на сводном плане сетей (уч. изм. 1.4).

Остальные решения без изменений в соответствии с положительным заключением

Согласовано:				
Взам. инв. №				
Подпись и дата				
Инв. № подл.				

						АА/БЭ- 03-ДСЗ-ПЗУ		
Изм.	Кол.уч.	Лист	№ док.	Подпись	Дата			
	Разработал	Кузнецова			02.09.24	Схема планировочной организации земельного участка. Текстовая часть.		
						Стадия	Лист	Листов
						П	1	15
						ООО «Артел Архитекс»		

экспертизы №77-2-1-3-047721-2024 от 19.08.2024 года.

а) Характеристика земельного участка, предоставленного для размещения объекта капитального строительства

Характеристика земельного участка сохранена в соответствии с положительным заключением экспертизы №77-2-1-3-047721-2024 от 19.08.2024 года.

б) Обоснование границ санитарно-защитных зон объектов капитального строительства в пределах границ земельного участка

Обоснование границ санитарно-защитных зон объектов капитального строительства в пределах границ земельного участка в соответствии с положительным заключением экспертизы №77-2-1-3-047721-2024 от 19.08.2024 года.

в) Обоснование планировочной организации земельного участка в соответствии с градостроительным и техническим регламентами либо документами об использовании земельного участка

Проект жилого комплекса был выполнен в границах ГПЗУ № РФ-77-4-53-3-76-2024-0641-0 от 09.02.2024 площадью 9856 м2 в связи с внесением изменений в предельные максимальные параметры разрешенного строительства.

Остальные решения без изменений –в соответствии с положительным заключением экспертизы №77-2-1-3-047721-2024 от 19.08.2024 года.

г) Технико-экономические показатели земельного участка, предоставленного для размещения объекта капитального строительства.

№ п/п	Наименование	Площадь	
		м.кв.	%
	Площадь территории в границе № РФ-77-4-53-3-76-2024-0641-0 от 09.02.2024	9856	100
	Площадь застройки в т.ч. подземная часть, выходящая за абрис здания (2579.25м ² в балансе не учитывается)	7550	
1	Площадь застройки наземной части зданий (без учета консольно-выступающих частей 211 м ²), в том числе:	4759.75	56.7

Взам. инв. №	
Подпись и дата	
Инв. № подл.	

Изм.	Кол.уч	Лист	№	Подп.	Дата

2	Площадь покрытий, в т.ч.:	2662	31.7
	- покрытие проездов (13 м ² под консольно-выступающими частями здания)	30	
	- покрытие тротуаров с возможностью проезда (27 м ² под консольно-выступающими частями здания)	2006	
	- покрытие тротуаров (171 м ² под консольно-выступающими частями здания)	513	
	- покрытие спортивной, детской площадок	113	
3	Площадь озеленения территории (в т.ч. газонная отмостка 167 м ²)	969.25	11.6
4	Площадь участка 2 этапа	1 465	
	Площадь территории благоустройства за границами ГПЗУ	48	
1	Площадь покрытий проездов	48	

Предельные максимальные параметры разрешенного строительства, установленные градостроительным регламентом для участка **ГПЗУ № РФ-77-4-53-3-76-2024-0641-0** от **09.02.2024:**

№	Наименование	Показатели по ГПЗУ № РФ-77-4-53-3-76-2024-0641-0	Показатели по проекту корректировки
1	Предельная высота, м	59	56.4 (см. том АР 2)
2	Суммарная поэтажная площадь объекта в габаритах наружных стен, кв. м, в т.ч:	31539	30765
	площадь квартир для городских нужд	не менее 5839	не менее 5839

Остальные технико-экономические показатели без изменений в соответствии с положительным заключением экспертизы №77-2-1-3-047721-2024 от 19.08.2024 года.

д) Обоснование решений по инженерной подготовке территории, в том числе решений по инженерной защите территории и объектов капитального строительства от последствий опасных геологических процессов, паводковых, поверхностных и грунтовых вод

Решения по инженерной подготовке территории сохранены в соответствии с положительным заключением экспертизы №77-2-1-3-047721-2024 от 19.08.2024 года.

Взам. инв. №

Подпись и дата

Инв. № подл.

Изм.	Кол.уч	Лист	№	Подп.	Дата

АА/БЭ- 03-ДС3-ПЗУ

Лист

3

е) Описание организации рельефа вертикальной планировкой

Основные решения по вертикальной планировке, выполненные ранее сохранены в соответствии с положительным заключением экспертизы №77-2-1-3-047721-2024 от 19.08.2024 года.

ж) Описание решений по благоустройству территории

Основные решения по благоустройству территории, выполненные ранее, сохранены в соответствии с положительным заключением экспертизы №77-2-1-3-047721-2024 от 19.08.2024 года.

и) Обоснование схем транспортных коммуникаций, обеспечивающих внешний и внутренний подъезд к объекту капитального строительства

Схемы транспортных коммуникаций, обеспечивающих внешний и внутренний подъезд к объектам, сохранены в соответствии с положительным заключением экспертизы №77-2-1-3047721-2024 от 19.08.2024 года.

Расчет обеспеченности машиномест на автостоянке изменился в связи с изменением расчетных показателей с сохранением решений по их размещению в соответствии с положительным заключением экспертизы №77-2-1-3-047721-2024 от 19.08.2024 года.015402-2022.

Расчет потребности в местах хранения автомобилей проведен на основании постановление Правительства Москвы от 23 декабря 2015 года (с изменениями на 24 декабря 2019 года) №945-ПП.

1. Расчет количества машиномест постоянного хранения для жителей дома

Расчетное количество жителей определяется в соответствии с классом жилья бизнес-класс –в соответствии с заданием на проектирование (40 м² согласно СП 42.132330 табл. 5.1 в расчете на одного человека).

Общая площадь квартир с летними помещениями составляет **22 830.33 м²**

Общее количество жителей в доме составит **22 830.33 / 40 м²/чел =571 чел.**

Количество машиномест для постоянного хранения индивидуального транспорта следует определять по формуле:

$N_{п} = N_{ф} \times КБп / 100\%$, где:

$N_{ф}$ – расчетное значение числа мест постоянного хранения автомобилей, установленного в соответствии с требованиями отраслевых документов.

Взам. инв. №	
Подпись и дата	
Инв. № подл.	

Изм.	Кол.уч	Лист	№	Подп.	Дата

АА/БЭ- 03-ДС3-ПЗУ

Лист

4

КБп – доля в % от расчетного числа мест постоянного хранения автомобилей, установленного в соответствии с требованиями отраслевых документов по стандартизации, утвержденных федеральным органом исполнительной власти, осуществляющим функции по выработке государственной политики и нормативно-правовому регулированию в сфере строительства, архитектуры, градостроительства, установленная в соответствии с положениями пункта 6.2.5 региональных нормативов градостроительного проектирования города Москвы в области транспорта, автомобильных дорог регионального или межмуниципального значения.

-уровень автомобилизации 350 машин на 1000 жителей (согласно заданию на проектирование);

$$N_{\text{ф}} = 0.35 \times 571 = 200 \text{ м/мест}$$

**Расчет балльной оценки уровня потребности
в местах постоянного хранения автомобилей, числа мест
постоянного хранения автомобилей**

N п/п	Критерий оценки потребности в местах постоянного хранения автомобилей (i)	Максимальный балл по критерию (B_i)	Показатели	Фактические значения	Весовой коэффициент к максимальному баллу по критерию i (k_i)	Расчетный балл критерия ($B_i \times k_i$)
1	2	3	4	5	6	7
1	Доступность наземного городского пассажирского транспорта (НГПТ)	5	Число остановок различных маршрутов НГПТ в пешей доступности (до 500 м)	1 и менее 1	1	5
2	Интенсивность движения НГПТ	5	Интервалы движения	Более 10-20 минут	1	5,0
3	Доступность	15	Радиус доступности	Более 700 м-не	0,25	3,75

Взам. инв. №	
Подпись и дата	
Инв. № подл.	

Изм.	Кол.уч	Лист	№	Подп.	Дата
------	--------	------	---	-------	------

АА/БЭ- 03-ДСЗ-ПЗУ

Лист

5

	станций метрополитена		станций метрополитена	более 1200 м		
4	Доступность станций железнодорожного транспорта	15	Радиус доступности станций железнодорожного транспорта	Более 700 м - не более 1200 м	0,25	3,75
5	Тип жилой застройки по уровню комфорта	20	Премиум и бизнес-класс		1	20
6	Плотность застройки в границах земельного участка	20	Более 20000 м/га		0,25	5
7	Уточняющий коэффициент урбанизации территории города Москвы при расчете числа мест постоянного хранения автомобилей	20	Т4		0,25	4
	Итоговая балльная оценка					46,5

Балльная оценка уровня потребности в местах постоянного хранения автомобилей рассчитывается по формуле:

$$B_{\Pi} = \sum_{i=1}^7 (B_i \times k_i), \text{ где:}$$

B_{Π} - балльная оценка уровня потребности в местах постоянного хранения автомобилей (баллов);

Взам. инв. №

Подпись и дата

Инв. № подл.

Изм.	Кол.уч	Лист	№	Подп.	Дата

АА/БЭ- 03-ДСЗ-ПЗУ

Лист

6

B_i - максимальный балл по критерию оценки потребности в местах постоянного хранения автомобилей i (баллов);

k_i - весовой коэффициент к максимальному баллу по критерию i .

$K_{Бп}$ - доля в % от расчетного числа мест постоянного хранения автомобилей, установленного в соответствии с требованиями отраслевых документов по стандартизации, утвержденных федеральным органом исполнительной власти, осуществляющим функции по выработке государственной политики и нормативно-правовому регулированию в сфере строительства, архитектуры, градостроительства, установленная в соответствии с положениями пункта 6.2.5 региональных нормативов градостроительного проектирования города Москвы в области транспорта, автомобильных дорог регионального или межмуниципального значения.

Согласно п. 6.2.5: Балльная оценка уровня потребности в местах постоянного хранения автомобилей составляет значение от 10 до 50 баллов включительно, число мест постоянного хранения автомобилей должно быть не менее 50% от расчетного значения аналогичного показателя, установленного в соответствии с требованиями отраслевых документов по стандартизации, утвержденных федеральным органом исполнительной власти, осуществляющим функции по выработке государственной политики и нормативно-правовому регулированию в сфере строительства, архитектуры, градостроительства

Таким образом, так как расчетный бал равен 46.5, то:

$$K_{Бп} = 50\%$$

Количество машиномест для постоянного хранения индивидуального транспорта по расчету:

$$N_{п} = 200 \text{ м/мест} \times 50\%/100\% = 100 \text{ м/м.}$$

Расчет количества машиномест для временного хранения индивидуального транспорта посетителей жилых зон (гостевые стоянки).

В соответствии с п. 6.2.11 гостевые парковки следует предусматривать в количестве 10% от расчетного числа машино-мест для постоянного хранения ($N_{ф}$).

Формула для расчета:

$$N_{г} = N_{ф} \times 10\%, \text{ где:}$$

$N_{ф}$ – расчетное значение числа мест постоянного хранения для жителей дома.

$N_{г}$ - количество машиномест для временного хранения индивидуального транспорта (гостевые).

Взам. инв. №	
Подпись и дата	
Инв. № подл.	

Изм.	Кол.уч	Лист	№	Подп.	Дата

$$N_{\Gamma} = 0,1 \times N_{\Phi} = 0,1 \times 200 = 20 \text{ м/м}$$

Расчет количества машиномест временного хранения для посетителей и работников ПОН.

В соответствии с приложением 1 для объектов делового управления (размещение объектов капитального строительства с целью: размещения органов управления производством, торговлей, банковской, страховой деятельностью, а также иной управленческой деятельностью, не связанной с государственным или муниципальным управлением), необходимо предусмотреть 1 машиноместо на 60 м² общей площади. Общая площадь помещений ПОН составляет 329.76 м²

Количество м/м для ПОН определяется по формуле:

$$N_{\text{в}} = S/S_2 \cdot K_3 \cdot K_2$$

$$K_3 = 0.7 - \text{зона Т4}$$

$$N_{\text{в}} = 329.76 \text{ м}^2 / 60 \text{ м}^2 \cdot 0.7 \cdot 0.85 = 4 \text{ м/м}$$

Расчет количества машиномест для МГН:

Машиноместа для МГН определяются согласно СП 59.13330.2020 п. 5.2.1.

$$24 \cdot 10\% = 3 \text{ м/м для МГН (из них 1 м/м для М4).}$$

Количество машиномест на застройку

Машиноместа	По расчету		В границах ГПЗУ	
	Было	Стало	Подземный гараж	Открытая автостоянка
Постоянного хранения	84	100	210	-
Временного	21	24	24	-

Взам. инв. №	
Подпись и дата	
Инв. № подл.	

Изм.	Кол.уч	Лист	№	Подп.	Дата

АА/БЭ- 03-ДСЗ-ПЗУ

Лист

8

хранения (гостевого)	(из них 2 м/м для МГН (в т.ч.1 м/м для М4)	(из них 3 м/м для МГН (в т.ч.1 м/м для М4)	(из них 3 м/м для МГН (в т.ч.1 м/м для М4)	
-------------------------	--	---	---	--

Количество необходимых машиномест:

Проектом предусмотрено размещение 234 м/м из них: в подземной автостоянке – 234 м/м (в т.ч. 3 м/м для МГН, из них 1 для МГН М4).

Взам. инв. №	
Подпись и дата	
Инв. № подл.	

Изм.	Кол.уч	Лист	№	Подп.	Дата

АА/БЭ- 03-ДСЗ-ПЗУ

Лист

9

Условные обозначения



- граница 1 этапа проектирования по ГПЗУ № РФ-77-4-53-3-76-2024-0641-0 от 09.02.2024
- граница благоустройства за границами проектируемого участка
- проектируемая подземная автостоянка
- проектируемое здание
- нависающая часть здания
- реконструируемое здание
- проектируемое здание 2 этап
- сносимые здания
- проектируемый газон
- проектируемый проезд
- проектируемые тротуары (в т.ч. с возможностью проезда спецтехники)
- проектируемые площадки
- скрытая отмотска
- въезд-выезд в подземный паркинг
- въезд-выезд на территорию пожарных машин и спецтехники
- проектируемое ограждение
- проектируемые ворота/калитка
- проектируемая подпорная стенка
- границы береговых полос.
- границы территории улично-дорожной сети
- границы охранных зон памятников истории и культуры.
- номера регламентных участков
- индекс режимов
- зоны возможного размещения объектов капитального строительства в границах регламентного участка
- объекты современного строительства
- объекты историко-градостроительной среды
- границы корректировки

Экспликация зданий и сооружений

No п/п	Наименование	Примечание
Здания и сооружения		
1	Корпус №1	Проектируемый
2	Корпус №2	Проектируемый
3	Корпус №3	Проектируемый
4	Корпус №3.1	Проектируемый
5	Корпус №4	Проектируемый
6	Въезд/выезд в подземную автостоянку (рампа)	Проектируемый
7	Детская площадка	Проектируемая
8	Спортивная площадка	Проектируемая
9	Площадка для отдыха	Проектируемая
10	Жилой дом	Существующий
11	Административно здание	Существующее
12	Трансформаторная подстанция	Существующая
13	Предприятие общественного питания	Проектируемое (2 этап)
14	Школа	Существующая



Садовническая ул., д. 76/71, стр 1 (часть 1) 1(1) сохранение архитектурно-художественной композиции и восстановление утраченных элементов декора ценного восточного фасада.

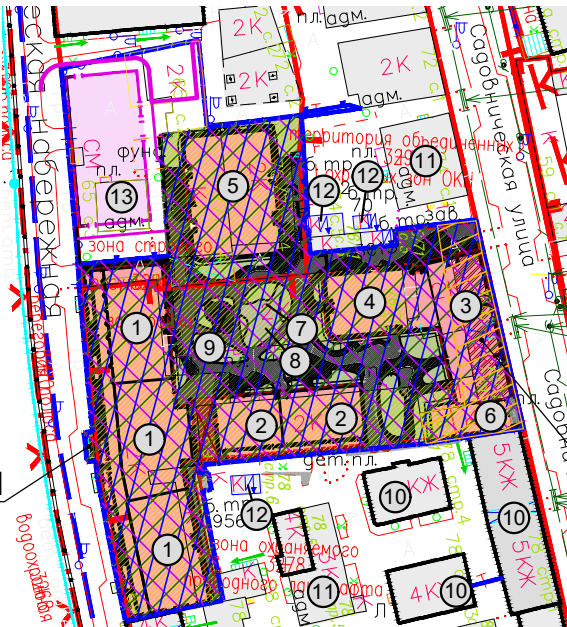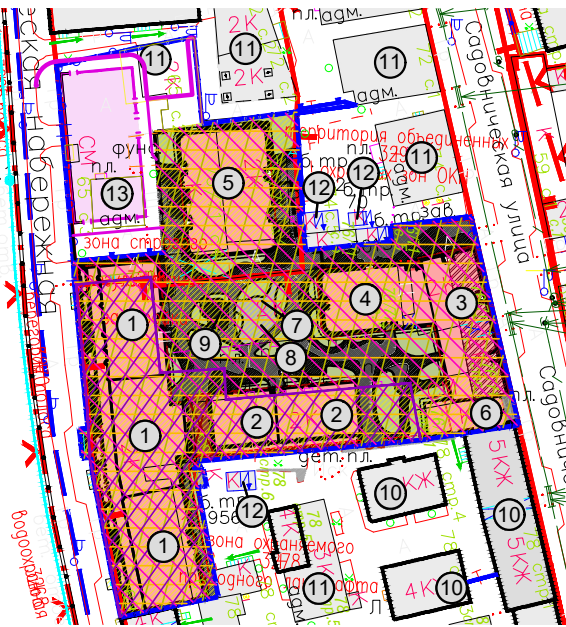

- Территория зоны сильного подтопления
 - Территории зоны строгого регулирования застройки и зоны охраняемого ландшафта
 - Территория культурного слоя "Садовнических слобод" XVI-XVII вв. н.э. (достопримечательное место)
 - Объект историко-градостроительной среды
- Территория зоны регулирования застройки
 - Территория культурного слоя (достопримечательное место)
 - Территория зоны охраняемого культурного слоя
 - Территория части земельного участка, расположенная в границах охранной зоны объектов культурного наследия (памятников истории и культуры)


1. Часть земельного участка №1, площадью 63 кв.м, расположена в границах красных линий улично-дорожной сети.
2. Часть земельного участка №2, площадью 800 кв. м, расположена в границах охранной зоны объектов культурного наследия (памятников истории и культуры) № 84.

0.000=123.20


АА/БЭ-03-ДС3-ПЗУ

"Жилой комплекс", расположенный по адресу:
г. Москва, ЦАО, Садовническая ул.,вл 76/71

						АА/БЭ-03-ДСЗ-ПЗУ			
1	2					"Жилой комплекс", расположенный по адресу: г. Москва, ЦАО, Садовническая ул.,вл 76/71			
Изм	Колуч	Лист	Недок	Подпись	Дата	Схема планировочной организации земельного участка	Стадия	Лист	Листов
							П	1	
Разработал	Кузнецова				09.24	Ситуационный план. М 1:2000			
Рук. отдела	Кузнецова				09.24				
ГАП	Добрякова				09.24				
Н. контр	Кузнецова				09.24				

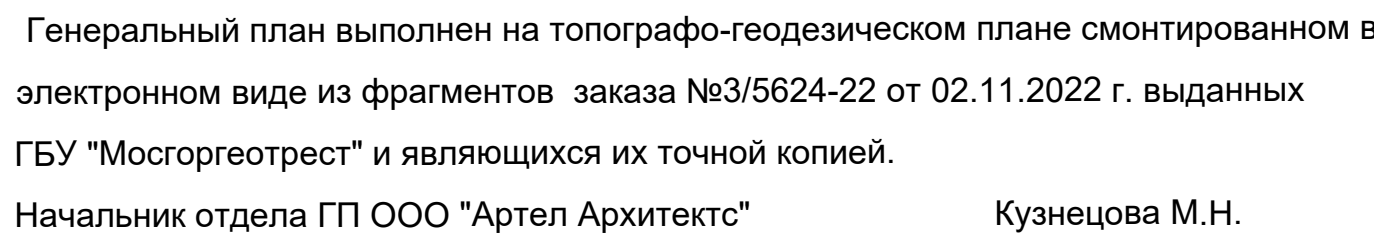

1	2
3	4

 Условные обозначения	
	- граница 1 этапа проектирования по ГПЗУ № РФ-77-4-53-3-76-2024-0641-0 от 09.02.2024
	- граница благоустройства за границами проектируемого участка
	- проектируемая подземная автостоянка
	- проектируемое здание
	- нависающая часть здания
	- реконструируемое здание
	- проектируемое здание 2 этап
	- сносимые здания
	- проектируемый газон
	- проектируемый проезд
	- проектируемые тротуары (в т.ч. с возможностью проезда спецтехники)
	- проектируемые площадки
	- скрытая отмостка
	- въезд-выезд в подземный паркинг
	- вход в жилые помещения
	- въезд-выезд на территорию пожарных машин и спецтехники
	- проектируемое ограждение
	- проектируемые ворота/калитка
	- проектируемая подпорная стенка
	- направление движения пожарных машин
	- направление движения транспорта
	- проектируемый водоотводной лоток
	- проектируемый пескоуловитель
	- номера регламентных участков
	- индекс режимов
	- зоны возможного размещения объектов капитального строительства в границах регламентного участка
	- границы корректировки

ЛИНИИ ГРАДОСТРОИТЕЛЬНОГО РЕГУЛИРОВАНИЯ НАНЕСЕНЫ ПО СОСТОЯНИЮ НА 20.10.22

ПРОЕКТИРОВАНИЕ ВЫПОЛНИТЬ В УВЯЗКЕ С СУЩЕСТВУЮЩИМИ ОТМЕТКАМИ

По вопросам несоответствия планового положения подземных коммуникаций обращаться по тел. (499)257-09-11 (доб.51-43)


М 1:500, высота сечения рельефа 0.5м

В ГОЛУБЫХ ГРАНИЦАХ НАНЕСЕНА ГРАНИЦА УЧАСТКА ПО ДАННЫМ МАТЕРИАЛАМ ПРЕДОСТАВЛЕННЫМ ЗАКАЗЧИКОМ. ДАННЫЙ МАТЕРИАЛ НЕ МОЖЕТ БЫТЬ ИСПОЛЬЗОВАН ДЛЯ РЕГИСТРАЦИИ ПРАВ СОБСТВЕННОСТИ.

					3/5624-22 - ИГДИ-Г				
Изм.	Коп. уч.	Лист	№ док.	Подпись	Дата	Наименование объекта: Жилой комплекс			
Разработан									
Полевые работы	Семенова А. А.				02.11.22	Заказчик: ООО "Балчуг Эстейт"			
Камерал. работы	Воронова О. А.				02.11.22	Местоположение (адрес) объекта: г. Москва, Садовническая площадь, 79/71			
Подзем. работы	Сидова А. М.				02.11.22	И			
Коррект. топогр.	Кортузова С. В.				02.11.22	3			
Коррект. подзем.	Рыжкова Л. А.				02.11.22	Листов			
ЛПР (к.пр.)	Черепанова Е. А.				02.11.22	ИНЖЕНЕРНО-ТОПОГРАФИЧЕСКИЙ ПЛАН (М 1:500)			
Дубликат. работ	Петрунина М. Д.				02.11.22	МОСКОВСКАЯ АРХИТЕКТУРА © ГБУ "Мосгоргеопротект"			

					3/5624-22 - ИГДМ-Г			
Изм.	Кол.ч.	Лист	№ док.	Подпись	Дата	Наименование объекта: Жилой комплекс		
Разработан						Заказчик: ООО "Балчуг Эстейт"		
Полевые работы Семенова А. А.						02.11.22		
Камерал. работы Воронкова О. А.						02.11.22	Местоположение (адрес) объекта: г. Москва, Садовническая ул. 76/1	
Подзем. работы Седова А. М.						02.11.22	Стадия	Лист
Корр.к. топогр. Коргулова С. В.							И	4
Корр.к. подзем. Рахимова Л. А.						02.11.22	Номенклатура: А-VIII-10-01	
ЛПР (Кр. лин.) Чернышова Е. А.						02.11.22	ИНЖЕНЕРНО-ТОПОГРАФИЧЕСКИЙ ПЛАН (М 1:500)	
Дубинчат. кр. оп. Петрушина М. Д.						02.11.22		
						МОСКОВСКАЯ АРХИТЕКТУРА © ГБУ "Мосгоргеопроект"		

Формат A1

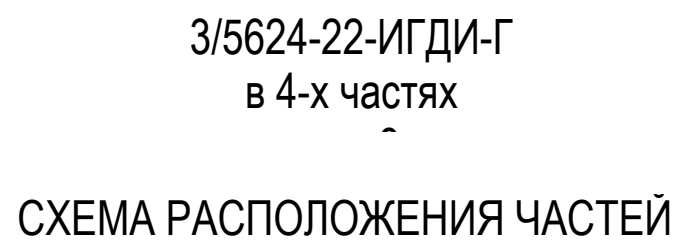

ЛИНИИ ГРАДОСТРОИТЕЛЬНОГО РЕГУЛИРОВАНИЯ НАНЕСЕНЫ ПО СОСТОЯНИЮ
НА 20.10.22

ПРОЕКТИРОВАНИЕ ВЫПОЛНИТЬ В УВЯЗКЕ С СУЩЕСТВУЮЩИМИ ОТМЕТКАМИ

По вопросам несоответствия планового положения подземных коммуникаций
обращаться по тел. (499)267-09-11 (доб.51-43)

М 1:500, высота сечения рельефа 0.5м

В ГОЛУБЫХ ГРАНИЦАХ НАНЕСЕНА ГРАНИЦА УЧАСТКА ПО ДАННЫМ МАТЕРИАЛАМ ПРЕДОСТАВЛЕННЫМ ЗАКАЗЧИКОМ. ДАННЫЙ МАТЕРИАЛ НЕ МОЖЕТ БЫТЬ ИСПОЛЬЗОВАН ДЛЯ РЕГИСТРАЦИИ ПРАВ СОБСТВЕННОСТИ.

система координат: Московская; система высот: Московская

						3/6/24-22 - ИГД Г			
Имя	Кол-во	Лист	№ док.	Подпись	Дата	Наименование объекта: Жилой комплекс			
Разработчик									
Полное наименование	Степанов А. А.				02.11.22	Заказчик: ООО "Балтэк Эстейт"			
Кампарт. работ	Степанов А. А.				02.11.22	Исполнитель (дизайн) объекта : Москва, Садовническая			
Полное наименование	Степанов А. А.				02.11.22	Стадия	Лист	Листов	
Кампарт. работ	Степанов А. А.				02.11.22	Имя: 7071	И	1	4
Корр.конт.	топографические С.В.				02.11.22	Инженерный: А.Х-03-05			
Корр.конт.	подземные Л.А.				02.11.22				
ГР (Кр.лик.)	Чарникова Е. А.				02.11.22	ИНЖЕНЕРНО-ТОПОГРАФИЧЕСКИЙ ПЛАН (М 1:500)			
Дубликат	от опл.	Петрушина М.Д.			02.11.22	МОСКМАРХИТЕКТУРА © ГБУ "Мосгоргеоцентр"			
						3/6/24-22 - ИГД Г			
Имя	Кол-во	Лист	№ док.	Подпись	Дата	Наименование объекта: Жилой комплекс			
Разработчик									
Полное наименование	Степанов А. А.				02.11.22	Заказчик: ООО "Балтэк Эстейт"			
Кампарт. работ	Степанов А. А.				02.11.22	Исполнитель (дизайн) объекта : Москва, Садовническая			
Полное наименование	Степанов А. А.				02.11.22	Имя: 7071			
Корр.конт.	топографические С.В.				02.11.22	Инженерный: А.Х-03-05			
Корр.конт.	подземные Л.А.				02.11.22				
ГР (Кр.лик.)	Чарникова Е. А.				02.11.22	ИНЖЕНЕРНО-ТОПОГРАФИЧЕСКИЙ ПЛАН (М 1:500)			
Дубликат	от опл.	Петрушина М.Д.			02.11.22	МОСКМАРХИТЕКТУРА © ГБУ "Мосгоргеоцентр"			

					3/5624-22 - ИГДАГ				
Изм.	Копул.	Лист	№ докум.	Подпись	Дата	Наименование объекта: Жилой комплекс			
Разработал									
Получил работу <i>Свиридов А. А.</i>						02.11.22	Знаком: ООО "Тангус Эстейт"		
Камерар. работ <i>Свиридов А. А.</i>						02.11.22	Исполнительное задание: Москва, Саднинская ул. 70/1		
Получил работу <i>Свиридов А. А.</i>						02.11.22	Страница	Лист	Листов
Корркт. пометки <i>Свиридов С. В.</i>						02.11.22	И	2	4
Корркт. пометки <i>Литвинов А. И.</i>						02.11.22	Комментарий: А-В-15-13		
ПТР (по вкл.) <i>Черепанов Е. Д.</i>						02.11.22	ИНЖЕНЕРНО-ТОПОГРАФИЧЕСКИЙ ПЛАН (М 1:500)		
Добавил в от. <i>Литвинов М. Д.</i>						02.11.22			
					3/5624-22 - ИГДАГ				
Изм.	Копул.	Лист	№ докум.	Подпись	Дата	Наименование объекта: Жилой комплекс			
Разработал									
Получил работу <i>Свиридов А. А.</i>						02.11.22	Знаком: ООО "Тангус Эстейт"		
Камерар. работ <i>Свиридов А. А.</i>						02.11.22	Исполнительное задание: Москва, Саднинская ул. 70/1		
Получил работу <i>Свиридов А. А.</i>						02.11.22	Страница	Лист	Листов
Корркт. пометки <i>Свиридов С. В.</i>						02.11.22	И	4	4
Корркт. пометки <i>Литвинов А. И.</i>						02.11.22	Комментарий: А-В-10-01		
ПТР (по вкл.) <i>Черепанов Е. Д.</i>						02.11.22	ИНЖЕНЕРНО-ТОПОГРАФИЧЕСКИЙ ПЛАН (М 1:500)		
Добавил в от. <i>Литвинов М. Д.</i>						02.11.22			
					3/5624-22 - ИГДАГ				
Изм.	Копул.	Лист	№ докум.	Подпись	Дата	Наименование объекта: Жилой комплекс			
Разработал									
Получил работу <i>Свиридов А. А.</i>						02.11.22	Знаком: ООО "Тангус Эстейт"		
Камерар. работ <i>Свиридов А. А.</i>						02.11.22	Исполнительное задание: Москва, Саднинская ул. 70/1		
Получил работу <i>Свиридов А. А.</i>						02.11.22	Страница	Лист	Листов
Корркт. пометки <i>Свиридов С. В.</i>						02.11.22	И	4	4
Корркт. пометки <i>Литвинов А. И.</i>						02.11.22	Комментарий: А-В-10-01		
ПТР (по вкл.) <i>Черепанов Е. Д.</i>						02.11.22	ИНЖЕНЕРНО-ТОПОГРАФИЧЕСКИЙ ПЛАН (М 1:500)		
Добавил в от. <i>Литвинов М. Д.</i>						02.11.22			

Бедомость водотводных сооружений						
Вид сооружения	Координата оси или номер сооружения	Координата (пикетаж)		Длина, шт.	Тип укрепления или конструкция	Примечание
		начала	конца			
Решетка водоприемная Drive RB-20 25.50 щелевая ВЧ С250, арт.253033-D		1		368	чугунная	000 "Standardpark"
Лоток водотводный BetonMax Drive LB-V 20.26.31-F-3-K23 арт.45076/23-23				88	Бетон	000 "Standardpark"
Лоток водотводный ScomPrax Drive LB-V 20.26.31-F-3-Y20 с уклоном арт.75076/20	2		1	Полимербетонный		000 "Standardpark"
Лоток водотводный ScomPrax Drive LB-V 20.26.31-F-3-Y19 с уклоном арт.75076/19	3		1	Полимербетонный		000 "Standardpark"
Лоток водотводный ScomPrax Drive LB-V 20.26.31-F-3-Y18 с уклоном арт.75076/18	4		1	Полимербетонный		000 "Standardpark"
Лоток водотводный ScomPrax Drive LB-V 20.26.31-F-3-Y17с уклоном арт.75076/17	5		1	Полимербетонный		000 "Standardpark"
Лоток водотводный ScomPrax Drive LB-V 20.26.31-F-3-Y16 с уклоном арт.75076/16	6		1	Полимербетонный		000 "Standardpark"
Лоток водотводный ScomPrax Drive LB-V 20.26.31-F-3-Y15 с уклоном арт.75076/15	7		1	Полимербетонный		000 "Standardpark"
Лоток водотводный ScomPrax Drive LB-V 20.26.31-F-3-Y14 с уклоном арт.75076/14	8		1	Полимербетонный		000 "Standardpark"
Лоток водотводный ScomPrax Drive LB-V 20.26.31-F-3-Y13 с уклоном арт.75076/13	9		1	Полимербетонный		000 "Standardpark"
Лоток водотводный ScomPrax Drive LB-V 20.26.31-F-3-Y12 полимербетонный с уклоном арт.75076/12	10		1	Полимербетонный		000 "Standardpark"
Лоток водотводный ScomPrax Drive LB-V 20.26.31-F-3-Y11 с уклоном арт.75076/11	11		1	Полимербетонный		000 "Standardpark"
Лоток водотводный ScomPrax Drive LB-V 20.26.31-F-3-Y10 с уклоном арт.75076/10	12		1	Полимербетонный		000 "Standardpark"
Лоток водотводный ScomPrax Drive LB-V 20.26.31-F-3-Y9 с уклоном арт.75076/9	13		1	Полимербетонный		000 "Standardpark"
Лоток водотводный ScomPrax Drive LB-V 20.26.31-F-3-Y8 с уклоном арт.75076/8	14		1	Полимербетонный		000 "Standardpark"
Лоток водотводный ScomPrax Drive LB-V 20.26.31-F-3-Y7 с уклоном арт.75076/7	15		1	Полимербетонный		000 "Standardpark"
Лоток водотводный ScomPrax Drive LB-V 20.26.31-F-3-Y6 с уклоном арт.75076/6	16		1	Полимербетонный		000 "Standardpark"
Лоток водотводный ScomPrax Drive LB-V 20.26.31-F-3-Y5с уклоном арт.75076/5	17		1	Полимербетонный		000 "Standardpark"
Лоток водотводный ScomPrax Drive LB-V 20.26.31-F-3-Y4 с уклоном арт.75076/4	18		1	Полимербетонный		000 "Standardpark"
Лоток водотводный ScomPrax Drive LB-V 20.26.31-F-3-Y3 с уклоном арт.75076/3	19		1	Полимербетонный		000 "Standardpark"
Лоток водотводный ScomPrax Drive LB-V 20.26.31-F-3-Y2 с уклоном арт.75076/2	20		1	Полимербетонный		000 "Standardpark"
Лоток водотводный ScomPrax Drive LB-V 20.26.31-F-3-Y1 с уклоном арт.75076/1	21		1	Полимербетонный		000 "Standardpark"
Лоток водотводный ScomPrax Drive LB-V 20.26.41-F1-3-K10 арт.75676/10-10	22		49	Полимербетонный		000 "Standardpark"
Лоток водотводный ScomPrax Drive LB-V 20.26.41-50-П-K10 для Т-и I -образного подпоясания арт.75671.050/10-10	23		4	Полимербетонный		000 "Standardpark"
Лоток водотводный ScomPrax Drive LB-V 20.26.26-F1 арт.7557-V1			9	Полимербетонный		000 "Standardpark"
Лоток водотводный ScomPrax Drive LB-V 20.26.21-F1-3 арт.75476V			21	Полимербетонный		000 "Standardpark"
Пескоуловитель секционный BetonMax ТУС-30.39.95-В-Б (бетонная (верхняя часть) арт.4780/1			5	Бетон	000 "Standardpark"	
Пескоуловитель секционный BetonMax ТУС-30.39.95-В-Н (бетонная (нижняя часть) арт.4780/3			5	Бетон	000 "Standardpark"	
Корниз для пескоуловителя КОТТ-20.39.95-ОС оцинкованная сталь арт.61798			5	Оцинкованная сталь	000 "Standardpark"	
Насадка НЩ-20.24.100-ОС-3-ТИП2-Т-1 00 щелевая Т-образная стальная оцинкованная С250 арт.2517-3-2Т-100-D			9	Оцинкованная сталь	000 "Standardpark"	
Насадка НЩР-20.24.50-ОС-3-ТИП2-Т-100 щелевая резиновая Т-образная стальная оцинкованная С250 арт.25175-3-2Т-100-D			1	Оцинкованная сталь	000 "Standardpark"	

Примечания:

1. Привязку лотков уточнить по месту.
2. Набор элементов водоотводных лотков и их монтаж выполнять с представителями фирмы ООО "Standartpark".

Экспликация зданий и сооружений		
No п/п	Наименование	Примечание
Здания и сооружения		
1	Корпус №1	Проектируемый
2	Корпус №2	Проектируемый
3	Корпус №3	Проектируемый
4	Корпус №3.1	Проектируемый
5	Корпус №4	Проектируемый
6	Въезд/выезд в подземную автостоянку (рампа)	Проектируемый
7	Детская площадка	Проектируемая
8	Спортивная площадка	Проектируемая
9	Площадка для отдыха	Проектируемая



Условные обозначения

- граница 1 этапа проектирования по ГПЗУ №
РФ-77-4-53-3-76-2024-0641-0 от 09.02.2024
- - граница благоустройства за границами
проектируемого участка
- - проектируемая подземная автостоянка
- - проектируемое здание
- - нависающая часть здания
- - реконструируемое здание
- - проектируемое ограждение
- - проектируемые ворота/калитка
- - проектируемая подпорная стенка
- - отметка чистого пола секций
- - проектируемые горизонтали
- проектный уклон %
расстояние, м
- переломная точка с проектной высотой
отметкой
- - отметка входа
- - проектируемый водосточный лоток
- - проектируемый пескоуловитель
- - границы корректировки

Генеральный план выполнен на топографо-геодезическом плане смонтированном в электронном виде из фрагментов заказа №3/5624-22 от 02.11.2022 г. выданных ГУП "Мосгортрест" и являющихся их точной копией.

Начальник отдела ГП ООО "Артел Архитектс" Кузнецова М.Н.

						0.000=123.20		
						AA/БЗ-03-ДС3-ПЗУ		
						"Жилой комплекс", расположенный по адресу: г. Москва, ЦАО, Сокольническая ул. в/п 76/17		
	1	2						
Имя	Колуч	Лист	Надх	Полнрв	Дата			
						Схема планировочной организации земельного участка		
						Стадия	Лист	Листов
							П	3
						План организации рельефа. М 1:500 А Б В Г Д Е		

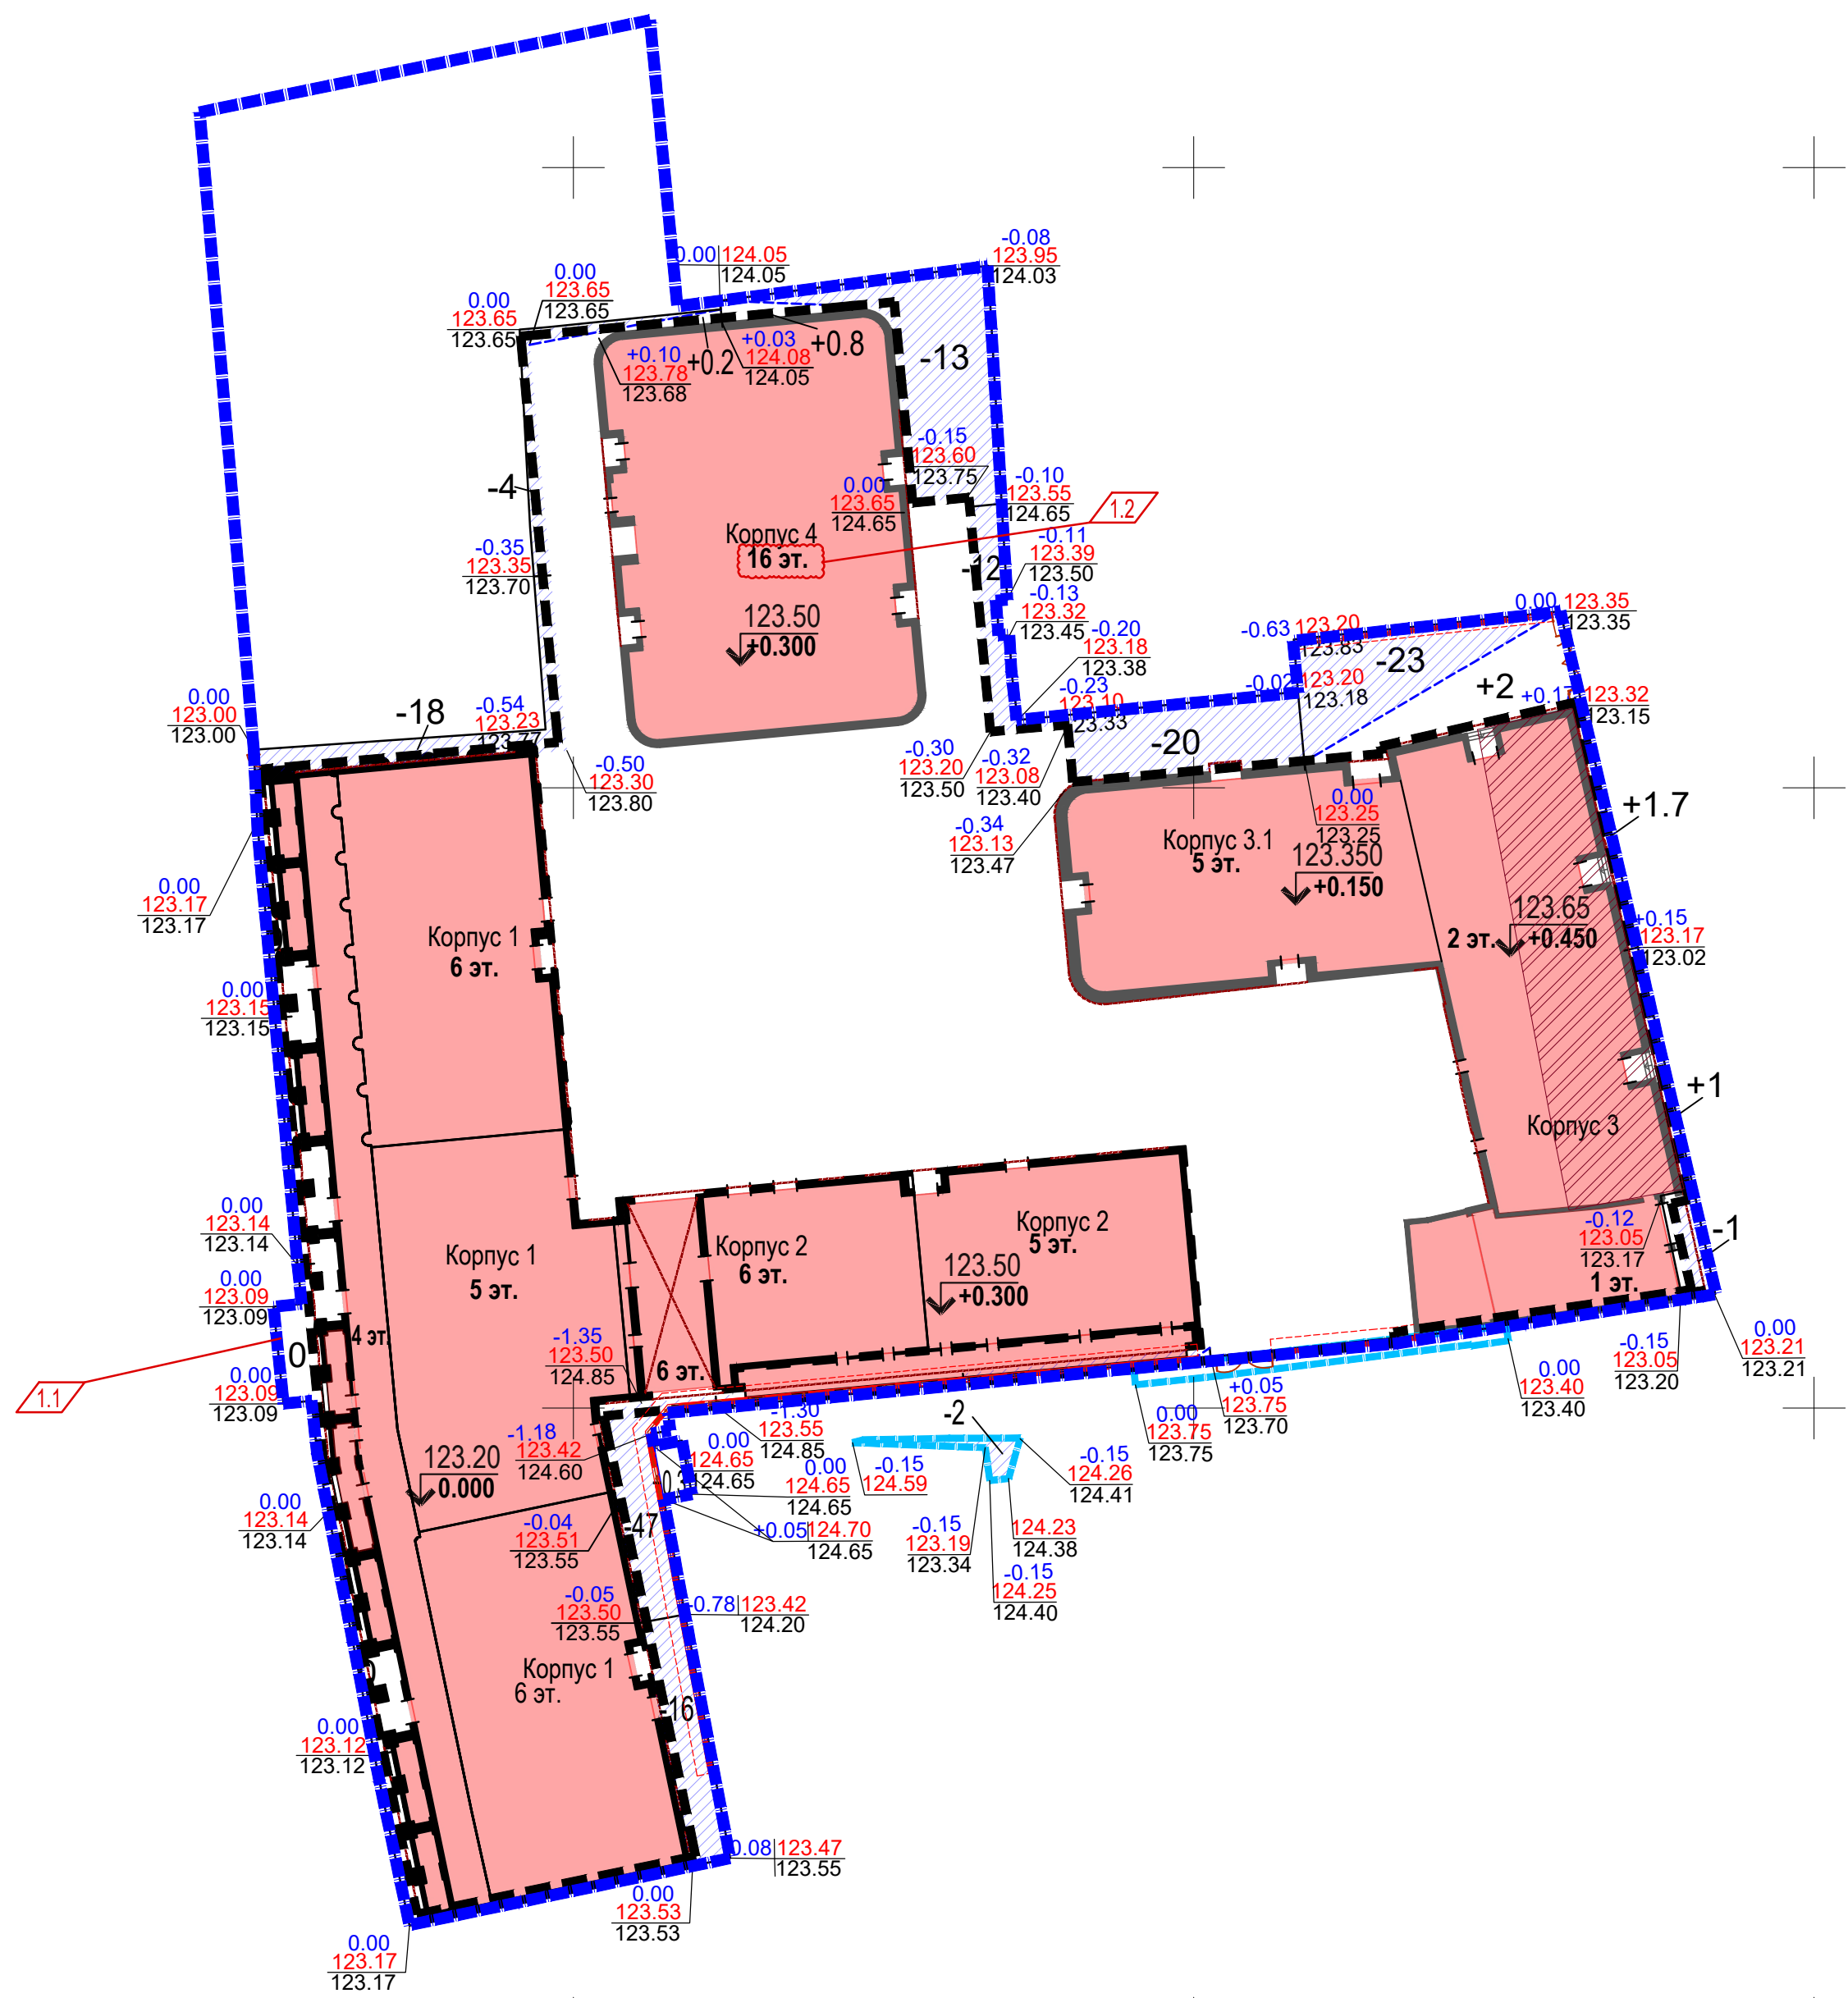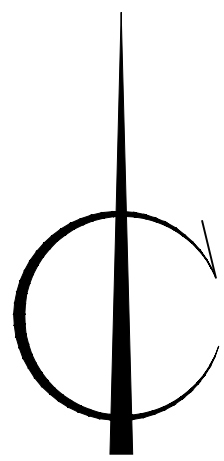

Итого, м3	Насыпь (+)	+0.3	+1	-	+4.7	Всего, м3	+6
	Выемка (-)	-85	-29	-20	-24		-158

Ведомость объемов земляных масс

Наименование грунта	Количество, м³		Примечание
	Насыпь (+)	Выемка (-)	
1. Грунт планировки территории	6	158	
2. Вытесненный грунт, в т.ч. при устройстве:		655	
а) автодорожных покрытий:		625	
покрытие проезда Тип 1, h=0.84 м		(25)	
покрытие тротуара с возможностью проезда Тип 2, 3 h=0.86 м		(429)	
покрытие тротуара Тип 4, 5, 6 h=0.83 м		(162)	
- покрытие газонной отмости Тип 8, h=0.35 м		(7)	
б) плодородной почвы на участках озеленения в т.ч.:		31	
- покрытие газона, h=0.20 м		(18)	
- покрытие цветника, h=0.40 м		(12)	
3. Поправка на уплотнение 10 %	1		
4. Грунт чрезвычайно опасный в слое 0-1.5 м		12586.5	
Всего грунта	7	12586.5	
4. Грунт чрезвычайно опасный, полностью подлежит вывозу на полигон		12586.5	
5. Недостаток пригодного грунта		7	
6. Плодородный грунт, всего, в т.ч.:	265		
а) используемый для озеленения территории:			
- газон, h=0.20 м (в т.ч. на кровле гаража)		(153)	
- цветник, h=0.40 м (в т.ч. на кровле гаража)		(78)	
- скрытая отмостка , h=0.20 м (в т.ч. на кровле гаража)		(33)	
б) недостаток плодородного грунта		265	
7. Итого перерабатываемого грунта	12858	12858	

Примечание:


- Объем грунта посчитан без учета грунта, вытесненного подземными частями зданий, сооружений, а так же инженерными сетями (объемы учтены в соответствующих разделах КР и ПОС).
- Согласно тому инженерно-экологических изысканий Б1166/ОР-22-ИЭИ территория участка в границах ГПЗУ является чрезвычайно опасной по загрязнению 3, 4-бензапирена в слое 0-1.5 м- подлежит вывозу и утилизации на специализированные полигоны в объеме **12586.5 м³ (8391м²x1.5м)**

Условные обозначения

- граница проектируемого участка по ГПЗУ № РФ-77-4-53-3-76-2024-0641-0 от 09.02.2024
- граница благоустройства за границами проектируемого участка
- проектируемая подземная автостоянка
- проектируемое здание
- нависающая часть здания
- реконструируемое здание
- проектируемое ограждение
- проектируемые ворота/калитка
- проектируемая подпорная стенка
- рабочая отметка красная (проектная) отметка черная (сущ.) отметка
- объем насыпи/ выемки, м³
- нулевая линия
- объем выемки, м³
- границы корректировки

0.000=123.20

						АА/БЭ-03-ДС3-ПЗУ			
						"Жилой комплекс", расположенный по адресу: г. Москва, ЦАО, Садовническая ул., вл 76/71			
1	2					Схема планировочной организации земельного участка	Стадия	Лист	Листов
Изм.	Кол.уч.	Лист	Недок.	Подпись	Дата		П	4	
Разработал	Кузнецова				08.24	План земляных масс. М 1:500			
Рук. отдела	Кузнецова				08.24				
ГАП	Добрякова				08.24				
Н. контр.	Кузнецова				08.24				

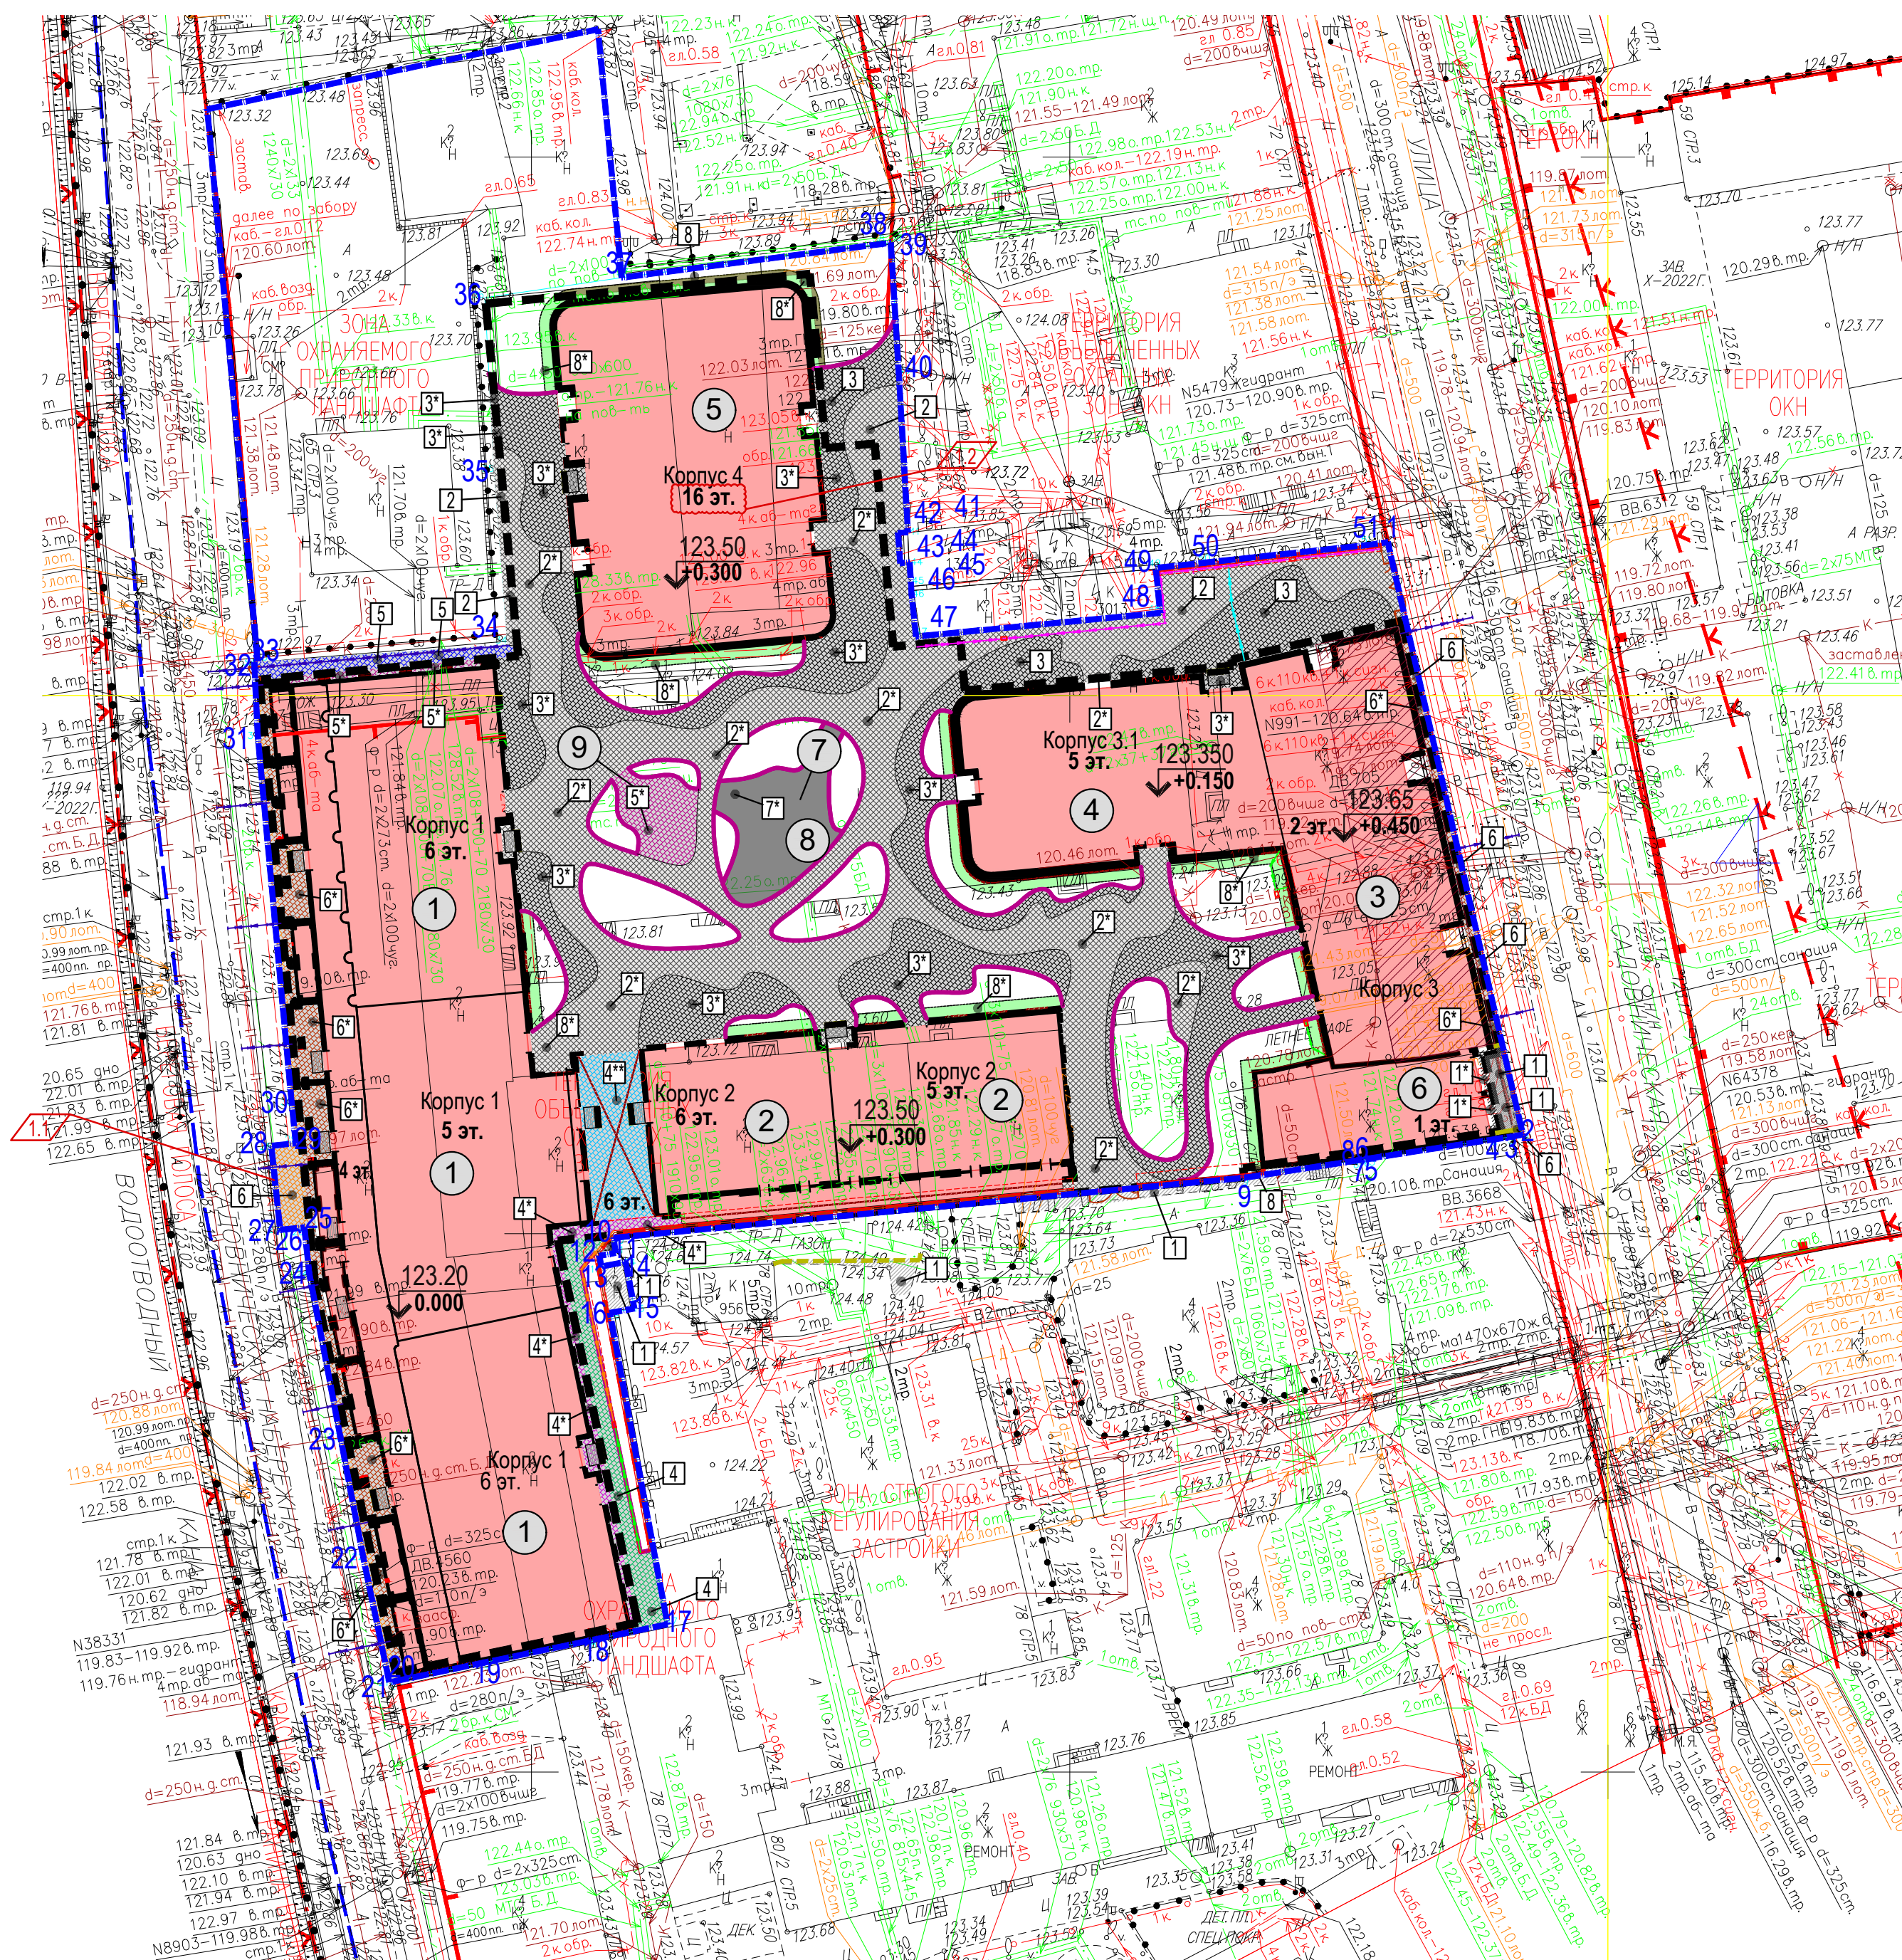

Условные обозначения

-  - граница 1 этапа проектирования по ГПЗУ
 РФ-77-4-53-33-76-2024-0641-0 от 09.02.2024 №
 - граница благоустройства за границами проектируемого участка
 - проектируемая подземная автостоянка
 - проектируемое здание
 - нависающая часть здания
 - реконструируемое здание
 - проектируемое ограждение
 - проектируемые ворота/калитка
 - проектируемая подпорная стенка
 - проектируемый водоотводной лоток
 - проектируемый пескоуловитель
 - границы корректировки

Экспликация зданий и сооружений

No n/n	Наименование	Примечание
Здания и сооружения		
1	Корпус №1	Проектируемый
2	Корпус №2	Проектируемый
3	Корпус №3	Проектируемый
4	Корпус №3.1	Проектируемый
5	Корпус №4	Проектируемый
6	Въезд/выезд в подземную автостоянку (рампа)	Проектируемый
7	Детская площадка	Проектируемая
8	Спортивная площадка	Проектируемая
9	Площадка для отдыха	Проектируемая



Ведомость покрытий тротуаров, дорожек и площадок

Поз.	Наименование	Тип	Площадь покрытия, м²	Примечание
------	--------------	-----	----------------------------	------------

Ведомость покрытий тротуаров, дорожек и площадок в уровне земли

1	Проезд из асфальтобетона	1	25	
2	Тротуар с покрытием из плитки с возможностью проезда пожарной техники, вид 1	2	234	
3	Тротуар с покрытием из плитки с возможностью проезда пожарной техники, вид 2	3	265	
4	Тротуар с покрытием из плитки, вид 1	4	72	
5	Тротуар с покрытием из плитки, вид 2	5	33	
6	Тротуар с покрытием из плитки, вид 3	6	90	
7	Газонная отмостка	8	21	
8	Площадь озеленения (см. совместно с листом 7)		-	

Ведомость покрытий тротуаров, дорожек и площадок на подземном гараже

  1	Проезд из асфальтобетона	1*	5	
2	Тротуар с покрытием из плитки с возможностью проезда пожарной техники, вид 1	2*	895	
3	Тротуар с покрытием из плитки с возможностью проезда пожарной техники, вид 2	3*	612	
4	Тротуар с покрытием из плитки, вид 2	5*	61	
5	Тротуар с покрытием из плитки, вид 1	4*	33	
6	Тротуар с покрытием из плитки(в арке), вид 1	4**	86.0	
7	Тротуар с покрытием из плитки, вид 3	6*	107	
8	Площадка с покрытием из полиуретана	7*	113.0	
9	Газонная отмостка	8*	146	
10	Площадь озеленения (см. совместно с листом 7)		-	

За границами ГПЗУ в границах благоустройства

1	Проезды из асфальтобетона	1	48	
	Гранитный борт ГбргП1 по ГОСТ 32018-2012 (м.пог.)		4	
	Бортовой камень БР 100.30.15 по ГОСТ 6665-91 (м.пог.)		14	
	Бортовой камень БР 100.20.08 по ГОСТ 6665-91 (м.пог.)		915	
	Тактильная плитка 500х500х60 по ГОСТ Р 52875-2018 с рифом конусы (шт.)		10	
	Грязезащитная решетка 1.0мх1.0м (шт.)		86	

Генеральный план выполнен на топографо-геодезическом плане смонтированном в электронном виде из фрагментов заказа №3/5624-22 от 02.11.2022 г. выданных ГБУ "Мосгоргеотрест" и являющихся их точной копией.

Начальник отдела ГП ООО "Артел Архитектс" Кузнецова М.Н.

0.000=123.20

						АА/БЗ-03-ДСЗ-ПЗУ			
1	2					"Жилой комплекс", расположенный по адресу: г. Москва, ЦАО, Садовническая ул. вл 76/71			
Изм	Колуч	Лист	№док	Подпись	Дата				
						Схема планировочной организации земельного участка	Стадия	Лист	Листов
							П	5	
Разработал		Кузнецова			09.24	План дорожных покрытий. М 1:500			
Рук. отдела		Кузнецова			09.24				
ГАП		Добрякова			09.24				
Н. контр.		Кузнецова			09.24				

Формат A1

3/5624-22-ИГДИ-Г
в 4-х частях

СХЕМА РАСПОЛОЖЕНИЯ ЧАСТЕЙ

1	2
3	4

ЛИНИИ ГРАДОСТРОИТЕЛЬНОГО РЕГУЛИРОВАНИЯ НАНЕСЕНЫ ПО СОСТОЯНИЮ
НА 20.10.22

ПРОЕКТИРОВАНИЕ ВЫПОЛНИТЬ В УВЯЗКЕ С СУЩЕСТВУЮЩИМИ ОТМЕТКАМИ

По вопросам несоответствия планового положения подземных коммуникаций
обращаться по тел. (499)257-09-11 (доб.51-43)

М 1:500, высота сечения рельефа 0.5м

В ГОЛУБЫХ ГРАНИЦАХ НАНЕСЕНА ГРАНИЦА УЧАСТКА ПО ДАННЫМ МАТЕРИАЛАМ ПРЕДОСТАВЛЕННЫМ ЗАКАЗЧИКОМ. ДАННЫЙ МАТЕРИАЛ НЕ МОЖЕТ БЫТЬ ИСПОЛЬЗОВАН ДЛЯ РЕГИСТРАЦИИ ПРАВ СОБСТВЕННОСТИ.

система координат: Московская; система высот: Московская

						3/5624-22 - ИГДИ-Г		
Изм.	Коп.уч.	Лист	№ док.	Подпись	Дата	Наименование объекта: Жилой комплекс		
Разработан								
Полевые работы		Семенов А. А.		02.11.22	Заказчик: ООО "Балчуг Эстейт"			
Камерал. работы		Борознова О. А.		02.11.22	Москостроение (адрес) объекта: г. Москва, Садовническая улица, 76/1			
Подзем. работы		Седова А. М.		02.11.22	Номенклатура: А/Х-9/16			
Корректи. топозем.		Христунова С. В.		02.11.22				
Корректи. подзем.		Ахьялова Л. А.		02.11.22				
П/Р (Кр.пл.)		Черепанова Е. А.		02.11.22	ИНЖЕНЕРНО-ТОПОГРАФИЧЕСКИЙ ПЛАН (М 1:500)			
Дубликат кр.отг.		Петрушина М. Д.		02.11.22				
						Стадия	Лист	Листов
						И	1	4
						МОСКОВСКАЯ АРХИТЕКТУРА с ГБУ "Мосгортреестр"		


					3/5624-22 - ИГД-Г
Изм.	Коп.ч.	Лист	№ док.	Подпись	Дата
Наименование объекта: Жилой комплекс					
Разработан					
Полевые работы Семенова А. А.					02.11.22
Камерал. работы Воронцова О. А.					02.11.22
Подзем. работы Седова А. М.					02.11.22
Коррект. топогр. Аргуусов С. В.					02.11.22
Коррект. подзем. Рыжкова Л. А.					02.11.22
ЛПР (Кр. лин.) Чернышова Е. А.					02.11.22
Дубликат кр. опл. Петрушина М. Д.					02.11.22
Заказчик: ООО "Балчуг Эстейт" Местоположение (адрес) объекта: г. Москва, Садовническая улица, 75/1 Номенклатура: А-VIII-69-04					
ИНЖЕНЕРНО-ТОПОГРАФИЧЕСКИЙ ПЛАН (М: 1:500) СТАДИЯ ЛИСТ ЛИСТОВ					
И 3 4					
МОСКОВСКАЯ АРХИТЕКТУРА © ГБУ "Мосгоргеопротект"					

						3/5624-22 - ИГДИ-Г			
Изм.	Коп.уч.	Лист	№ док.	Подпись	Дата	Наименование объекта: Жилой комплекс			
Разработан						Заказчик: ООО "Балчуг Эстейт"			
Полевые работы	Семенов А. А.			02.11.22		Москотоволеное (адрес) объекта: г. Москва, Садовническая ул., 76/1	Стадия	Лист	Листов
Камерал. работ	Воронова О. А.			02.11.22			И	2	4
Подзем. работы	Седов А. А.			02.11.22		Номенклатура: А-IX-10-13			
Коррект. топогр.	Коршунова С. В.			02.11.22					
Коррект. подзем.	Яковлева Л. А.			02.11.22					
ЛПР (Кл.инж.)	Чернышова Е. А.			02.11.22		ИНЖЕНЕРНО-ТОПОГРАФИЧЕСКИЙ ПЛАН (М 1:500)	МОСКОВСКАЯ АРХИТЕКТУРА © ГБУ "Мосгортестпроект"		
Дубликат кр.отп.	Петрушина М. Д.			02.11.22					

						3/5624-22 - ИГДИ-Г			
Изм.	Коп. уч.	Лист	№ док.	Подпись	Дата	Наименование объекта: Жилой комплекс			
Разработал						Заказчик: ООО "Балчун Эстейт"			
Полетные работы						Семановой А. А.	02.11.22		
Камерал. работы						Воронова О. А.	02.11.22		
Подзем. работы						Седова А. М.	02.11.22		
Коррект. топоз.						Корпусова С. В.	02.11.22		
Коррект. подзем.						Алексеева Л. А.	02.11.22		
ЛПГ (Ю.г. лин.)						Чернышова Е. А.	02.11.22		
Дубликат гр. отн.						Делютина М. Д.	02.11.22		
ИНЖЕНЕРНО-ТОПОГРАФИЧЕСКИЙ ПЛАН (М 1:500)							Стадия	Лист	Листов
							И	4	4
							МОСКОВСКАЯ АРХИТЕКТУРА © ГБУ "Мосгортреестр"		

Проезд, Тип 1
с возможностью проезда
пожарной техники


(альбом СК-6101-2010, тип А-2)

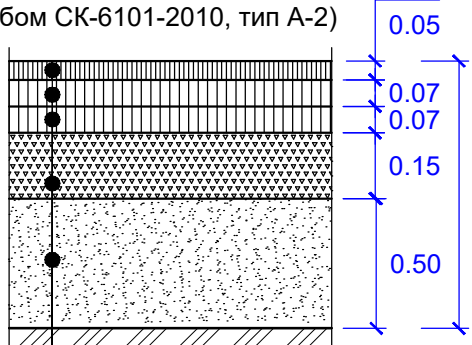

Мелкозернистый плотный асфальтобетон марки II типа "В" по ГОСТ 9128-2013
Крупнозернистый плотный асфальтобетон типа "В" марки II по ГОСТ 9128-2013
Крупнозернистый плотный асфальтобетон типа "В" марки III по ГОСТ 9128-2013
Щебеночные смеси по ГОСТ 25607-2009
Геотекстиль
Песок с/з. Кф≥3 м/сут., Купл.=0,98 по ГОСТ 8736-2014
Местный уплотненный грунт Купл.=0,95

Проезд на подземном гараже, Тип 1*
с возможностью проезда
пожарной техники


(альбом СК-6101-2010, тип А-2)

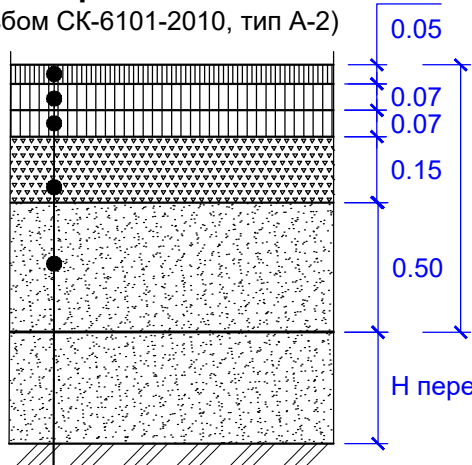

Мелкозернистый плотный асфальтобетон марки II типа "В" по ГОСТ 9128-2013
Крупнозернистый плотный асфальтобетон типа "В" марки II по ГОСТ 9128-2013
Крупнозернистый плотный асфальтобетон типа "В" марки III по ГОСТ 9128-2013
Щебеночные смеси по ГОСТ 25607-2009
Геотекстиль
Песок с/з. Кф≥3 м/сут., Купл.=0,98 по ГОСТ 8736-2014
Песок с/з. Кф≥3 м/сут., Купл.=0,98 по ГОСТ 8736-2014 h перемен.
Геотекстиль для разделения слоев по ГОСТ 56419-2015 (прочность на растяжение не менее 5кН/м)
Конструкция подземного гаража (см. раздел АР)

Тротуар из плитки, тип 2, 3
с возможностью проезда пожарной техники


(альбом Типовых конструкций г. Москвы, применительно к табл.8)

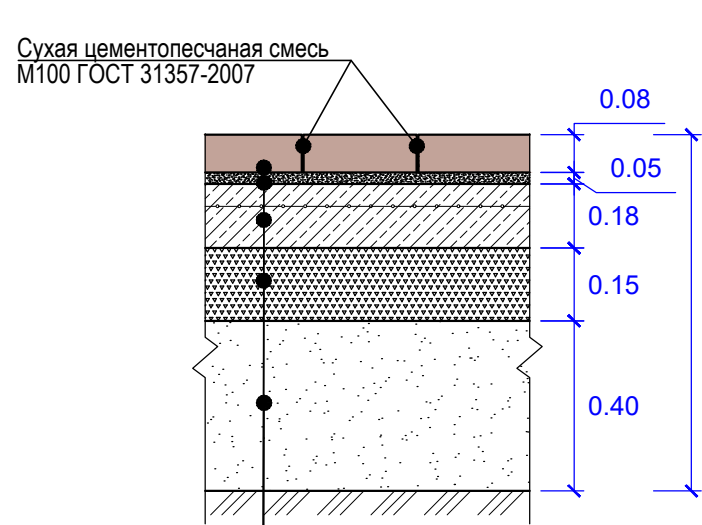

Бетонная тротуарная плитка по ГОСТ 17608-2017
Сухая цементопесчаная смесь М100 по ГОСТ 31357-2007
Цементобетон монолитный В15 Вtb2.4, F100 по ГОСТ 26633-2015 армированный сеткой Ø5 Вр1 100х100 по ГОСТ 8478-81
Щебеночно-гравийная-песчаная смесь С 5 М600 по ГОСТ 25607-2009
Геотекстиль для разделения слоев по ГОСТ 56419-2015 (прочность на растяжение не менее 5кН/м)
Песок с/з. Кф≥3 м/сут. по ГОСТ 8736-2014, Купл.=0,98
Местный уплотненный грунт Купл.=0,98

Тротуар из плитки, тип 4, 5, 6


(альбом Типовых конструкций г. Москвы, применительно к табл.8)

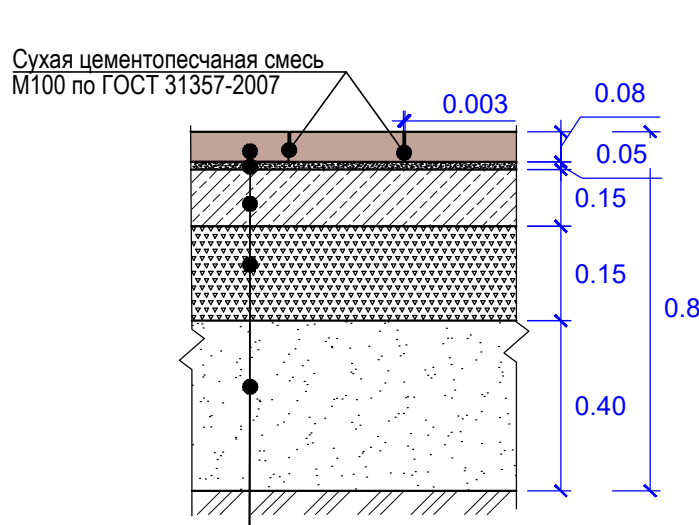

Бетонная тротуарная плитка по ГОСТ 17608-2017
Сухая цементопесчаная смесь М100 по ГОСТ 31357-2007
Цементобетон монолитный В15 Вtb2.4, F100 по ГОСТ 26633-2015
Щебеночно-гравийная-песчаная смесь С 5 М600 по ГОСТ 25607-2009
Геотекстиль для разделения слоев по ГОСТ 56419-2015 (прочность на растяжение не менее 5кН/м)
Песок с/з. Кф≥3 м/сут. по ГОСТ 8736-2014, Купл.=0,98
Местный уплотненный грунт Купл.=0,98

Тротуар из плитки, тип 2*, 3*
с возможностью проезда пожарной техники на
подземном гараже


(альбом Типовых конструкций г. Москвы, применительно к табл.8)

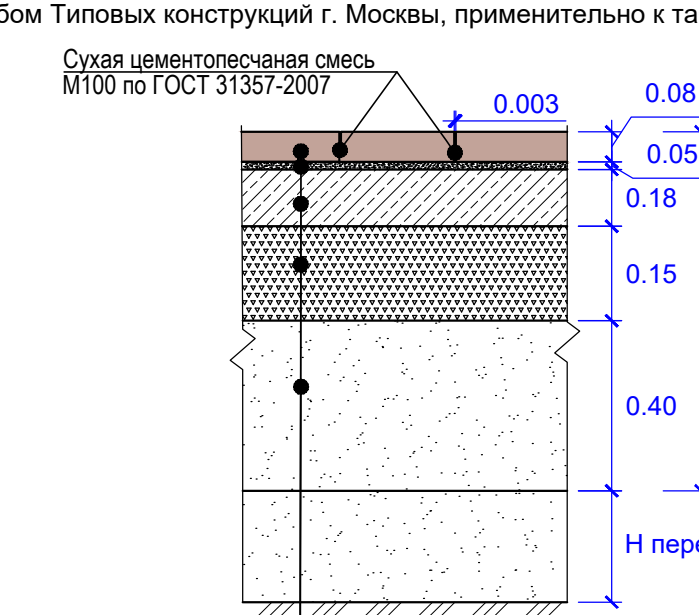

Бетонная тротуарная плитка по ГОСТ 17608-2017
Сухая цементопесчаная смесь М100 по ГОСТ 31357-2007
Цементобетон монолитный В15 Вtb2.4, F100 по ГОСТ 26633-2015
Щебеночно-гравийная-песчаная смесь С 5 М600 по ГОСТ 25607-2009
Геотекстиль для разделения слоев по ГОСТ 56419-2015 (прочность на растяжение не менее 5кН/м)
Песок с/з. Кф≥3 м/сут. по ГОСТ 8736-2014, Купл.=0,98
Песок с/з. Кф≥3 м/сут., Купл.=0,98 по ГОСТ 8736-2014 h перемен.
Геотекстиль для разделения слоев по ГОСТ 56419-2015 (прочность на растяжение не менее 5кН/м)
Конструкция подземного гаража (см. раздел АР)


Тротуар из плитки, тип 4*, 4**, 5*, 6* на подземном гараже

(альбом Типовых конструкций г. Москвы, применительно к табл.8)

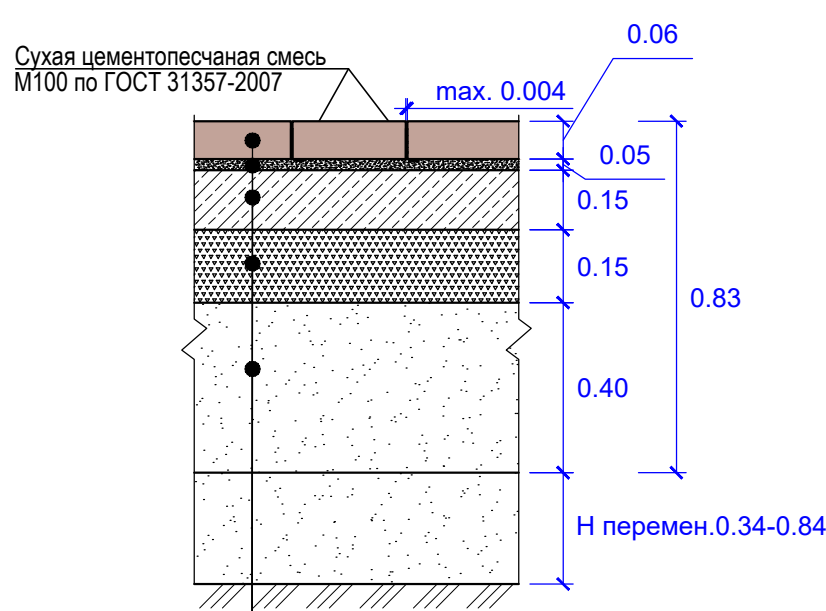

Бетонная тротуарная плитка по ГОСТ 17608-2017
Сухая цементопесчаная смесь М100 по ГОСТ 31357-2007
Цементобетон монолитный В15 Вtb2.4, F100 по ГОСТ 26633-2015
Щебеночно-гравийная-песчаная смесь С 5 М600 по ГОСТ 25607-2009
Геотекстиль
Песок с/з. Кф≥3 м/сут. по ГОСТ 8736-2014, Купл.=0,98
Песок с/з. Кф≥3 м/сут., Купл.=0,98 по ГОСТ 8736-2014 h перемен.
Геотекстиль для разделения слоев по ГОСТ 56419-2015 (прочность на растяжение не менее 5кН/м)
Конструкция подземного гаража (см. раздел АР)


Покрытие из полиуретана на подземном гараже, тип 7*

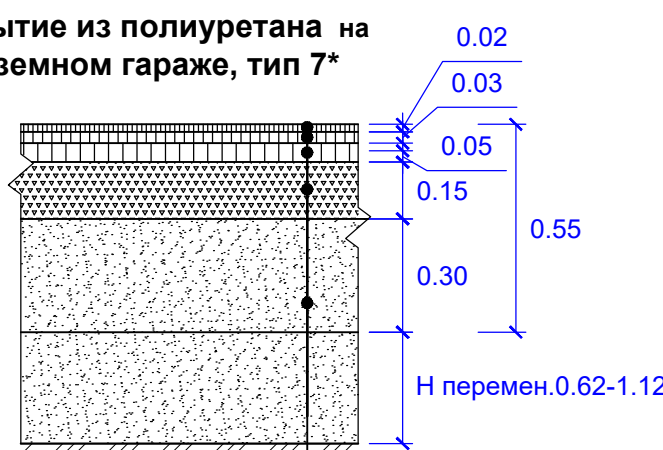


Каучуковая крошка фракцией 5 мм (полиуритановый клей, краситель)
Резиновая крошка фракцией 5 мм
Крупнозернистый а/б тип В марка III по ГОСТ 9128-2013
Щебень М400, фракции 5-20 мм по ГОСТ 8267-93
Песок с/з. Кф≥3 м/сут., Купл.=0,95 по ГОСТ 8736-2014
Песок с/з. Кф≥3 м/сут., Купл.=0,98 по ГОСТ 8736-2014 h перемен.
Геотекстиль для разделения слоев по ГОСТ 56419-2015 (прочность на растяжение не менее 5кН/м)
Конструкция подземного гаража (см. раздел АР)

Схемы сопряжения покрытий


Сопряжение покрытий тротуара, газона и проезда

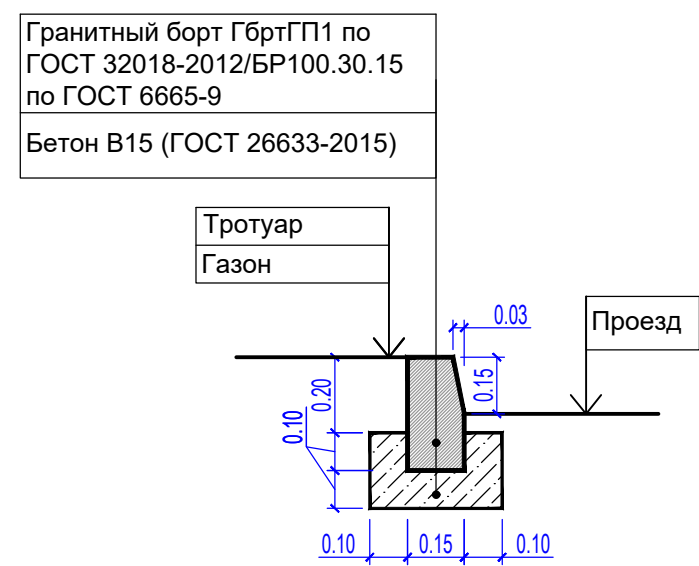


Сопряжение покрытий тротуара и газона

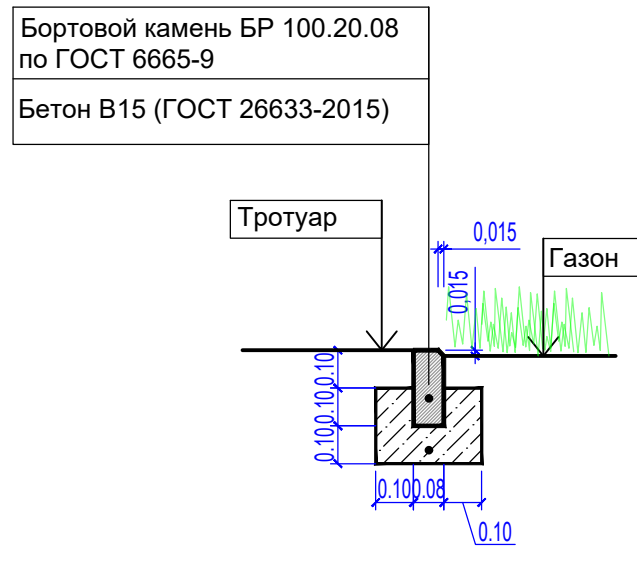

Сопряжение покрытия из полиуретана и газона

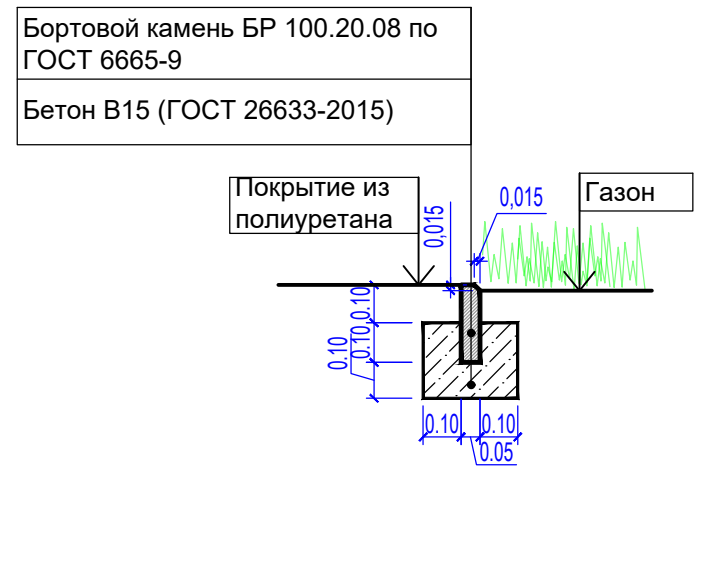


Сопряжение покрытия из полиуретана и тротуара

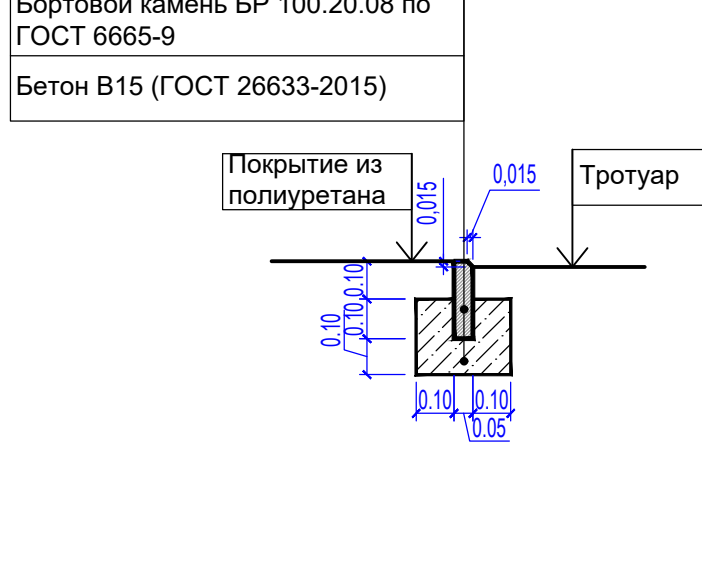


Наружная стена здания

Конструкция скрытой отмостки с покрытием из газона, тип 8

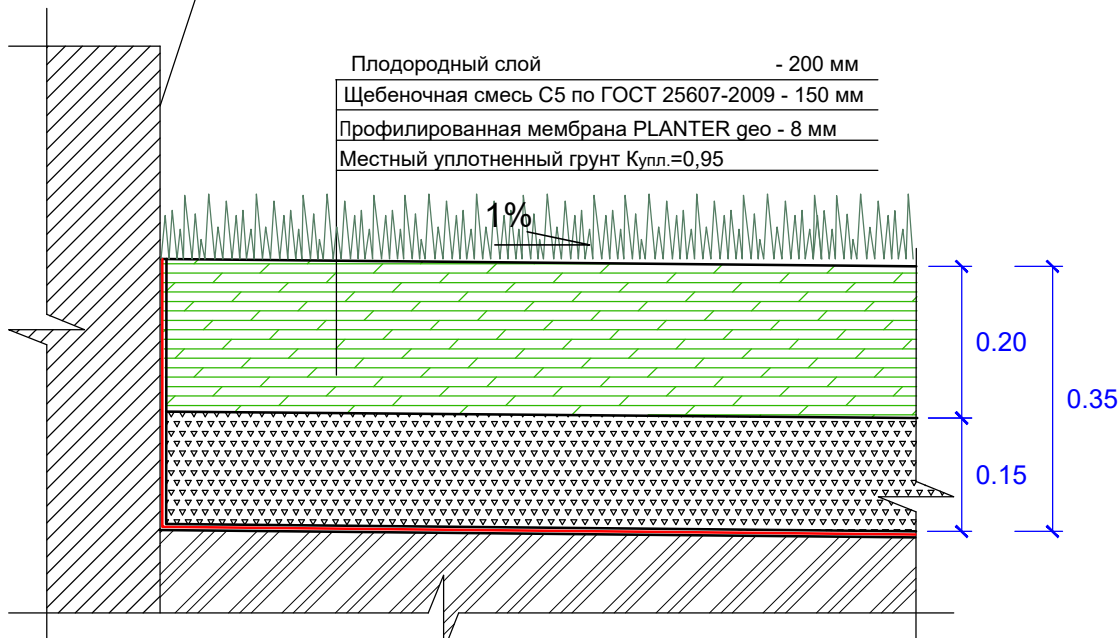



Наружная стена здания

Конструкция скрытой отмостки с покрытием из газона, тип 8*

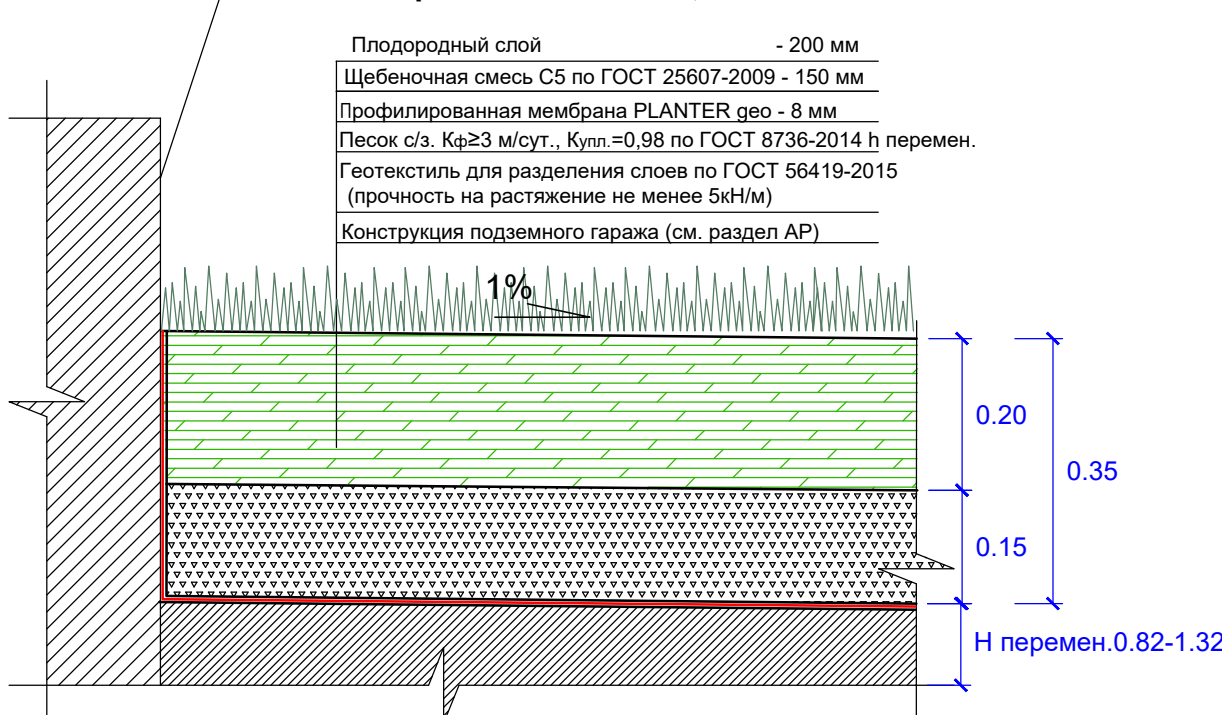



Примечание:
1. См. совместно с листом 5 "План дорожных покрытий".

						АА/БЗ-03-ДС3-ПЗУ					
						"Жилой комплекс", расположенный по адресу: г. Москва, ЦАО, Садовническая ул.,вл 76/71					
Изм.	Кол.уч.	Лист	Нед.	Подпись	Дата	Схема планировочной организации земельного участка			Стадия	Лист	Листов
									П	6	
Разработал	Кузнецова				09.24	Конструкции дорожных покрытий. М 1:500			А R C H I T E C T		
Рук.отдела	Кузнецова				09.24						
ГАП	Добрякова				09.24						
Н.контр.	Кузнецова				09.24						

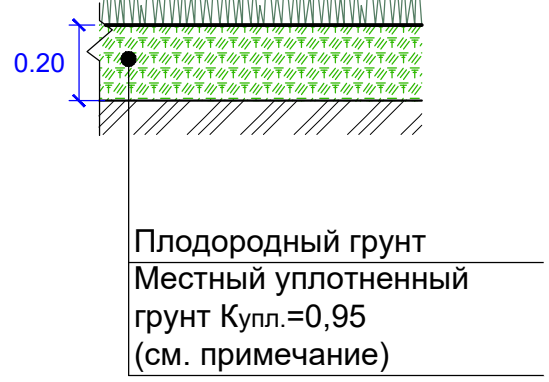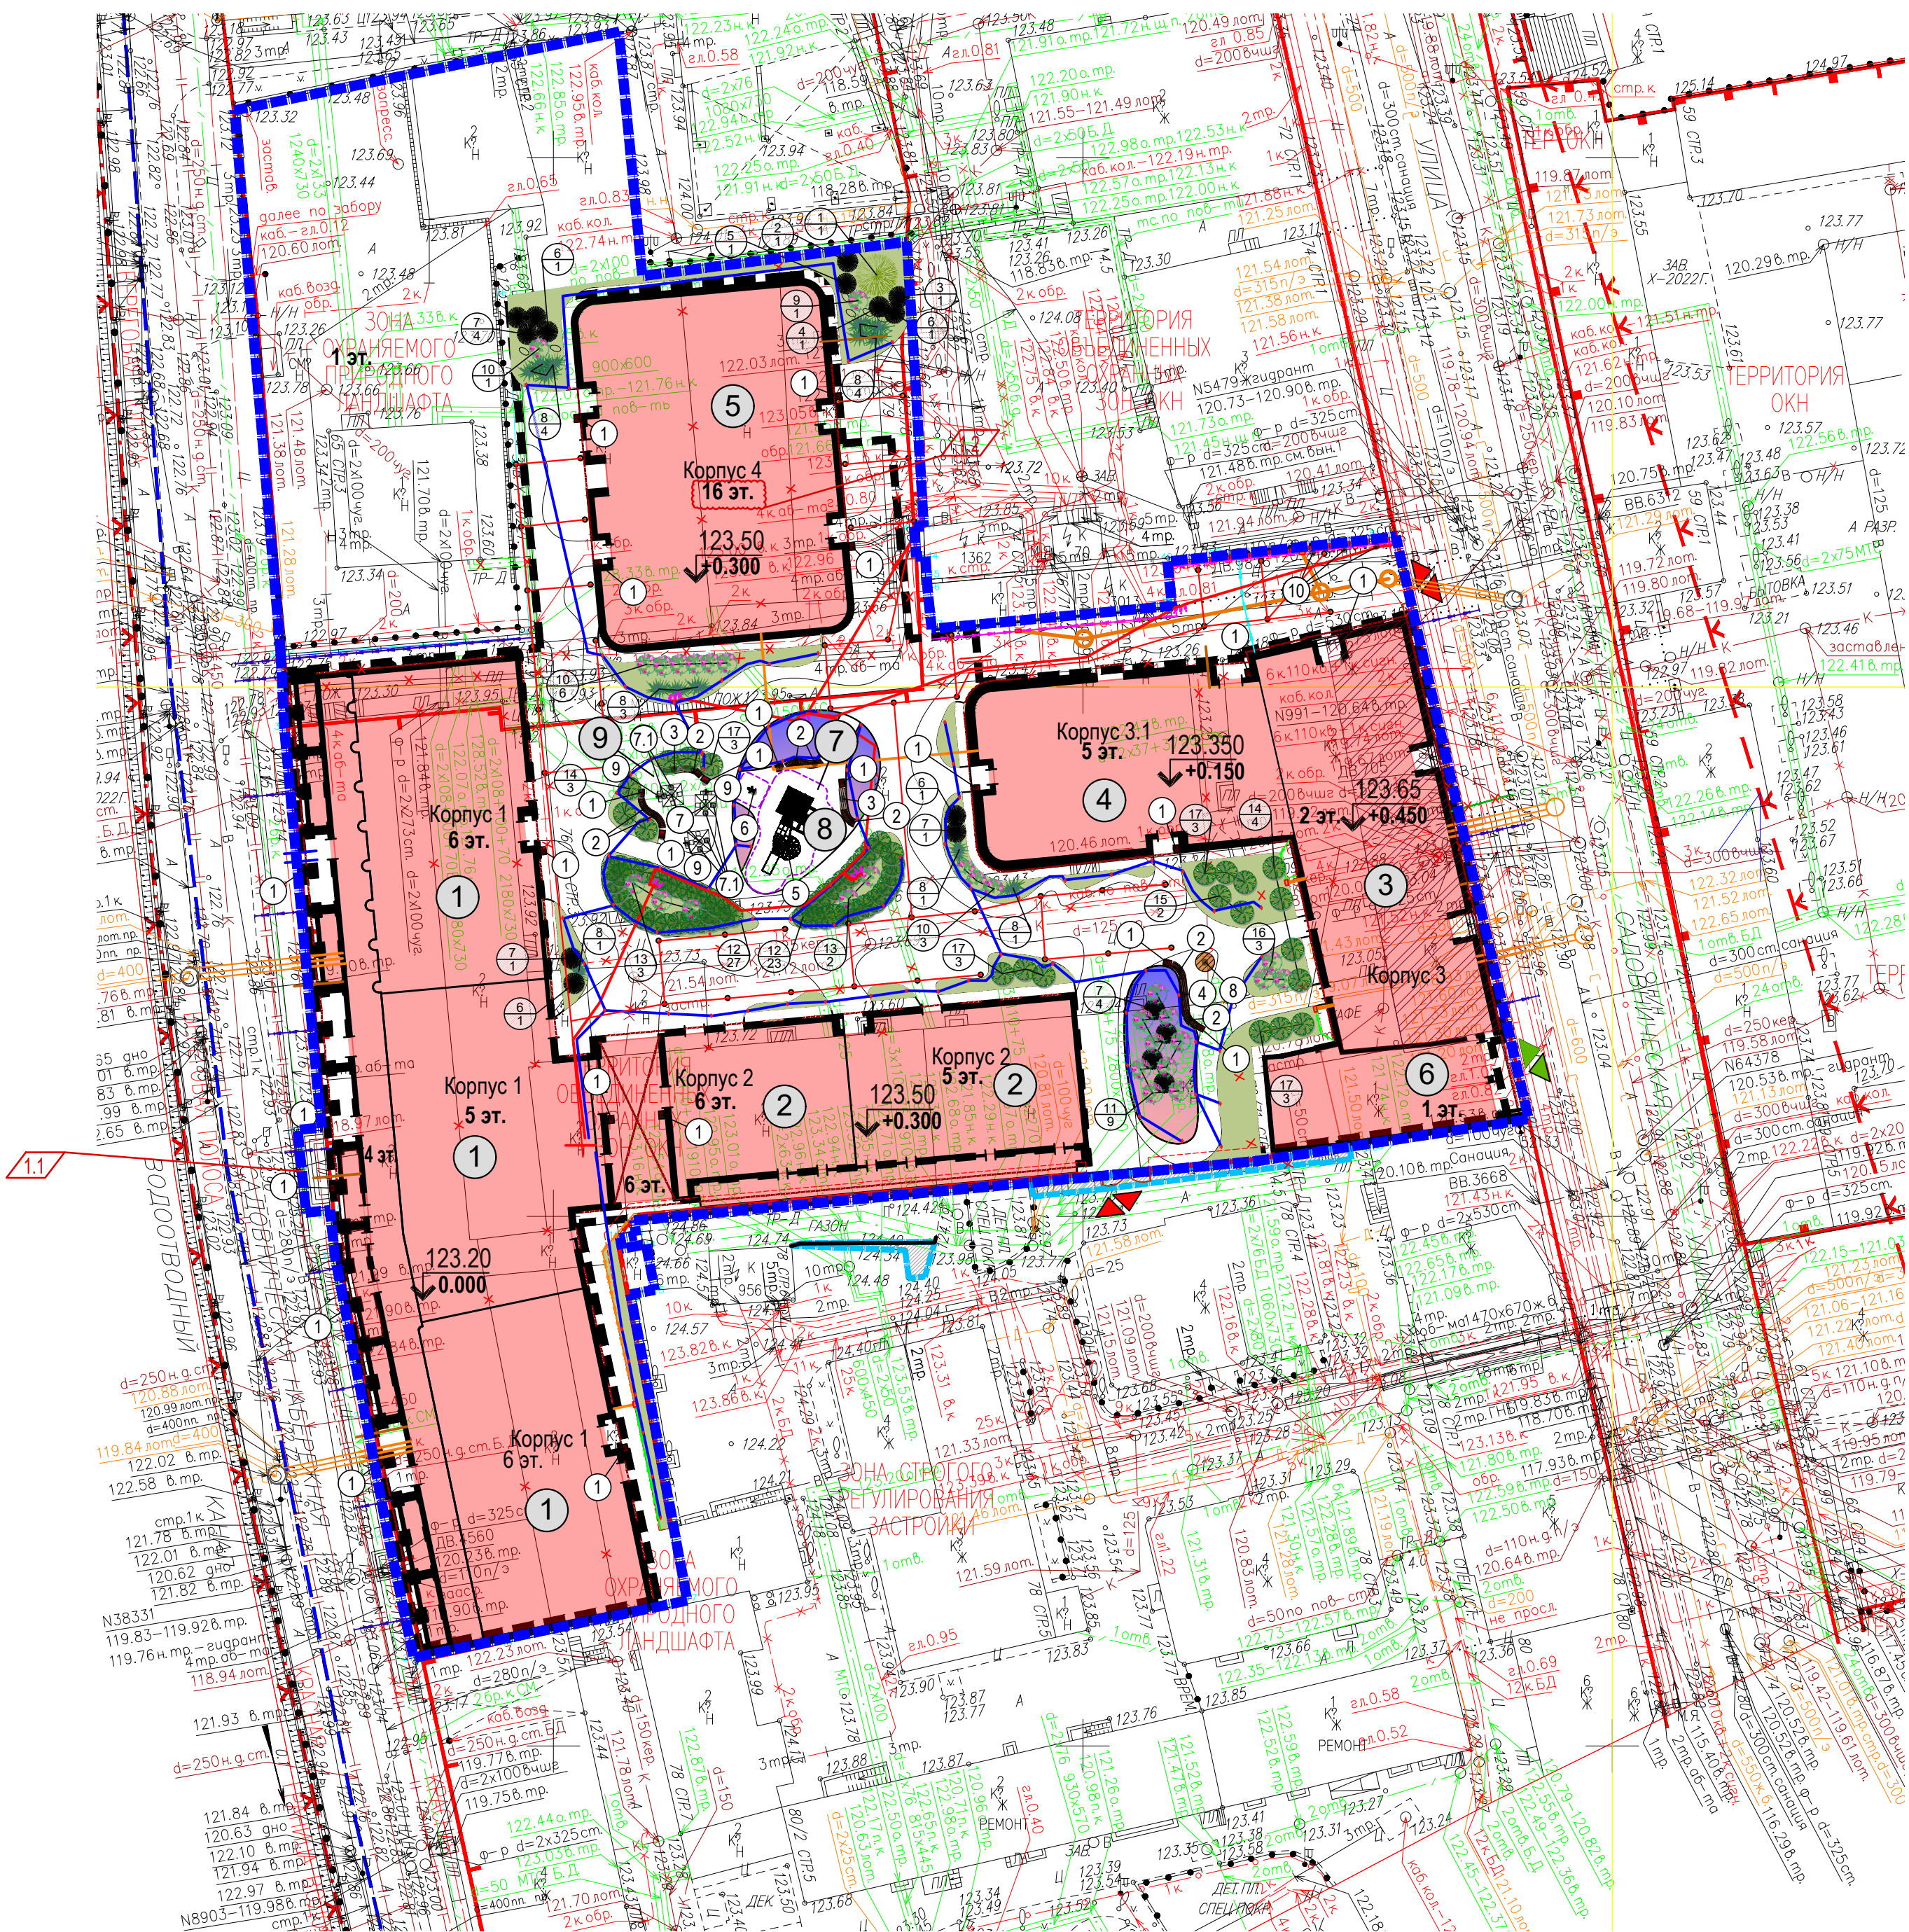

0.20

Плодородный грунт
Местный уплотненный
грунт $K_{упл.} = 0,95$
(см. примечание)
Геотекстиль для
разделения слоев по
ГОСТ 56419-2015
(прочность на растяжение
не менее 5кН/м)
Конструкция подземного
гаража (см. раздел АР)

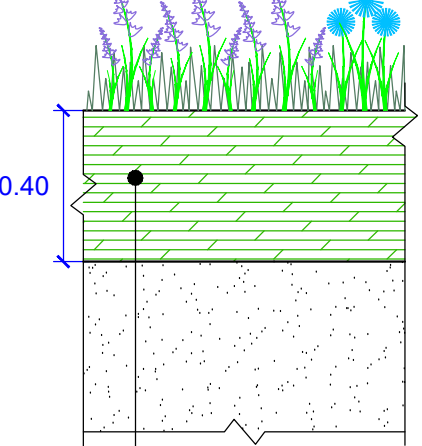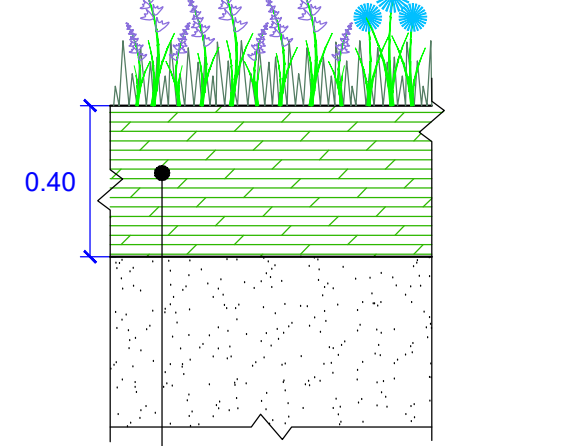

Плодородный грунт
Местный уплотненный грунт $K_{упл}=0.95$ (см. примечание)
Геотекстиль для разделения слоев по ГОСТ 56419-2015 (прочность на растяжение не менее 5кН/м)
Конструкция подземного гаража (см. раздел АР)

СХЕМА РАСПОЛОЖЕНИЯ ЧАСТЕЙ

1	2
3	4

В ГОЛУБЫХ ГРАНИЦАХ НАНЕСЕНА ГРАНИЦА УЧАСТКА ПО ДАННЫМ МАТЕРИАЛАМ ПРЕДОСТАВЛЕННЫМ ЗАКАЗЧИКОМ. ДАННЫЙ МАТЕРИАЛ НЕ МОЖЕТ БЫТЬ ИСПОЛЬЗОВАН ДЛЯ РЕГИСТРАЦИИ ПРАВ СОБСТВЕННОСТИ.

[illegible]

					35624-22-ИД-П								
Изм.	Кол.уч.	Лист	№ дораб.	Подпись	Дата	Наименование объекта. Краткое описание							
Разработчик						Издание: ООО "Техно-Эксперт" Местонахождение: адрес объекта: Москва, Садовнический проезд, 19/171 Дата: 19.09.18 Инженер: А.В.Ов-98					Страница	Лист	Листов
Получение работ/Специалист А.А.											И	1	4
Кампания работ/Специалист А.А.													
Получение работ/Специалист А.А.													
Корректировка работ/Специалист С.В.													
Корректировка работ/Специалист С.В.						ИНЖЕНЕРНО-ТОПОГРАФИЧЕСКИЙ ПЛАН М:1:500					МОСКОВСКАЯ АРХИТЕКТУРА © ГБУ "Мосгоргеоцентр"		
ПРП (Курсы)													
Корректировка работ/Специалист М.Д.													
Дубликат работ/Специалист М.Д.													

					3.9564-22 – ИТДАГ			
Имя	Колуч	Лист	№ док	Подпись	Дата	Наименование объекта, задачи, объекта		
Разработчик								
Получатель работ	Селиванов А.А.				02.11.22	Заказчик: ООО "Тяжелый Асфальт"		
Клиент	работы	Селиванов А.А.			02.11.22	Исполнитель: предприятие – Москва, Свердловское шоссе, 19/21		
Получатель работ	Селиванов А.А.				02.11.22	Наименование: А/В-09/04		
Клиент	работы	Селиванов А.А.			02.11.22	Страница	Лист	Листов
Клиент	работы	Селиванов А.А.			02.11.22	И	3	4
ПР (К.руч.)	Селиванов А.А.				02.11.22	ИЖЕНЕРО-ТОПОГРАФИЧЕСКИЙ ПУНКТ (М: 1:500)		
ПР (К.руч.)	Селиванов А.А.				02.11.22	ОБЪЕКТ: "Мосгорпроект"		

Поз.	Наименование растений	Возраст, лет	Кол-во, шт.	Примечание
в границе ГПЗУ				
Деревья:				
1	Ель колочная "Blue Diamond"	12-15	1	с комом 1.3 х 1.3 х 0.6 м
2	Можжевельник китайский "Spirita"	12-15	1	с комом 1.0 х 1.0 х 0.6 м
3	Можжевельник обыкновенный "Hibernica"	12-15	1	с комом 1.0 х 1.0 х 0.6 м
4	Ель плачущая "Inversa"	12-15	1	с комом 1.3 х 1.3 х 0.6 м
5	Туя западная "Sunkist"	12-15	1	с комом 1.0 х 1.0 х 0.6 м
Итого кдеревьев:			5	
Кустарники:				
6	Туя западная "Golden Globe"	2 - 3	4	с комом 0,5 х 0,5 х 0,4 м
7	Туя западная "Brobeck's Tower"	2 - 3	10	с комом 0,5 х 0,5 х 0,4 м
8	Можжевельник горизонтальный "Blue Chip"	2 - 3	14	с комом 0,5 х 0,5 х 0,4 м
9	Ива цельнолистная "Hakuro-nishiki"	2 - 3	1	с комом 0,5 х 0,5 х 0,4 м
10	Барбарис Тунберга "Harlequin"	2 - 3	10	с комом 0,5 х 0,5 х 0,4 м
11	Спирея японская "Goldflame"	2 - 3	9	с комом 0,5 х 0,5 х 0,4 м
12	Спирея японская "Little Princess"	2 - 3	50	с комом 0,5 х 0,5 х 0,4 м
13	Чубушник вечноцветущий "Philadelphus coronarius"	2 - 3	6	с комом 0,5 х 0,5 х 0,4 м
14	Дерен белый "Elegantissima"	2 - 3	7	с комом 0,5 х 0,5 х 0,4 м
15	Снежногоним белый "Symphoricarpos albus"	2 - 3	2	с комом 0,5 х 0,5 х 0,4 м
16	Магония падуболистная "Apolo"	2 - 3	3	с комом 0,5 х 0,5 х 0,4 м
17	Спирея березолистная "Betulafolia"	2 - 3	12	с комом 0,5 х 0,5 х 0,4 м
Итого кустарников:			127	

18	Цветники из многолетников,	(м²)	31	
19	Газон обыкновенный,	(м²)	97	

20	Цветники из многолетников,	(м²)		165	
21	Газон обыкновенный,	(м²)		676.25	

No п/п	Наименование	Примечание
Здания и сооружения		
1	Корпус №1	Проектируемый
2	Корпус №2	Проектируемый
3	Корпус №3	Проектируемый
4	Корпус №3.1	Проектируемый
5	Корпус №4	Проектируемый
6	Въезд/выезд в подземную автостоянку (рампа)	Проектируемый
7	Детская площадка	Проектируемая
8	Спортивная площадка	Проектируемая
9	Площадка для отдыха	Проектируемая

Поз.	Обозначение	Наименование	Кол.	Примечание
1		Урна стальная «Новая Москва», арт. 12144, шт.	24	ООО "Хоббиа"
2		Скамейка стальная «Радий» со спинкой, арт.9705, шт.	8	ООО "Хоббиа"
3		Скамейка стальная «Лондон» без спинки 2 м, арт.24379, шт.	2	ООО "Хоббиа"
4		Скамейка стальная «Лондон» 3 м, арт. 14839, шт.	1	ООО "Хоббиа"
5		Игровой комплекс QUANTWOOD «Звезда», арт.25527, шт.	1	ООО "Хоббиа"
6		Качалка на пружине HARDWOOD «Дентон», арт.26481, шт.	1	ООО "Хоббиа"
7		Стул для кафе/террасы, серия "MONTMARTRE by Jonas Wagell", шт.	3	"Mitab"
7.1		Стул для кафе/террасы, серия "MONTMARTRE by Jonas Wagell", шт.	12	"Mitab"
8		Модульная скамейка «Эколимбс Комби-5», арт.12156, шт.	1	ООО "Хоббиа"
9		Зонт от солнца со смещением, серия "AMBIENTE", шт.	3	ООО "Gizat"
10		Стопка велосипедная "Город", арт. 20334, шт.	7	ООО "Хоббиа"
* Возможна замена на аналог				

* Возможна замена на аналог

■ ■ ■ ■ ■ - граница 1 этапа проектирования по ГПЗУ №
РФ-77-4-53-3-76-2024-0641-0 от 09.02.2024

- | | |
|--|---|
| | - граница благоустройства за границами проектируемого участка |
| | - проектируемая подземная автостоянка |
| | - проектируемое здание |
| | - нависающая часть здания |
| | - реконструируемое здание |
| | - скрытая отмостка |
| | - въезд-выезд в подземный parking |
| | - въезд-выезд на территорию пожарных машин и спецтехники |
| | - проектируемое ограждение |
| | - проектируемые ворота/калитка |
| | - проектируемая подпорная стенка |
| | - проектируемые деревья |
| | - проектируемые кустарники |
| | - проектируемый водоотводный лоток |
| | - проектируемый пескоуловитель |
| | - проектируемая дождевая канализация |
| | - проектируемый водопровод |
| | - проектируемая хоз. бытовая канализация |
| | - проектируемые сети наружного освещения в ПНД трубе |
| | - проектируемые электрические кабели |
| | - стробоскопические лампы |
| | - проектируемая телефонная канализация |
| | - границы корректировки |

электронном виде из фрагментов заказа №3/5624-22 от 02.11.2022 г. выданных
ГБУ "Мосгоргеострест" и являющихся их точной копией.

Начальник отдела ГП ООО "Артел Архитектс"

Кузнецова М.Н.

0.000=123.20


					АА/БЗ-03-ДС-ПЗУ					
1	2				"Жилый комплекс", расположенный по адресу: г. Москва, ЦАО, Садовническая ул. д/76/71					
Имя	Контакт	Лист	Подпись	Дата						
					Схема планировочной организации земельного участка			Старший	Лист	Листов
Разработчик	Кузнецова			09.24				П	7	
Рук. отдела	Кузнецова			09.24						
ГАП	Добрынина			09.24						
И.н.конт.	Кузнецова			09.24						
					План благоустройства и озеленения территории. М 1:500			А Б В Г Д Е Ж		

Экспликация зданий и сооружений

No п/п	Наименование	Примечание
Здания и сооружения		
1	Корпус №1	Проектируемый
2	Корпус №2	Проектируемый
3	Корпус №3	Проектируемый
4	Корпус №3.1	Проектируемый
5	Корпус №4	Проектируемый
6	Въезд/выезд в подземную автостоянку (рампа)	Проектируемый
7	Детская площадка	Проектируемая
8	Спортивная площадка	Проектируемая
9	Площадка для отдыха	Проектируемая


Условные обозначения

- граница 1 этапа проектирования по ГПЗУ № РФ-77-4-53-3-76-2024-0641-0 от 09.02.2024
- граница благоустройства за границами проектируемого участка
- проектируемая подземная автостоянка
- проектируемое здание
- нависающая часть здания
- реконструируемое здание
- проектируемое ограждение
- проектируемые ворота/калитка
- проектируемая подпорная стенка
- проектируемая дождевая канализация
- проектируемый водопровод
- проектируемая хозяйственная канализация
- проектируемое сети наружного освещения в ГНД трубе
- проектируемые электрические кабели
- стробоскопические лампы
- проектируемая телефонная канализация
- проектируемый водоотводной лоток
- проектируемый пескоуловитель
- границы корректировки

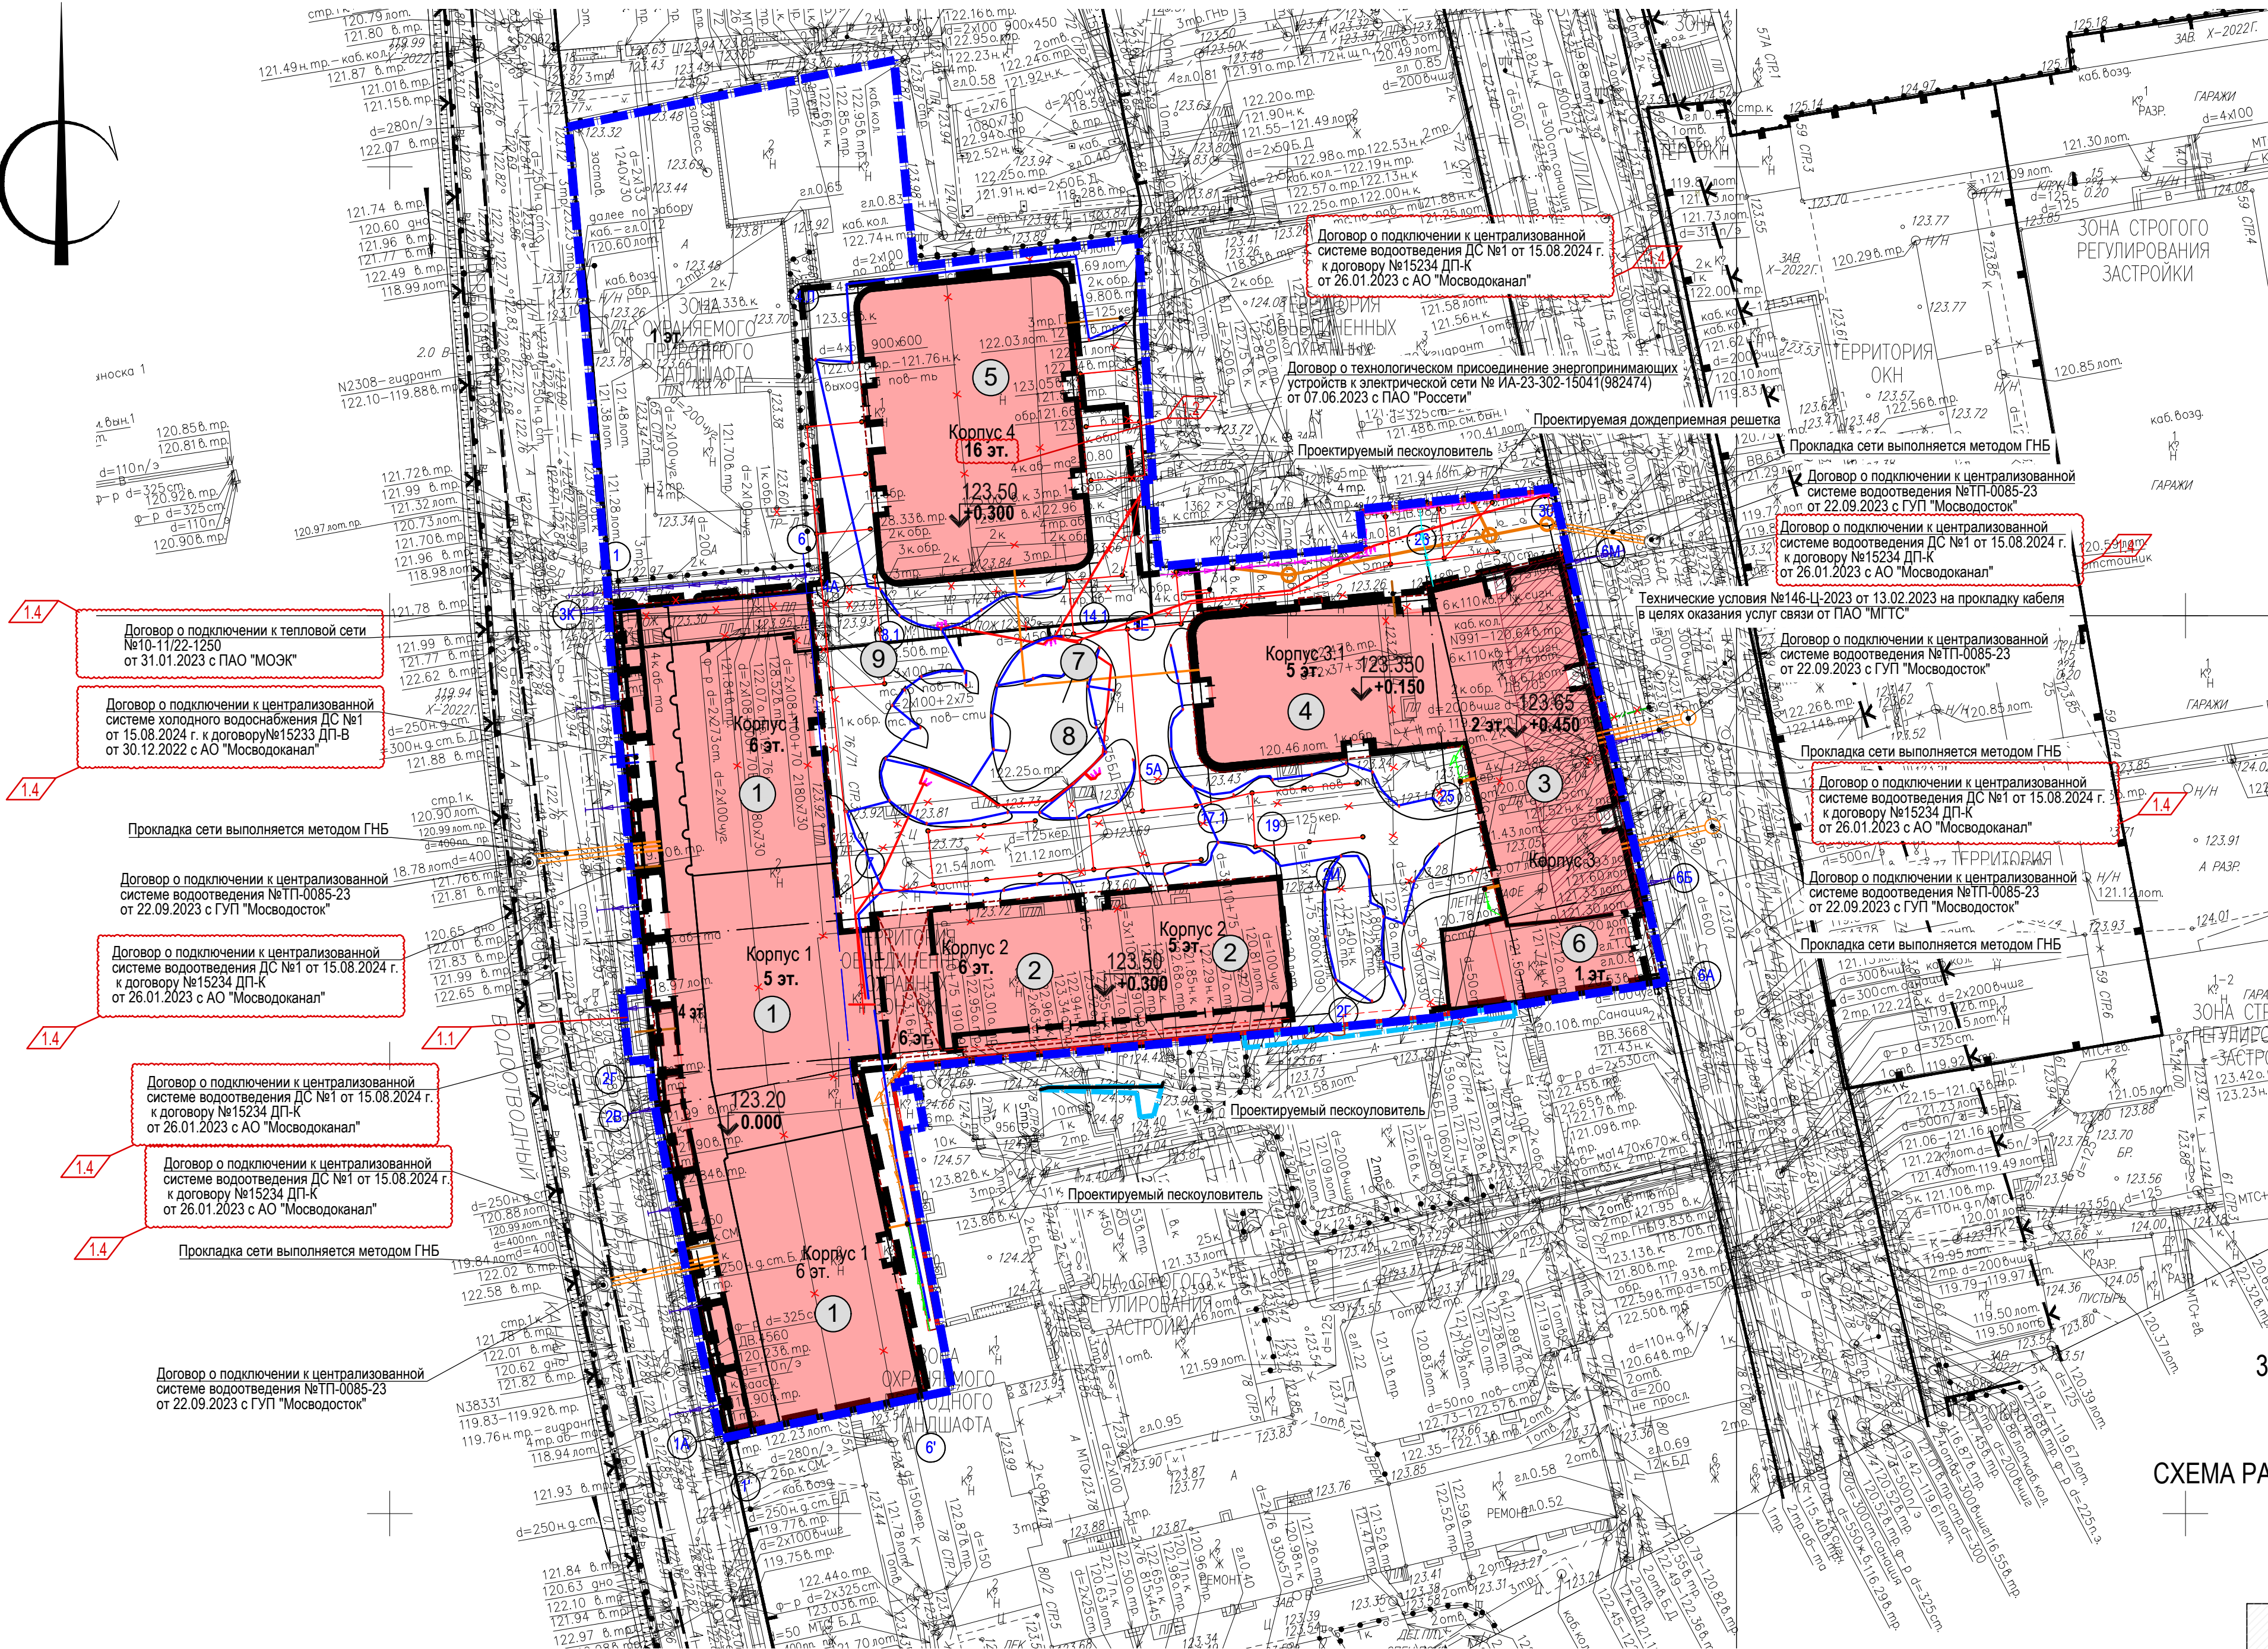

3/5624-22-ИГДИ-Г
в 4-х частях

СХЕМА РАСПОЛОЖЕНИЯ ЧАСТЕЙ

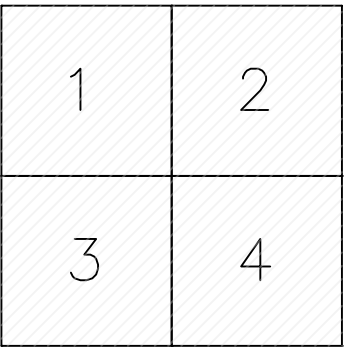

ЛИНИИ ГРАДОСТРОИТЕЛЬНОГО РЕГУЛИРОВАНИЯ НАНЕСЕНЫ ПО СОСТОЯНИЮ НА 20.10.22

ПРОЕКТИРОВАНИЕ ВЫПОЛНИТЬ В УВЯЗКЕ С СУЩЕСТВУЮЩИМИ ОТМЕТКАМИ

По вопросам несоответствия планового положения подземных коммуникаций обращаться по тел. (499)257-09-11 (доб.51-43)

М 1:500, высота сечения рельефа 0.5м

В ГОЛУБЫХ ГРАНИЦАХ НАНЕСЕНА ГРАНИЦА УЧАСТКА ПО ДАННЫМ МАТЕРИАЛАМ ПРЕДОСТАВЛЕННЫМ ЗАКАЗЧИКОМ. ДАННЫЙ МАТЕРИАЛ НЕ МОЖЕТ БЫТЬ ИСПОЛЬЗОВАН ДЛЯ РЕГИСТРАЦИИ ПРАВ СОБСТВЕННОСТИ.

система координат: Московская; система высот: Московская

					3/5624-22 - ИГДИ-Г				
Изм.	Кол.уч.	Лист	№ док.	Подпись	Дата	Наименование объекта: Жилой комплекс			
Разработал						Заказчик: ООО "Балчуг Эстейт"			
Полевые работы	Семенов А. А.		02.11.22			Местоположение (адрес) объекта: г. Москва, Садовническая ул., 76/1			
Камерал. работы	Воронова О. А.		02.11.22			Номенклатура: А-IX-09-16			
Подзем. работы	Сидова А. М.		02.11.22			И			
Коррект. топогр.	Корпусова С. В.		02.11.22			СТАДИЯ			
Коррект. подзем.	Рыжкова Л. А.		02.11.22			ЛИСТ			
ЛПР (Кр. лин.)	Черепанова Е. А.		02.11.22			ЛИСТОВ			
Дубликат кр. отп.	Петрушина М. Д.		02.11.22			ИНЖЕНЕРНО-ТОПОГРАФИЧЕСКИЙ ПЛАН (М 1:500)			
						МОСКОМАРХИТЕКТУРА © ГБУ "Мосгоргеотрест"			

					3/5624-22 - ИГДИ-Г				
Изм.	Кол.уч.	Лист	№ док.	Подпись	Дата	Наименование объекта: Жилой комплекс			
Разработал						Заказчик: ООО "Балчуг Эстейт"			
Полевые работы	Семенов А. А.		02.11.22			Местоположение (адрес) объекта: г. Москва, Садовническая ул., 76/1			
Камерал. работы	Воронова О. А.		02.11.22			Номенклатура: А-VIII-09-04			
Подзем. работы	Сидова А. М.		02.11.22			И			
Коррект. топогр.	Корпусова С. В.		02.11.22			СТАДИЯ			
Коррект. подзем.	Рыжкова Л. А.		02.11.22			ЛИСТ			
ЛПР (Кр. лин.)	Черепанова Е. А.		02.11.22			ЛИСТОВ			
Дубликат кр. отп.	Петрушина М. Д.		02.11.22			ИНЖЕНЕРНО-ТОПОГРАФИЧЕСКИЙ ПЛАН (М 1:500)			
						МОСКОМАРХИТЕКТУРА © ГБУ "Мосгоргеотрест"			

					3/5624-22 - ИГДИ-Г				
Изм.	Кол.уч.	Лист	№ док.	Подпись	Дата	Наименование объекта: Жилой комплекс			
Разработал						Заказчик: ООО "Балчуг Эстейт"			
Полевые работы	Семенов А. А.		02.11.22			Местоположение (адрес) объекта: г. Москва, Садовническая ул., 76/1			
Камерал. работы	Воронова О. А.		02.11.22			Номенклатура: А-IX-10-13			
Подзем. работы	Сидова А. М.		02.11.22			И			
Коррект. топогр.	Корпусова С. В.		02.11.22			СТАДИЯ			
Коррект. подзем.	Рыжкова Л. А.		02.11.22			ЛИСТ			
ЛПР (Кр. лин.)	Черепанова Е. А.		02.11.22			ЛИСТОВ			
Дубликат кр. отп.	Петрушина М. Д.		02.11.22			ИНЖЕНЕРНО-ТОПОГРАФИЧЕСКИЙ ПЛАН (М 1:500)			
						МОСКОМАРХИТЕКТУРА © ГБУ "Мосгоргеотрест"			

					3/5624-22 - ИГДИ-Г				
Изм.	Кол.уч.	Лист	№ док.	Подпись	Дата	Наименование объекта: Жилой комплекс			
Разработал						Заказчик: ООО "Балчуг Эстейт"			
Полевые работы	Семенов А. А.		02.11.22			Местоположение (адрес) объекта: г. Москва, Садовническая ул., 76/1			
Камерал. работы	Воронова О. А.		02.11.22			Номенклатура: А-VIII-10-01			
Подзем. работы	Сидова А. М.		02.11.22			И			
Коррект. топогр.	Корпусова С. В.		02.11.22			СТАДИЯ			
Коррект. подзем.	Рыжкова Л. А.		02.11.22			ЛИСТ			
ЛПР (Кр. лин.)	Черепанова Е. А.		02.11.22			ЛИСТОВ			
Дубликат кр. отп.	Петрушина М. Д.		02.11.22			ИНЖЕНЕРНО-ТОПОГРАФИЧЕСКИЙ ПЛАН (М 1:500)			
						МОСКОМАРХИТЕКТУРА © ГБУ "Мосгоргеотрест"			

							0.000=123.20					
							АА/БЗ-03-ДСЗ-ПЗУ					
							"Жилой комплекс", расположенный по адресу: г. Москва, ЦАО, Садовническая ул., вл 76/71					
1	3						Схема планировочной организации земельного участка			Стадия	Лист	Листов
Изм.	Колуч.	Лист	Недок.	Подпись	Дата	П				8		
Разработал		Кузнецова		09.24		Сводный план инженерных сетей. М 1:500			ARCHITECT			
Рук. отдела		Кузнецова		09.24								
ГАП		Добрякова		09.24								
Н. контр.		Кузнецова		09.24								