


ООО "МБ-Проект-бюро"

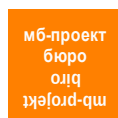

Заказчик

ООО «Специализированный застройщик Балчуг эстейт»

**«Жилой комплекс» расположенный по адресу: г. Москва, ЦАО,
Садовническая ул., вл 76/71**

ПРОЕКТНАЯ ДОКУМЕНТАЦИЯ

Раздел 10. Мероприятия по обеспечению доступа инвалидов


АА/БЭ- 03-ДСЗ-ОДИ

Корректировка

Том 10

Москва, 2025

ООО "МБ-Проект-бюро"

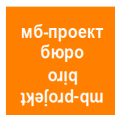

Заказчик

ООО «Специализированный застройщик Балчуг эстейт»

**«Жилой комплекс» расположенный по адресу: г. Москва,
ЦАО, Садовническая ул., вл 76/71**

ПРОЕКТНАЯ ДОКУМЕНТАЦИЯ

Раздел 10. Мероприятия по обеспечению доступа инвалидов

АА/БЭ- 03-ДСЗ-ОДИ

Корректировка

Том 10

Главный архитектор

Руководитель проекта

М. Станишич

В. Шталматович

Содержание тома

	Наименование	
	Содержание	
	Справка о соответствии	
	Пояснительная записка	
	Графические материалы:	
	Схема планировочной организации земельного участка с указанием путей перемещения МГН. М 1_500.	Лист 1
	План первого подземного этажа на отм. -6,000. Схема путей перемещения и эвакуации МГН. М 1_200.	Лист 2
	Корпуса 1, 2. План 1 этажа . Схема путей перемещения и эвакуации МГН . М 1_500.	Лист 3
	Корпуса 1, 2. План 2-4 этажей. Схема путей перемещения и эвакуации МГН. М 1_200.	Лист 4
	Корпуса 1, 2. План 5 этажа . Схема путей перемещения и эвакуации МГН . М 1_200.	Лист 5
	Корпуса 1, 2. План 6 этажа . Схема путей перемещения и эвакуации МГН . М 1_200.	Лист 6
	Корпуса 3, 3.1. План 1 этажа . Схема путей перемещения и эвакуации МГН . М 1_200.	Лист 7
	Корпуса 3, 3.1. План типового этажа. Схема путей перемещения и эвакуации МГН. М 1_200.	Лист 8
	Корпус 4. План 1 этажа. Схема путей перемещения и эвакуации МГН. М 1_200.	Лист 9
	Корпус 4. План типового этажа. Схема путей перемещения и эвакуации МГН. М 1_200.	Лист 10

- 1 -

Изм.	Кол.	Лист	№ док.	Подпись	Дата				
Разработал	Зиновьева	Зиновьева	11.25			Мероприятия по обеспечению доступности инвалидов.	Стадия	Лист	Листов
Проверил	Усманов	Усманов	11.25						
ГАП	Станишич	Станишич	11.25						
Рук.проекта	Шталматович	Шталматович	11.25			Содержание тома.			

СПРАВКА О СОБЛЮДЕНИИ ДЕЙСТВУЮЩИХ НОРМАТИВОВ.

Технические решения, принятые в проекте, соответствуют государственным нормативам, правилам, стандартам, исходным данным, а также техническим условиям и требованиям, выданным органами государственного надзора (контроля) и заинтересованными организациями при соблюдении исходно-разрешительной документации, а также нормам пожаро- и взрывобезопасности эксплуатации объекта и нормам защиты населения и устойчивости объекта в чрезвычайных ситуациях.

Гл. архитектор проекта



М. Станишич

							Лист
							2
Изм.	Кол.уч.	Лист	№ док.	Подп.	Дата		

А. ПЕРЕЧЕНЬ МЕРОПРИЯТИЙ ПО ОБЕСПЕЧЕНИЮ ДОСТУПА ИНВАЛИДОВ К ОБЪЕКТАМ, ПРЕДУСМОТРЕННЫМ В ПУНКТЕ 10 ЧАСТИ 12 СТАТЬИ 48 ГРАДОСТРОИТЕЛЬНОГО КОДЕКСА РОССИЙСКОЙ ФЕДЕРАЦИИ;

А.1. ОБЩАЯ ЧАСТЬ

Проект имеет положительное заключение экспертизы №77-2-1-3-047721-2024 от 19.08.2024

Основанием данной корректировки является поручение Заказчика

- Дополнительное соглашение №3 к договору АА/БЭ-03 от 24.05.2024г
- Задания на корректировку проектной документации объекта «Жилой комплекс» по адресу: г. Москва, ЦАО, Садовническая ул., вл 76/71» от 14.04.2025г
- Градостроительный план земельного участка (ГПЗУ) №РФ-77-4-53-3-76-2025-01998-0 от 14.03.2025, подготовленный Комитетом по архитектуре и градостроительству города Москвы.

Корректировка проектной документации разработана в соответствии с требованием технических регламентов, а также действующих нормативных документов:

- Постановление «О составе разделов проектной документации и требования к их содержанию» от 16 февраля 2008 года №87 (с изм. На 01 декабря 2021 года);
- Постановление правительства РФ от 28 мая 2021 года №815.

Целью корректировки является приведение проектной документации Раздела 3 «Архитектурные решения» объекта «Жилой комплекс, расположенный по адресу: г. Москва, ЦАО, Садовническая ул., вл. 76/71» в соответствии с требованиями дополнительного соглашения №3.

Корректировкой проекта предусмотрено уточнение:

- Актуализирован ГПЗУ №РФ-77-4-53-3-76-2025-01998-0 от 14.03.2025 в связи с изменением предельных максимальных параметров разрешенного строительства;
- Увеличена этажность корпуса 4 с 10 до 16 этажей, откорректировано количество квартир;
- Откорректированы планировочные решения и квартирография корпусов 2 и 3.1 в соответствии с заданием Заказчика;
- Откорректированы планировочные решения первого этажа и количество квартир корпуса 1 – исключена квартира, расположенная на 1-ом этаже в осях 3.К-3.Е/1-6;
- Откорректированы планировочные решения подземной части – увеличено количество кладовых в связи с увеличением количества квартир;
- Откорректировано количество машино-мест для МГН в соответствии с изменением в расчете (увеличение этажности корпуса 4 и квартирография);

						АА/БЭ-03-ДС3-ОДИ			
Изм.	Кол.уч	Лист	№док.	Подп.	Дата	Пояснительная записка	Стадия	Лист	Листов
Разработал	Зиновьева		Зиновьева	11.25					
Проверил	Усманов			11.25					
ГАП	Станищич			11.25					

- Откорректированы планировочные решения первого этажа корпуса 1: выполнена замена пандусов на подъемники наклонного перемещения, которые устанавливаются после сдачи объекта;
- Откорректированы планировочные решения МОП 2-16 этажа корпуса 4: поэтажный выход в лестничную клетку (кроме 1-го этажа) предусмотрен через лифтовой холл, являющийся пожаробезопасной зоной для МГН – в связи с корректировкой этажности корпуса и требований изменения №1 СТУ, отражающих специфику обеспечения пожарной безопасности;
- Откорректированы технико-экономические показатели жилого комплекса;
- Внесены изменения в проектную документацию в части взаимоувязки смежных разделов в части расположения инженерных коммуникаций.

Остальные решения без изменений в соответствии с положительным заключением экспертизы №77-2-1-3-047721-2024 от 19.08.2024.

ОПИСАНИЕ ОБЪЕКТА

Характеристика земельного участка, градостроительная посадка комплекса без изменений, в соответствии с положительным заключением экспертизы №77-2-1-3-047721-2024 от 19.08.2024.

Габариты в осях, этажность и структура корпусов 1, 2, 3 и 3.1 и подземной автостоянки в соответствии с положительным заключением экспертизы №77-2-1-3-047721-2024 от 19.08.2024.

Корпус 4 – прямоугольный в плане объем: 16-ти этажный корпус с габаритами (22,9х32.4 в осях 8.1/14.1 – 4.А/4.Л).

Класс функциональной пожарной опасности жилых корпусов 1,2, 3.1 и 4 принят Ф1.3. Класс функциональной пожарной опасности корпуса 3 принят Ф1.4.

За условную отметку 0.000 принята отметка чистого пола вестибюлей первого этажа 1-го корпуса, что соответствует абсолютной отметке: $0.000 = 123,20$

А.2. РЕШЕНИЯ ПО ОБЕСПЕЧЕНИЮ УСЛОВИЙ ЖИЗНЕДЕЯТЕЛЬНОСТИ МАЛОМОБИЛЬНЫХ ГРУПП НАСЕЛЕНИЯ

- Увеличена этажность корпуса 4 с 10 до 16 этажей, доступ на жилые этажи предусмотрен в МОП 1-16 этажа до дверей квартир (гостевой доступ).

Остальные решения без изменений, в соответствии с положительным заключением экспертизы №77-2-1-3-047721-2024 от 19.08.2024.

А.3. МАШИНО-МЕСТА ДЛЯ МАЛОМОБИЛЬНЫХ ГРУПП НАСЕЛЕНИЯ

Откорректирован расчет машино-мест в связи с увеличением количества жителей (увеличение этажности корпуса 4 и квартирография).

Расчет потребности в местах хранения автомобилей проведен на основании постановления Правительства Москвы от 23 декабря 2015 года (с изменениями на 24

						АА/БЭ-03-ДС3-ОДИ	Лист
Изм.	Кол.уч	Лист	№ док.	Подп.	Дата		

декабря 2019 года) №945-ПП. Подробный расчет потребности машиномест представлен в раздел ПЗУ.

1. Расчет количества машиномест постоянного хранения для жителей дома

Расчетное количество жителей определяется в соответствии с классом жилья бизнес-класс – в соответствии с заданием на проектирование (40 м² согласно СП 42.132330 табл. 5.1 в расчете на одного человека).

Общая площадь квартир с летними помещениями составляет **22 665.31 м²**

Общее количество жителей в доме составит **22 665.31 / 40 м²/чел = 567 чел.**

В соответствии с расчетом, приведенном в разделе ПЗУ, количество машиномест составляет: **Nф = 0.35 x 567 = 199 м/мест.**

Расчет балльной оценки уровня потребности в местах постоянного хранения автомобилей, числа мест постоянного хранения автомобилей приведен в разделе ПЗУ. В соответствии с расчетом итоговое количество машиномест для постоянного хранения индивидуального транспорта по расчету:

$$N_{п} = 199 \text{ м/мест} \times 50\%/100\% = 100 \text{ м/м.}$$

2. Расчет количества машиномест для временного хранения индивидуального транспорта посетителей жилых зон (гостевые стоянки).

В соответствии с п. 6.2.11 гостевые парковки следует предусматривать в количестве 10% от расчетного числа машино-мест для постоянного хранения (Nф).

$$N_{г} = 0,1 \times N_{ф} = 0,1 \times 199 = 20 \text{ м/м.}$$

3. Расчет количества машиномест временного хранения для посетителей и работников ПОН:

В соответствии с приложением 1 для объектов делового управления (размещение объектов капитального строительства с целью: размещения органов управления производством, торговлей, банковской, страховой деятельностью, а также иной управленческой деятельностью, не связанной с государственным или муниципальным управлением), необходимо предусмотреть 1 машиноместо на 60 м² общей площади. Общая площадь помещений ПОН составляет 492.51 м².

Количество м/м для работников ПОН определяется по формуле:

$$N_{в} = S/S_2 * K_3 * K_2$$

$$K_3 = 0.7 - \text{зона Т4}$$

						АА/БЭ-03-ДС3-ОДИ	Лист
Изм.	Кол.уч	Лист	№ док.	Подп.	Дата		

$N_{в}=492.51 \text{ м}^2/ 60 \text{ м}^2*0.7*0.85= 5 \text{ м/м}$

4. Расчет количества машиномест для МГН:

Машиноместа для МГН определяются согласно СП 59.13330.2020 п. 5.2.1.

$25*10\% = 3 \text{ м/м}$ для МГН (из них 2 м/м для М4).

Количество машиномест для жилого комплекса

Машиноместа	По расчету	В границах ГПЗУ	
		Подземный гараж	Открытая автостоянка
Постоянного хранения	100	209	-
Временного хранения (гостевого)	25 (из них 3 м/м для МГН МГН (в т.ч. 2 м/м для М4)	25 (из них 3 м/м для МГН МГН (в т.ч. 2 м/м для М4)	-

Количество необходимых машиномест:

Проектом предусмотрено размещение 234 м/м из них: в подземной автостоянке – 234 м/м (в т.ч. 3 м/м для МГН, из них 2 для МГН М4).

Размещение машиномест для МГН предусмотрено на -1 уровне автостоянки, в зоне выезда из ramпы.

А.4. ОРГАНИЗАЦИЯ ПЕРЕДВИЖЕНИЯ ИНВАЛИДОВ ПО ТЕРРИТОРИИ УЧАСТКА И ДОСТУПА К ВХОДНЫМ ГРУППАМ - без изменений, в соответствии с положительным заключением экспертизы №77-2-1-3-047721-2024 от 19.08.2024.

А.5. МЕРОПРИЯТИЯ ДЛЯ БЕСПРЕПЯТСТВЕННОГО ПЕРЕДВИЖЕНИЯ ИНВАЛИДОВ ВНУТРИ ЗДАНИЯ

В уровне первого этажа передвижение инвалидов всех групп мобильности обеспечено по вестибюльной (входной) зоне жилого комплекса.

- Откорректированы планировочные решения первого этажа корпуса 1: выполнена замена пандусов на подъемники наклонного перемещения, которые устанавливаются после сдачи объекта;

- Откорректированы планировочные решения МОП 2-16 этажа корпуса 4: поэтажный выход в лестничную клетку (кроме 1-го этажа) предусмотрен через лифтовой холл, являющийся пожаробезопасной зоной для МГН – в связи с корректировкой этажности корпуса и требований изменения №1 СТУ, отражающих специфику обеспечения пожарной безопасности. Размещение зон безопасности для корпусов 1, 2 и 3.1 без изменений в соответствии с положительным заключением экспертизы №77-2-1-3-047721-2024 от 19.08.2024.

Остальные решения без изменений - в соответствии с положительным заключением экспертизы №77-2-1-3-047721-2024 от 19.08.2024.

А.6. СРЕДСТВА ИНФОРМАЦИИ - без изменений, в соответствии с положительным заключением экспертизы №77-2-1-3-047721-2024 от 19.08.2024.

А.7. ПУТИ ЭВАКУАЦИИ

Проектное решение корпусов жилого комплекса обеспечивает безопасность МГН в соответствии с требованиями ФЗ №123-ФЗ «Технический регламент о требованиях пожарной безопасности», с учетом мобильности инвалидов-колясочников и инвалидов разных категорий. Конструкции эвакуационных путей класса КО (непожароопасные), предел их огнестойкости соответствует требованиям №123-ФЗ. Материалы для отделки полов, потолков, стен на путях эвакуации применяются в соответствии с таблицей 28 №123-ФЗ. В разработанном проекте эвакуационные пути совмещены с коммуникационными путями перемещения.

В наземной части.

- Откорректированы планировочные решения МОП 2-16 этажа корпуса 4: пожаробезопасная зона для МГН размещена в лифтовом холле – в связи с корректировкой этажности корпуса и требований изменения №1 СТУ, отражающих специфику обеспечения пожарной безопасности. Размещение зон безопасности для корпусов 1, 2 и 3.1 без изменений в соответствии с положительным заключением экспертизы №77-2-1-3-047721-2024 от 19.08.2024.

Остальные решения без изменений – в соответствии с положительным заключением экспертизы №77-2-1-3-047721-2024 от 19.08.2024.

Пожаробезопасные зоны предусмотрены в корпусах 1, 2, 3.1 и 4 на наземных этажах (2-16 этажи), кроме первого, для размещения МГН группы мобильности М4, оснащены системой двусторонней связи. МГН групп мобильности М1-М3 эвакуируются с 2-16 этажей по лестничным клеткам. Ширина межквартирного коридора принята не менее 1,5м.

Ширина лестничных маршей между поручнем и стеной для корпусов 1, 2 и 3.1 - 1,05м, для корпуса 4 – 1,2м. Ограждение высотой 0,9м предусмотрено с внутренней стороны маршей лестниц. Эвакуация МГН из жилой части с первого этажа через вестибюль непосредственно наружу. Эвакуация МГН из коммерческих помещений, расположенных на первом (Корпус 1, 1 и 2 секции) этаже непосредственно на улицу.

Расчет ПБЗ для наземной части (расчет выполнен для наибольшей площади квартир на этаже - типовой этаж корпуса 4)

						АА/БЭ-03-ДС3-ОДИ	Лист
Изм.	Кол.уч	Лист	№ док.	Подп.	Дата		

Количество людей на типовом этаже, проживающих в корпусе 4 с общей площадью квартир 622 м2 на этаже, исходя из обеспеченности 40м2 на человека (в соответствии с заданием на проектирование) принимается – 16 человек – $622 : 40 = 15,6$.

Количество МГН принимается 10% от находящихся на этаже людей. 16 чел.: 10 = 2 чел. МГН.

На этаже возможно нахождение 2-х инвалидов: 1 инвалид группы мобильности М4, и 1 инвалид группы мобильности М2 или М3. Для спасения инвалида группы мобильности М4 предусмотрено его размещение в ПБЗ в лифтовых холлах (4 корпус). Зона размещения М4 занимает 2,4м2. Ширина эвакуационных проходов не заужает эвакуационный путь к лестничной клетке, составляющий 1,2м.

Расчет ПБЗ секций корпуса 1, 2 и корпуса 3.1 выполнен аналогично. На этаже возможно нахождение 2-х инвалидов, 1 инвалид группы мобильности М4, и 1 инвалид группы мобильности М2 или М3. Для спасения инвалида группы мобильности М4 предусмотрено его размещение в ПБЗ – на площадке незадымляемой лестничной клетки. Зона размещения М4 на площадке занимает 2,4м2. Ширина эвакуационных проходов не заужает эвакуационный путь по лестничной клетке, составляющий 1,05м.

В подземной части.

В автостоянке на -1 этаже запроектированы места для парковки МГН. Выделенные места расположены при выезде из ramпы между 2-мя эвакуационными выходами. Для размещения инвалида группы мобильности М4 предусмотрены пожаробезопасные зоны, расположенные в лифтовых холлах лифтов для перевозки пожарных подразделений.

Откорректирован расчет ПБЗ в связи с увеличением количества машино-мест для МГН:

В соответствии с расчетом м/м в автостоянке предусмотрено размещение 3-х гостевых м/м для инвалидов: 2 м/м для М4 и 1 м/м для М1, М2, М3. ПБЗ размещены в 2-х лифтовых холлах площадью 24м2 / 21м2. Зона размещения М4 в помещении лифтового холла (ПБЗ) принята 2,65м2. Ширина эвакуационного прохода в ПБЗ к лестничной клетке НЗ составляет не менее 1м.

Остальные решения без изменений – в соответствии с положительным заключением экспертизы №77-2-1-3-047721-2024 от 19.08.2024.

А.8. ЛИФТЫ - без изменений, в соответствии с положительным заключением экспертизы №77-2-1-3-047721-2024 от 19.08.2024.

Лифты, предназначенные для транспортировки маломобильных групп населения, отвечают следующим требованиям:

- лифты обозначены знаком доступности для МГН;
- внутренние габариты кабины не менее 2,1 x 1,1м;
- ширина дверного проема в свету не менее 0,9м;
- в кабине предусмотрены поручни на высоте 0,9м;
- лифты оборудованы световой или звуковой информацией о движении;

						АА/БЭ-03-ДС3-ОДИ	Лист
Изм.	Кол.уч	Лист	№ док.	Подп.	Дата		

- прибытие кабины на этажи сопровождается звуковым сигналом;
- кнопочные элементы на панели управления кабинами лифтов рельефные;
- у каждой двери лифта, предназначенного для МГН, предусмотрена световая и звуковая информирующая сигнализация, соответствующая ГОСТ Р 51631;
- лифты оснащены системой управления и противодымной защитой в соответствии с требованиями НПБ250.

А.9. САНИТАРНО-БЫТОВЫЕ ПОМЕЩЕНИЯ - без изменений, в соответствии с положительным заключением экспертизы №77-2-1-3-047721-2024 от 19.08.2024.

Б. ОБОСНОВАНИЕ ПРИНЯТЫХ КОНСТРУКТИВНЫХ, ОБЪЕМНО-ПЛАНИРОВОЧНЫХ И ИНЫХ ТЕХНИЧЕСКИХ РЕШЕНИЙ, ОБЕСПЕЧИВАЮЩИХ БЕЗОПАСНОЕ ПЕРЕМЕЩЕНИЕ ИНВАЛИДА НА ОБЪЕКТАХ, УКАЗАННЫХ В ПОДПУНКТЕ «А» НАСТОЯЩЕГО ПУНКТА, А ТАКЖЕ ИХ ЭВАКУАЦИЮ ИЗ УКАЗАННЫХ ОБЪЕКТОВ В СЛУЧАЕ ПОЖАРА ИЛИ СТИХИЙНОГО ВОЗДЕЙСТВИЯ.

Корректировка проекта «Жилого комплекса» по адресу: г. Москва, ЦАО, Садовническая ул., вл. 76/71 разработана на основании:

- Дополнительного соглашения №3 к договору АА/БЭ-03 от 24.05.2024г;
- Градостроительного плана земельного участка (ГПЗУ) **№РФ-77-4-53-3-76-2025-01998-0 от 14.03.2025г**, подготовленного Комитетом по архитектуре и градостроительству города Москвы;
- **Задания на корректировку проектной документации объекта «Жилой комплекс» по адресу: г. Москва, ЦАО, Садовническая ул., вл 76/71» от 14.04.2025г**

Корректировка проектных решений разработана и запроектирована в соответствии с требованиями технических регламентов, а также действующих нормативных документов, включенных в перечень национальных стандартов, обеспечивающих требования №384-ФЗ от 30.12.2009, но не ограничиваясь:

- СП 54.13330.2016 «Здания жилые многоквартирные»
- СП 59.13330.2020 «Доступность зданий и сооружений для маломобильных групп населения»
- СП 136.13330.2012 «Здания и сооружения. Общие положения проектирования с учетом доступности для маломобильных групп населения»;
- СП 137.13330.2012 «Жилая среда с планировочными элементами, доступными инвалидам. Правила проектирования»;
- Федеральный закон от 24 ноября 1995 года - №181-ФЗ – О социальной защите инвалидов в Российской Федерации;
- ГОСТ 5746-2015 «Лифты пассажирские. Основные параметры и размеры»;
- ГОСТ Р 52131-2019 «Средства отображения информации знаковые для инвалидов»;

						АА/БЭ-03-ДС3-ОДИ	Лист
Изм.	Кол.уч	Лист	№ док.	Подп.	Дата		

- ГОСТ Р 52875-2018 «Указатели тактильные наземные для инвалидов по зрению. Технические требования»;

- ГОСТ Р 51261-2022 «Устройства опорные стационарные для маломобильных групп населения. Типы и общие технические требования»;



- ГОСТ Р 51671-2020 «Средства связи и информации технические общего пользования, доступные для инвалидов. Классификация. Требования доступности и безопасности»;

- ГОСТ 33652-2019 «Лифты. Специальные требования безопасности и доступности для инвалидов и других маломобильных групп населения».

В. ОПИСАНИЕ ПРОЕКТНЫХ РЕШЕНИЙ ПО ОБУСТРОЙСТВУ РАБОЧИХ МЕСТ ИНВАЛИДОВ - без изменений, в соответствии с положительным заключением экспертизы №77-2-1-3-047721-2024 от 19.08.2024.

Согласно утвержденному Заданию на проектирование организация рабочих мест для инвалидов не предусмотрена.


						АА/БЭ-03-ДС3-ОДИ	Лист
Изм.	Кол.уч	Лист	№ док.	Подп.	Дата		

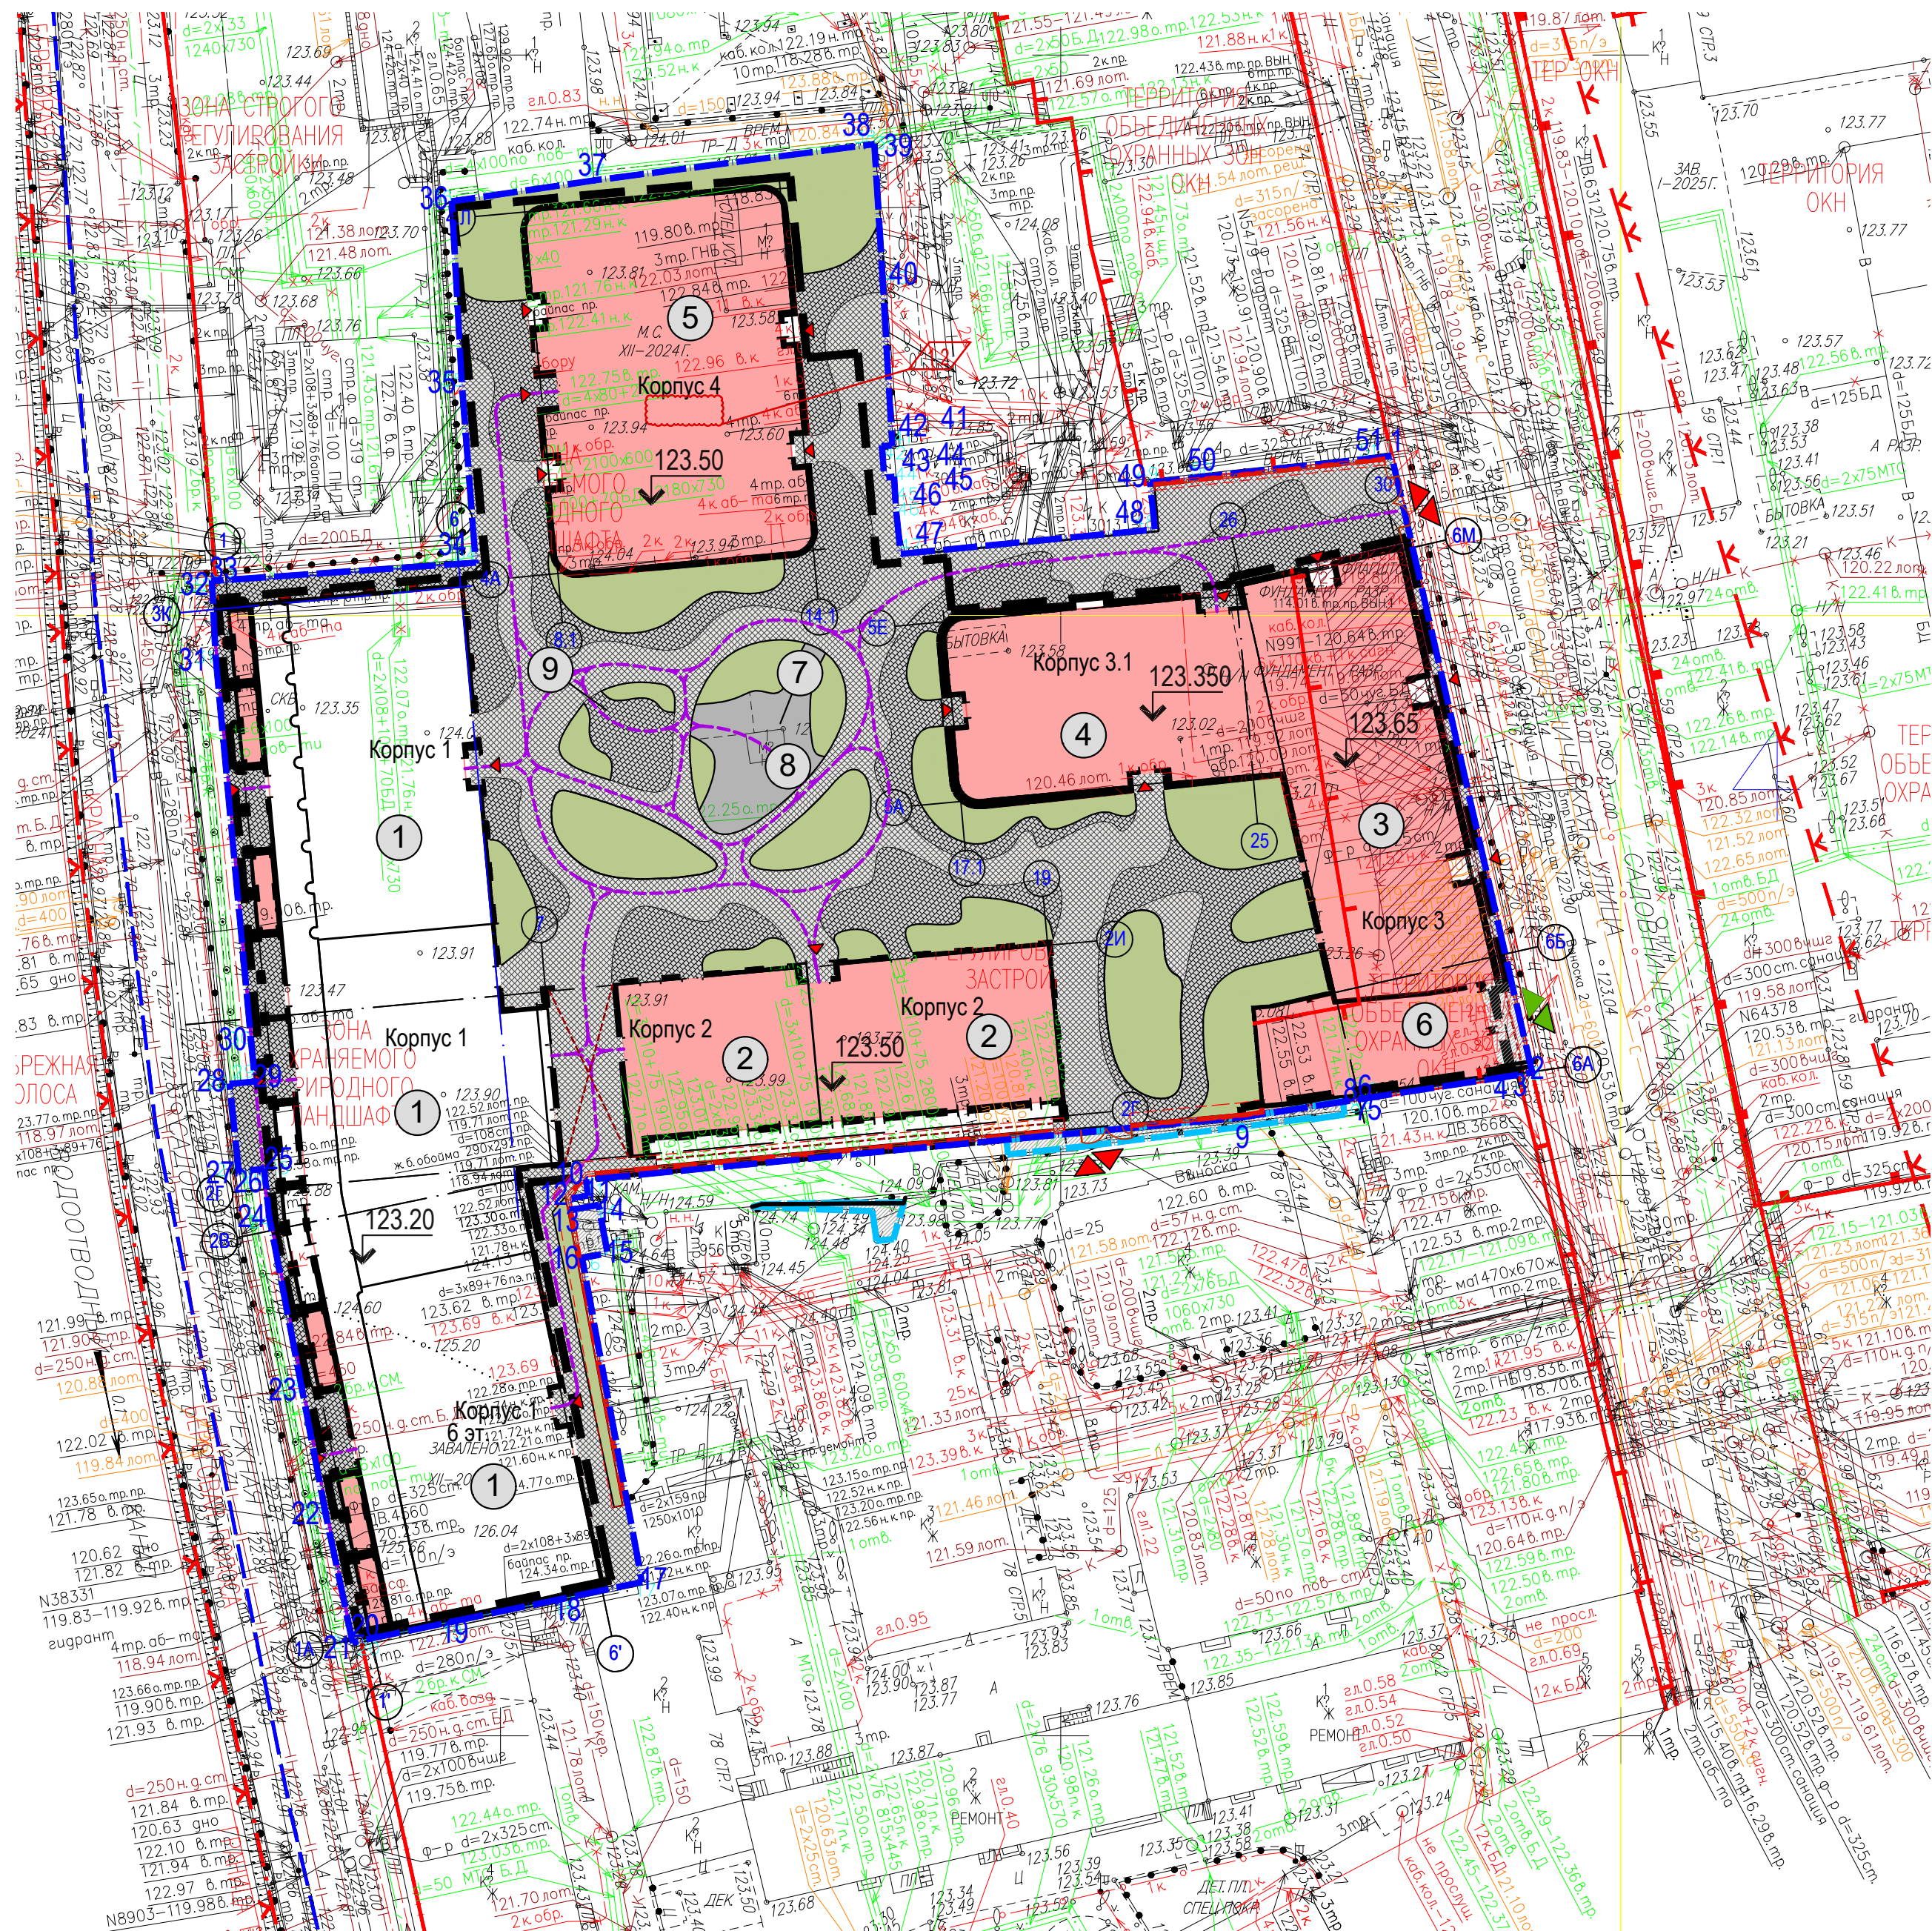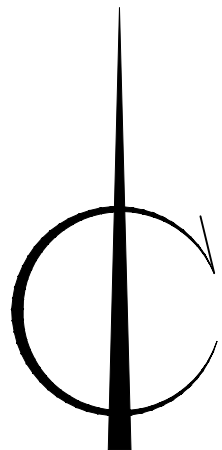

3/6480-24-ИГДИ-Г
в 4-х частях

СХЕМА РАСПОЛОЖЕНИЯ ЧАСТЕЙ

СХЕМА РАСПОЛОЖЕНИЯ ЧАСТЕЙ

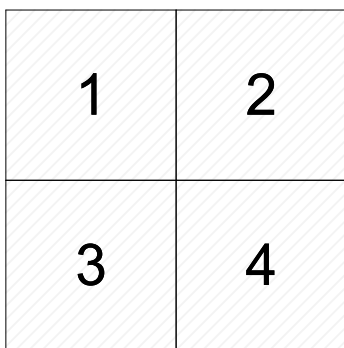

Экспликация зданий и сооружений

No п/п	Наименование	Примечание
Здания и сооружения		
1	Корпус №1	Проектируемый
2	Корпус №2	Проектируемый
3	Корпус №3	Реконструируемый
4	Корпус №3.1	Проектируемый
5	Корпус №4	Проектируемый
6	Въезд/выезд в подземную автостоянку (рампа)	Проектируемый
7	Детская площадка	Проектируемая
8	Спортивная площадка	Проектируемая
9	Площадка для отдыха	Проектируемая

Условные обозначения

- граница проектирования по ГПЗУ № Р-77-4-53-3-76-2025-01998-0 от 14.03.2025
- граница благоустройства за границами проектируемого участка
- проектируемая подземная автостоянка
- проектируемое здание
- нависающая часть здания
- реконструируемое здание
- сносимые здания
- проектируемый газон
- проектируемый проезд
- въезд-выезд в подземный parking
- вход в жилые помещения
- въезд-выезд на территорию пожарных машин и спецтехники
- проектируемое ограждение
- проектируемые ворота/калитка
- проектируемая подпорная стенка
- грязезащитная решетка/тактильная плитка усеченный конус по ГОСТ Р 52875-2018
- пути движения маломобильных групп населения

Условные обозначения линий градостроительного регулирования

границы территории общего пользования	границы несамоулаживаемых территорий	границы зон регулирования застройки и комплексной застройки	границы зон охраны объектов культурного наследия
границы зон охраны объектов культурного наследия	
ЛИНИИ ГРАДОСТРОИТЕЛЬНОГО РЕГУЛИРОВАНИЯ НАНЕСЕНЫ ПО СОСТОЯНИЮ НА 23.01.23

ПРОЕКТИРОВАНИЕ ВЫПОЛНИТЬ В УВЯЗКЕ С СУЩЕСТВУЮЩИМИ ОТМЕТКАМИ

По вопросам несоответствия планового положения подземных коммуникаций обращаться по тел. (499)257-09-11 (доб.51-43)

М 1:500, высота сечения рельефа 0.5м

система координат: Московская; система высот: Московская

Изм.	Нол.уч.	Лист	№ док.	Подпись	Дата	Наименование объекта: «Жилой комплекс» по адресу: г. Москва, ЦАО, ул. Садовническая, вл. 76/71	Заказчик: ООО "СЗ Балугэйст"	Стадия	Лист	Листов
Разработал	Беленко Г. И.	30.01.25				Местоположение (адрес) объекта: г. Москва, внутригородское муниципальное образование Замоскворечье, ул. Садовническая, вл. 76/71	Номенклатура: А-IX-09-16	И	1	4
Проверил	Воронова О. А.	30.01.25								
ЛПР (Н.д.п.)	Невразина А. А.	30.01.25								
Н.контр.	Седова А. М.	30.01.25								
ИНЖЕНЕРНО-ТОПОГРАФИЧЕСКИЙ ПЛАН (М 1:500)							МОСКОМАРХИТЕКТУРА © ГБУ "Мосгоргеотрест"			

Изм.	Нол.уч.	Лист	№ док.	Подпись	Дата	Наименование объекта: «Жилой комплекс» по адресу: г. Москва, ЦАО, ул. Садовническая, вл. 76/71	Заказчик: ООО "СЗ Балугэйст"	Стадия	Лист	Листов
Разработал	Беленко Г. И.	30.01.25				Местоположение (адрес) объекта: г. Москва, внутригородское муниципальное образование Замоскворечье, ул. Садовническая, вл. 76/71	Номенклатура: А-VIII-09-04	И	3	4
Проверил	Воронова О. А.	30.01.25								
ЛПР (Н.д.п.)	Невразина А. А.	30.01.25								
Н.контр.	Седова А. М.	30.01.25								
ИНЖЕНЕРНО-ТОПОГРАФИЧЕСКИЙ ПЛАН (М 1:500)							МОСКОМАРХИТЕКТУРА © ГБУ "Мосгоргеотрест"			

Изм.	Нол.уч.	Лист	№ док.	Подпись	Дата	Наименование объекта: «Жилой комплекс» по адресу: г. Москва, ЦАО, ул. Садовническая, вл. 76/71	Заказчик: ООО "СЗ Балугэйст"	Стадия	Лист	Листов
Разработал	Беленко Г. И.	30.01.25				Местоположение (адрес) объекта: г. Москва, внутригородское муниципальное образование Замоскворечье, ул. Садовническая, вл. 76/71	Номенклатура: А-IX-10-13	И	2	4
Проверил	Воронова О. А.	30.01.25								
ЛПР (Н.д.п.)	Невразина А. А.	30.01.25								
Н.контр.	Седова А. М.	30.01.25								
ИНЖЕНЕРНО-ТОПОГРАФИЧЕСКИЙ ПЛАН (М 1:500)							МОСКОМАРХИТЕКТУРА © ГБУ "Мосгоргеотрест"			


Изм.	Нол.уч.	Лист	№ док.	Подпись	Дата	Наименование объекта: «Жилой комплекс» по адресу: г. Москва, ЦАО, ул. Садовническая, вл. 76/71	Заказчик: ООО "СЗ Балугэйст"	Стадия	Лист	Листов
Разработал	Беленко Г. И.	30.01.25				Местоположение (адрес) объекта: г. Москва, внутригородское муниципальное образование Замоскворечье, ул. Садовническая, вл. 76/71	Номенклатура: А-VIII-10-01	И	4	4
Проверил	Воронова О. А.	30.01.25								
ЛПР (Н.д.п.)	Невразина А. А.	30.01.25								
Н.контр.	Седова А. М.	30.01.25								
ИНЖЕНЕРНО-ТОПОГРАФИЧЕСКИЙ ПЛАН (М 1:500)							МОСКОМАРХИТЕКТУРА © ГБУ "Мосгоргеотрест"			

Генеральный план выполнен на топографо-геодезическом плане смонтированном в электронном виде из фрагментов заказа №3/5624-22 от 02.11.2022 г. выданных ГБУ "Мосгоргеотрест" и являющихся их точной копией.

Гл. архитектор проекта М. Станинич

0.000=123.20

Изм.	Коп.уч.	Лист	№ док.	Подпись	Дата	"Жилой комплекс", расположенный по адресу: г. Москва, ЦАО, Садовническая ул., вл. 76/71				
Разработал	Зиновьева	11.25				Схема планировочной организации земельного участка	Стадия	Лист	Листов	
Проверил	Усанов	11.25					П	1		
ГАП	Станинич	11.25								
Рук. проекта	Штапатович	11.25				Схема планировочной организации земельного участка с указанием путей перемещения МГН. М 1:500	000"МБ-Проект бюро"			
Н. контр.	Боснич	11.25								

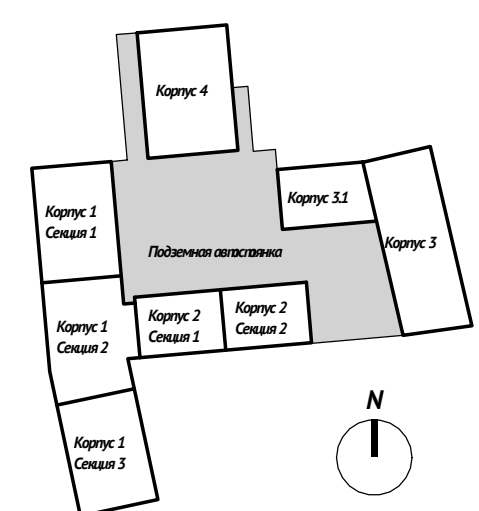

						АА/БЗ-03-ДСЗ – ОДИ			
						Жилой комплекс, расположенный по адресу: г. Москва, ЦАО, Садовническая ул., д. 16/171			
Изм.	Колыч	Лист	№ док.	Подп.	Дата	Мероприятия по обеспечению доступности инвалидов.	Стандия	Лист	Листов
Разработал	Зиновьева	Зиновьева	11.25				П	2	
Проверил	Исачков	Исачков	11.25						
ГАП	Степачич	Степачич	11.25						
Рук.проекта	Шталамович	Шталамович	11.25						
Уполн. контр.	Басич	Басич	11.25			План первого подземного этажа на отм. –6,000. Схема путей перемещения и эвакуации МГН. М1 200.	000"М-Проект Эксп"		

Экспликация МОП 1 этажа (корпус 1)

Номер помещения	Наименование	Площадь, м²	Категория пом.
-----------------	--------------	-------------	----------------

Секция 1

101.1	Лестничная клетка /Л1.1	7,51	
101.1n	Лестничная клетка /Лп1.1	13,28	
101.2	Вестибюль	71,89	
101.3	ПУИ	3,10	
101.4	Колясочная	9,60	
101.5	Универсальный санузел	5,20	

Секция 2

101.6	Лестничная клетка /Л1.2	20,49	
101.7	Вестибюль	166,71	
101.8	ПУИ	2,95	
101.9	Колясочная	15,95	
101.10	Универсальный санузел	5,05	
101.11	Помещение хранения уличного инвентаря	9,15	
101.12	Диспетчерская	43,36	
101.13	Санузел диспетчерской	2,75	
101.14	Служебное помещение	4,59	

Секция 3

101.30	Лестничная клетка /Л1.3	7,51	
101.30n	Лестничная клетка /Лп1.3	13,28	
101.31	Вестибюль	81,84	
101.32	ПУИ	3,10	
101.33	Колясочная	9,66	
101.34	Универсальный санузел	5,20	

502,17

Экспликация МОП 1 этажа (корпус 2)

Номер помещения	Наименование	Площадь, м²	Категория пом.
-----------------	--------------	-------------	----------------

Секция 1

201.1	Лестничная клетка /Л2.1	13,16	
201.1n	Лестничная клетка /Лп2.1	5,78	
201.2	Вестибюль	110,83	
201.3	Колясочная	7,18	
201.4	Универсальный санузел	5,99	
201.5	ПУИ	4,24	
201.6	Лестничная клетка /Л2.2	8,16	
201.6n	Лестничная клетка /Лп2.2	10,91	

166,25

Экспликация помещений общего назначения (корпус 1)

Номер помещения	Наименование	Площадь, м²	Категория пом.
-----------------	--------------	-------------	----------------

Секция 1

101.35	БКТ(Офисные помещения)	150,23	
101.36	ПУИ	4,15	
101.37	Универсальный санузел	7,25	

Секция 2


101.15	БКТ(Офисные помещения)	124,67	
101.16	ПУИ	3,05	
101.17	Универсальный санузел	5,41	
101.18	Тренажерный зал	82,65	
101.19	Раздевалка	7,98	
101.20	Душевая	2,62	
101.21	С/у	2,25	
101.22	Раздевалка	5,64	
101.23	С/у	2,19	
101.24	Душевая	1,92	
101.25	Салон красоты	39,51	
101.26	Салон красоты	17,76	
101.27	С/у	3,30	
101.28	С/у персонала	2,61	
101.29	Помещение для досуговых занятий	29,32	

492,51



УСЛОВНЫЕ ОБОЗНАЧЕНИЯ:

- Путь эвакуации малоомобильных групп населения
- Путь движения малоомобильных групп населения
- Лифт, доступный для МГН, а так же для транспортировки МГН сотрудниками пожарных подразделений
- Зоны, доступные для МГН всех групп в МОП
- Зоны, доступные для МГН в помещениях общего назначения (ПОН)
- Санузлы, приспособленные для МГН и оборудованные тревожной кнопкой

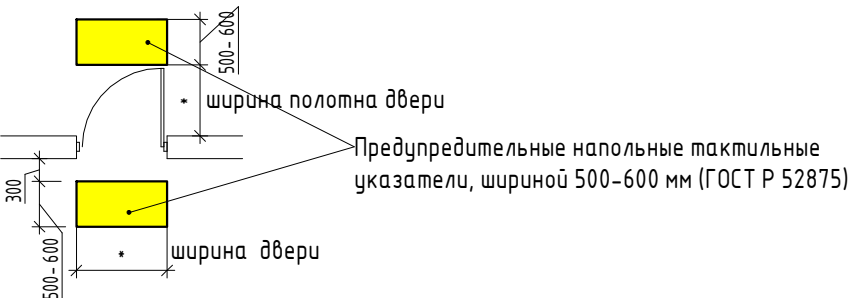

+0.000=123.200

АА/БЗ-03-ДС - ОДИ

"Жилой комплекс", расположенный по адресу: г. Москва, ЦАО, Садовническая ул., вл. 76/71

Мероприятия по обеспечению доступности инвалидов.

Корпуса 1, 2. План 1 этажа. Схема путей перемещения и эвакуации МГН. М 1_200.

ООО "МБ-Проект бюро"

информация
об объекте
работы

Экспликация МОП 2 этажа (корпус 1)			
Номер помещения	Наименование	Площадь, м²	Категория пом.
Секция 1			
102.1	Лестничная клетка Л1.1	22,23	
102.2	Коридор	35,03	
Секция 2			
102.3	Лестничная клетка Л1.2	22,10	
102.4	Коридор	45,22	
Секция 3			
102.5	Лестничная клетка Л1.3	22,23	
102.6	Коридор	47,00	
		193,81	

Экспликация МОП 2 этажа (корпус 2)			
Номер помещения	Наименование	Площадь, м²	Категория пом.
Секция 1			
202.1	Лестничная клетка Л2.1	20,18	
202.2	Коридор	18,51	
Секция 2			
202.3	Лестничная клетка Л2.2	20,18	
202.4	Коридор	18,09	
		76,96	



УСЛОВНЫЕ ОБОЗНАЧЕНИЯ:

- Путь эвакуации маломобильных групп населения
- Путь движения маломобильных групп населения
- Лифт, доступный для МГН, а также для транспортировки МГН сотрудниками пожарных подразделений
- Зоны, доступные для МГН всех групп в МОП
- Зона безопасности МГН

ПРИМЕЧАНИЕ:
1. В качестве типового решения представлен план 2 этажа.

+0.000=123.200


АА/БЗ-03-ДСЗ - ОДИ					
"Жилой комплекс", расположенный по адресу: г. Москва, ЦАО, Садовническая ул., вл. 76/71					
Изм.	Колуч	Лист	№ док.	Подп.	Дата
Разработал	Зинovieва	Зинovieва	11.25		
Проверил	Усманов	Усманов	11.25		
Г.АП	Станиш	Станиш	11.25		
Рук.проекта	Шталматович	Шталматович	11.25		
Норм. контр.	Боснич	Боснич	11.25		
Мероприятия по обеспечению доступности инвалидов.				Стадия	Лист
Корпуса 1, 2. План 2-4 этажей. Схема путей перемещения и эвакуации МГН. М.1_200.				4	Листов
ООО "МБ-Проект бюро"				Исполнитель: [подпись]	

Экспликация МОП 5 этажа (корпус 1)

Номер помещения	Наименование	Площадь, м²	Категория пом.
Секция 1			
105.1	Лестничная клетка Л1.1	22,23	
105.2	Коридор	31,25	
Секция 2			
105.3	Лестничная клетка Л1.2	22,10	
105.4	Коридор	31,25	
Секция 3			
105.5	Коридор	30,20	
105.6	Лестничная клетка Л1.3	22,23	
		159,26	

Экспликация МОП 5 этажа (корпус 2)

Номер помещения	Наименование	Площадь, м²	Категория пом.
Секция 1			
205.1	Лестничная клетка Л2.1	20,18	
205.2	Коридор	18,51	
Секция 2			
205.3	Лестничная клетка Л2.2	20,18	
205.4	Коридор	18,09	
		76,96	

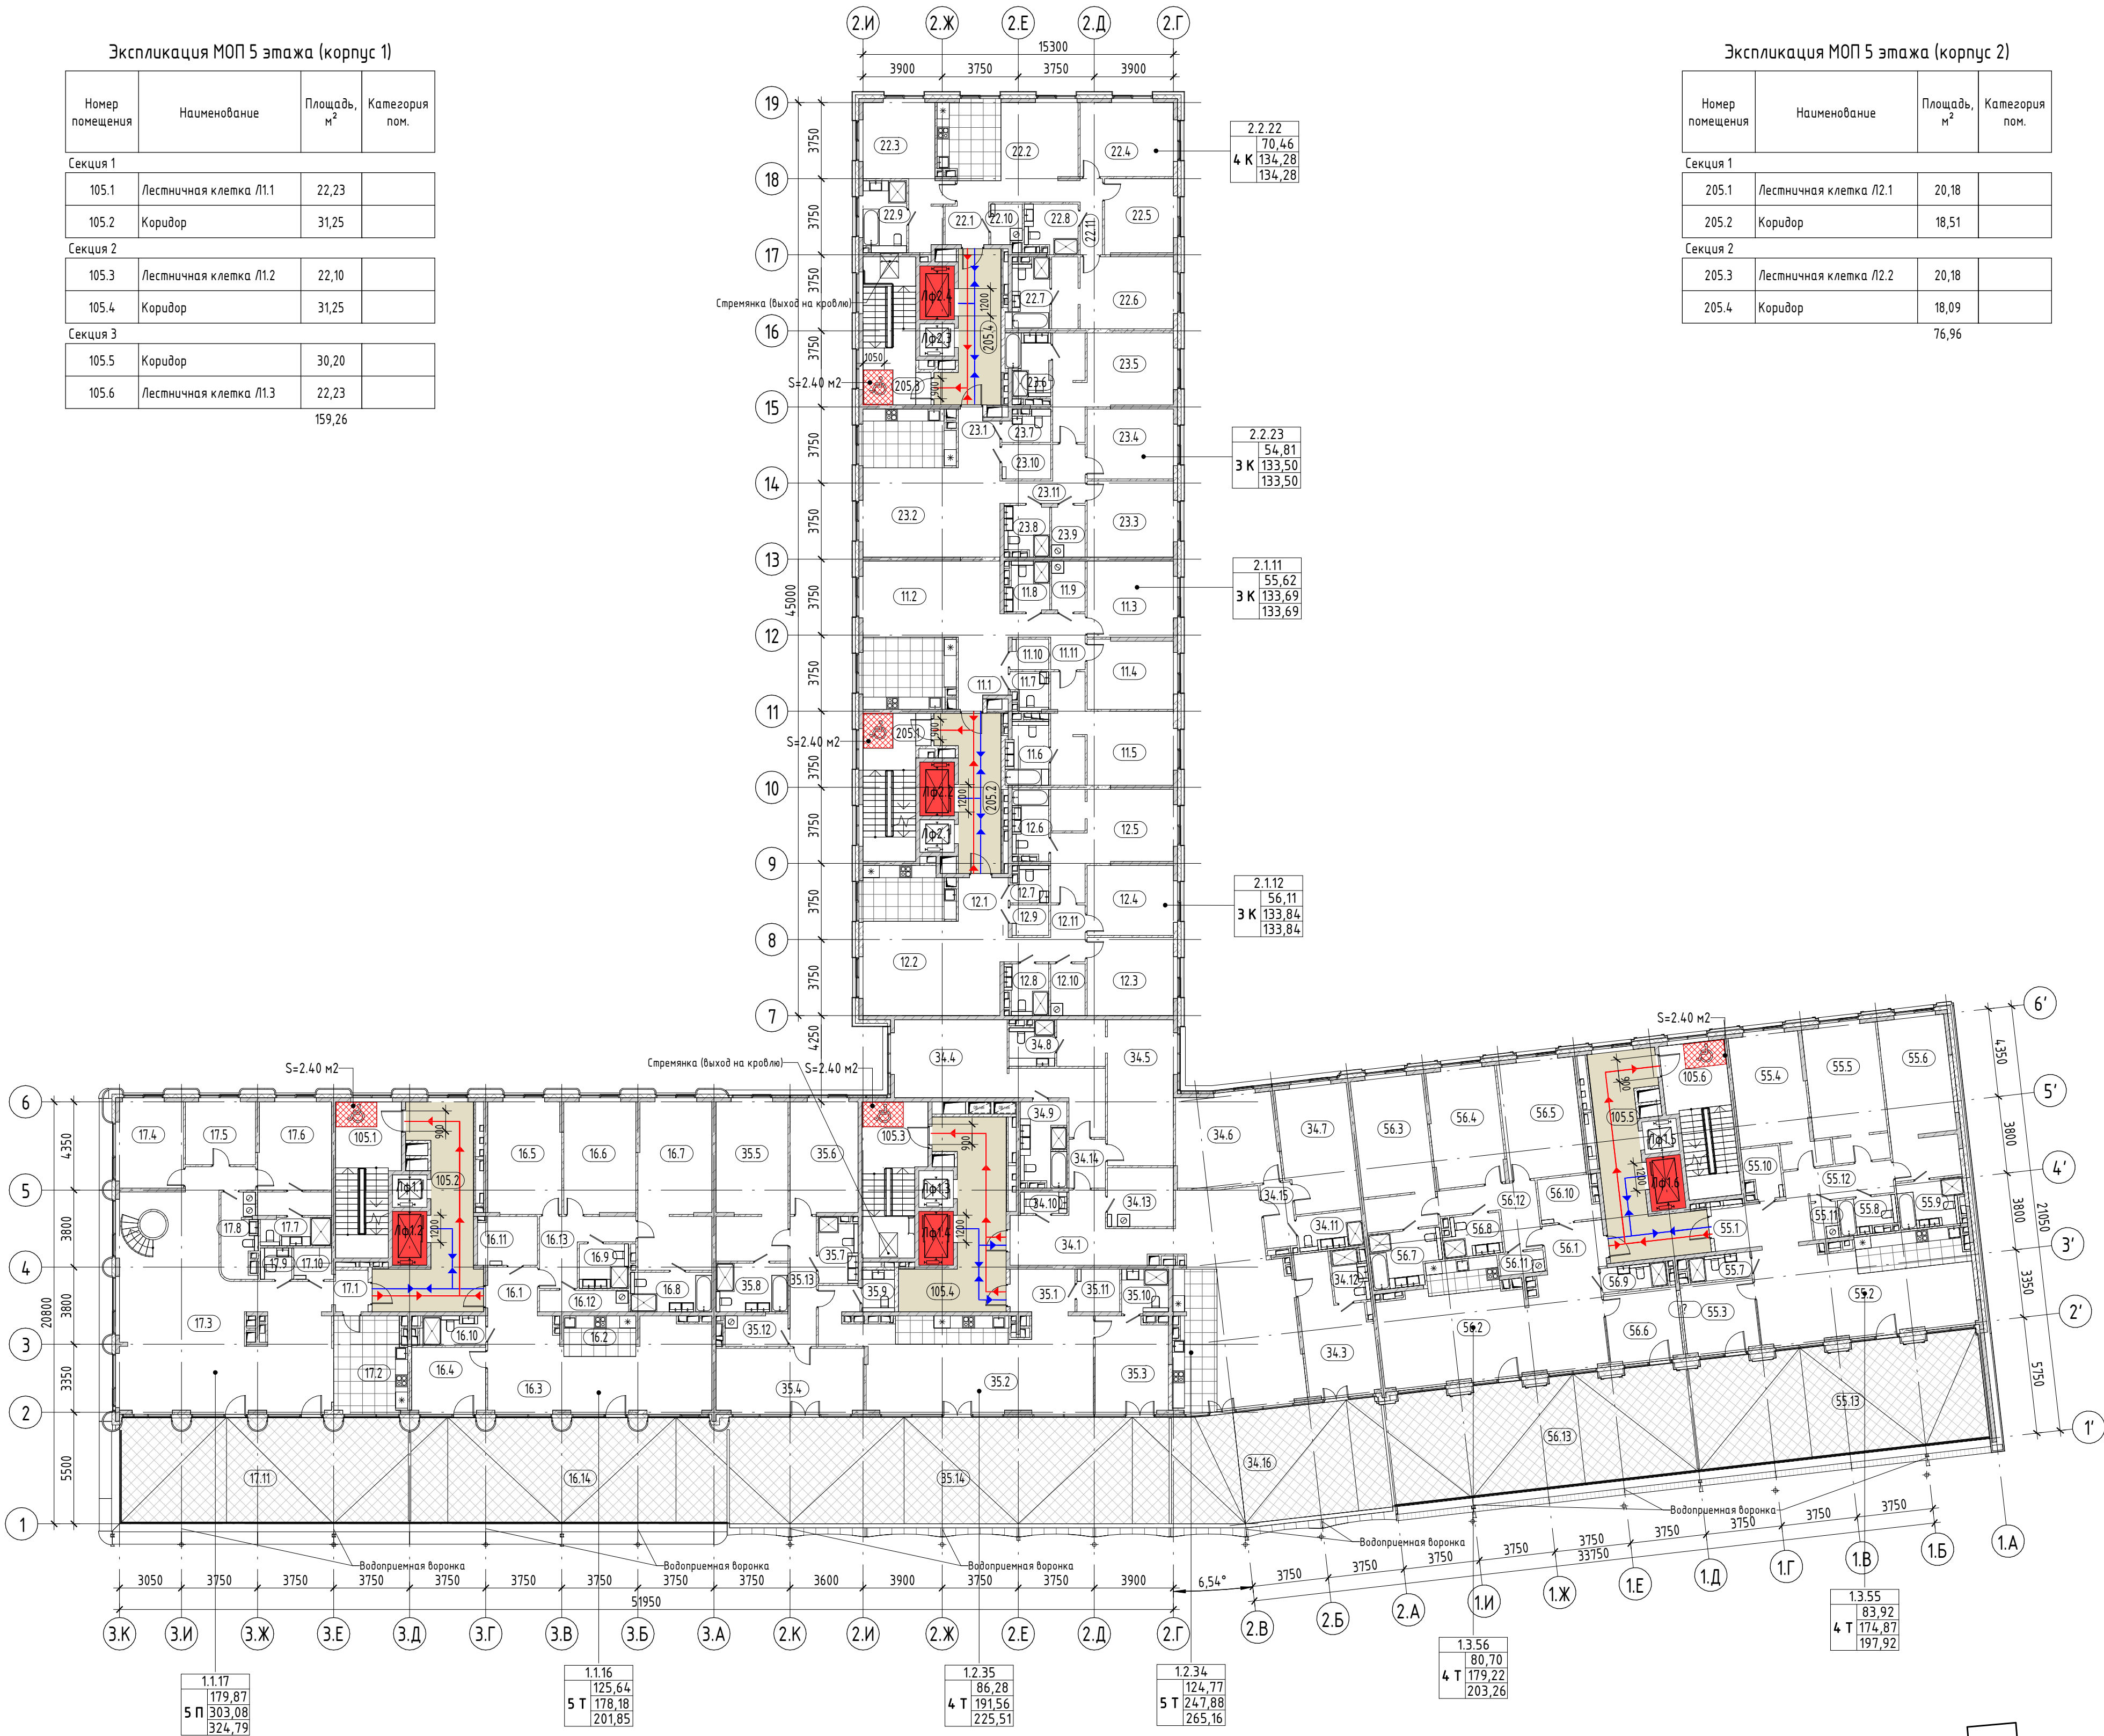

УСЛОВНЫЕ ОБОЗНАЧЕНИЯ:

- Пути эвакуации маломобильных групп населения
- Пути движения маломобильных групп населения
- Лифт, доступный для МГН, а также для транспортировки МГН сотрудниками пожарных подразделений
- Зоны, доступные для МГН всех групп в МОП
- Зона безопасности МГН

+0.000=123.200

АА/БЗ-03-ДСЗ - ОДИ				
"Жилой комплекс", расположенный по адресу: г. Москва, ЦАО, Садовническая ул., вл. 76/71				
Изм.	Колуч.	Лист	№ док.	Подп.
Разработал	Зиновьева	Зиновьева	11.25	
Проверил	Усманов	Усманов	11.25	
Г.АП	Станиш	Станиш	11.25	
Рук.проекта	Шталматович	Шталматович	11.25	
Норм. контр.	Боснич	Боснич	11.25	
Мероприятия по обеспечению доступности инвалидов.			Стадия	Лист
Корпуса 1, 2. План 5 этажа. Схема путей перемещения и эвакуации МГН М 1_200.			5	Листов
000"МБ-Проект бюро"			Исполнитель: "Бюро" "МБ-Проект"	


Экспликация МОП 6 этажа (корпус 1)

Номер помещения	Наименование	Площадь, м²	Категория пом.
Секция 1			
106.1	Лестничная клетка Л1.1	22,23	
106.2	Коридор	31,25	
Секция 3			
106.3	Лестничная клетка Л1.3	22,23	
106.4	Коридор	30,20	
		105,91	

Экспликация МОП 6 этажа (корпус 2)


Номер помещения	Наименование	Площадь, м²	Категория пом.
Секция 1			
206.1	Лестничная клетка Л2.1	20,18	
206.2	Коридор	18,51	
		38,69	



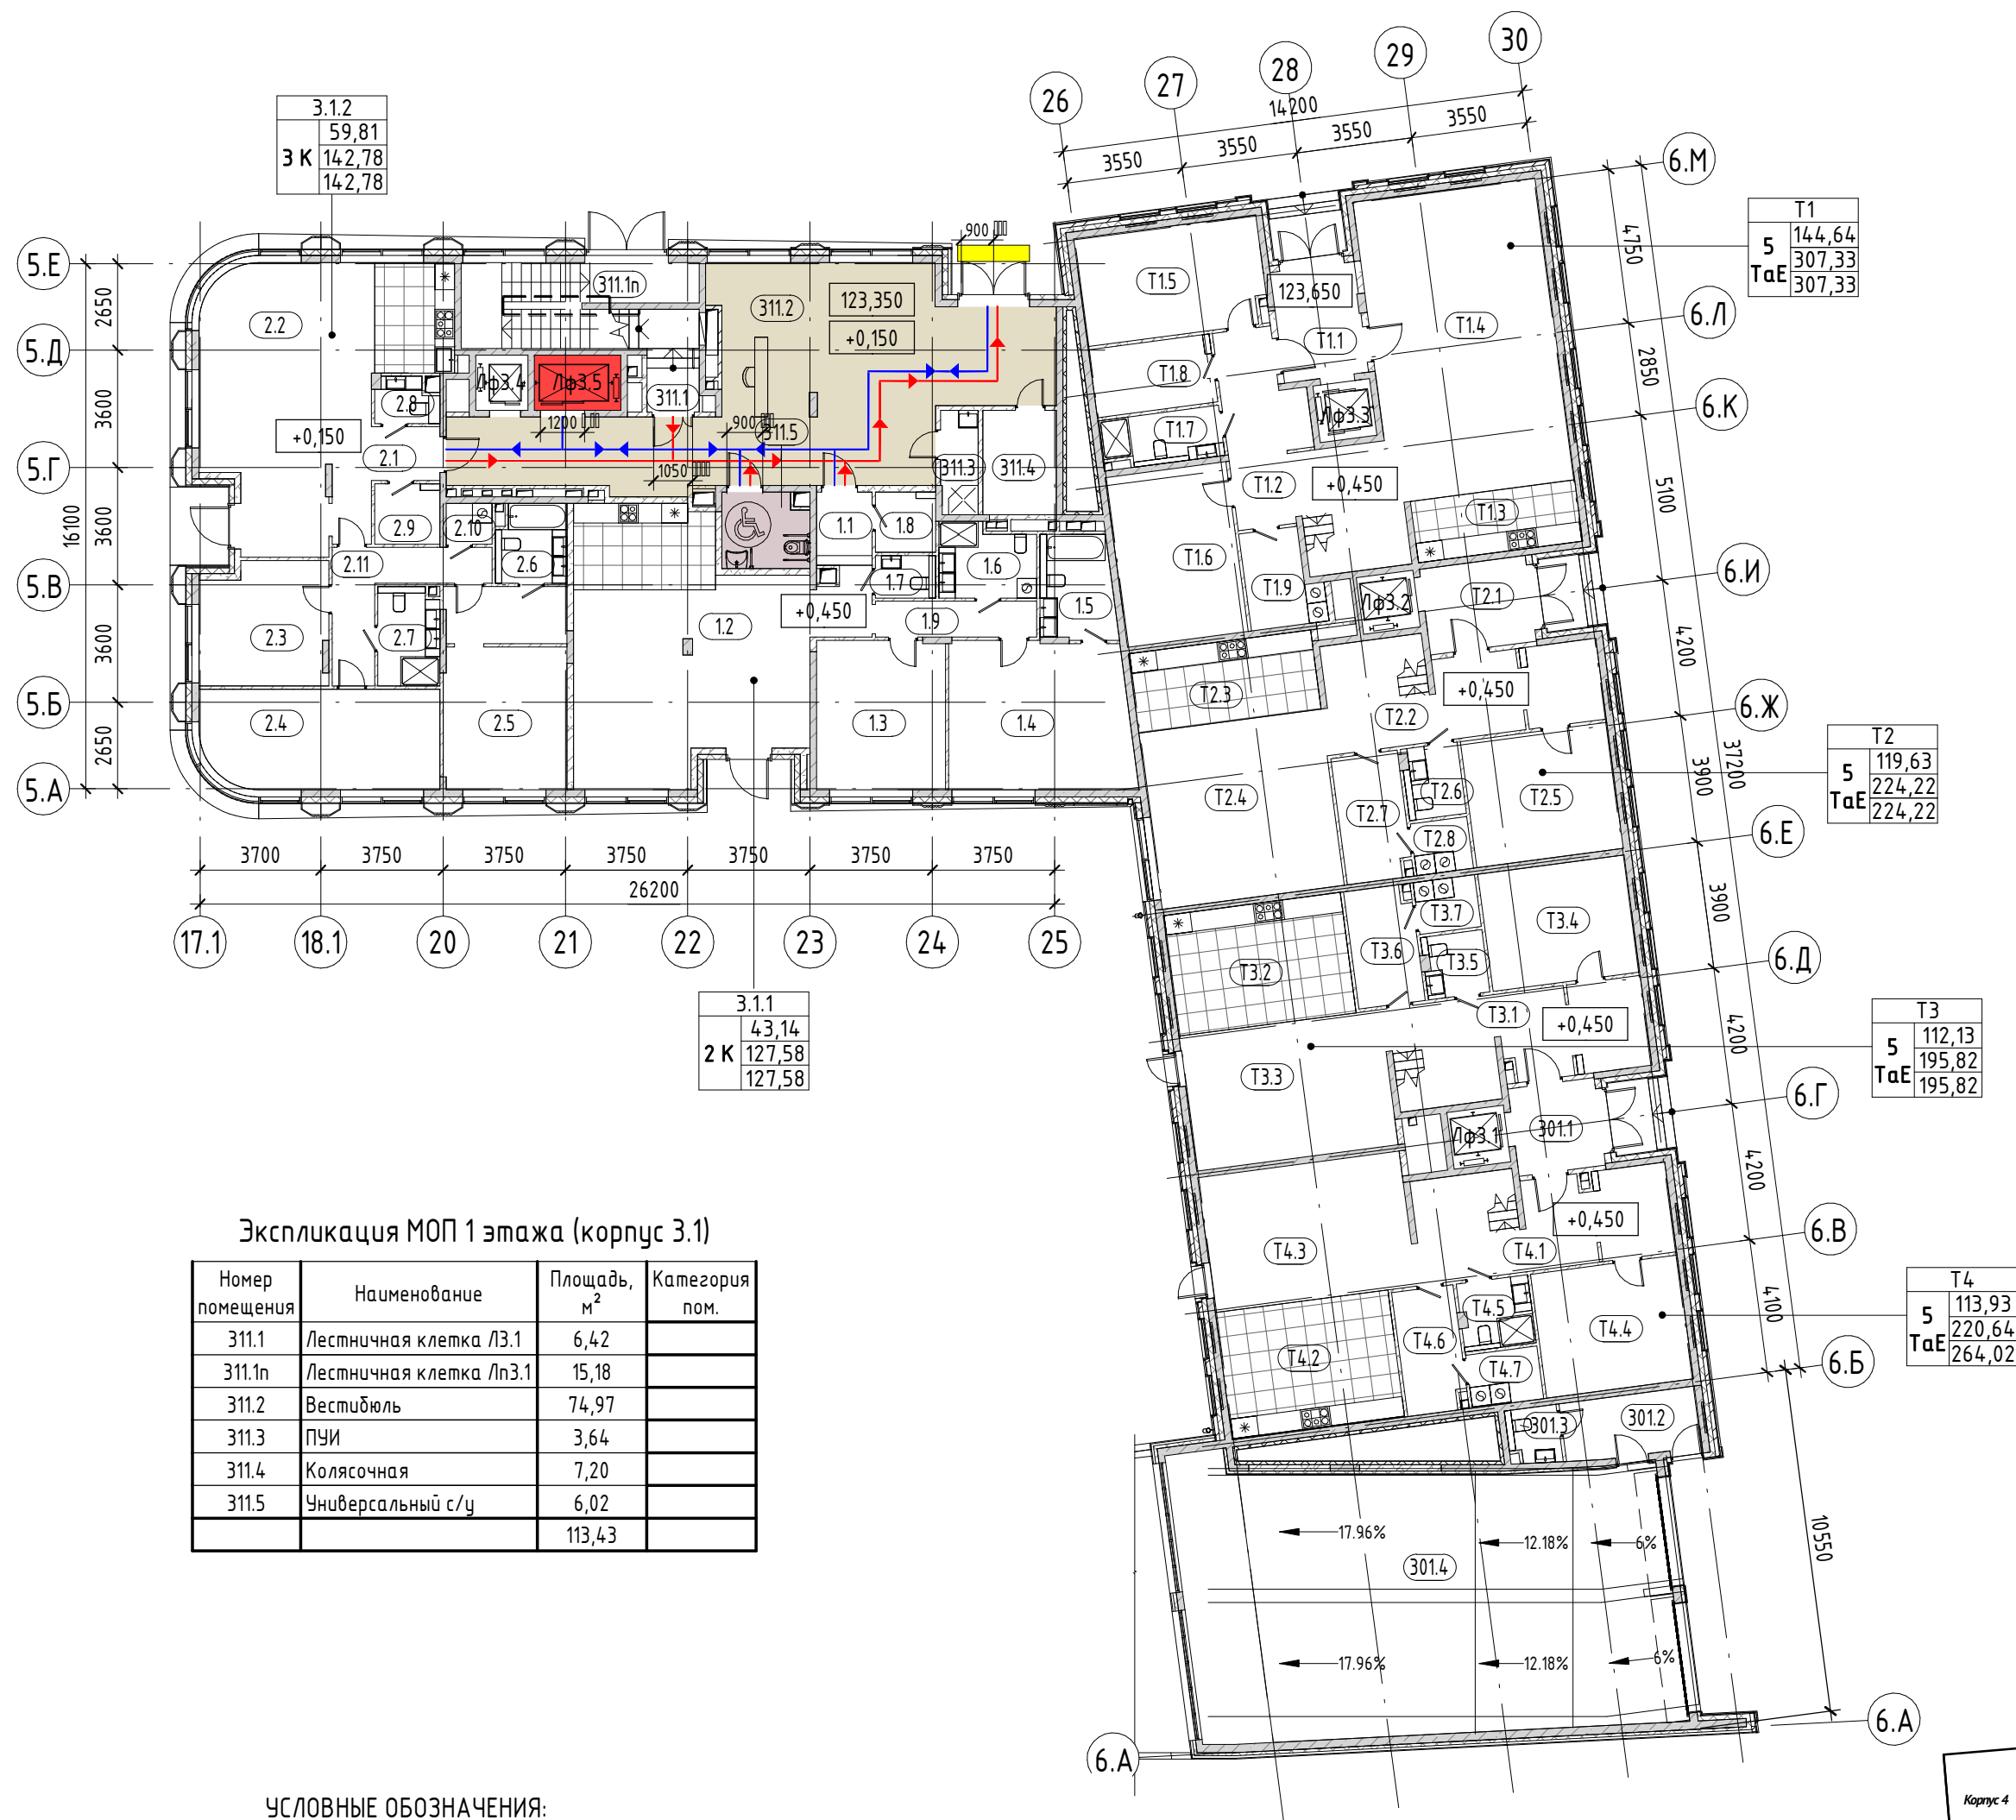

АА/БЗ-03-ДСЗ - ОДИ					
"Жилой комплекс", расположенный по адресу: г. Москва, ЦАО, Садовническая ул., вл. 76/71					
Изм.	Кол.уч.	Лист	№ док.	Подп.	Дата
Разработал	Зиновьева	Зиновьева	11.25		
Проверил	Усманов	Усманов	11.25		
ГАП	Станишч	Станишч	11.25		
Рук.проекта	Шаломатович	Шаломатович	11.25		
Норм. контр.	Боснич	Боснич	11.25		
Мероприятия по обеспечению доступности инвалидов.				Стадия	Лист
				П	7
Корпуса 3, 3.1. План 1 этажа. Схема путей перемещения и эвакуации МГН. М 1_200.				ООО "МБ-Проект Бюро"	
				МБ-проект бюро одобрено 14.12.2024	

Инв. № подл.	Подп. и дата	Взам. инв. №

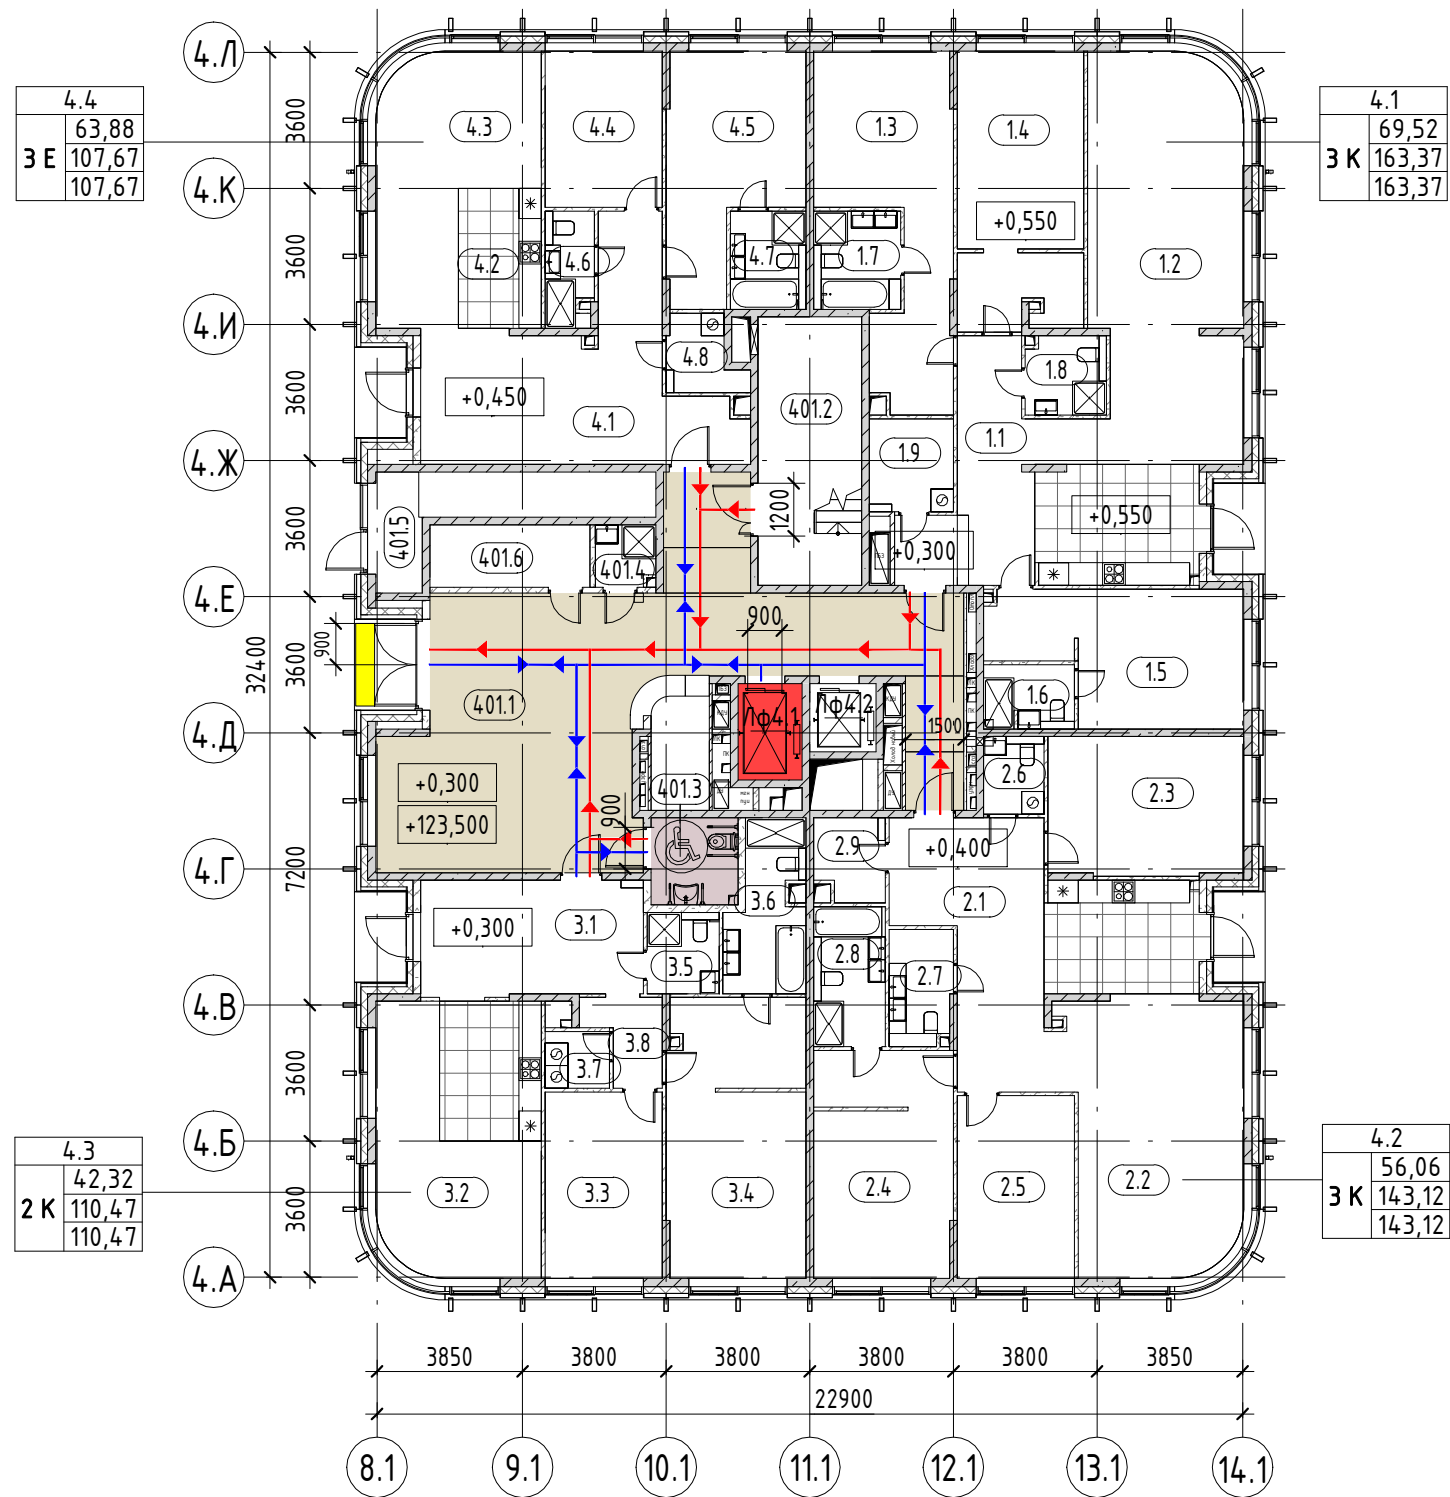


Экспликация МОП 1 этажа

Номер помещения	Наименование	Площадь, м²	Категория помещения
401.1	Вестибюль	83,39	
401.2	Лестничная клетка Л4	19,45	
401.3	Универсальный санузел	5,29	
401.4	ПУИ	2,53	
401.5	Лестничная клетка Лп4	3,94	
401.6	Колясочная	6,98	
		121,58	

УСЛОВНЫЕ ОБОЗНАЧЕНИЯ:

- ← Пути эвакуации маломобильных групп населения
- ← Пути движения маломобильных групп населения
- Лифт, доступный для МГН, а так же для транспортировки МГН сотрудниками пожарных подразделений
- Зоны, доступные для МГН всех групп в МОП
- Санузлы, приспособленные для МГН и оборудованные тревожной кнопкой
- Предупредительные напольные тактильные указатели, шириной 500-600 мм (ГОСТ Р 52875)

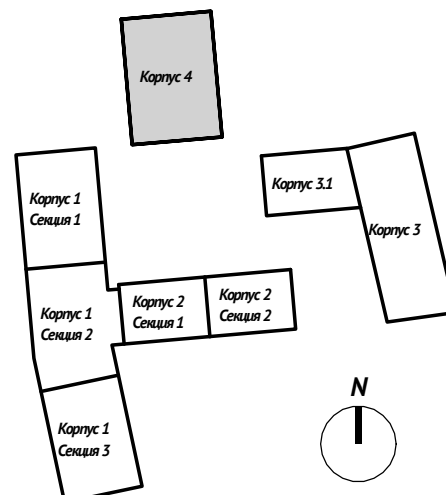


						АА/БЭ-03-ДСЗ - ОДИ			
						"Жилой комплекс", расположенный по адресу: г. Москва, ЦАО, Садовническая ул., вл. 76/71			
Изм.	Кол.уч.	Лист	№ док.	Подп.	Дата	Мероприятия по обеспечению доступности инвалидов.	Стадия	Лист	Листов
Разработал	Зиновьева	Зиновьева	11.25				П	9	
Проверил	Усманов		11.25						
ГАП	Станишч		11.25						
Рук.проекта	Шталматович	BM	11.25			Корпус 4. План 1 этажа. Схема путей перемещения и эвакуации МГН. М 1_200.	000"МБ-Проект бюро" мб-проект бюро оид unisoid-qui		
Норм. контр.	Боснич	ББ	11.25						

Экспликация МОП 2 этажа

Номер помещения	Наименование	Площадь, м ²
402.1	Лифтовый холл ПБЗ	12,95
402.2	Лестничная клетка Л4	17,40
402.3	Коридор	8,86
402.4	Коридор	8,86
		48,07

УСЛОВНЫЕ ОБОЗНАЧЕНИЯ:


- | | |
|---|--|
|  | Пути эвакуации маломобильных групп населения |
|  | Пути движения маломобильных групп населения |
|  | Лифт, доступный для МГН, а также для транспортировки МГН сотрудниками пожарных подразделений |
|  | Зоны, доступные для МГН всех групп в МОП |
|  | Зона безопасности МГН |

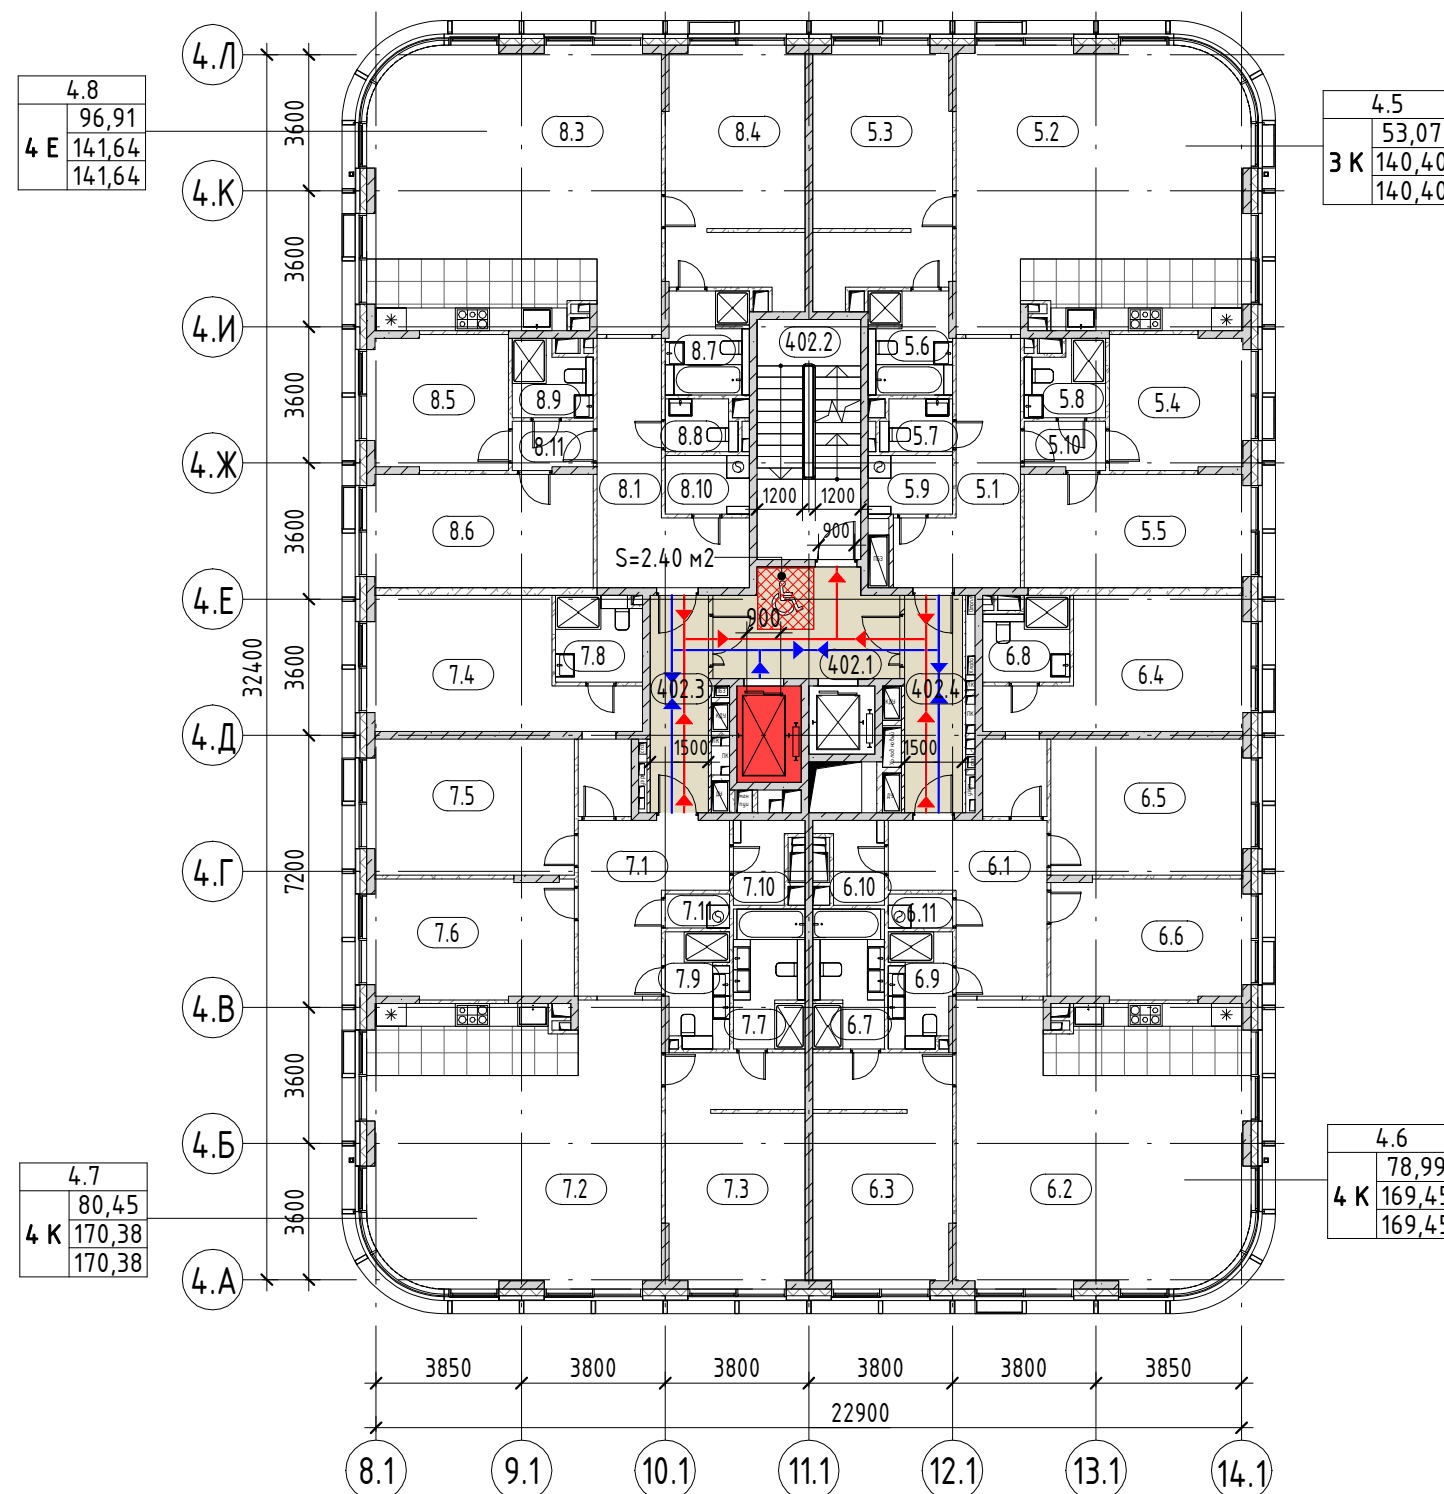

ПРИМЕЧАНИЕ:

1. В качестве типового решения представлен план 2 этажа.

+0.000=123.200

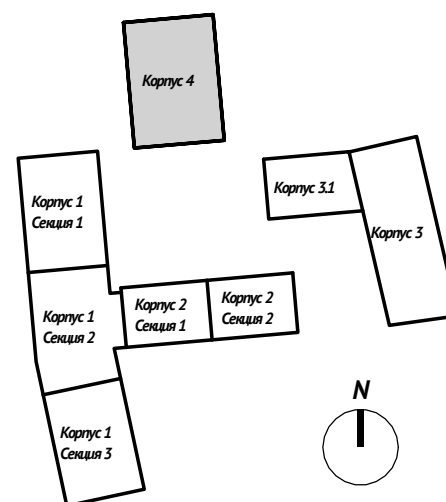

						АА/БЭ-03-ДСЭ - ОДИ			
						"Жилой комплекс", расположенный по адресу: г. Москва, ЦАО, Садовническая ул., в/д 76/71			
Изм.	Кол.уч.	Лист	№ док.	Подп.	Дата				
Разработал	Зиновьева	Зиновьева	11.25			Мероприятия по обеспечению доступности инвалидов.	Стадия	Лист	Листов
Проверил	Усманов	Усманов	11.25				П	10	
ГАП	Станишч	Станишч	11.25						
Рук.проекта	Шталматович	Шталматович	11.25			Корпус 4. План типового этажа. Схема путей перемещения и эвакуации МГН. М 1_200.	000"МБ-Проект дьюр"		мб-проект бюро ооо мб-проект
Норм. контр.	Боснич	Боснич	11.25						

Формат А3А

Инв. № подл.	Подп. и дата	Взам. инв. №