

Проектная организация
"МБ-Проект Бюро"

Заказчик
ООО «Специализированный застройщик Балчуг эстейт»

ЖИЛОЙ КОМПЛЕКС
по адресу:
г. Москва, ЦАО, ул. Садовническая, вл. 76/71

ПРОЕКТНАЯ ДОКУМЕНТАЦИЯ **Корректировка**

Положительные заключения
№77-2-1-3-047721-2024 от 19.08.2024г.
№77-2-1-2-022133-2025 от 23.04.2025г.
№77-2-1-2-032022-2025 от 09.06.2025г.
№77-2-1-3-079426-2025 от 23.12.2025г.

Раздел 5
Сведения об инженерном оборудовании, о сетях
инженерно-технического обеспечения, перечень инженерно-технических
мероприятий, содержание технологических решений
(внутренние инженерные системы)

Подраздел 3
Система водоотведения
Часть 1
Внутренние системы водоотведения

АА/БЭ-03-ДСЗ-ИОС3.1
Корректировка

Главный инженер проекта



Шталматович В.

г. Москва
2026 год

Свидетельство №49-09-6658340247-П-069 от 20 ноября 2015 г.

Заказчик – ООО «МБ-Проект Бюро»

**«Жилой комплекс» расположенный по адресу: г. Москва, ЦАО,
Садовническая ул., вл 76/71**

Проектная документация

Раздел 5

**Сведения об инженерном оборудовании, о сетях
инженерно-технического обеспечения, перечень
инженерно-технических
мероприятий, содержание технологических решений
(внутренние инженерные системы)**

Подраздел 3

Система водоотведения

Часть 1

Внутренние системы водоотведения

АА/БЭ-03-ДСЗ-ИОСЗ.1

Корректировка

Изм.	№ док	Подп.	Дата

Свидетельство №49-09-6658340247-П-069 от 20 ноября 2015 г.

Заказчик – ООО «МБ-Проект Бюро»

**«Жилой комплекс» расположенный по адресу: г. Москва, ЦАО,
Садовническая ул., вл 76/71**

Проектная документация

Раздел 5

**Сведения об инженерном оборудовании, о сетях
инженерно-технического обеспечения, перечень
инженерно-технических
мероприятий, содержание технологических решений
(внутренние инженерные системы)**

Подраздел 3

Система водоотведения

Часть 1

Внутренние системы водоотведения

АА/БЭ-03-ДСЗ-ИОСЗ.1

Корректировка

Директор



В.Б. Сальников

Главный инженер проекта



М.В.Шараева

Изм.	№ док	Подп.	Дата

Заверение проектной документации

Технические решения, принятые в проекте «Жилой комплекс» по адресу:
г. Москва, ЦАО, Садовническая ул., вл. 76/71, соответствуют требованиям экологических, санитарно-гигиенических, противопожарных, строительных норм и правил, действующих на территории Российской Федерации, а также обеспечивают безопасную для жизни и здоровья людей эксплуатацию объекта при их выполнении

Главный инженер проекта



М.В.Шараева

Инв. № подл.	Подп. И дата	Взам. инв. №							Лист
Изм.	Кол.уч.	Лист	№ док.	Подп.	Дата	AA/БЭ-03-ДС3-ИОС3.1			2

"Жилой комплекс" расположенный по адресу: г. Москва, ЦАО, Садовническая ул., вл 76/71»


КОРРЕКТИРОВКА СТАДИИ «ПРОЕКТ»

В соответствии с заданием на корректировку стадии «Проект», была откорректирована проектная документация по перечню локальных изменений, приведенных в таблице основных отличий.

Таблица основных отличий.

№	Ранее разработанные решения ПД, получившие положительное заключение негосударственной экспертизы от 19.08.2024 №77-2-1-3-047721-2024, от 23.04.2025 № 77-2-1-2-022133-2025, от 09.06.2025 № 77-2-1-2-032022-2025	Суть изменения, внесенного в рамках корректировки ПД	Ссылка по внесенным изменениям на состав ПД (Том, часть, страница, лист, корпус/оси/этап/секция)
1		Откорректирована схема систем К1, К2 ниже отм. 0,000	Том 5.3.1. ГЧ л.1-4
2		Добавлена канализационная насосная станция	Том 5.3.1. ГЧ л.3
3		Откорректированы места расположения воронок на террасах	Том 5.3.1. ГЧ л.1-4
4		Добавлен технический чердак	Том 5.3.1. ГЧ л.4
5	Бытовые сточные воды от помещений подземных этажей отводятся с использованием насосных установок типа WILO Hi Drainlift3-37 или аналог. Из помещений ТБО стоки удаляются при помощи установки WILO Drainlift BOX 40/11 или аналог.	Бытовые сточные воды от комнаты водителей и помещения хранения ТБО отводятся с использованием насосной установки типа N-Lift 2E-120/1/1-EM, N= 1.1кВт, U=220v или аналог.	

Взам. инв. №	Подп. и дата	Инв. № подл
--------------	--------------	-------------

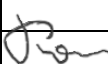Изм.	Кол.уч.	Лист	№ док.	Подп.	Дата
Разраб.		Степанов			12.25
Проверил		Шишкина			12.25
Н.контр.		Костылева			12.25

АА/БЭ-03-ДСЗ-ИОС3.1.ТО					
Пояснительная записка					
				Стадия	Лист
				П	1
				Листов	
				 ИНПАД проектирование обследование зданий навесные фасады	

6

По периметру парковки, для сбора воды после срабатывания системы АУПТ, предусмотрены трапы на -1 этаже и приемки на -2 этаже размерами не менее 1 м³. В этих приемках установлены два дренажных насоса ГНОМ 25-20 Q=25м³/ч, Н=20м (или аналог), без ШУ, с поплавковым выключателем.

В помещениях приточных вент. камер предусмотрены трапы на -1 этаже и приемки на -2 этаже размерами 0,6х0,6х0,6 (h). В этих приемках установлен один дренажный насос ГНОМ 10-10 Q=10м³/ч, Н=10м, (или аналог).

В помещении ИТП на -1 этаже предусмотрен трап и приямок 0,6х0,6х0,8 (h) на -2 этаже (общий для насосной, ИТП) с установкой дренажных насосов Wilo-Drine TMT 32M 113/7,5Si с повышенной температурой перекачиваемой жидкости (до 95°C) (1раб+1рез) с ШУ и комплектом поплавков.

По периметру парковки, для сбора воды после срабатывания системы АУПТ, предусмотрены трапы на -1 этаже и приемки на -2 этаже с суммарным объемом не менее 2 м³. В этих приемках установлены два дренажных насоса NSP 50/400-1.5, N= 1.5кВт, U=3~400v. (1 рабочий, 1 резервный) с поплавковым выключателем.

В помещениях приточных вент. камер предусмотрены трапы на -1 этаже и приемки на -2 этаже. В этих приемках установлен один дренажный насос TMT 32M113/7,5Ci, N= 0,75кВт, U=3~380v, (1 рабочий).

В помещении ИТП на -1 этаже предусмотрен приямок с установкой дренажных насосов Wilo TMT 32M113/7,5Ci N= 0,75кВт, U=3~380v. (1 рабочий, 1 резервный) с поплавковым выключателем.

В помещении насосной АПТ, насосной ХВС и помещении узла ввода на -1 этаже предусмотрен приямок

Взам. инв. №	Подп. и дата	Инв. № подл

Изм.	Кол.уч.	Лист	№ док.	Подп.	Дата

АА/БЭ-03-ДС3-ИОС3.1.ТО

Лист

2

		с установкой дренажных насосов NSP 50/400-1.5, N= 1.5кВт, U=3~400v. (1 рабочий, 1 резервный) с поплавковым выключателем.	
7		Откорректирована Таблица 1. Расчетные показатели водоотведения.	
8		Откорректирована Таблица 2. Ведомости насосного оборудования для отвода дренажных вод.	

Остальные ранее разработанные решения ПД, получившие положительное заключение негосударственной экспертизы №77-2-1-3-047721-2024 от 19.08.2024 г., № 77-2-1-2-022133-2025 от 23.04.2025 г. и № 77-2-1-2-032022-2025 от 09.06.2025 г.

Взам. инв. №	Подп. и дата	Инв. № подл							Лист	
Изм.	Кол.уч.	Лист	№ док.	Подп.	Дата	АА/БЭ-03-ДСЗ-ИОС3.1.ТО				3

Содержание

Общие положения. 2

а) сведения о существующих и проектируемых системах канализации, водоотведения и станциях очистки сточных вод; 4

б) обоснование принятых систем сбора и отвода сточных вод, объема сточных вод, концентраций их загрязнений, способов предварительной очистки, применяемых реагентов, оборудования и аппаратуры; ... 4

в) обоснование принятого порядка сбора, утилизации и захоронения отходов - для объектов производственного назначения; 4

г) описание и обоснование схемы прокладки канализационных трубопроводов, описание участков прокладки напорных трубопроводов (при наличии), условия их прокладки, оборудование, сведения о материале трубопроводов и колодцев, способы их защиты от агрессивного воздействия грунтов и грунтовых вод 4

д) решения в отношении ливневой канализации и расчетного объема дождевых стоков;..... 4

е) решения по сбору и отводу дренажных вод 5

Согласовано		

Взам. инв. №	

Подп. и дата	

Инв. № подл.	

						АА/БЭ-03-ДС3-ИОС3.1.ПЗ		
Изм.	Коп.уч.	Лист	№ док.	Подп.	Дата	Пояснительная записка		
Разраб.	Степанов				12.25			
Проверил	Шишкина				12.25			
Н.контроль	Костылева				12.25			
						Стадия	Лист	Листов
						П	1	
						 ИНПАД проектирование обследование зданий навесные фасады		

а) сведения о существующих и проектируемых системах канализации, водоотведения и станциях очистки сточных вод

Остальные ранее разработанные решения ПД, получившие положительное заключение негосударственной экспертизы №77-2-1-3-047721-2024 от 19.08.2024 г., № 77-2-1-2-022133-2025 от 23.04.2025 г. и № 77-2-1-2-032022-2025 от 09.06.2025 г., остались без изменений.

б) обоснование принятых систем сбора и отвода сточных вод, объема сточных вод, концентраций их загрязнений, способов предварительной очистки, применяемых реагентов, оборудования и аппаратуры

5,7

Бытовые сточные воды от комнаты водителей и помещения хранения ТБО отводятся с использованием насосной установки типа N-Lift 2E-120/1/1-ЕМ, N= 1.1кВт, U=220v или аналог.

Расчетные расходы хозяйственно-бытовых вод рассчитаны и сведены в таблицу 1.

Таблица 1. Расчетные показатели водоотведения.

Наименование системы	Расчетный расход стоков				Примечание
	м³/сут	м³/ч	л/с	При пожаре, л/с	
Общий расход					
Общий расход стоков на весь дом	121,33	12,24	4,81+1,6=6,41		
Жилая часть					
Общий расход стоков	115,56	12,22	4,77+1,6=6,37		
Административные помещения (диспетчерская)+тренажерный зал+ салон красоты					
Общий расход стоков	1,04	0,58	0,43+1,6=2,03		

в) обоснование принятого порядка сбора, утилизации и захоронения отходов - для объектов производственного назначения

Остальные ранее разработанные решения ПД, получившие положительное заключение негосударственной экспертизы №77-2-1-3-047721-2024 от 19.08.2024 г., № 77-2-1-2-022133-2025 от 23.04.2025 г. и № 77-2-1-2-032022-2025 от 09.06.2025 г., остались без изменений.

г) описание и обоснование схемы прокладки канализационных трубопроводов, описание участков прокладки напорных трубопроводов (при наличии), условия их прокладки, оборудование, сведения о материале трубопроводов и колодцев, способы их защиты от агрессивного воздействия грунтов и грунтовых вод

Остальные ранее разработанные решения ПД, получившие положительное заключение негосударственной экспертизы №77-2-1-3-047721-2024 от 19.08.2024 г., № 77-2-1-2-022133-2025 от 23.04.2025 г. и № 77-2-1-2-032022-2025 от 09.06.2025 г., остались без изменений.

д) решения в отношении ливневой канализации и расчетного объема дождевых стоков

Остальные ранее разработанные решения ПД, получившие положительное заключение негосударственной экспертизы №77-2-1-3-047721-2024 от 19.08.2024 г., № 77-2-1-2-022133-2025 от 23.04.2025 г. и № 77-2-1-2-032022-2025 от 09.06.2025 г., остались без изменений.

Взам. инв. №	
Подп. и дата	
Инв. № подл.	

е) решения по сбору и отводу дренажных вод

6,8

По периметру парковки, для сбора воды после срабатывания системы АУПТ, предусмотрены трапы на -1 этаже и приемки на -2 этаже с суммарным объемом не менее 2 м³. В этих приемках установлены два дренажных насоса NSP 50/400-1.5, N= 1.5кВт, U=3~400v. (1 рабочий, 1 резервный) с поплавковым выключателем.

В помещениях приточных вент. камер предусмотрены трапы на -1 этаже и приемки на -2 этаже. В этих приемках установлен один дренажный насос TMT 32M113/7,5Ci, N= 0,75кВт, U=3~380v, (1 рабочий).

В помещении ИТП на -1 этаже предусмотрен приемок с установкой дренажных насосов Wilo TMT 32M113/7,5Ci N= 0,75кВт, U=3~380v. (1 рабочий, 1 резервный) с поплавковым выключателем.

В помещении насосной АПТ, насосной ХВС и помещении узла ввода на -1 этаже предусмотрен приемок с установкой дренажных насосов NSP 50/400-1.5, N= 1.5кВт, U=3~400v. (1 рабочий, 1 резервный) с поплавковым выключателем.

В помещении КНС на -2 этаже предусмотрен приемок с установкой дренажных насосов NSP 50/400-1.5, N= 1.5кВт, U=3~400v. (1 рабочий) с поплавковым выключателем.

Марки и тип дренажных насосов указаны в табл.2.


Таблица 2. Ведомости насосного оборудования для отвода дренажных вод.

Наименование	Тип, марка	Завод-изготовитель, поставщик	Примечание
Дренажные насосы			
N-Lift 2E-120/1/1-EM		Wilo	
NSP 50/400-1.5		Wilo	
TMT 32M113/7,5Ci		Wilo	
Wilo TMT 32M113/7,5Ci		Wilo	

Остальные ранее разработанные решения ПД, получившие положительное заключение негосударственной экспертизы №77-2-1-3-047721-2024 от 19.08.2024 г., № 77-2-1-2-022133-2025 от 23.04.2025 г. и № 77-2-1-2-032022-2025 от 09.06.2025 г., остались без изменений.

Инов. № подл.	Подп. и дата	Взам. инв. №

Изм.	Копуч.	Лист	№ док.	Подп.	Дата	АА/БЭ-03-ДС3-ИОС3.1.ПЗ	Лист
							5

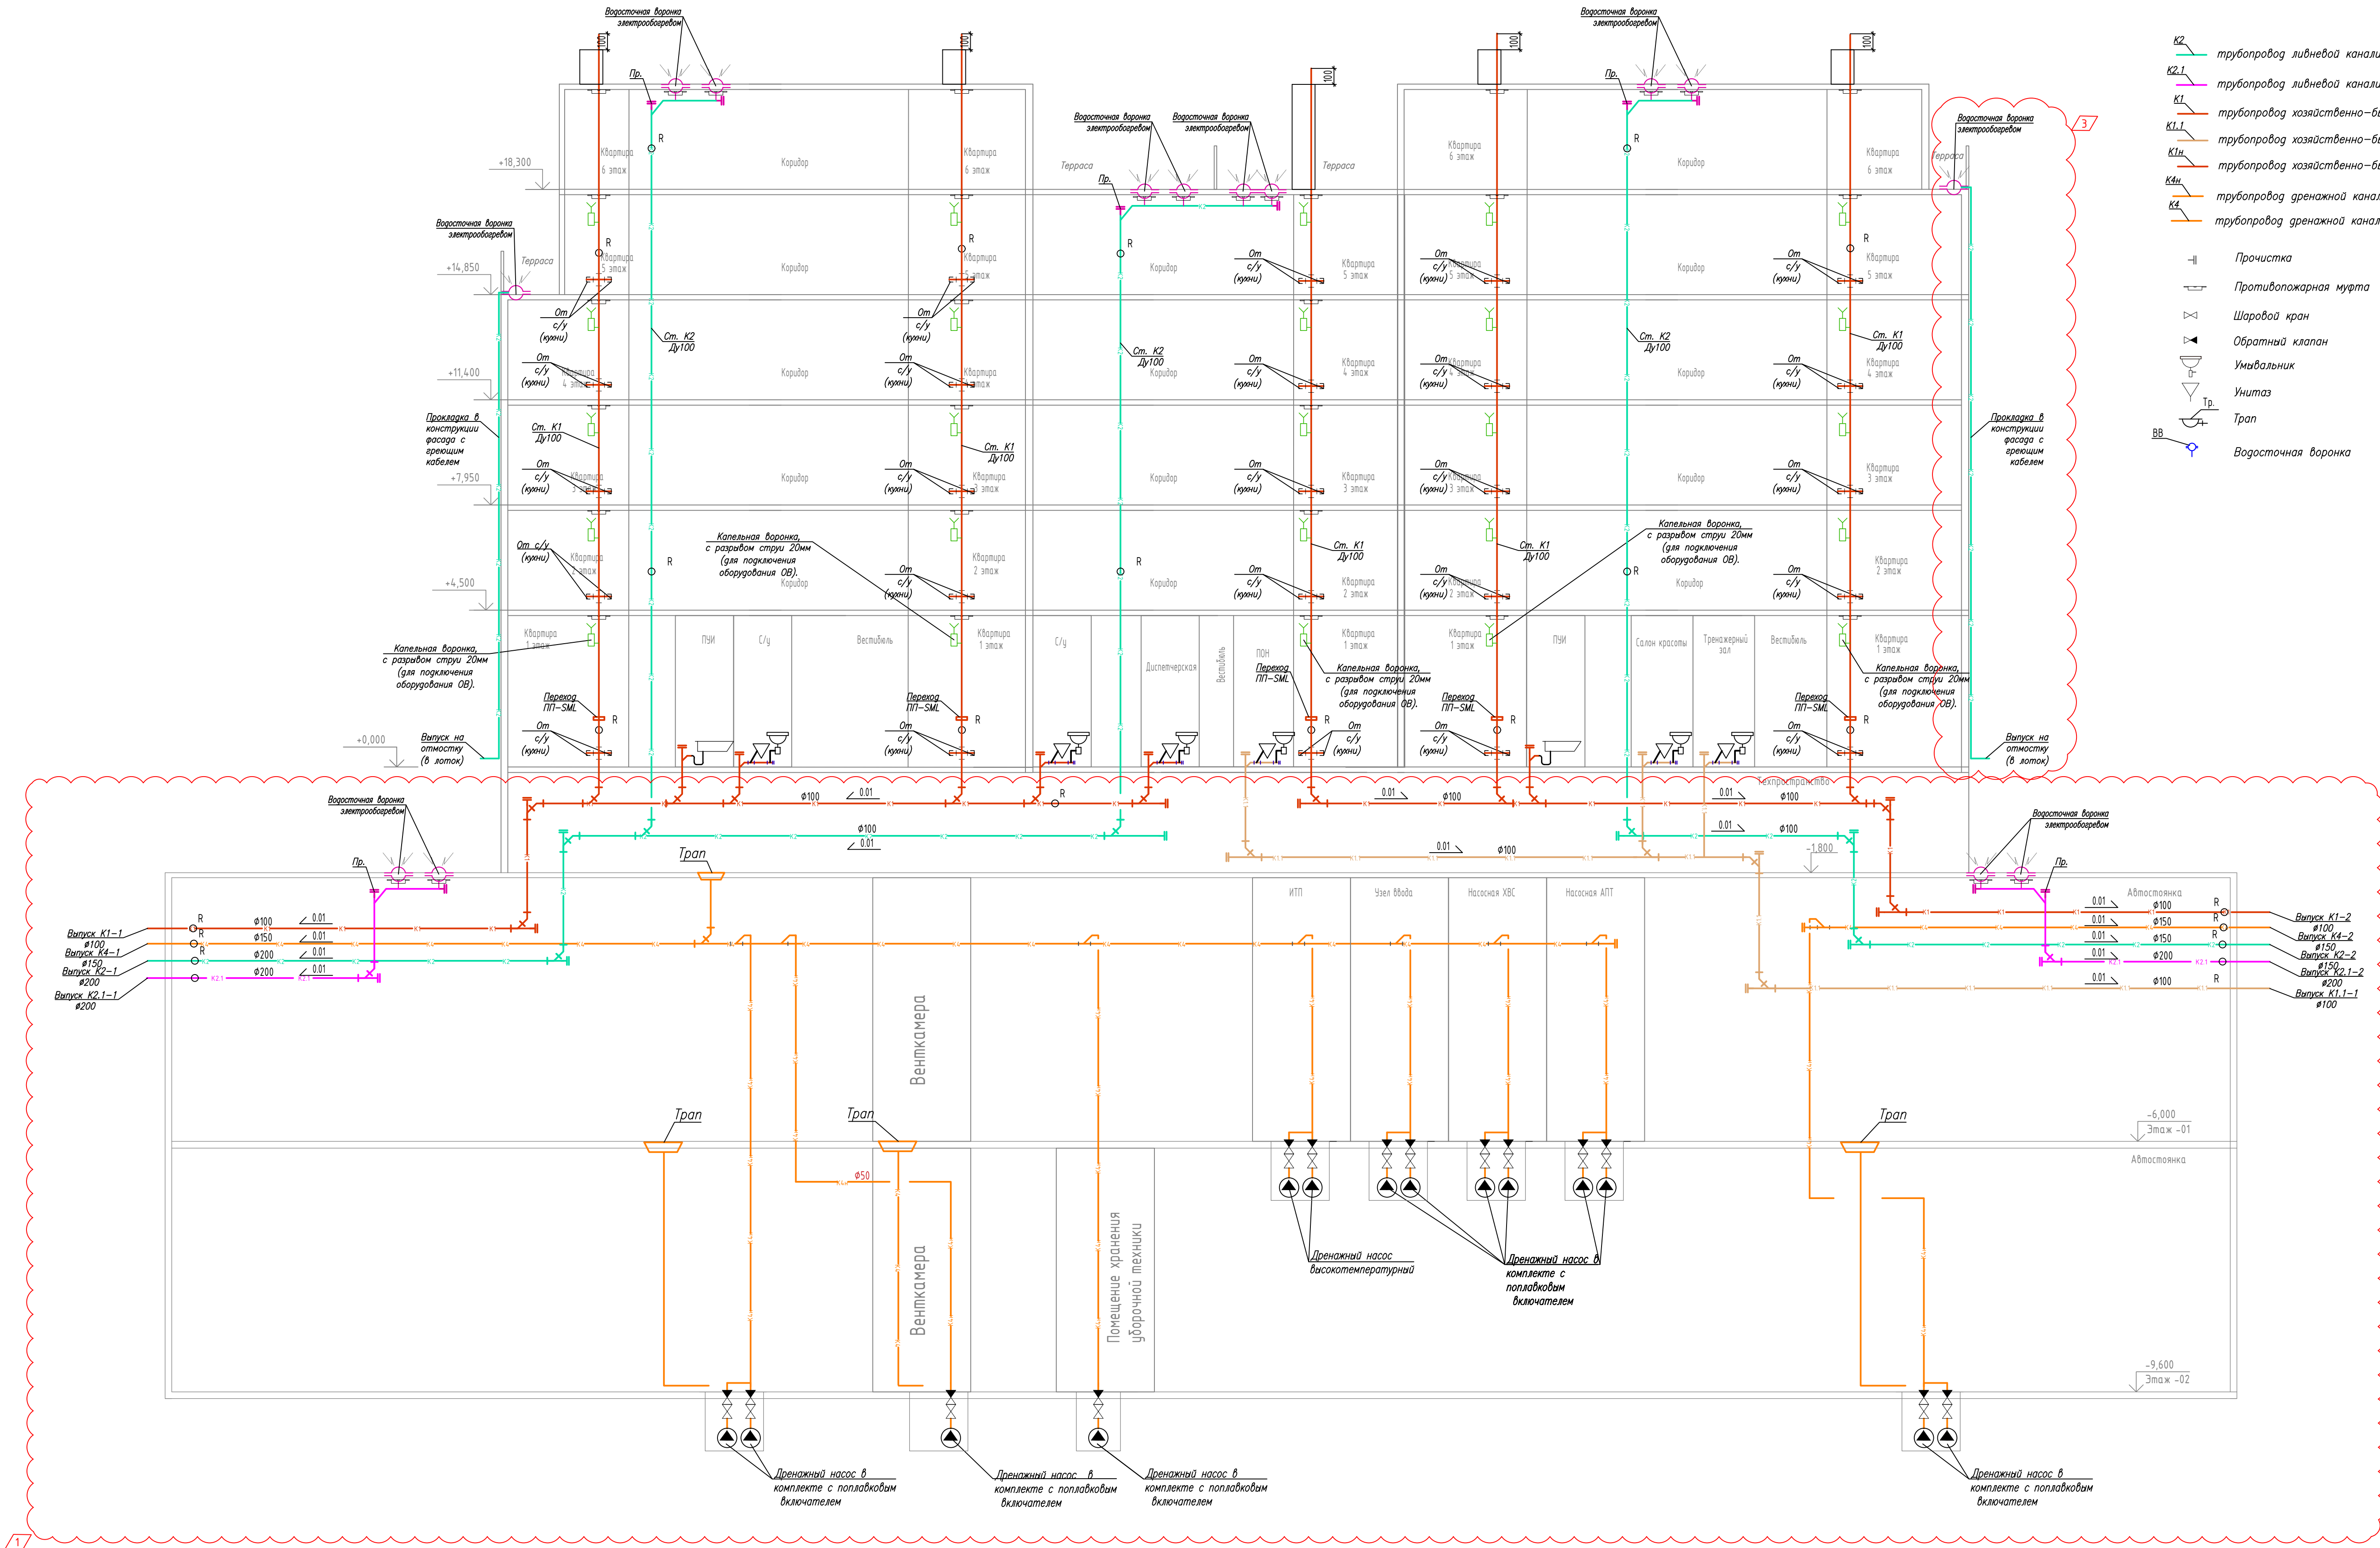


Примечания:

1. Количество стояков показано условно. Диаметр трубопроводов и количество выпусков уточняется в рабочей части проекта.
2. Количество и направления подключений к стоякам хозяйственно-бытовой канализации жилой указаны условно.
3. Количество и расстановка ревизий и прочисток уточняется в рабочей части проекта.
4. Количество и расстановка водосточных воронок кровли жилой части уточняется в рабочей части проекта.
5. Отводы от водосточных воронок и стояки водостока жилой части теплоизолировать. Теплоизоляция трубопроводов условно не указана.
6. Трубопроводы водостока в паркинге теплоизолировать изоляцией П, условно не указана.

						АА/БЗ-03-ДС3-ИЭС.1ГЧ		
						"Жилой комплекс" расположенный по адресу: г. Москва, ЦАО, Садовническая ул., вл 76/71		
Изм.	Жол.ч.	Лист	И. док.	Подп.	Дата	Внутренние системы водоотведения	Стация	Лист
Разраб.		Степанов			12.25		П	1
Проверил		Шукина		<i>Шукина</i>	12.25			
Н.контр.		Косылева		<i>Косылева</i>	12.25	Принципиальная схема систем водоотведения. (Корпус 1).	 ИНПАД	
						Формат А1		

Корпус №2


Условные обозначения

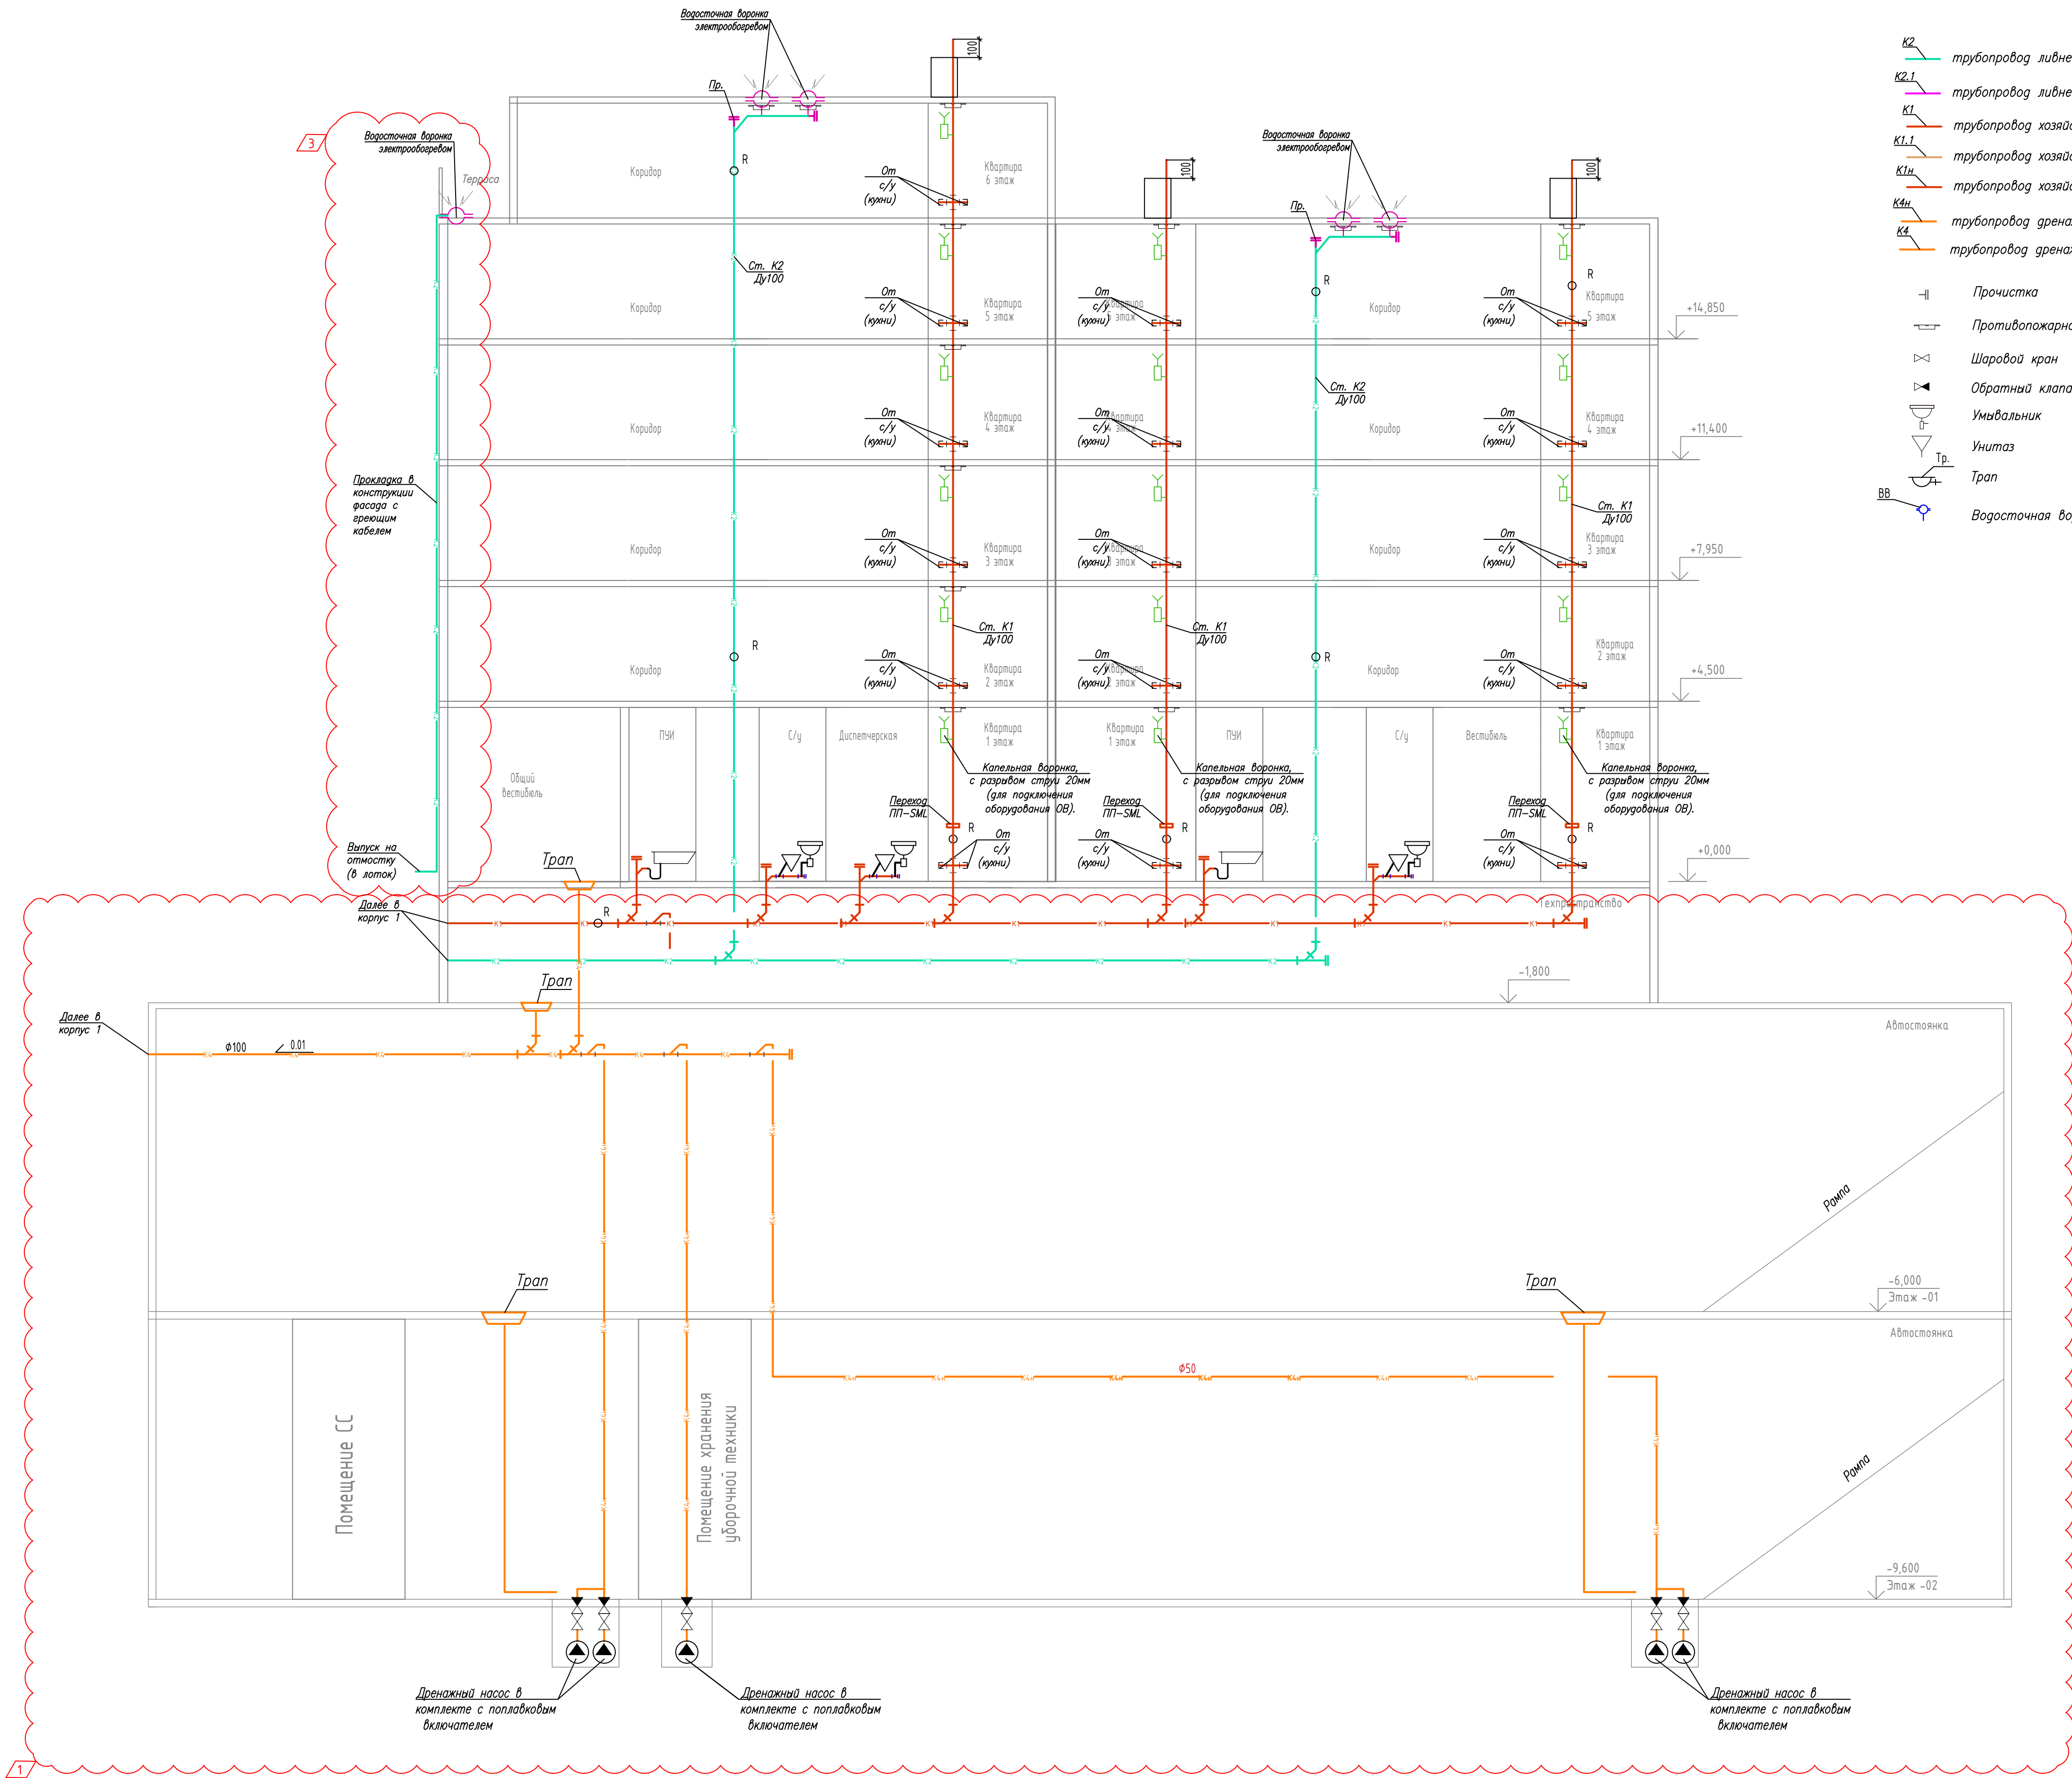

Примечания:

1. Количество стояков показано условно. Диаметр трубопроводов и количество выпусков уточняется в рабочей части проекта.
2. Количество и направления подключений к стоякам хозяйственно-бытовой канализации жилой указаны условно.
3. Количество и расстановка ревизий и прочисток уточняется в рабочей части проекта.
4. Количество и расстановка водосточных воронок кровли жилой части уточняется в рабочей части проекта.
5. Отводы от водосточных воронок и стояки водостока жилой части теплоизолировать. Теплоизоляция трубопроводов условно не указана.
6. Трубопроводы водостока в паркинге теплоизолировать изоляцией П1, условно не указана.

						АА/БЗ-03-ДС3-ИОС3.1ГЧ			
						"Жилой комплекс" расположенный по адресу: г. Москва, ЦАО, Садовническая ул., вл 76/71			
Изм.	Жолуч	Лист	№ док.	Подп.	Дата	Внутренние системы водоотведения	Стация	Лист	Листов
Разработ.	Степанов			И	12.25		п	2	
Проверил	Шукина			Шукина	12.25				
Н.контр.	Косылева			О	12.25	Принципиальная схема систем водоотведения. (Корпус 2).	 ИНПАД		

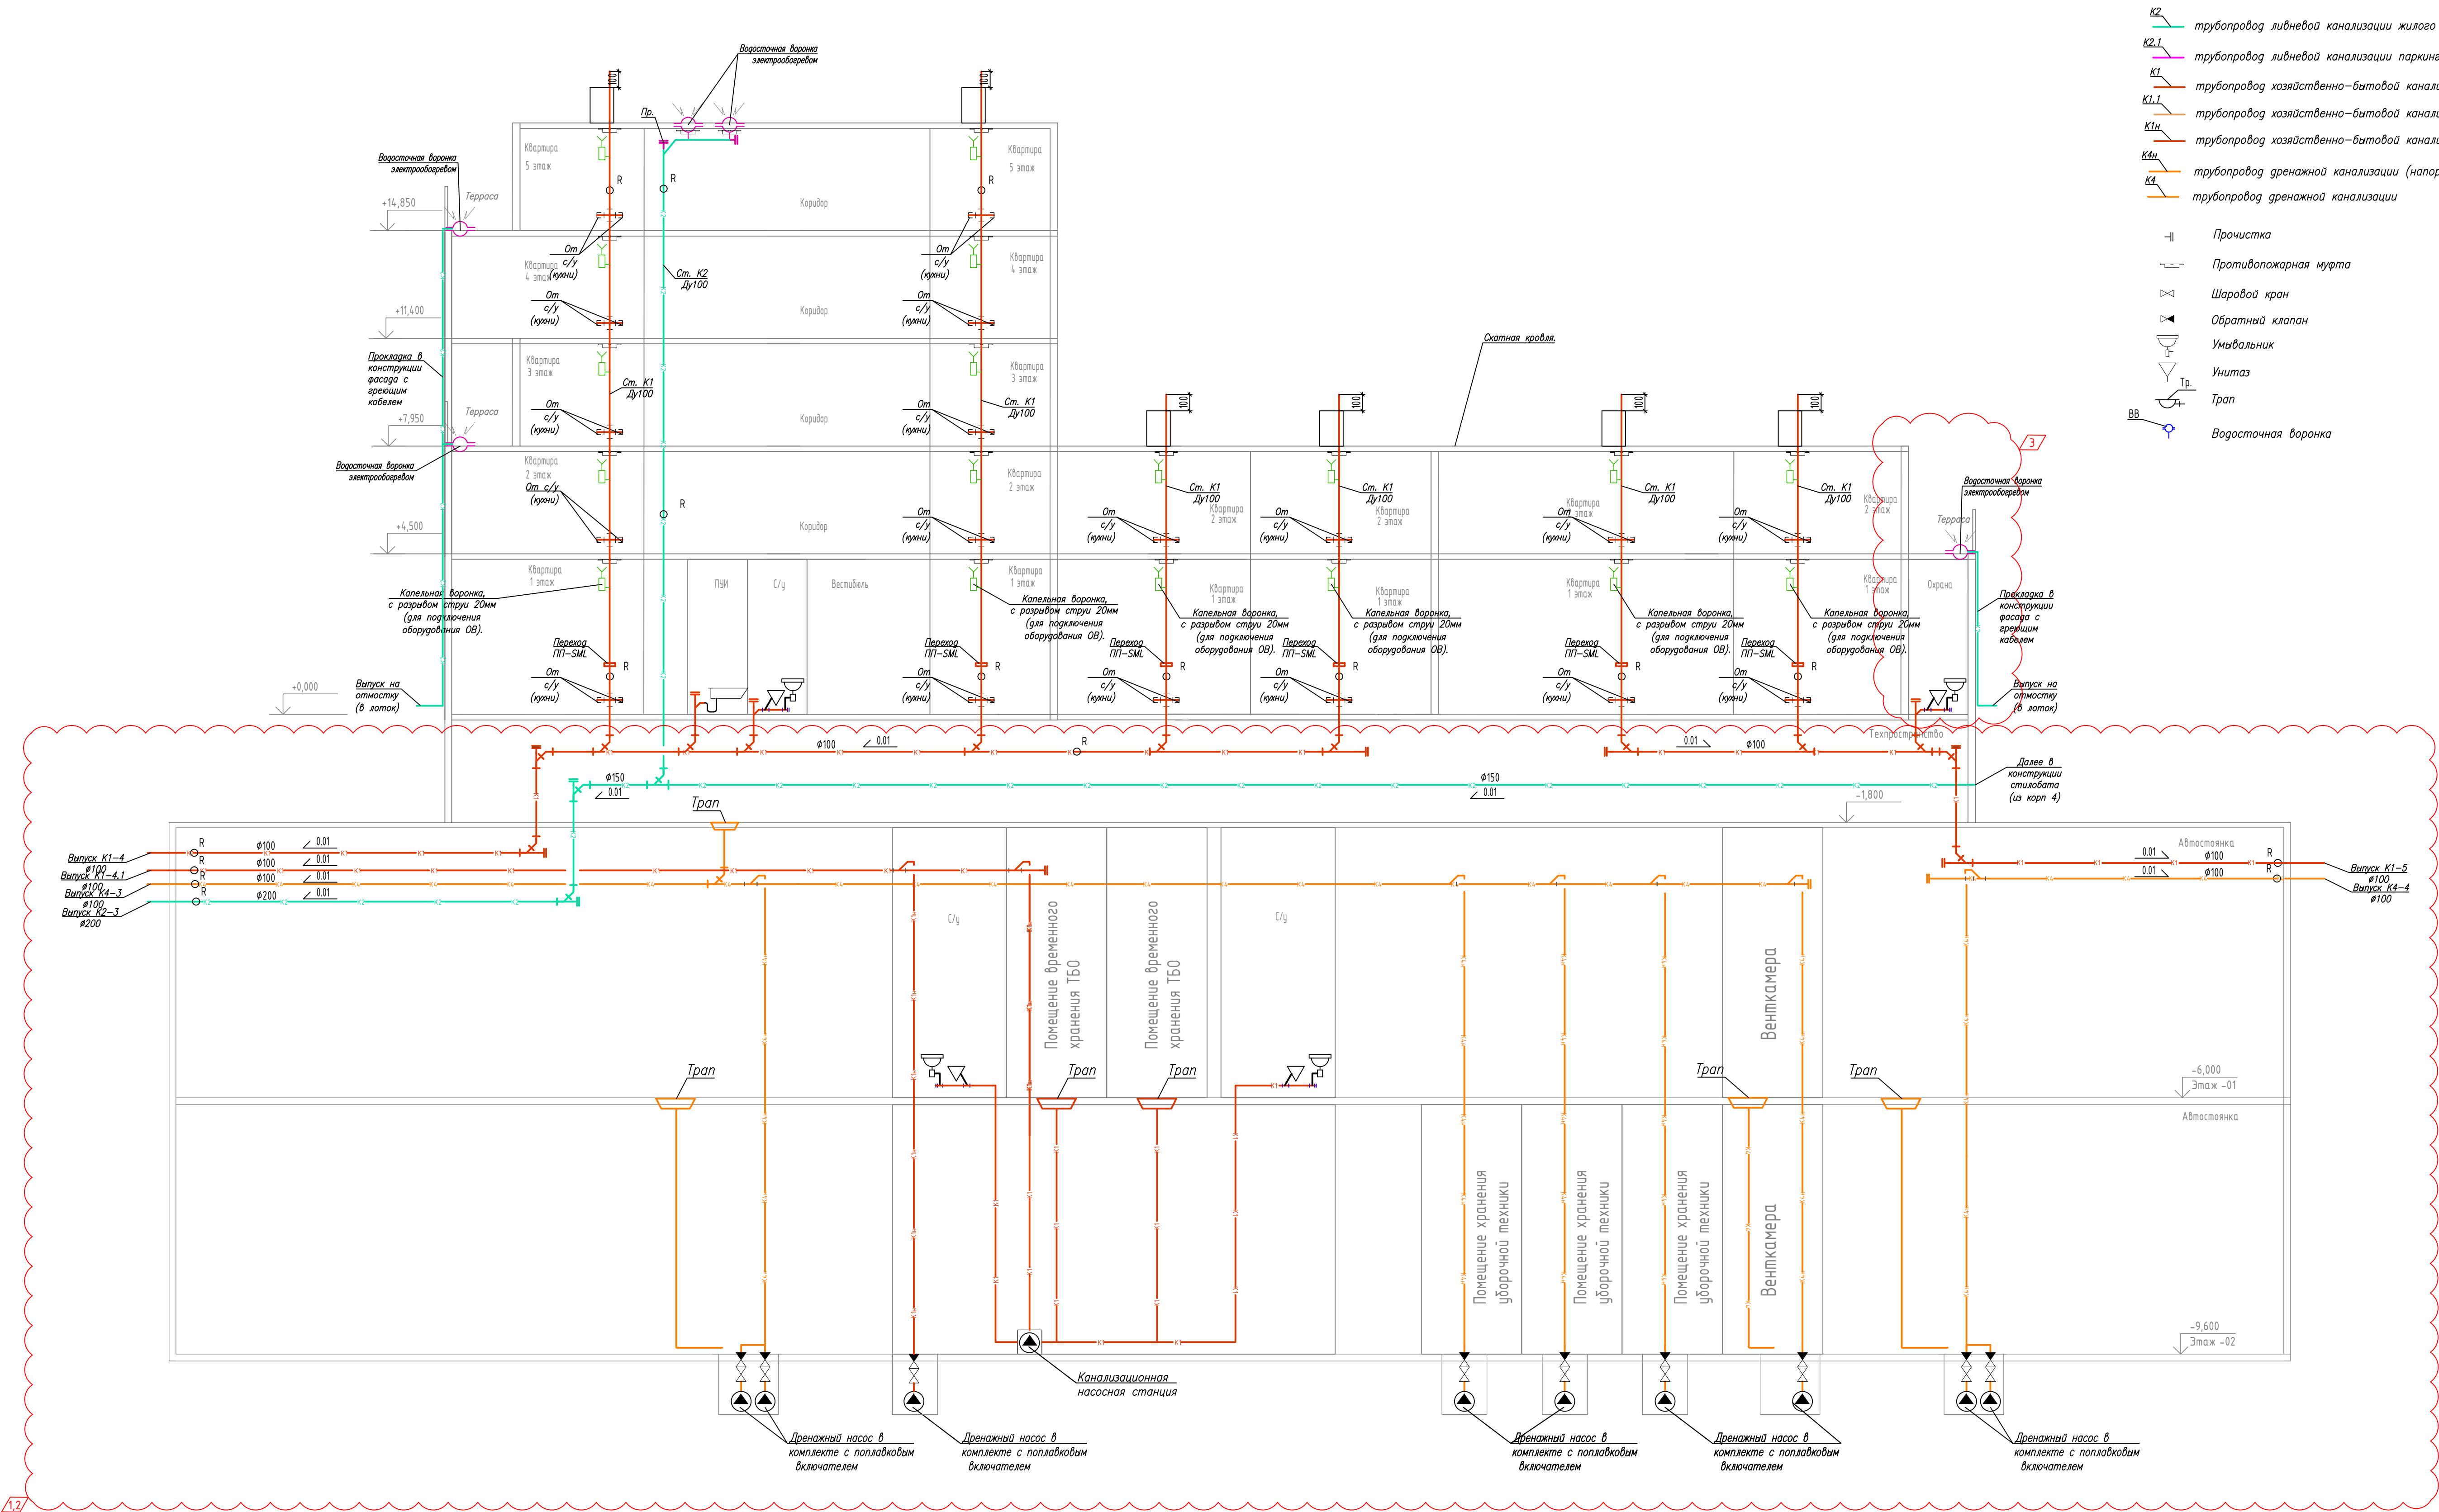

- К2 труборовод ливневой канализации жилого корпуса
- К2.1 труборовод ливневой канализации паркинга
- К1 труборовод хозяйственно-бытовой канализации жилых квартир
- К1.1 труборовод хозяйственно-бытовой канализации нежилых помещений
- К1н труборовод хозяйственно-бытовой канализации жилых квартир (напорный)
- К4 труборовод дренажной канализации (напорный)
- К4 труборовод дренажной канализации
- Прочистка
- Противопожарная муфта
- Шаровый кран
- Обратный клапан
- Умывальник
- Унитаз
- Трап
- Водосточная воронка

Примечания

- Количество стояков показано условно. Диаметр трубороводов и количество выпусков уточняется в рабочей части проекта.
- Количество и направления подключений к стоякам хозяйственно-бытовой канализации жилой указаны условно.
- Количество и расстановка ревизий и прочисток уточняется в рабочей части проекта.
- Количество и расстановка водосточных воронок кровли жилой части уточняется в рабочей части проекта.
- Отводы от водосточных воронок и стояки водостока жилой части теплоизолировать. Теплоизоляция трубороводов условно не указана.
- Трубороводы водостока в паркинге теплоизолировать изоляцией П, условно не указана.

АА/БЗ-03-ДСЗ-ИОСЗ.1ГЧ					
"Жилой комплекс" расположенный по адресу: г. Москва, ЦАО, Садовническая ул., вл. 76/71					
Изм.	Жол.ч.	Лист	И. док.	Подп.	Дата
Разраб.	Степанов	12	25	12.25	
Проверил	Шушкова	12	25	12.25	
Н.контр.	Космылева	12	25	12.25	
Внутренние системы водоотведения				Стация	Лист
Принципиальная схема систем водоотведения. (Корпус 3).				П	3
ИНПАД				Формат А1	

[illegible]

Условные обозначения

- | | |
|---|---|
|  | трубопровод ливневой канализации жилого корпуса |
|  | трубопровод ливневой канализации паркинга |
|  | трубопровод хозяйственно-бытовой канализации жилых квартир |
|  | трубопровод хозяйственно-бытовой канализации нежилых помещений |
|  | трубопровод хозяйственно-бытовой канализации жилых квартир (напорный) |
|  | трубопровод дренажной канализации (напорный) |
|  | трубопровод дренажной канализации |
|  | Прочистка |
|  | Противопожарная муфта |
|  | Шаровый кран |
|  | Обратный клапан |
|  | Умывальник |
|  | Унитаз |
|  | Трап |
|  | Трап |
|  | Водосточная воронка |

~~Примечания:~~

1. Количество стояков показано условно. Диаметр трубопроводов и количество выпусков уточняется в рабочей части проекта.
2. Количество и направления подключений к стоякам хозяйственно-бытовой канализации жилой указаны условно.
3. Количество и расстановка ревизий и прочисток уточняется в рабочей части проекта.
4. Количество и расстановка водосточных воронок кровли жилой части уточняется в рабочей части проекта.
5. Отводы от водосточных воронок и стояки водосточка жилой части теплоизолировать. Теплоизоляция трубопроводов условно не указана.
6. Грубопрорисов водосточка в паркинге теплоизолировать изоляцией П, условно не указана.

						АА/БЗ-03-ДСЗ-ИОСЗ.1ГЧ		
						"Жилой комплекс" расположенный по адресу: г. Москва, ЦАО, Садовническая ул., вл 76/71		
Изм.	Колуч	Лист	N док.	Подп.	Дата			
Разработ.	Степанов			<i>СН</i>	12.25	Внутренние системы водоотведения	Стадия	Лист
Проверил	Шшикина			<i>Лев</i>	12.25		П	4
Н.контр.	Костылева			<i>О</i>	12.25	Принципиальная схема систем водоотведения. (Корпус 4).		ИНПАД

ДОПОЛНИТЕЛЬНОЕ СОГЛАШЕНИЕ № 1

к Договору от 26.01.2023г. № 15234ДП-К о подключении (технологическом присоединении) к централизованной системе водоотведения (далее: «Договор»)

г. Москва

«15» АВГ 2024 г.

Акционерное общество «Мосводоканал», именуемое в дальнейшем АО «Мосводоканал», в лице начальника управления по перспективному развитию и присоединениям АО «Мосводоканал» Бобровского Юрия Анатольевича, действующего на основании Доверенности № (30)01.08-1644/21 от 30.12.2021г., с одной стороны, и Общество с ограниченной ответственностью «Специализированный застройщик Балчуг эстейт» (ООО «СЗ Балчуг эстейт»), именуемое в дальнейшем «Заявитель», в лице Генерального директора Савосько Евгения Вячеславовича, действующего на основании Устава, с другой стороны, именуемые в дальнейшем «Стороны», заключили настоящее Дополнительное соглашение к Договору о нижеследующем:

1. Внести в Договор следующие изменения:

1.1. В связи с изменением наименования ООО «Балчуг эстейт», в преамбуле Договора и по всему тексту Договора, включая Приложения, наименование Заявителя – Общество с ограниченной ответственностью «Специализированный застройщик Балчуг эстейт» (ООО «СЗ Балчуг эстейт»).

1.2. Пункт 2.1. Договора в следующей редакции:

«Срок подключения объекта – до 30.06.2026 г.».

1.3. Пункт 3.3. Договора в следующей редакции:

Потребности объекта – величина подключаемой мощности (нагрузки) объекта, который обязано обеспечить АО «Мосводоканал» в точках подключения (технологического присоединения), составляет 114,080 м3/сут. приема сточных вод.

1.4. Пункт 5.2 Договора в следующей редакции:

Заявитель обязан внести плату в размере, предусмотренном приложением № 4 к настоящему договору, на расчетный счет АО «Мосводоканал» в следующем порядке:

- 6 322 905 рублей 78 копеек вносится в течение 15 дней с даты заключения настоящего договора;

- 9 032 722 рубля 54 копейки вносится в течение 90 дней с даты заключения настоящего договора, но не позднее даты фактического подключения;

- 774 768 рублей 53 копейки вносится в течение 15 дней с даты заключения настоящего Дополнительного соглашения;

- 2 846 540 рублей 62 копейки (15 % платы за подключение (технологическое присоединение) вносится в течение 15 дней с даты подписания сторонами акта о подключении (технологическом присоединении) объекта к централизованной системе водоотведения по форме согласно приложению № 5, но не позднее выполнения условий подключения (технологического присоединения).

В случае если сроки фактического присоединения объекта Заявителя не соблюдаются в связи с действиями (бездействием) Заявителя и АО «Мосводоканал» выполнены все необходимые мероприятия для создания технической возможности подключения (технологического присоединения) и выполнения работ по подключению (технологическому

присоединению), оставшаяся доля платы за подключение (технологическое присоединение) вносится в течение 15 дней со дня подписания акта о выполнении мероприятий по обеспечению технической возможности подключения (технологического присоединения) по форме согласно приложению № 6 либо в течение 10 календарных дней со дня получения заявителем уведомления, АО «Мосводоканал» о расторжении настоящего договора в одностороннем порядке, но не позднее срока подключения (технологического присоединения), указанного в настоящем договоре.

1.5. Пункт 9.1. Договора в следующей редакции:

«Настоящий договор вступает в силу со дня его подписания сторонами и действует до 30.06.2026 года, а в части обязательств, не исполненных к моменту окончания срока его действия - до полного их исполнения Сторонами».

1.6. Реквизиты Заказчика изложить в следующей редакции:

ООО «СЗ Балчуг эстейт»

Юридический адрес:

115035, г. Москва, Садовническая наб., дом 69

ОГРН 1167746249406

ИНН 9705062309

КПП 770501001

р/с 40702810700480031753

в АО "Банк ДОМ.РФ"

БИК 044525266

к/с 30101810345250000266

Оператор ЭДО:

ИНН _____

ОГРН _____

1.7. Изложить приложение № 1 - «Технические условия подключения (технологического присоединения) к централизованной системе водоотведения» в новой редакции (Приложение № 1 к настоящему дополнительному соглашению).

1.8. Изложить приложение № 2 - «Параметры подключения (технологического присоединения) к централизованной системе водоотведения» в новой редакции (Приложение № 2 к настоящему дополнительному соглашению).

1.9. Изложить приложение № 3 - «Перечень мероприятий (в том числе технических) по подключению (технологическому присоединению) объекта к централизованной системе водоотведения» в новой редакции (Приложение № 3 к настоящему дополнительному соглашению).

1.10. Изложить приложение № 4 - «Размер платы за подключение (технологическое присоединение) к централизованной системе водоотведения» в новой редакции (Приложение № 4 к настоящему дополнительному соглашению).

2. Стороны подтверждают, что на момент подписания настоящего Дополнительного соглашения Заявителем внесена плата за подключение по Договору в размере: 15 355 628 (пятнадцать миллионов триста пятьдесят пять тысяч шестьсот двадцать восемь) рубля 32 копейки, в том числе НДС (20 %) 2 559 271 рубль 39 копеек.

3. Во всем, что не оговорено настоящим Дополнительным соглашением, стороны руководствуются условиями заключенного Договора.

4. Настоящее Дополнительное соглашение вступает в силу с момента его заключения.

5. Настоящее Дополнительное соглашение является неотъемлемой частью Договора.

6. Настоящее Дополнительное соглашение составлено в двух экземплярах, имеющих равную юридическую силу, по одному для каждой из Сторон.

7. К настоящему Дополнительному Соглашению прилагается и является его неотъемлемой частью:

- Приложение № 1 – «Технические условия подключения (технологического присоединения) к централизованной системе водоотведения»;

- Приложение № 2 - «Параметры подключения (технологического присоединения) к централизованной системе водоотведения»;

- Приложение №3 – «Перечень мероприятий (в том числе технических) по подключению (технологическому присоединению) объекта к централизованной системе водоотведения»;

- Приложение № 4 – «Размер платы за подключение (технологическое присоединение) к централизованной системе водоотведения».

Реквизиты и подписи Сторон:

АО «Мосводоканал»

Юридический адрес: 105005,
г. Москва, Плетешковский пер., 2

ОГРН 1127747298250

ИНН 7701984274

КПП 770101001

Р/с 40602810338000000060

в ПАО Сбербанк

К/с 30101810400000000225

БИК 044525225

Оператор ЭДО:

ООО «Компания «Тензор»

ИНН 7605016030

ОГРН 1027600787994

ООО «СЗ БАЛЧУГ ЭСТЕЙТ»

Юридический адрес:

115035, г. Москва, Садовническая наб.,
дом 69

ОГРН 1167746249406

ИНН 9705062309

КПП 770501001

р/с 40702810700480031753

в АО "Банк ДОМ.РФ"

БИК 044525266

к/с 30101810345250000266

Оператор ЭДО:

ИНН _____

ОГРН _____

Начальник управления по перспективному
развитию и присоединениям

М.П.

" " 20__ г.

Начальник СТП УР
Куриленков А.Ю.

По доверенности №(30)01.08-1640/21



Ю.А. Бобровский

15 АВГ 2024

Генеральный директор



Е.В.Савосько

" " 20__ г.

15 АВГ 2024

Приложение № 1
к Дополнительному соглашению
№ 1 от 15 АВГ 2024 г.
Приложение 1
к Договору о подключении (технологическом
присоединении) к централизованным системам
водоотведения от 26.01.2023г. № 15234ДП-К

ТЕХНИЧЕСКИЕ УСЛОВИЯ ПОДКЛЮЧЕНИЯ (ТЕХНОЛОГИЧЕСКОГО ПРИСОЕДИНЕНИЯ) К ЦЕНТРАЛИЗОВАННОЙ СИСТЕМЕ ВОДООТВЕДЕНИЯ

Сведения об исполнителе:

Полное наименование: Акционерное общество "Мосводоканал"
Сокращенное наименование: АО "Мосводоканал"
ОГРН 1127747298250
Юридический адрес: 105005, Москва, Плетешковский пер., д 2
Телефон: 8-499-763-34-34
E-mail: post@mosvodokanal.ru
Заявитель: ОБЩЕСТВО С ОГРАНИЧЕННОЙ ОТВЕТСТВЕННОСТЬЮ
"СПЕЦИАЛИЗИРОВАННЫЙ ЗАСТРОЙЩИК БАЛЧУГ ЭСТЕЙТ"
Наименование объекта Жилой комплекс с подземной автостоянкой
Адрес объекта Садовническая ул., владение 76/71

Информация о точке (точках) присоединения:

существующие колодцы на канализационной сети $d=300\text{мм}$ с восточной стороны, канализационной сети $d=450\text{мм}$ с западной стороны и в существующий колодец К-2015019 на канализационной сети $d=125-200\text{мм}$.

Информация о максимальной мощности (нагрузке) в возможных точках присоединения, в пределах которой исполнитель обязуется обеспечить возможность подключения подключаемого объекта: не запрашивалась.

Начальник управления по
перспективному развитию и
присоединениям
АО «Мосводоканал»

Генеральный директор
ООО «СЗ БАЛЧУГ ЭСТЕЙТ»

М.П.  Ю.А. Бобровский

Е.В.Савосько

М.П.

М.П.

20 ____ г.

Зам. начальника управления —
начальник
Куриленков Д.Ю. В.А.
По доверенности №(30)01.08-1640/21

15 АВГ 2024



15 АВГ 2024

ПАРАМЕТРЫ ПОДКЛЮЧЕНИЯ (ТЕХНОЛОГИЧЕСКОГО ПРИСОЕДИНЕНИЯ) К ЦЕНТРАЛИЗОВАННОЙ СИСТЕМЕ ВОДООТВЕДЕНИЯ

Основание:	Заявка на подключение № 15234ДП-К
Причина обращения:	НОВОЕ СТРОИТЕЛЬСТВО
Подключаемый объект:	Жилой комплекс с подземной автостоянкой Садовническая ул., владение 76/71
Кадастровый номер земельного участка	77:01:0002014:6383
Заявитель:	ОБЩЕСТВО С ОГРАНИЧЕННОЙ ОТВЕТСТВЕННОСТЬЮ "СПЕЦИАЛИЗИРОВАННЫЙ ЗАСТРОЙЩИК БАЛЧУГ ЭСТЕЙТ"

Точка подключения (технологического присоединения) к централизованной системе водоотведения: внешняя стенка колодца/колодцев на выпусках из здания.

Необходимо выполнить:

- строительство канализационной сети в интервале К-2015019-К-2015028 для обеспечения пропускной способности сети в нормальном гидравлическом режиме с учетом дополнительного объема стоков от подключаемого объекта;

- устройство колодца/колодцев на выпусках из здания/зданий;

- строительство канализационной сети от колодца/колодцев на выпусках из здания/зданий до точки присоединения.

Технические требования к объектам капитального строительства Заявителя, в том числе к устройствам и сооружениям для подключения (технологического присоединения), а также к выполняемым Заявителем мероприятиям для осуществления подключения (технологического присоединения):

- обеспечить сохранность транзитных сетей от зданий остающихся в эксплуатации или переключить их на проектируемые/перекладываемые канализационные сети с сохранением непрерывного водоотведения от объектов;

- канализационные сети исключаемые из эксплуатации должны быть ликвидированы, колодцы демонтированы и забутованы;

- переустройство/ликвидацию сетей, не состоящих на балансе АО "Мосводоканал" согласовать с владельцем сети. Копию согласования приложить к документации, представляемой в АО "Мосводоканал".

- выполнить все мероприятия, предусмотренные приложением № 3 к договору. Мероприятия должны быть выполнены в сроки, установленные приложением № 3.

Нарушение Заявителем условий подключения путем невыполнения предусмотренных разделом II приложения № 3 перечня мероприятий является существенным нарушением условий договора.

Проектирование и строительство внутриплощадочных сетей вести в соответствии с требованиями АО "Мосводоканал".

Предъявлять АО "Мосводоканал":

- до начала работ для определения технического состояния и качества: трубы, фасонные части, конструктивные элементы колодцев, металлоконструкции, арматуру, запорную арматуру и другое применяемое при строительстве оборудование и материалы, а также сертификаты и паспорта на них;

- выполнение скрытых работ по строительству внутриплощадочных сетей в полном объеме: основания под трубопроводы, упоры, гидроизоляцию колодцев, камер, вязку арматурных каркасов, сварные швы, телевизионный контроль и т.д.;

- гидравлические испытания трубопроводов в соответствии с СП 129.13330.2019;

- исполнительную документацию в составе:

- Акты на скрытые работы по устройству оснований, фундаментов, упоров, уплотнений грунтов, изоляции и др.;
- Сертификаты и технические паспорта на трубы, арматуру, оборудование и материалы;
- Акты гидравлических испытаний коммуникаций и сооружений на прочность и герметичность;
- Журнал производства работ;
- Исполнительная документация законченного строительством объекта с решением Комитета по архитектуре и градостроительству города Москвы (МОСКОМАРХИТЕКТУРЫ) о приемке данной исполнительной документации для ведения сводного плана подземных коммуникаций и сооружений;
- Акт технической приемки законченного строительством объекта;
- Гарантийный паспорт строительной организации на сдаваемый объект с указанием срока ответственности за скрытые дефекты;
- Акт технической приемки системы внутренней канализации объекта;
- Исполнительные чертежи (заверенные подписями и печатями Заявителя, проектной и подрядной организаций) системы внутренней канализации в составе: плана технического подполья с разводкой канализации и аксонометрического чертежа по стоякам с сантехприборами.

Отметка лотков в точке (точках) присоединения к централизованной системе водоотведения : определить проектом.

Нагрузка в точке подключения хозяйственно-бытовых сточных вод 114,08 м³/сут;
6,5 л/с

Нормативы по объему сточных вод, нормативы состава сточных вод, требования к составу и свойствам сточных вод, установленные в целях предотвращения негативного воздействия на работу централизованной системы водоотведения - не предусмотрено.

Режим отведения сточных вод – круглосуточно.

Требования к устройствам, предназначенным для отбора проб и учета объема сточных вод, требования к проектированию узла учета, к месту размещения устройств учета, требования к схеме установки устройств учета и иных компонентов узла учета, требования к техническим характеристикам устройств учета, в том числе точности, диапазону измерений и уровню погрешности (требования к устройствам не должны содержать указания на определенные марки приборов и методики измерения) – не предусмотрено.

Требования по сокращению сброса загрязняющих веществ, которые должны быть учтены в плане снижения сбросов, плане по обеспечению соблюдения требований к составу и свойствам сточных вод, установленных в целях предотвращения негативного воздействия на работу централизованной системы водоотведения – не предусмотрено.

Границы эксплуатационной ответственности по канализационным сетям АО "Мосводоканал" и Заявителя: внешняя стенка колодца/колодцев на выпусках из здания.

Информация о наличии сетей канализации в зоне проведения работ


В случае необходимости сноса (выноса) инженерных сетей и (или) сооружений, принадлежащих АО "Мосводоканал" на праве собственности, Застройщик обязан после утверждения границ строительной площадки и посадки проектируемых зданий, сооружений или линейных объектов, до начала разработки проектной документации и выполнения работ по подготовке строительной площадки обратиться в АО "Мосводоканал" с Заявкой и заключить Соглашение о компенсации потерь (далее по тексту - СКП) по объекту по форме, утвержденной и размещенной на сайте <http://www.mosvodokanal.ru/>.

Застройщик обязан: в установленном СКП порядке, размере и сроке компенсировать АО "Мосводоканал" все его расходы и убытки.

В случае наличия в проекте технического решения о сносе/выносе водопроводных и/или канализационных сетей, сооружений, зданий, оборудования или иного имущества (далее по тексту - Объекты), принадлежащего на праве собственности городу Москве, мероприятия по сносу/выносу Объектов обеспечиваются Застройщиком с обязательным соблюдением требований постановлений Правительства Москвы от 29.06.2010 №540-ПП "Об утверждении положения об управлении объектами нежилого фонда, находящимися в собственности города Москвы" и от 15.12.2015 № 861-ПП "О порядке осуществления денежной компенсации городу Москве в связи со сносом инженерных сетей и сооружений, сооружений связи, линий связи и сетей связи, объектов электросетевого хозяйства, находящихся в собственности города Москвы, осуществляемых в процессе строительства объектов капитального строительства".

Начальник управления по
перспективному развитию и
присоединениям
АО «Мосводоканал»

Ю.А. Бобровский

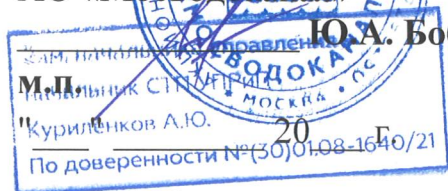

Генеральный директор
ООО «СЗ БАЛЧУГ ЭСТЕЙТ»

Е.В.Савосько



15 АВГ 2024

20 ____ г.

Приложение № 3 к Дополнительному соглашению
Приложение 3
к Договору о подключении (технологическом
присоединении)
к централизованным системам
водоотведения
от 26.01.2023г. № 15234 ДП-К

П Е Р Е Ч Е Н Ь
МЕРОПРИЯТИЙ ПО ПОДКЛЮЧЕНИЮ (ТЕХНОЛОГИЧЕСКОМУ
ПРИСОЕДИНЕНИЮ) ОБЪЕКТА К ЦЕНТРАЛИЗОВАННОЙ СИСТЕМЕ
ВОДООТВЕДЕНИЯ

№ п/п	Наименование мероприятия	Состав мероприятия	Срок выполнения
I. Мероприятия АО «Мосводоканал»			
1.	Разработка проектной документации и согласование	Длина и диаметр определяются проектом	30.06.2026 г.
2.	Строительство канализации		
II. Мероприятия Заявителя			
1	Предоставление исходных данных в АО «Мосводоканал»	1. Планово-высотное положение проектируемого колодца канализации с указанием отметки лотка, проектируемого на границе участка; 2. План организации рельефа (вертикальная планировка) территории застройки; 3. Топографический план с посадкой проектируемого (существующего) здания	1 месяц с даты заключения договора
2	Предоставление проектной документации внутриобъектных сетей и согласование с АО «Мосводоканал»	1. Разработка и согласование проектной документации. 2. Предоставление выписки из раздела утвержденной в установленном порядке проектной документации, в которой содержатся сведения об инженерном оборудовании, водопроводных (канализационных) сетях, перечень инженерно-технических мероприятий и содержание технологических решений.	4 месяца с даты заключения договора
3.	Строительство внутриобъектных сетей и оборудования Устройство КНС при необходимости	Определить проектом	31.05.2026 г.
4	Направление уведомления о выполнении условий подключения (технологического присоединения)		

Начальник управления по перспективному
развитию и присоединениям
АО «Мосводоканал»

_____ **Ю.А. Бобровский**

Генеральный директор
ООО «СЗ БАЛЧУГ ЭСТЕЙТ»

_____ **Е.В.Савосько**

М.П.

Зам. начальника управления –
начальник СТП УПРИП 20__ г.

Куриленков А.Ю.

По доверенности №(30)01.08-1640/21

15 АВГ 2024



20__ г.

15 АВГ 2024

Приложение № 4
к Дополнительному соглашению
Приложение 4
к Договору о подключении (технологическом
присоединении) к централизованным системам
водоотведения
от 26.01.2023г. № 15234ДП-К

Р А З М Е Р ПЛАТЫ ЗА ПОДКЛЮЧЕНИЕ (ТЕХНОЛОГИЧЕСКОЕ ПРИСОЕДИНЕНИЕ) К ЦЕНТРАЛИЗОВАННОЙ СИСТЕМЕ ВОДООТВЕДЕНИЯ

Плата за подключение (технологическое присоединение) по договору от 26.01.2023г. № 15234ДП-К составляет 15 814 114 (пятнадцать миллионов восемьсот сорок четыре тысячи сто сорок четыре) рублей 56 копеек, кроме того, НДС (20 %) 3 162 822 рубля 91 копейка, установлена и определена путем суммирования:

1) произведения действующего тарифа на подключение в размере 1 379,23 руб./куб.м, установленного Приказом Департамента экономической политики и развития города Москвы от 18.12.2023г. № ДПР-ТР-340/23, и подключаемой нагрузки в точке подключения в размере 114,080 куб.м/сут;

2) произведения действующего тарифа на покрытие расходов на прокладку сетей в размере 104 378,48 руб. за п.м., установленного Приказом Департамента экономической политики и развития города Москвы от 18.12.2023г. № ДПР-ТР-340/23, и расстояния от точки подключения объекта капитального строительства до точки подключения канализационных сетей к централизованной системе водоотведения АО «Мосводоканал» - 150 п.м. прокладываемого трубопровода диаметром от 101 мм до 200 мм (включительно) при однострунной закрытой прокладке;

3) НДС (20 %) 3 162 822 рубля 91 копейка.

Начальник управления по
перспективному развитию и присоединениям
АО «Мосводоканал»

Генеральный директор
ООО «СЗ БАЛЧУГ ЭСТЕЙТ»

Ю.А. Бобровский

Е.В.Савосько

М.П.

М.П.

" "

" "

20 ____ г.

Зам. начальника управления –
начальник СТОУП
Куриленков А.Ю.
По доверенности №(30)01.08-1640/21

15 АВГ 2024

15 АВГ 2024

ГОСУДАРСТВЕННОЕ УНИТАРНОЕ ПРЕДПРИЯТИЕ
города Москвы по эксплуатации московских водоотводящих систем
«МОСВОДОСТОК»

119017, Москва, Новокузнецкая ул., 26/8 стр. 1
ОГРН 1027739015567

тел.: (495) 953-29-01
Email: cancel@mosvodostok.info

ТЕХНИЧЕСКИЕ УСЛОВИЯ

№ 957/22 от 25.10.2022 г.

**на подключение к централизованной системе водоотведения поверхностных сточных вод.
Технологическое подключение объекта осуществляется на основании
заключенного договора о подключении.**

№ письма: 0001-90000003-068701-0014981/22

Заявитель: ООО "БАЛЧУГ ЭСТЕЙТ"

Объект: Жилой комплекс

Адрес: Город Москва, Улица Садовническая Земельный участок Владение 76/71

Планируемая нагрузка: 129 л/сек.

**Осуществить подключение к централизованной системе водоотведения поверхностных
сточных вод:**

D=400мм вблизи Садовнической улицы, дом 67с1 в смотровой колодез К1.

Максимальная нагрузка в точке присоединения: 150 л/сек.

Эксплуатационный гидротехнический район по адресу объекта - ЭГТР-1, тел.: +7(495) 685-38-20

Срок действия технических условий: 3 года от даты выдачи.

В случае если в течение 12 календарных месяцев (при комплексном развитии территории в течение 36 календарных месяцев) со дня выдачи технических условий заявителем не будет подано заявление о подключении, срок действия технических условий прекращается.

Приложение: ситуационный план с обозначением точки подключения.

Инженер 1 категории
Тел.: (495) 657-87-19 (1180)

Н.И. Подсадник

Главный инженер

А.А. Чибриков

