

ООО «СовИкоН»

«Современная инженерная концепция»

СРО, основанные на членстве лиц, осуществляющих подготовку проектной документации
109147, Россия, город Москва, улица Воронцовская, дом 35 Б, корпус 2, офис 600,
www.sromaster.ru, info@sromaster.ru

Регистрационный номер в государственном реестре саморегулируемых организаций
СРО-П-202-09082018
выдана Обществу с ограниченной ответственностью «Современная инженерная концепция»

«Жилой комплекс»

**по адресу: г. Москва, ЦАО, Садовническая ул., вл.
76/71**

ПРОЕКТНАЯ ДОКУМЕНТАЦИЯ

Раздел 5

**Сведения об инженерном оборудовании, о сетях
инженерно-технического обеспечения, перечень
инженерно-технических
мероприятий, содержание технологических решений
(внутренние инженерные системы)**

Подраздел 3

Система водоотведения

Часть 1

Внутренние системы водоотведения

ААБЭ-03-ДС3-ИОС-3.1

ООО «СовИкоН»

«Современная инженерная концепция»

СРО, основанные на членстве лиц, осуществляющих подготовку проектной документации
109147, Россия, город Москва, улица Воронцовская, дом 35 Б, корпус 2, офис 600,
www.sromaster.ru, info@sromaster.ru

Регистрационный номер в государственном реестре саморегулируемых организаций
СРО-П-202-09082018
выдана Обществу с ограниченной ответственностью «Современная инженерная концепция»

Жилой комплекс»

**по адресу: г. Москва, ЦАО, Садовническая ул., вл.
76/71**

ПРОЕКТНАЯ ДОКУМЕНТАЦИЯ

Раздел 5

**Сведения об инженерном оборудовании, о сетях
инженерно-технического обеспечения, перечень
инженерно-технических
мероприятий, содержание технологических решений
(внутренние инженерные системы)**

Подраздел 3

Система водоотведения

Часть 1

Внутренние системы водоотведения

ААБЭ-03-ДСЗ-ИОС-3.1

Заказчик: ООО «Артел Архитектс»

Проектировщик: ООО «СовИкоН»

Генеральный директор

Главный инженер проекта



Джамилев С.А.

Сафин Р.А.

г. Москва, 2022

Заверение проектной документации

Технические решения, принятые в проекте «Жилой комплекс» по адресу:
г. Москва, ЦАО, Садовническая ул., вл. 76/71, соответствуют требованиям экологических, санитарно-гигиенических, противопожарных, строительных норм и правил, действующих на территории Российской Федерации, а также обеспечивают безопасную для жизни и здоровья людей эксплуатацию объекта при их выполнении

Главный инженер проекта



Р.А. Сафин

Инв. № подл.	Подп. И дата	Взам. инв. №							Лист	
										2
Изм.	Кол.уч.	Лист	№ док.	Подп.	Дата	ААБЭ-03-ДСЗ-ИОС-3.1.3				

Содержание

Общие положения. 2

а) сведения о существующих и проектируемых системах канализации, водоотведения и станциях очистки сточных вод; 3

б) обоснование принятых систем сбора и отвода сточных вод, объема сточных вод, концентраций их загрязнений, способов предварительной очистки, применяемых реагентов, оборудования и аппаратуры; ... 3

в) обоснование принятого порядка сбора, утилизации и захоронения отходов - для объектов производственного назначения; 4

г) описание и обоснование схемы прокладки канализационных трубопроводов, описание участков прокладки напорных трубопроводов (при наличии), условия их прокладки, оборудование, сведения о материале трубопроводов и колодцев, способы их защиты от агрессивного воздействия грунтов и грунтовых вод 4

д) решения в отношении ливневой канализации и расчетного объема дождевых стоков;..... 5

е) решения по сбору и отводу дренажных вод 6

Согласовано							ААБЭ-03-ДСЗ-ИОС-3.1.ТЧ			
Взам. инв. №							Пояснительная записка	Стадия	Лист	Листов
								П	1	6
								ООО «СовИкоН»		
Подп. и дата										
Инв. № подл.	Изм.	Копуч.	Лист	№ док.	Подп.	Дата				
	ГИП		Сафин		<i>Сафин</i>	07.23				
	Разработал		Малянов		<i>Малянов</i>	07.23				
	Проверил		Шмелева		<i>Шмелева</i>	07.23				

На стояках и магистральных трубопроводах канализации устраиваются ревизии, а в местах поворота прочистки.

На стояках хозяйственно-бытовой канализации установлены ревизии:

- на всех стояках, в верхнем и нижнем этажах, а также через 3 этажа.
- на поворотах магистральных трубопроводах.

У места установки ревизий предусмотрена установка люков доступа.

Стояки канализации жилой части на последнем этаже выводятся через плоскую кровлю здания на 0,1м выше от обреза вентиляционной шахты.

Стояки водоотводящей сети присоединяются под углом 45° к сборному магистральному трубопроводу, проходящему под потолком парковки с уклоном в сторону выпусков.

Расчетные расходы хозяйственно-бытовых вод рассчитаны и сведены в таблицу 1.

Таблица 1. Расчетные показатели водоотведения.

Наименование системы	Расчетный расход стоков				Примечание
	м³/сут	м³/ч	л/с	При пожаре, л/с	
Общий расход					
Общий расход стоков на весь дом	114,08	10,58	4,65		
Жилая часть					
Общий расход стоков	113,04	10,69	4,61		
Административные помещения (диспетчерская)+тренажерный зал+ салон красоты					
Общий расход стоков	0,89	0,48	0,36		
Обслуживающий персонал					
Общий расход стоков	0,15	0,28	0,25		

в) обоснование принятого порядка сбора, утилизации и захоронения отходов - для объектов производственного назначения

Настоящим проектом не предусматривается.

г) описание и обоснование схемы прокладки канализационных трубопроводов, описание участков прокладки напорных трубопроводов (при наличии), условия их прокладки, оборудование, сведения о материале трубопроводов и колодцев, способы их защиты от агрессивного воздействия грунтов и грунтовых вод

Стояки системы хозяйственно-бытовой канализации выполнены из труб ПП Ø110мм, магистральные трубопроводы в подземной части предусмотрены из чугунных безраструбных труб Smart SML Ø100 мм.

Диаметры трубопроводов рассчитаны на пропуск максимального секундного расхода стоков.

Напорные участки хозяйственно-бытовой канализации от насосных установок выполнены из чугунных безраструбных труб Smart SML Ø50. На напорном участке от установок установить запорную арматуру, а обратный клапан состоит в комплекте к насосной установке.

При проходе пластмассовых трубопроводов через перекрытия, пространство между трубой и окружающим ее строительным элементом заполняется негорючим материалом, а также устанавливаются противопожарные муфты.

Соединение вертикальных и горизонтальных участков трубопроводов из труб SML предусмотрено при помощи соединительных хомутов.

Изм.	Копуч.	Лист	№ док.	Подп.	Дата
Изм.	Копуч.	Лист	№ док.	Подп.	Дата
Изм.	Копуч.	Лист	№ док.	Подп.	Дата

ААБЭ-03-ДСЗ-ИОС-3.1.ТЧ

Лист

4

д) решения в отношении ливневой канализации и расчетного объема дождевых стоков

Отвода поверхностных стоков от здания предусматривается в проектируемую сеть дождевой канализации.

Отвод поверхностного стока от здания предусматривается в самотечном режиме при помощи выпусков $\phi 100-150\text{мм}$.

Для отвода дождевых вод с кровель зданий предусматриваются внутренние водостоки.

Система внутренних водостоков включает: кровельные воронки, стояки, магистральные и разводящие сети с отводами от кровельных воронок, прочистки и ревизии, выпуски.

В соответствии с Техническим заданием на проектирование, отвод дождевых вод с кровли здания осуществляется посредством кровельных воронок с электроподогревом фирмы HL Hutterer & Lechner GmbH (или аналог).

Стояки внутреннего водостока прокладываются в шахтах. Магистральные трубопроводы внутреннего водостока прокладываются по подвальному этажу, далее по выпуску сток отводится в наружную сеть дождевой канализации.

Внутренние водостоки предусмотрены из чугунных безраструбных труб Smart SML, соединенных с помощью усиливающих хомутов SML Krallen.

Расчетный расход дождевых стоков для кровли с уклоном более 1,5% определяется в соответствии с п.21.10 СП 30.13330.2020 по формуле:

$$Q_{\text{дожд.}} = F \cdot q_5 / 10000$$

где, F - площадь кровли с учетом 30% примыкающих вертикальных поверхностей, м^2 ;

q_5 - интенсивность дождя, л/с с 1 га, продолжительностью 5 мин при периоде однократного превышения расчетной интенсивности, равной 1 году, вычисляемая по формуле:

$$q_5 = 4^n \cdot q_{20}.$$

$$q_5 = (4^{0,71}) \times 80 = 214,07 \text{ л/с}$$

Расход стоков составит (общий расход с кровли и террас):

$$Q_{\text{ложл.}} = 149,40 \text{ л/с.}$$

Прокладка магистральных трубопроводов предусмотрена под потолком, стояков - в шахтах. Трубопроводы в подвале изолируются для предотвращения выпадения конденсата.

На стояках устанавливаются ревизии на нижнем жилом этаже.

На горизонтальных трубопроводах в местах поворота, в начале горизонтальных участков, перед выпуском из здания устанавливаются прочистки и ревизии.

В соответствии с требованием п.21.7 СП 30.13330.2020 уклон трубопроводов внутреннего водостока принят не менее 0,005.

Для отведения поверхностных дождевых и талых стоков на территории застройки предусматривается строительство закрытой сети дождевой канализации, проектируемой по отдельному проекту.

На террасах последних этажей предусматривается установка водоприемных парапетных воронок с листоуловителями HL68H.0/75 (или аналог). Данные воронки подключаются к стоякам, прокладываемых в конструкции фасада здания, далее на отмокту. Воронки и стояки обогреваются с помощью греющего саморегулируемого кабеля. Материал стояков – трубопроводы из коррозионностойкой стали, бесшовные холодно- или теплодеформированные DN75 по ГОСТ 9941-81.

Взам. инв. №	Подп. и дата	Инв. № подл.	В соответствии с требованием п.21.7 СП 30.13330.2020 уклон трубопроводов внутреннего водостока принят не менее 0,005.						Лист	
			Для отведения поверхностных дождевых и талых стоков на территории застройки предусматривается строительство закрытой сети дождевой канализации, проектируемой по отдельному проекту.							
			На террасах последних этажей предусматривается установка водоприемных парапетных воронок с листоуловителями НЛ68Н.0/75 (или аналог). Данные воронки подключаются к стоякам, прокладываемых в конструкции фасада здания, далее на отмостку. Воронки и стояки обогреваются с помощью греющего саморегулируемого кабеля. Материал стояков – трубопроводы из коррозионностойкой стали, бесшовные холодно- или теплодеформированные DN75 по ГОСТ 9941-81.							
Изм.	Копуч.	Лист	Недок.	Подп.	Дата	ААБЭ-03-ДСЗ-ИОС-3.1.ТЧ				5

е) решения по сбору и отводу дренажных вод

Для сбора и отвода с пола, от оборудования условно-чистых вод из технических помещений (приточных венткамер, насосных станций, ИТП), а также воды с пола парковки после срабатывания АУПТ проектом предусмотрена система дренажной канализации.

По периметру парковки, для сбора воды после срабатывания системы АУПТ, предусмотрены трапы на -1 этаже и приемки на -2 этаже размерами не менее 1 м³. В этих приемках установлены два дренажных насоса ГНОМ 25-20 Q=25м³/ч, H=20м (или аналог), без ШУ, с поплавковым выключателем.

В помещениях приточных вент. камер предусмотрены трапы на -1 этаже и приемки на -2 этаже размерами 0,6х0,6х0,6 (h). В этих приемках установлен один дренажный насос ГНОМ 10-10 Q=10м³/ч, H=10м, (или аналог).

В помещении ИТП на -1 этаже предусмотрен трап и приямок 0,6х0,6х0,8 (h) на -2 этаже (общий для насосной, ИТП) с установкой дренажных насосов Wilo-Drine TMT 32M 113/7,5Si с повышенной температурой перекачиваемой жидкости (до 95°C) (1раб+1рез) с ШУ и комплектом поплавков.

В блоках кладовых, где проходят трубопроводы со спускной арматурой, с устройствами прочистки предусмотрены на -2 этаже приямки.

В помещениях -1 этажа установлены трапы, стоки от которых отводятся в приемки на -2 этаже.

На напорных линиях от насосов устанавливается запорная арматура и обратный клапан.

От дренажных насосов, по напорным трубопроводам, стоки направляются в магистральный самотечный трубопровод расположенный на -1 этаже (дренажная канализация), с последующим выпуском в наружные сети дождевой канализации.

При проходе трубопроводов через перекрытия и стены пространство между трубой и окружающим ее строительным элементом заполняется негорючим материалом, а также устанавливаются противопожарные муфты.

Напорные трубопроводы дренажной канализации выполняются из стальных оцинкованных электросварных труб $\phi 40-50$ мм по ГОСТ 10704-91. Напорные участки дождевой канализации подключить к самотечным магистральным трубопроводам через петлю гашения напора.

Марки и тип дренажных насосов указаны в табл.2.

Таблица 2. Ведомости насосного оборудования для отвода дренажных вод.

Наименование	Тип, марка	Завод-изготовитель, поставщик	Примечание
Дренажные насосы			
Wilo-Drine TMT 32M 113/7,5Si (или аналог)	TMT 32M 113/7,5Si	Wilo	Стационарный насос с ШУ
ГНОМ 25-20 Q=25м ³ /ч, H=20м, t=40°C (или аналог)	ГНОМ 25-20	Московский насосный завод	Стационарный насос без ШУ, с поплавковым выключателем
ГНОМ 10-10 Q=10м ³ /ч, H=10м, t=40°C (или аналог)	ГНОМ 10-10	Московский насосный завод	Стационарный насос без ШУ, с поплавковым выключателем
WILO Drainlift BOX 40/11 (или аналог)	BOX 40/11	Wilo	Помещение ТБО

Взам. инв. №	
Подп. и дата	
Инв. № подл.	

						ААБЭ-03-ДС3-ИОС-3.1.ТЧ	Лист
							6
Изм.	Копуч.	Лист	№ док.	Подп.	Дата		

- К2

К2.1

К1

К1.1

К1н

К4н

К4

трубопровод ливневой канализации жилого корпуса

трубопровод ливневой канализации паркинга

трубопровод хозяйственно-бытовой канализации жилых квартир

трубопровод хозяйственно-бытовой канализации нежилых помещений

трубопровод хозяйственно-бытовой канализации жилых квартир (напорный)

трубопровод дренажной канализации (напорный)

трубопровод дренажной канализации
- II—

Прочистка

Противопожарная муфта

Шаровый кран


Обратный клапан

Умывальник

Унитаз

Трап

Водосточная воронка

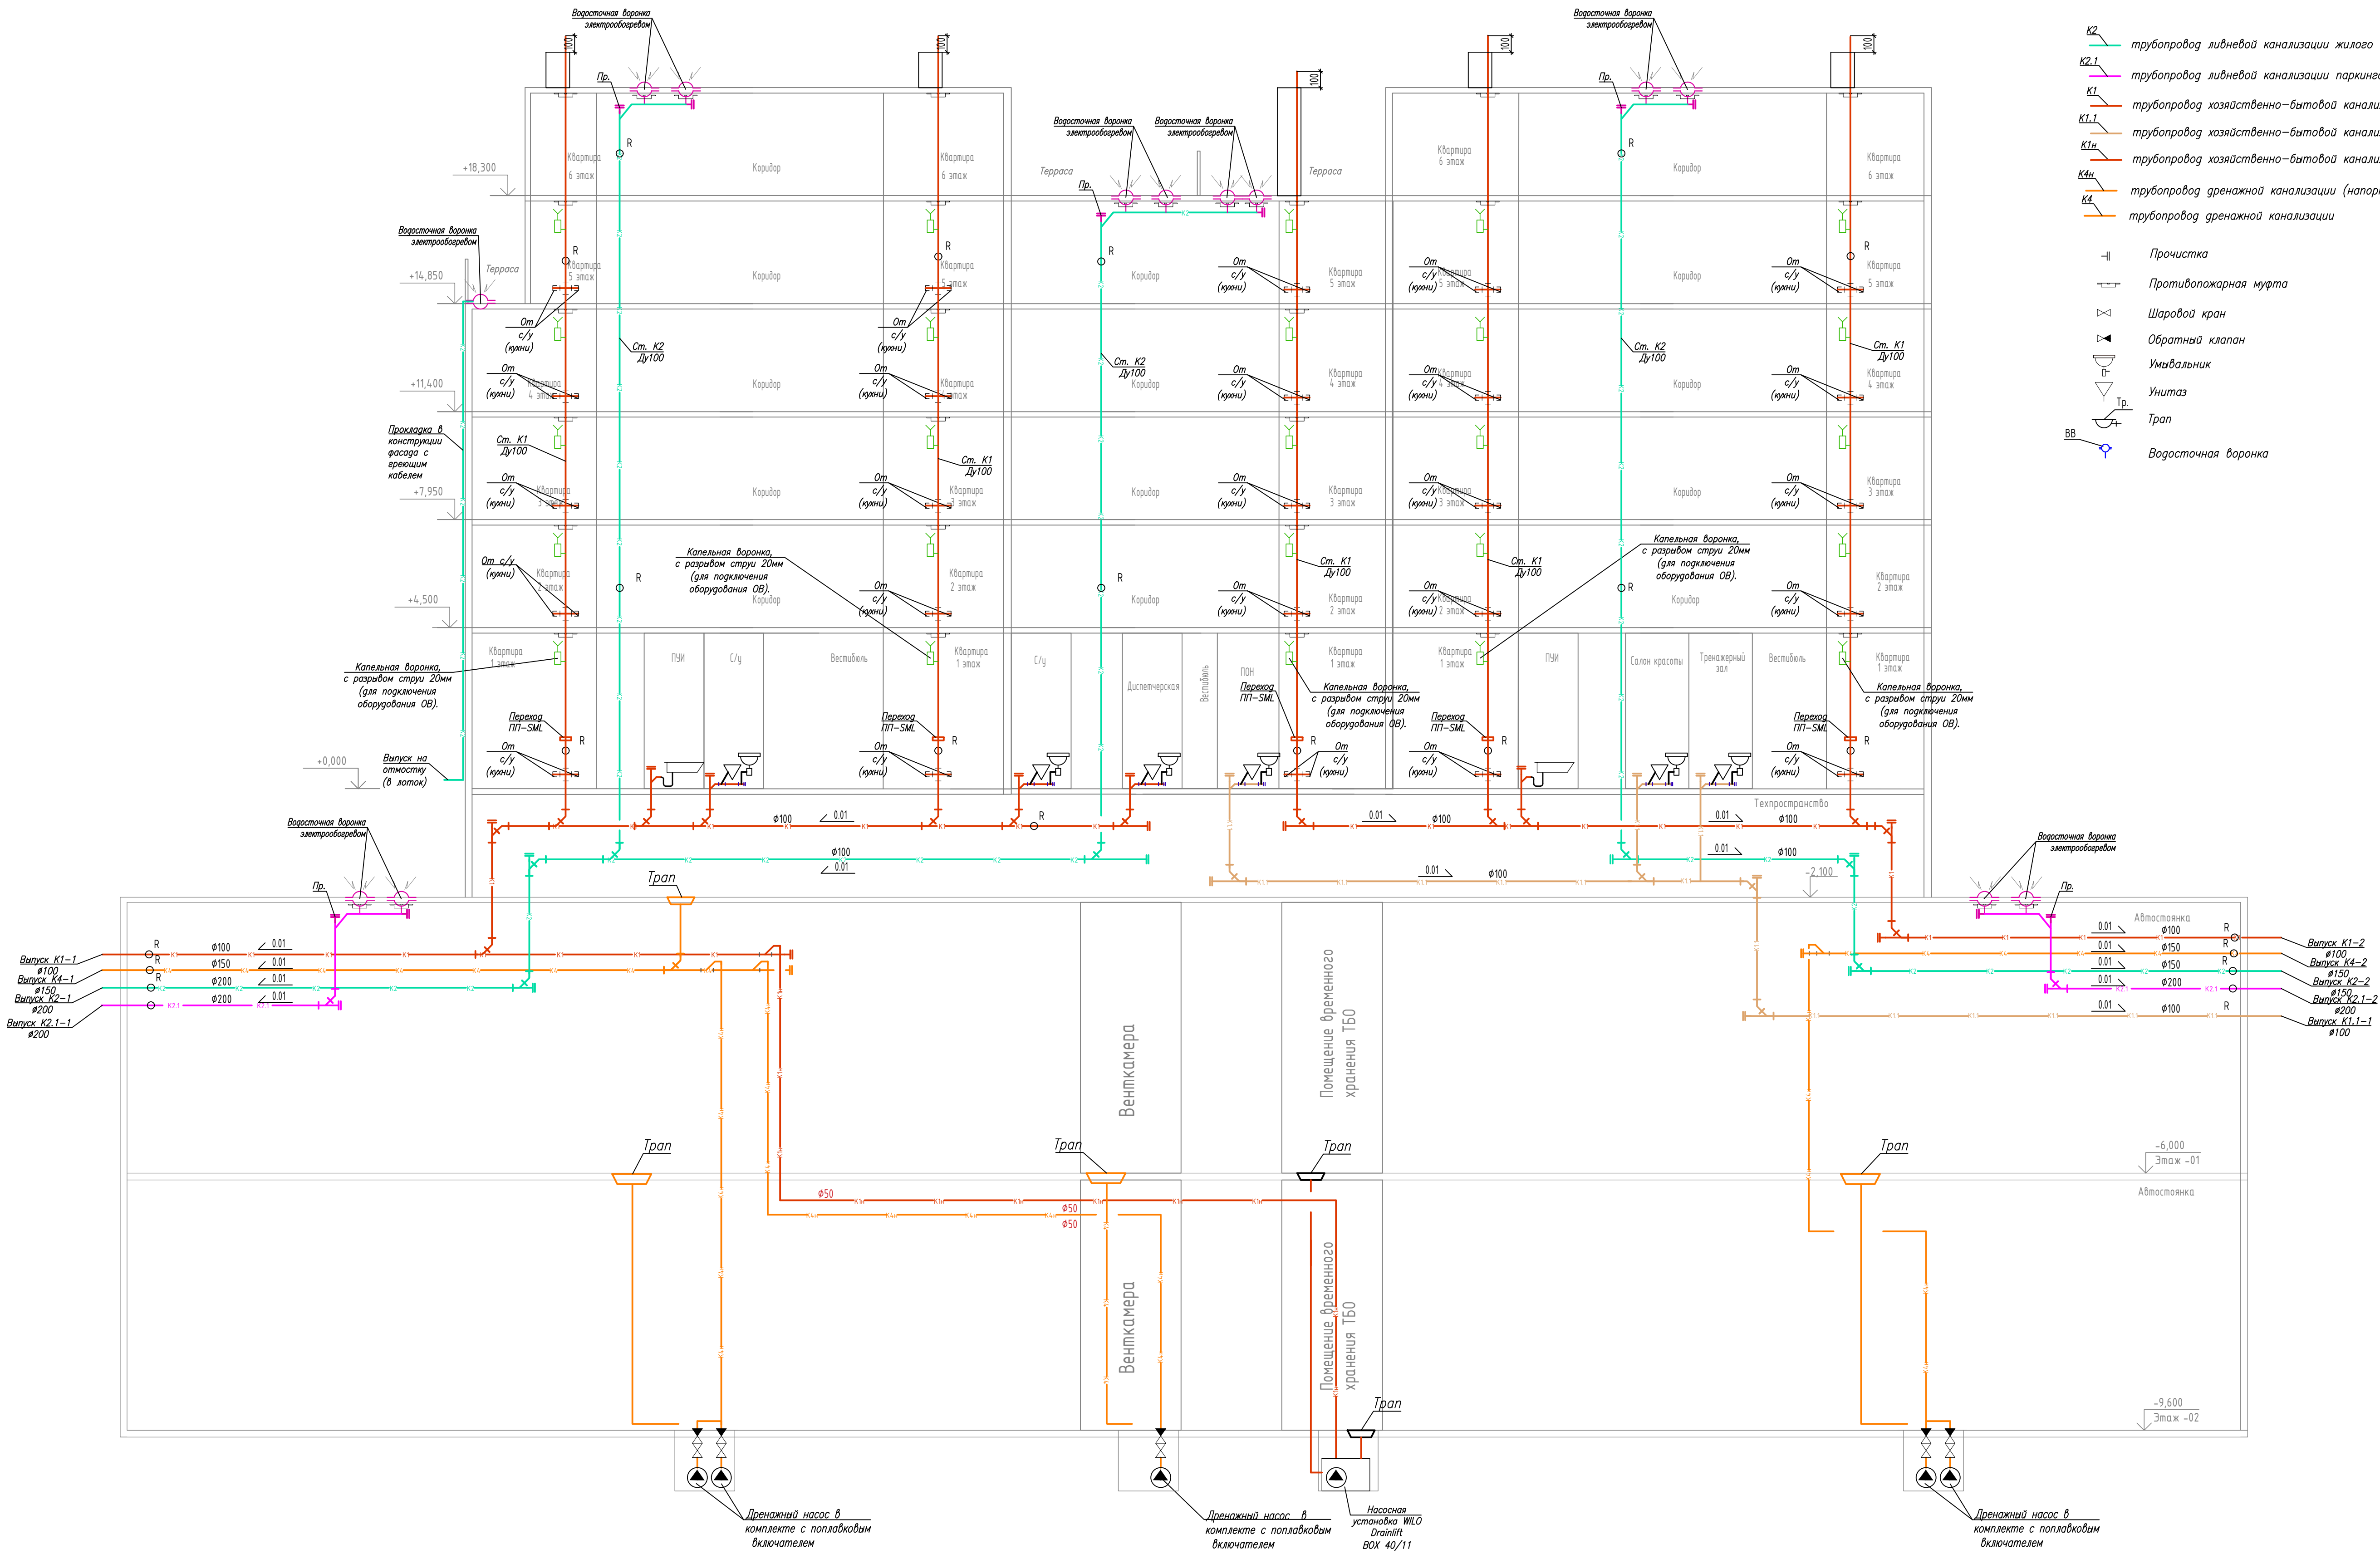

Примечания:

1.

Количество стояков показано условно. Диаметр трубопроводов и количество выпусков уточняется в рабочей части проекта.
2.

Количество и направления подключений к стоякам хозяйственно-бытовой канализации жилой указаны условно.
3.

Количество и расстановка ревизий и прочисток уточняется в рабочей части проекта.
4.

Количество и расстановка водосточных воронок кровли жилой части уточняется в рабочей части проекта.
5.


Отводы от водосточных воронок и стояки водостока жилой части теплоизолировать. Теплоизоляция трубопроводов условно не указана.
6.

Трубопроводы водостока в паркинге теплоизолировать изоляцией П1, условно не указана.

						ААБЭ-03-ДС-ИОС-3.1		
						ЖИЛОЙ КОМПЛЕКС		
						ПО АДРЕСУ: Г. МОСКВА, ЦАО, САДОВНИЧЕСКАЯ УЛ., ВЛ. 76/71		
Изм.	Кол-во	Лист	№ док	Подпись	Дата	Внутренние системы водоотведения	Стадия	Лист
Разработал	Маянгов	12.22					П	1
Проверил	Шмелева	12.22				Принципиальная схема систем водоотведения. (Корпус 1).	ООО «СовИкоН»	
Гип	Сафин	12.22						

Корпус №2

Условные обозначения

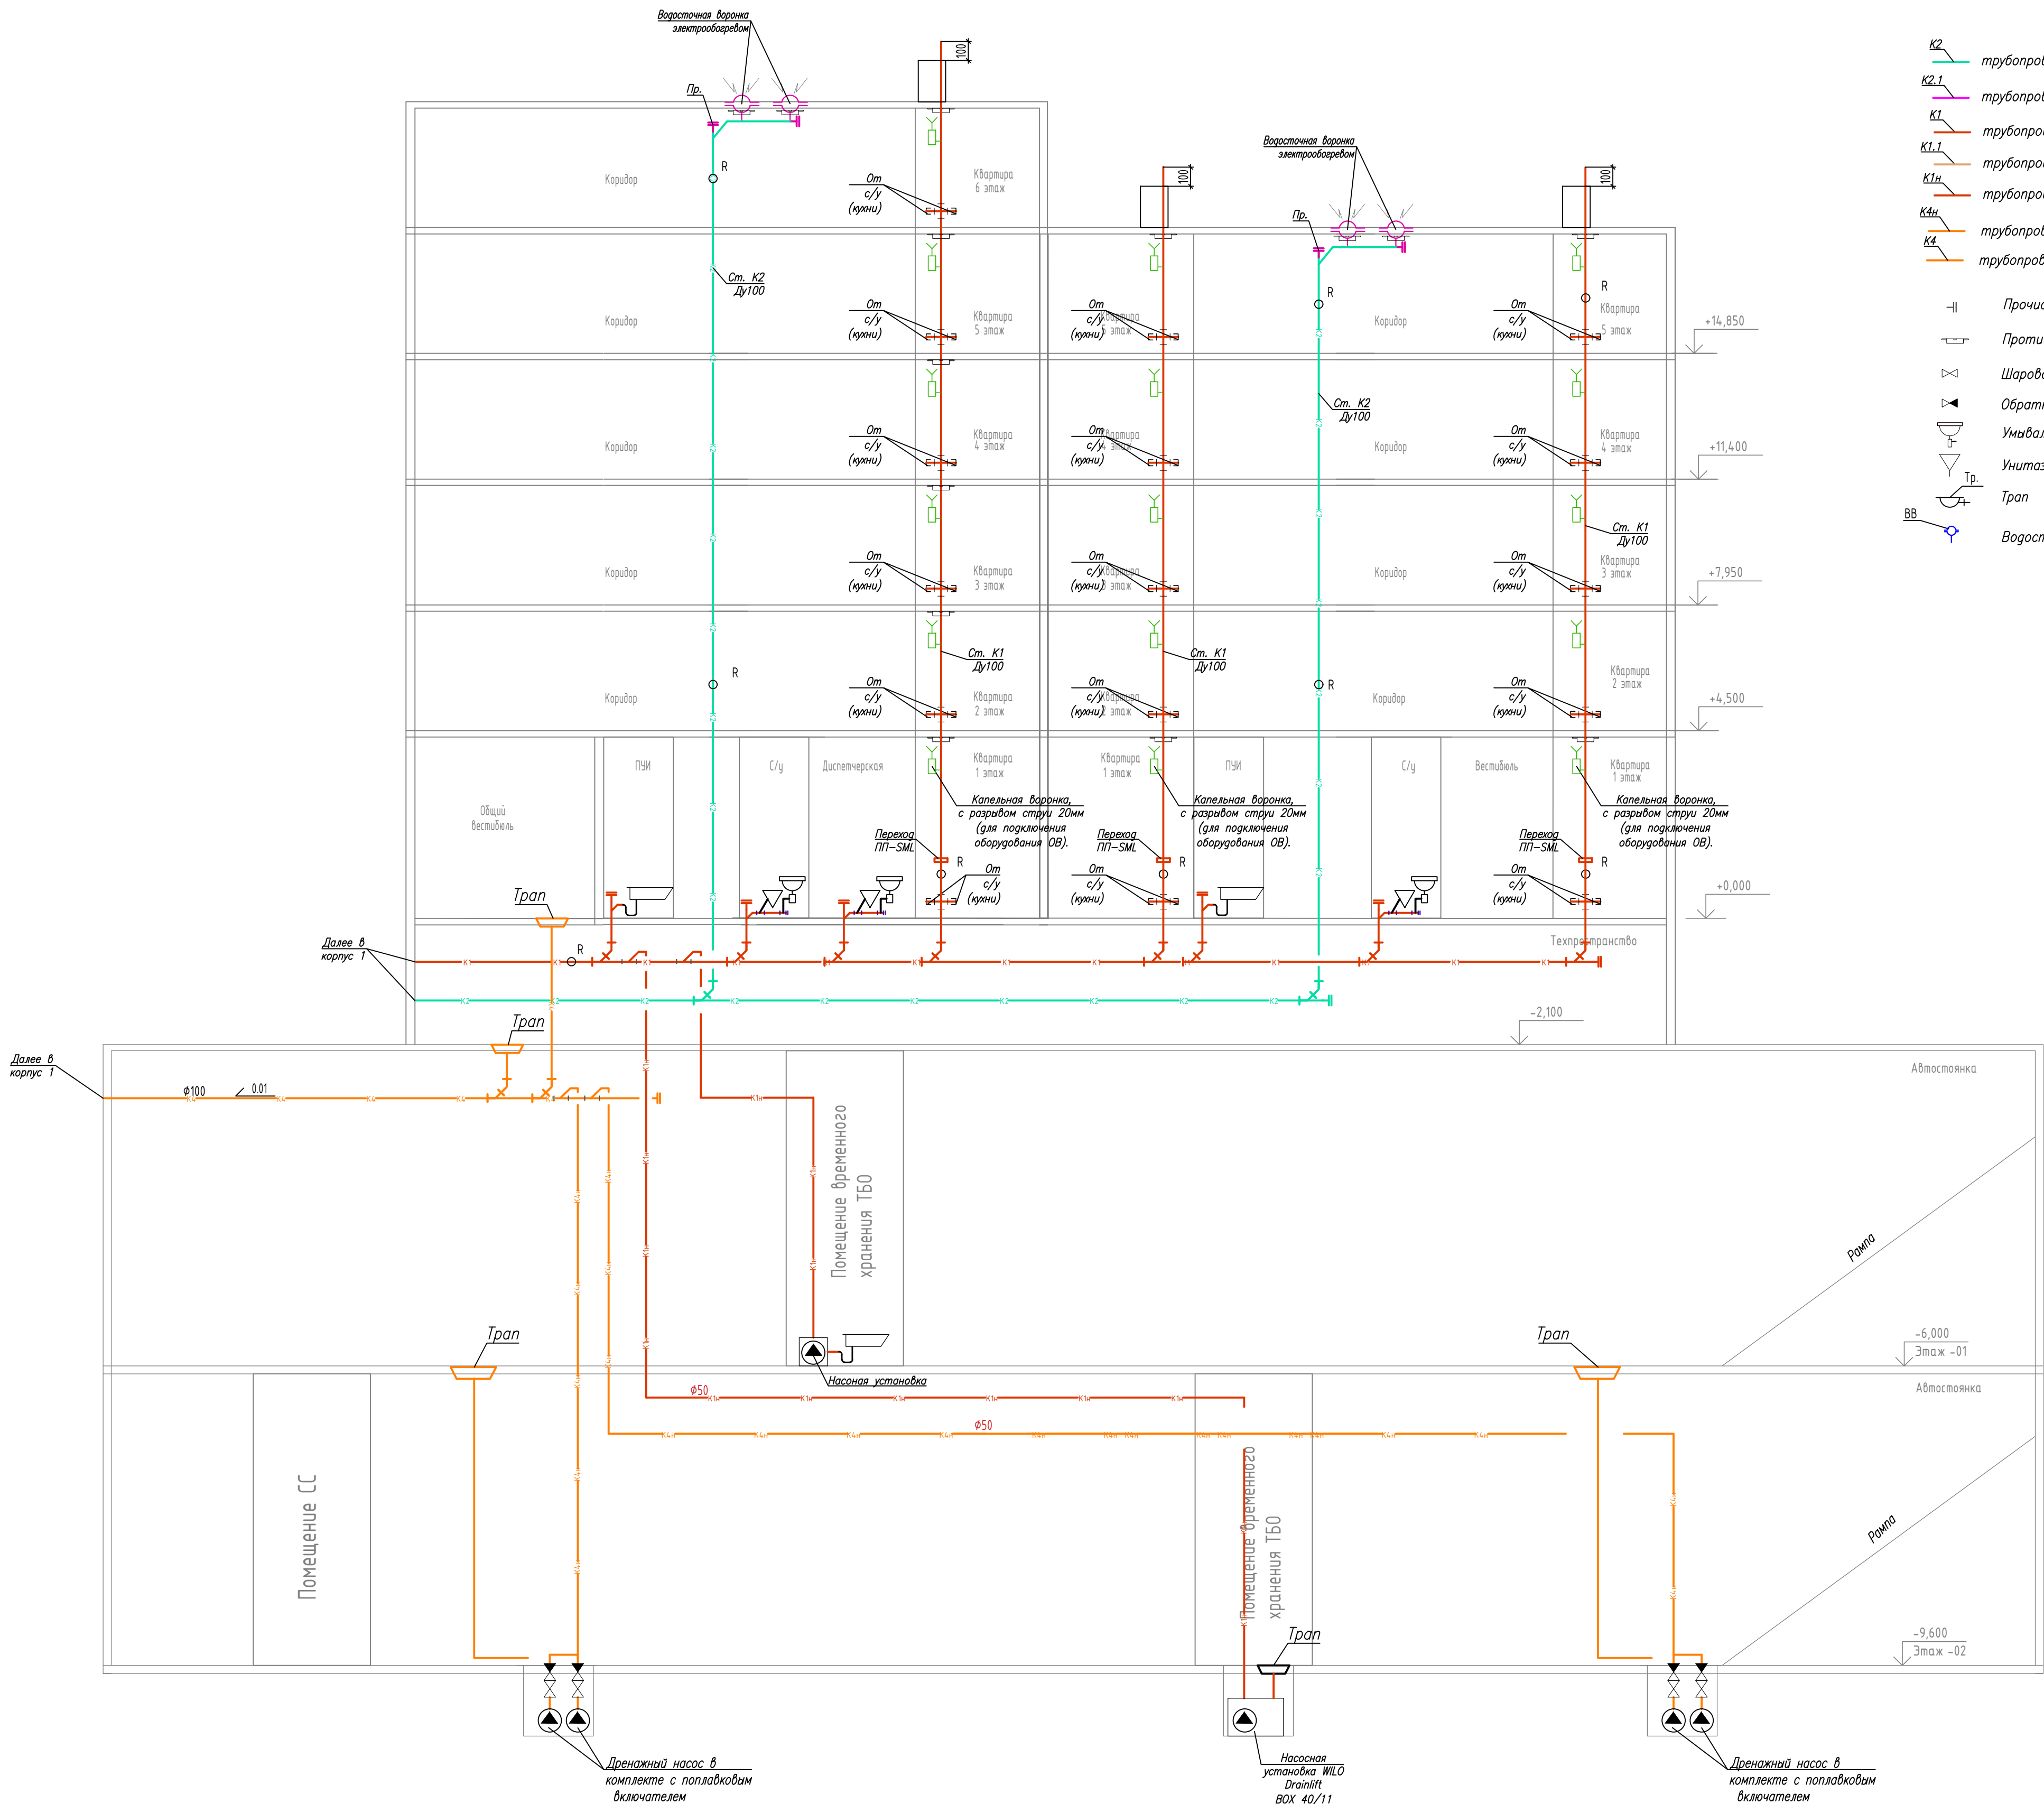


- K2 труборывод ливневой канализации жилого корпуса
- K2.1 труборывод ливневой канализации паркинга
- K1 труборывод хозяйственно-бытовой канализации жилых квартир
- K1.1 труборывод хозяйственно-бытовой канализации нежилых помещений
- K1n труборывод хозяйственно-бытовой канализации жилых квартир (напорный)
- K4n труборывод дренажной канализации (напорный)
- K4 труборывод дренажной канализации
- Прочистка
- Противопожарная муфта
- Шаровый кран
- Обратный клапан
- Умывальник
- Унитаз
- Трап
- Водосточная воронка

Примечания:

- Количество стояков показано условно. Диаметр труборыводов и количество выпусков уточняется в рабочей части проекта.
- Количество и направления подключений к стоякам хозяйственно-бытовой канализации жилой указаны условно.
- Количество и расстановка ревизий и прочисток уточняется в рабочей части проекта.
- Количество и расстановка водосточных воронок кровли жилой части уточняется в рабочей части проекта.
- Отводы от водосточных воронок и стояки водостока жилой части теплоизолировать. Теплоизоляция труборыводов условно не указана.
- Труборыводы водостока в паркинге теплоизолировать изоляцией П1, условно не указана.

						ААБЗ-03-ДС-ИОС-3.1				
						ЖИЛОЙ КОМПЛЕКС ПО АДРЕСУ: Г. МОСКВА, ЦАО, САДОВНИЧЕСКАЯ УЛ, ВЛ. 76/71				
Изм.	Кол-во	Лист	№ док	Подпись	Дата	Внутренние системы водоотведения	Стадия	Лист	Листов	
Разработал		Малянов			12.22		П	2		
Проверил		Шмелева			12.22					
						Принципиальная схема систем водоотведения. (Корпус 2).	ООО «СовИкоН»			
ГИП		Сафин			12.22					

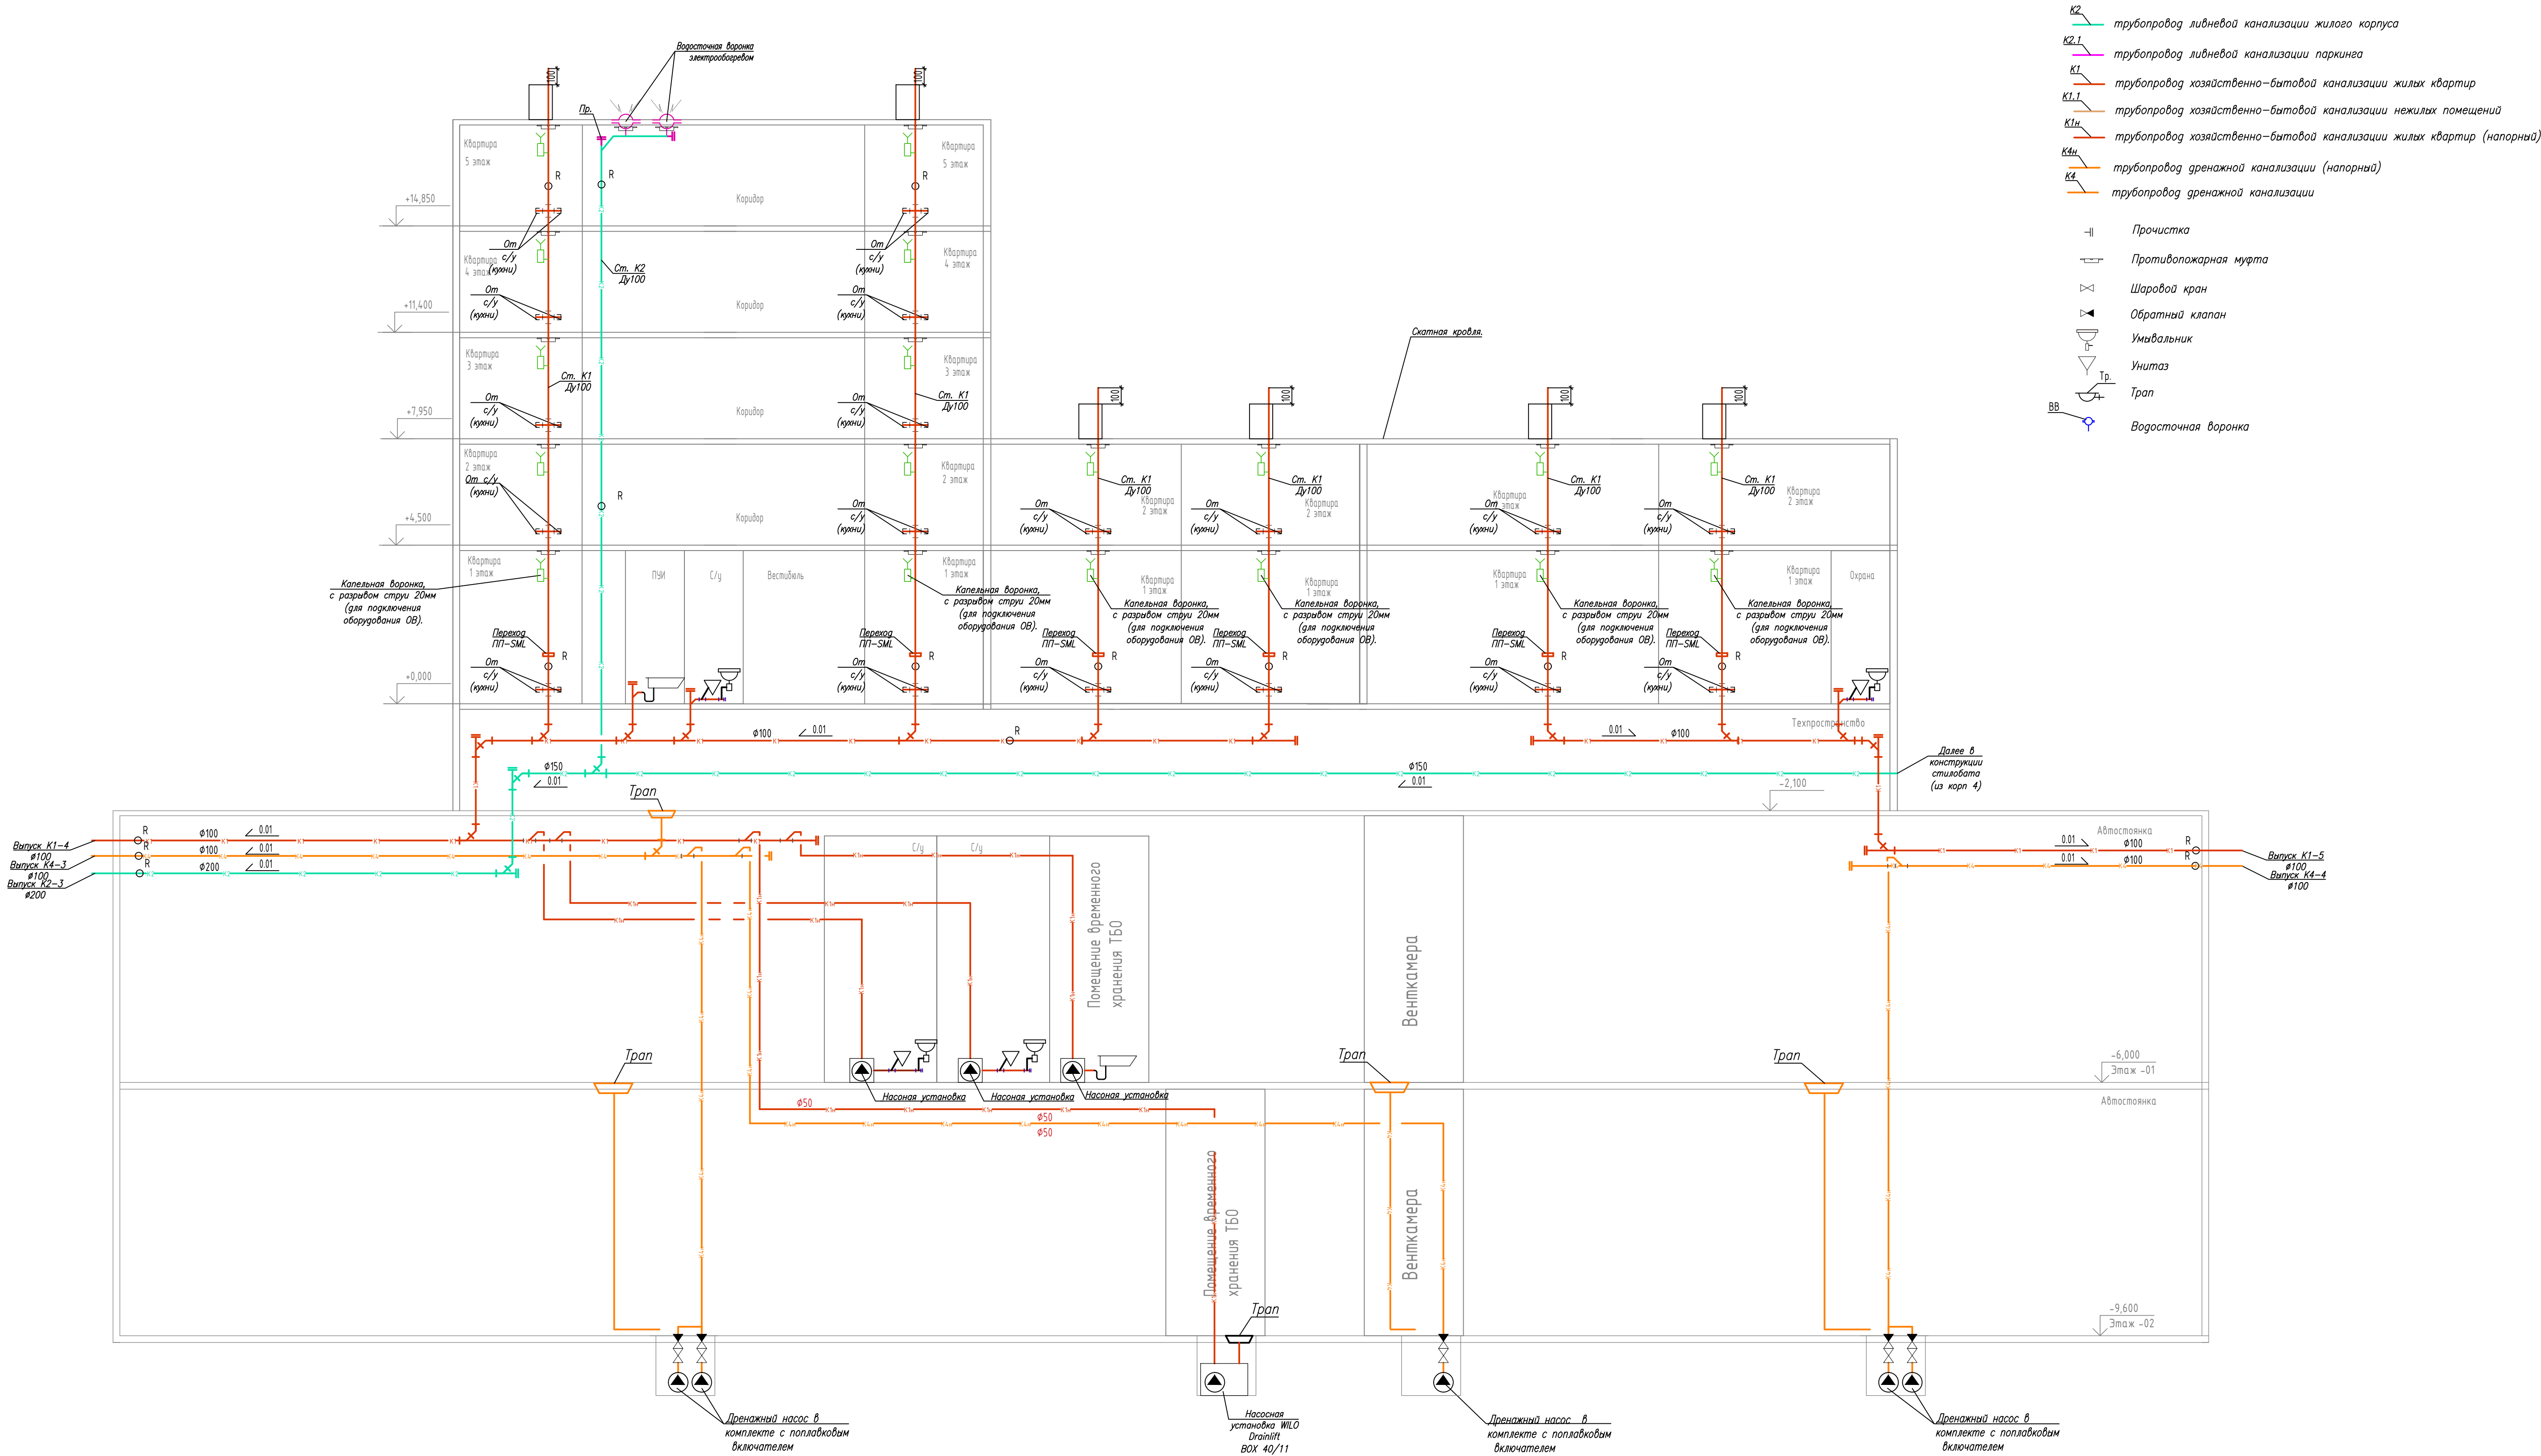


Примечания:

1. Количество стояков показано условно. Диаметр трубопроводов и количество выпусков уточняется в рабочей части проекта.
2. Количество и направления подключений к стоякам хозяйственно-бытовой канализации жилой части указаны условно.
3. Количество и расстановка ревизий и прочисток уточняется в рабочей части проекта.
4. Количество и расстановка водосточных воронок кровли жилой части уточняется в рабочей части проекта.
5. Отводы от водосточных воронок и стояки водостока жилой части теплоизолировать. Теплоизоляция трубопроводов условно не указана.
6. Трубопроводы водостока в паркинге теплоизолировать изоляцией ПИ, условно не указана.

						ААБЗ-03-ДСЗ-ИОС-3.1		
						ЖИЛОЙ КОМПЛЕКС ПО АДРЕСУ: Г. МОСКВА, ЦАО, САДОВНИЧЕСКАЯ УЛ, ВЛ. 76/71		
Изм.	Кол.уч.	Лист	№ док	Подпись	Дата	Внутренние системы водоотведения	Стадия	Лист
Разработал	Маянгов	12.22					П	3
Проверил	Шмелева	12.22				Принципиальная схема систем водоотведения. (Корпус 3).	ООО «СовИкоН»	
ГИП	Сафин	12.22						

Корпус №4

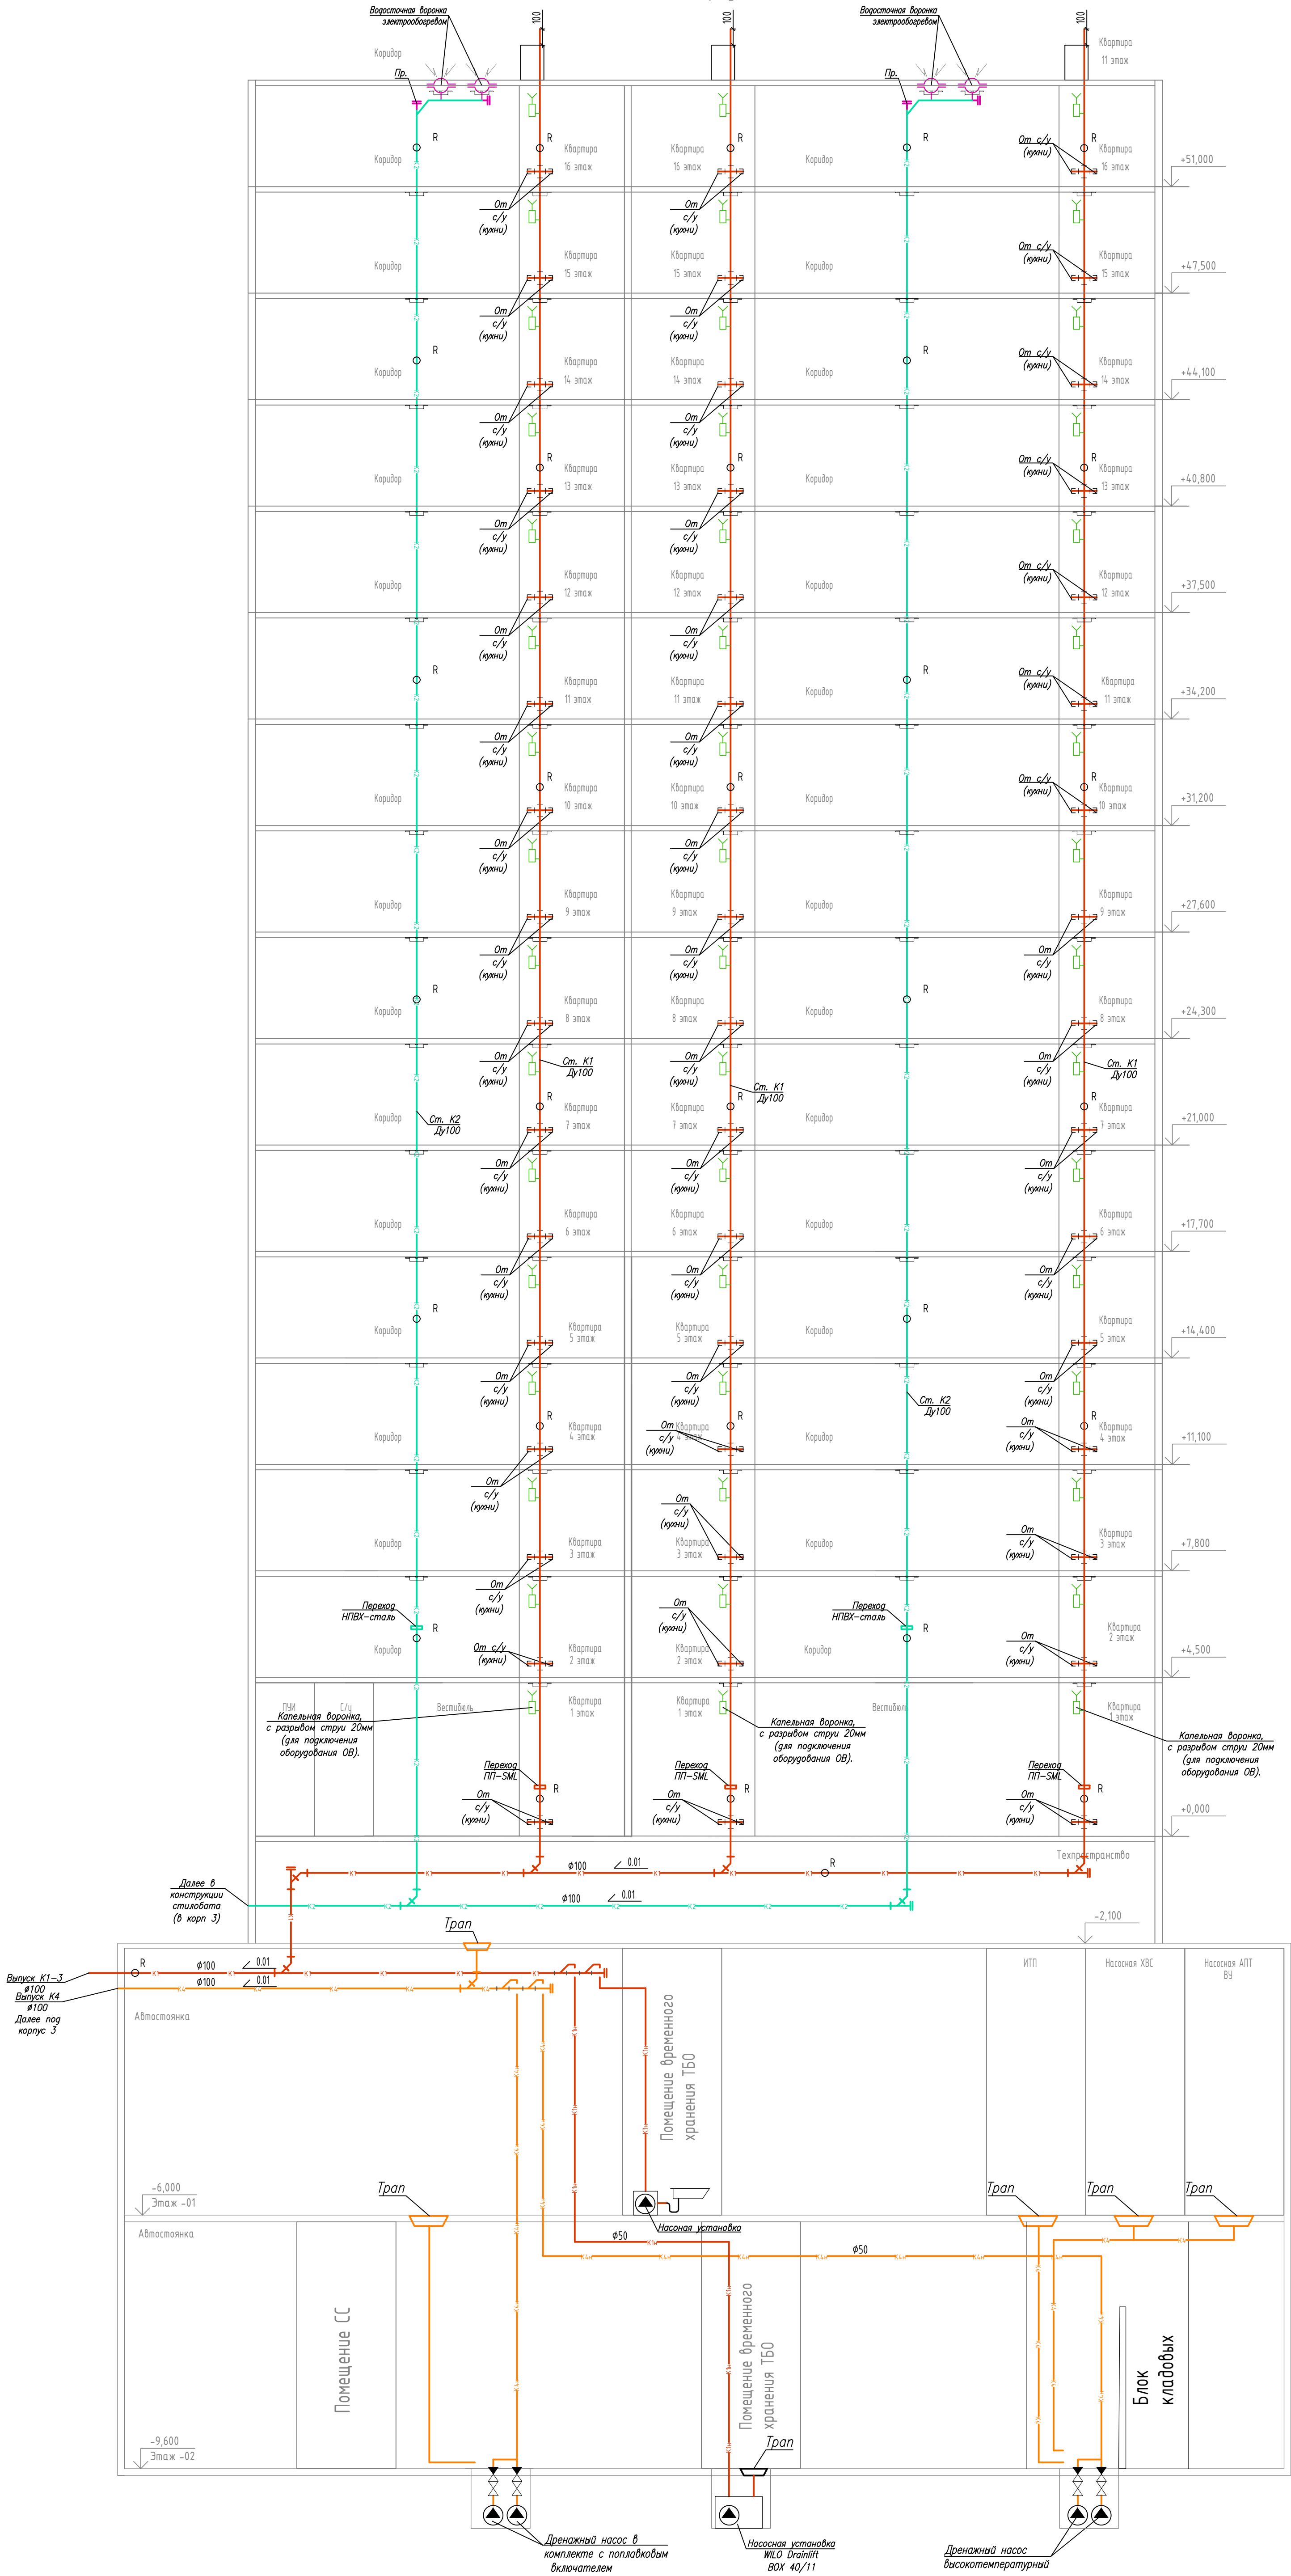




Условные обозначения

- K2 трубапровод ливневой канализации жилого корпуса
- K2.1 трубапровод ливневой канализации паркинга
- K1 трубапровод хозяйственно-бытовой канализации жилых квартир
- K1.1 трубапровод хозяйственно-бытовой канализации нежилых помещений
- K4n трубапровод хозяйственно-бытовой канализации жилых квартир (напорный)
- K4 трубапровод дренажной канализации (напорный)
- Прочистка
- Противопожарная муфта
- Шаровый кран
- Обратный клапан
- Умывальник
- Унитаз
- Трап
- Водосточная воронка

Примечания:

- Количество стояков показано условно. Диаметр трубопроводов и количество выпусков уточняется в рабочей части проекта.
- Количество и направления подключений к стоякам хозяйственно-бытовой канализации жилой указаны условно.
- Количество и расстановка ревизий и прочисток уточняется в рабочей части проекта.
- Количество и расстановка водосточных воронок кровли жилой части уточняется в рабочей части проекта.
- Отводы от водосточных воронок и стояки водостока жилой части теплоизолировать. Теплоизоляция трубопроводов условно не указана.
- Трубопроводы водостока в паркинге теплоизолировать изоляцией П, условно не указана.

					ААБЗ-03-ДСЗ-ИОС-3.1				
					ЖИЛОЙ КОМПЛЕКС ПО АДРЕСУ: Г. МОСКВА, ЦАО, САДОВНИЧЕСКАЯ УЛ., ВЛ. 76/71				
Изм.	Колуч	Лист № док	Подпись	Дата	Внутренние системы водоотведения	Стадия	Лист	Листов	
Разработал		Малков	<i>Малков</i>	12.22		П	4		
Проверил		Шмелева	<i>Шмелева</i>	12.22					
					Принципиальная схема систем водоотведения. (Корпус 4).	ООО «СовИкоН»			
ГИП		Сафин	<i>Сафин</i>	12.22					

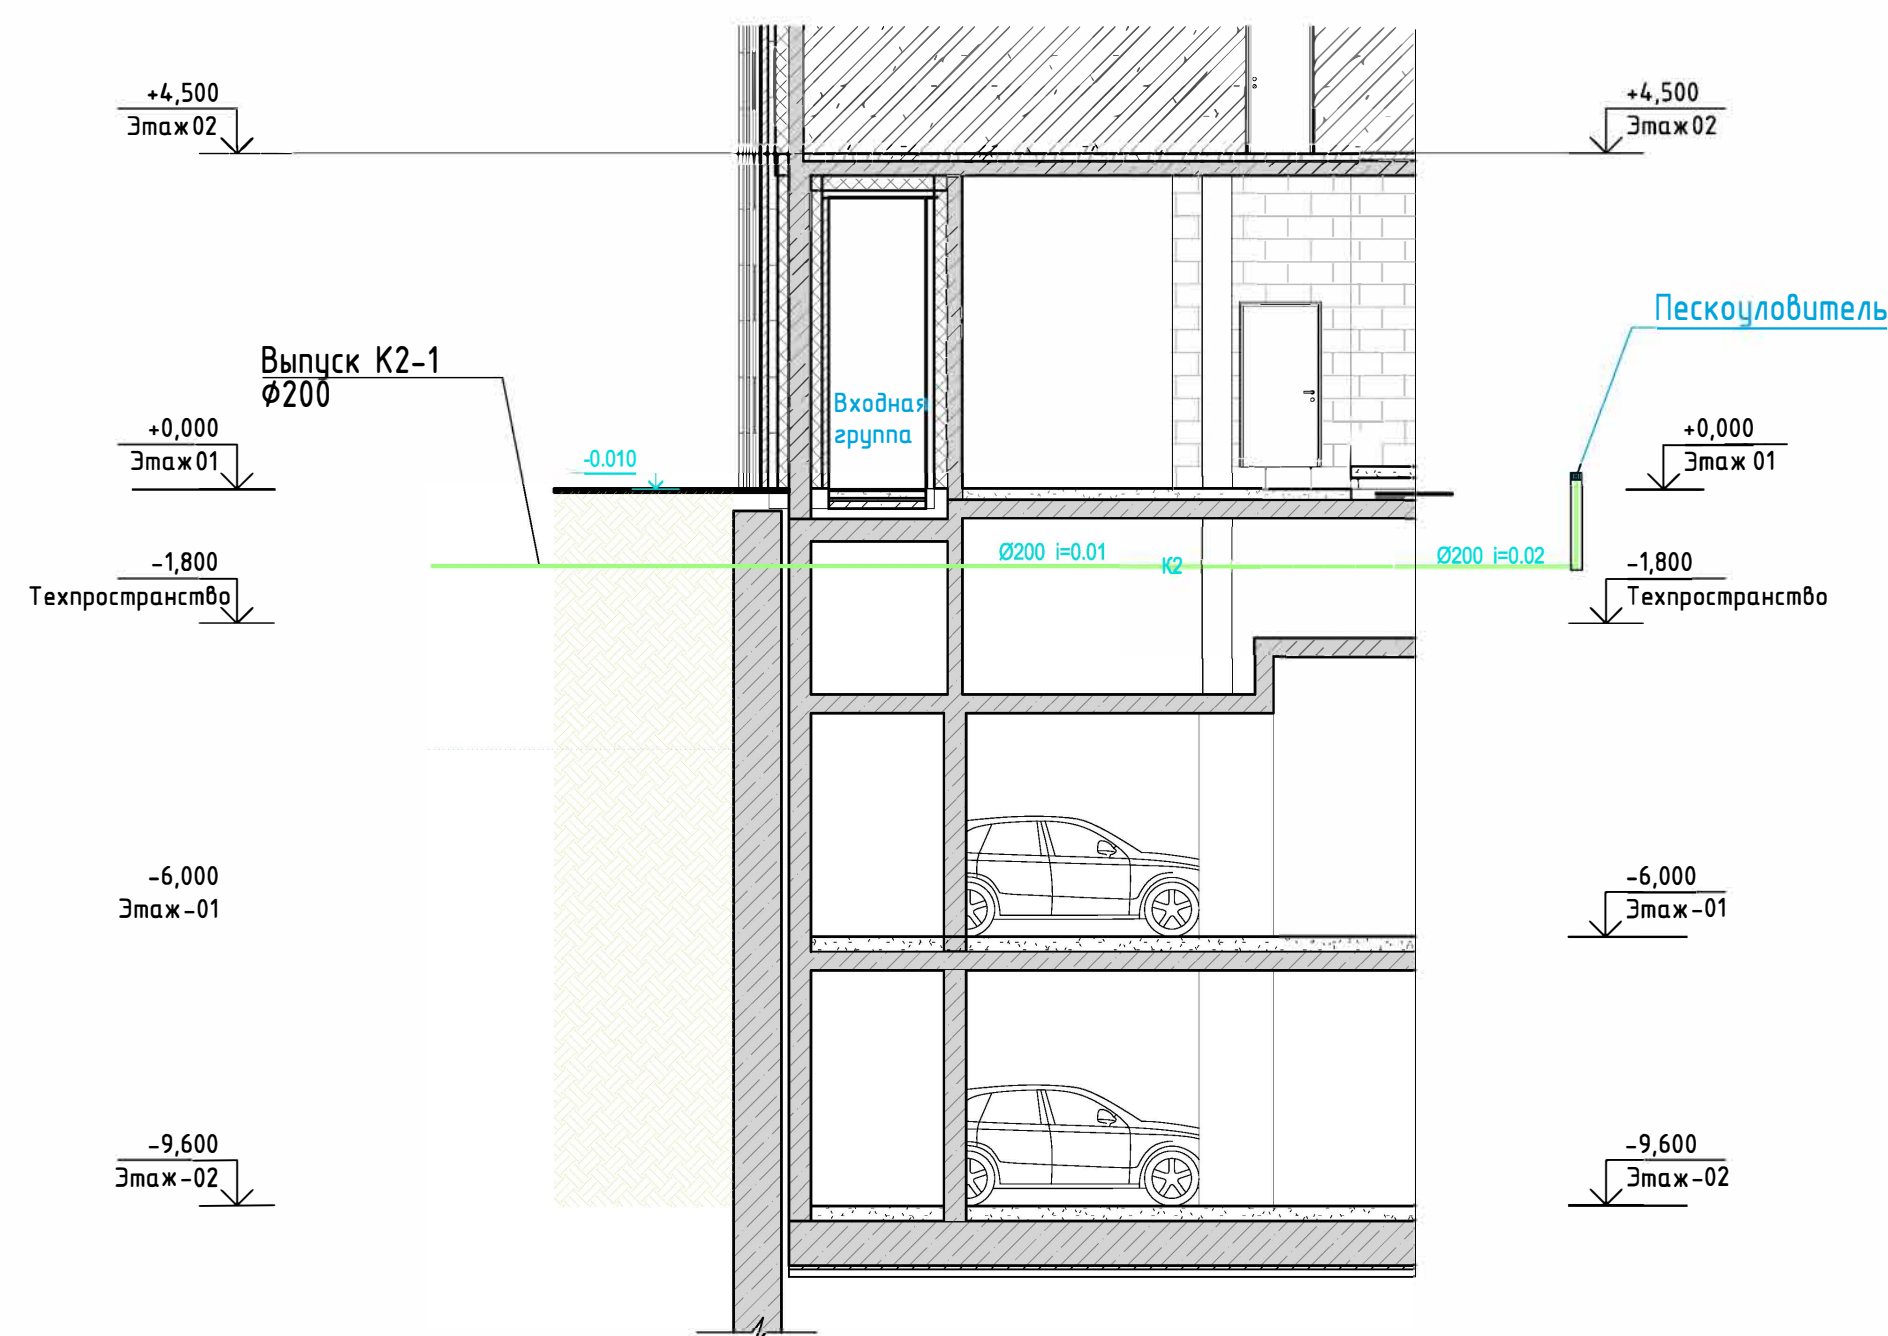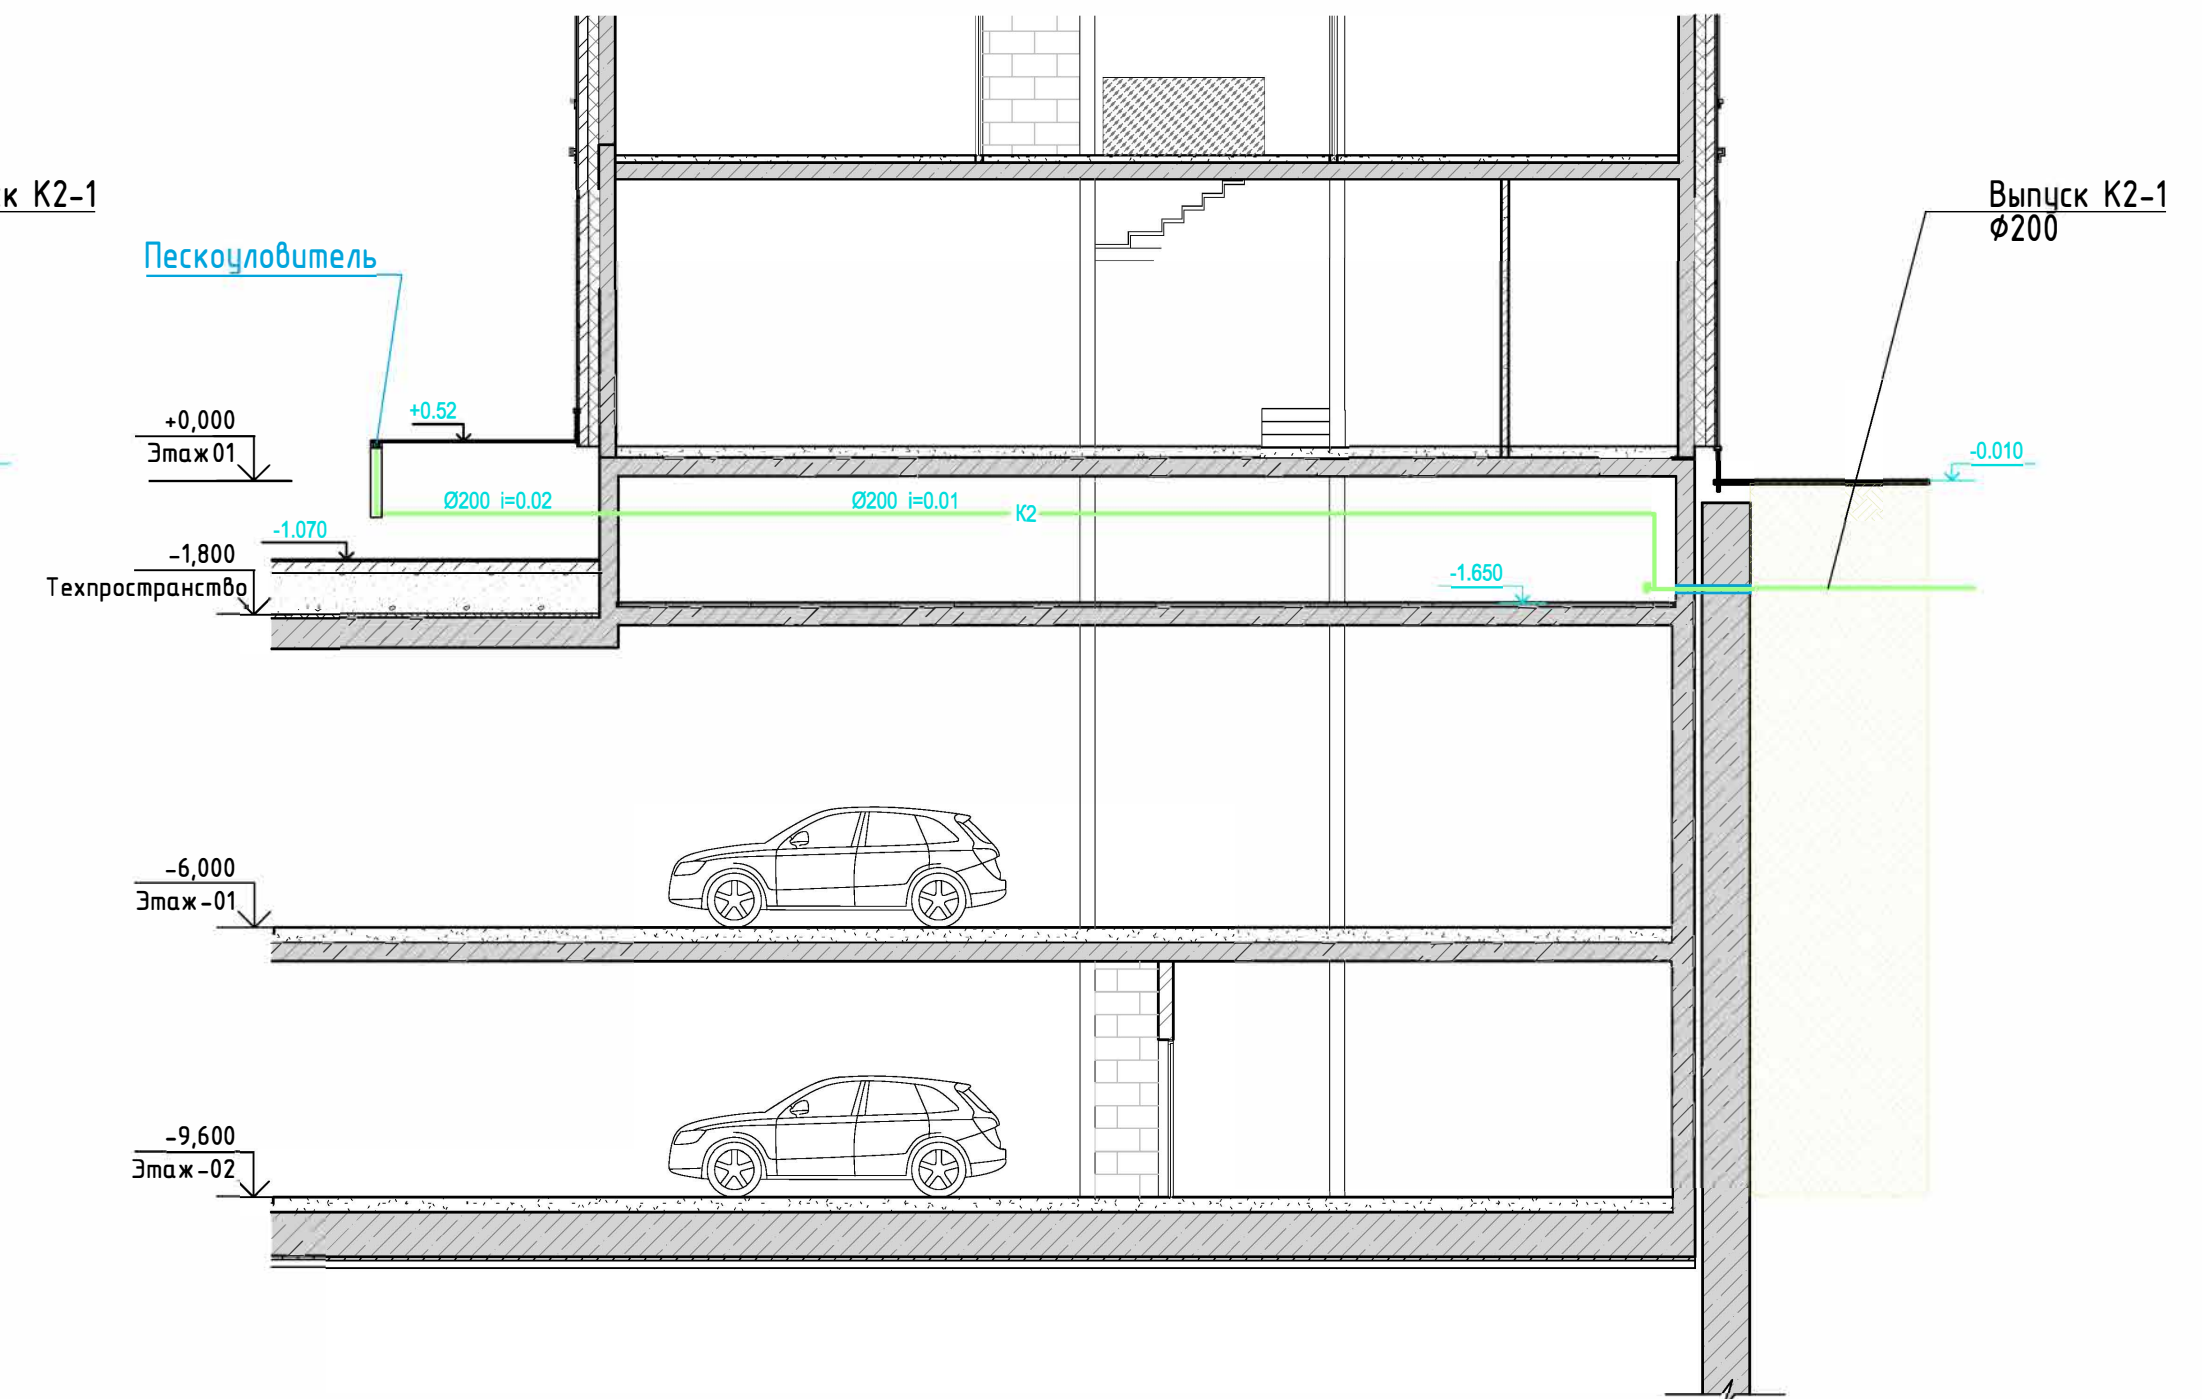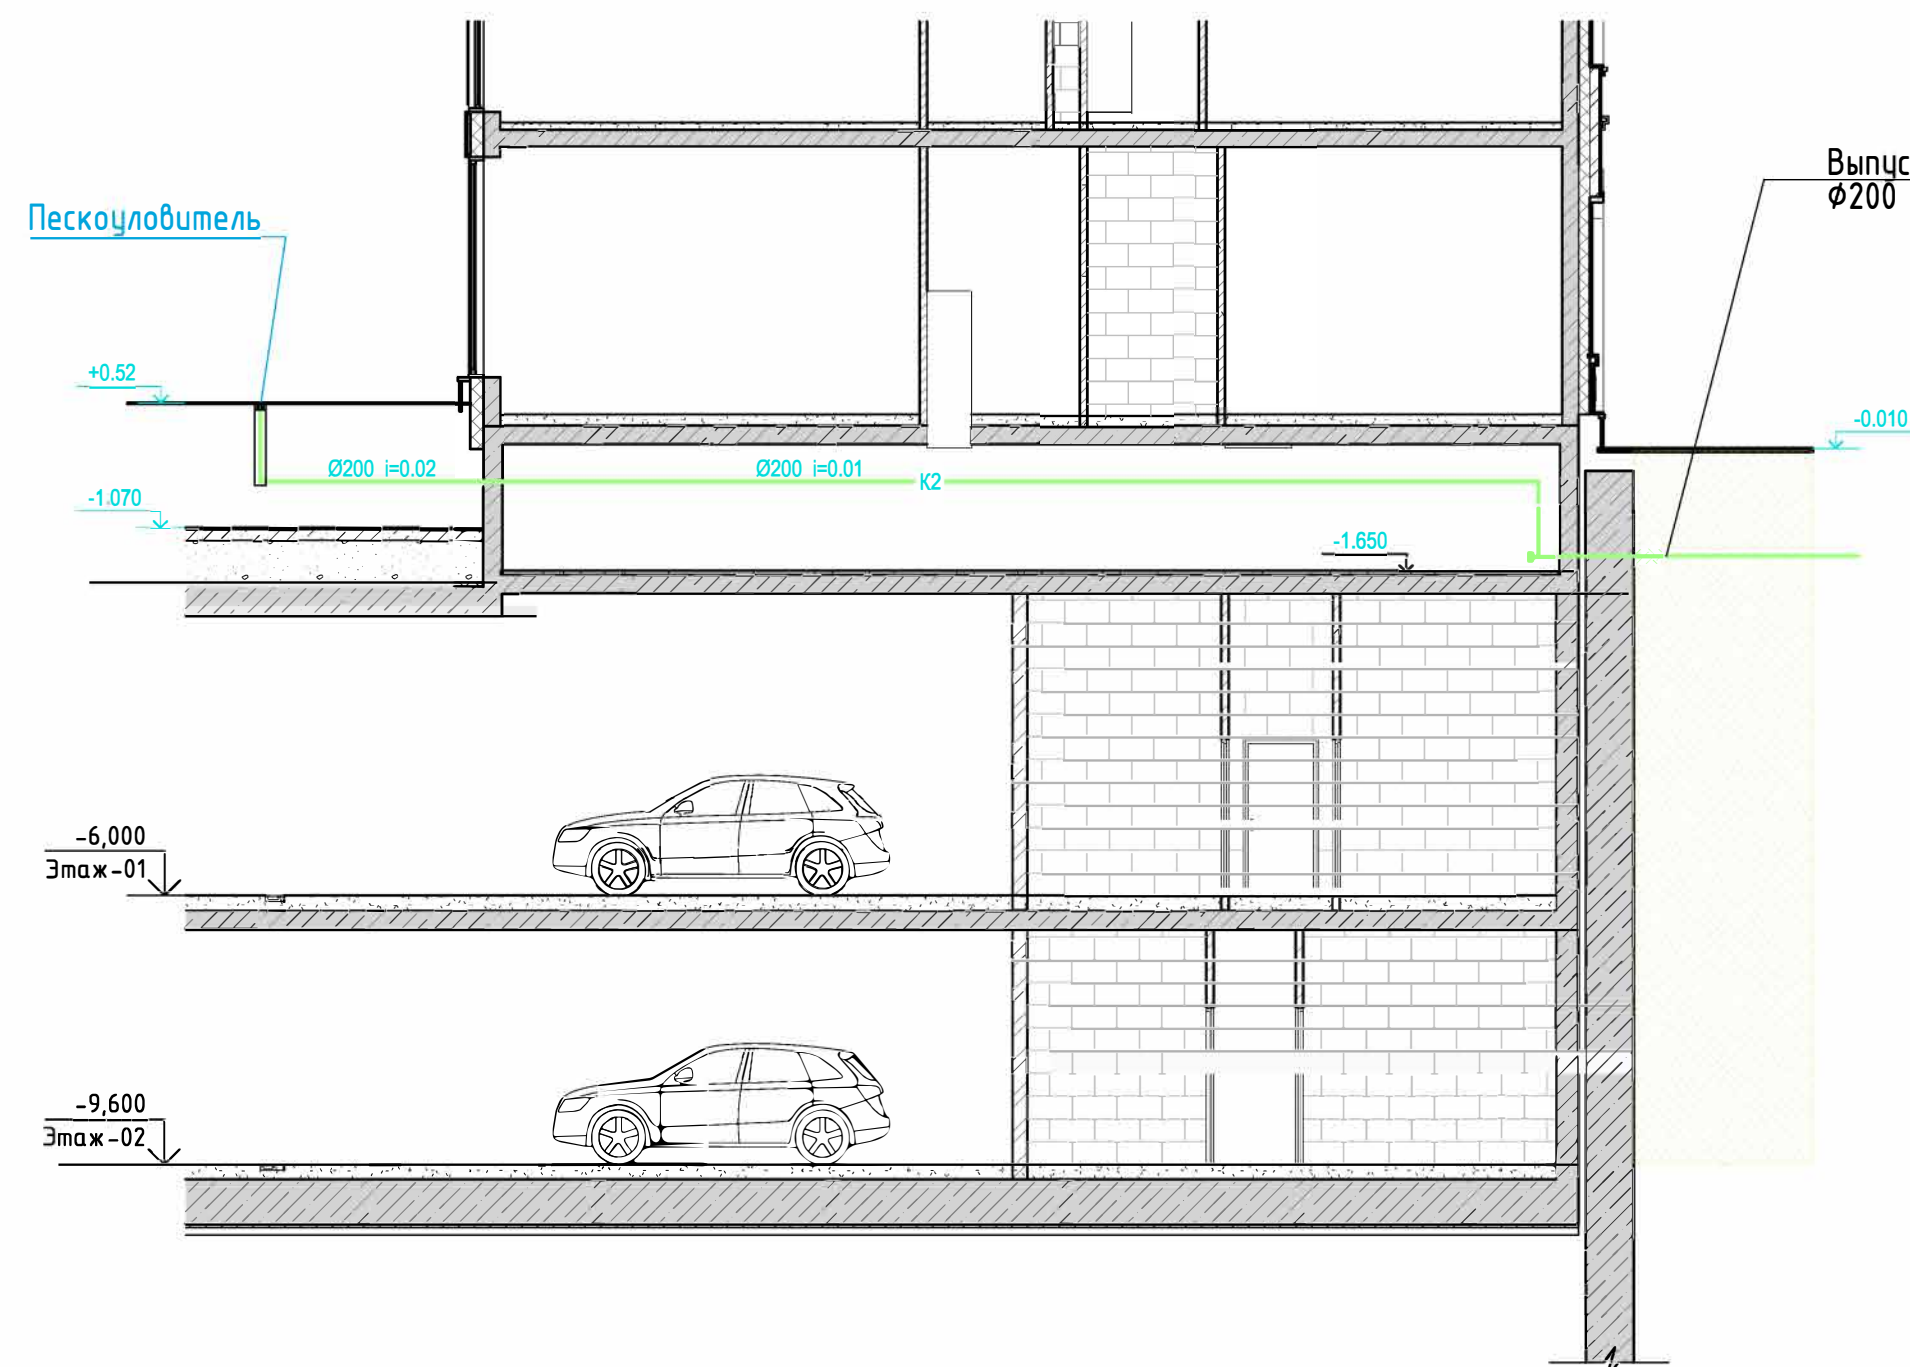

						ААБЭ-03-ДСЭ-ИОС-3.1			
						ЖИЛОЙ КОМПЛЕКС ПО АДРЕСУ: Г. МОСКВА, ЦАО, САДОВНИЧЕСКАЯ УЛ., ВЛ. 76/71			
Изм.	Кол. экз.	Лист	№ док.	Подп.	Дата	Внутренние системы водоотведения.	Стадия	Лист	Листов
Разработал	Шмелева	Шмелева	08.23	08.23	08.23		П	5	
Проверил	Шмелева	Шмелева	08.23	08.23	08.23	Принципиальная схема системы водостока со стилобата.	ООО "Совикон"		
ГИП	Сафин	Сафин	08.23	08.23	08.23				

ДОПОЛНИТЕЛЬНОЕ СОГЛАШЕНИЕ № 1

к Договору от 26.01.2023г. № 15234ДП-К о подключении (технологическом присоединении) к централизованной системе водоотведения (далее: «Договор»)

г. Москва

«15» АВГ 2024 г

Акционерное общество «Мосводоканал», именуемое в дальнейшем АО «Мосводоканал», в лице начальника управления по перспективному развитию и присоединениям АО «Мосводоканал» Бобровского Юрия Анатольевича, действующего на основании Доверенности № (30)01.08-1644/21 от 30.12.2021г., с одной стороны, и Общество с ограниченной ответственностью «Специализированный застройщик Балчуг эстейт» (ООО «СЗ Балчуг эстейт»), именуемое в дальнейшем «Заявитель», в лице Генерального директора Савосько Евгения Вячеславовича, действующего на основании Устава, с другой стороны, именуемые в дальнейшем «Стороны», заключили настоящее Дополнительное соглашение к Договору о нижеследующем:

1. Внести в Договор следующие изменения:

1.1. В связи с изменением наименования ООО «Балчуг эстейт», в преамбуле Договора и по всему тексту Договора, включая Приложения, наименование Заявителя – Общество с ограниченной ответственностью «Специализированный застройщик Балчуг эстейт» (ООО «СЗ Балчуг эстейт»).

1.2. Пункт 2.1. Договора в следующей редакции:

«Срок подключения объекта – до 30.06.2026 г.».

1.3. Пункт 3.3. Договора в следующей редакции:

Потребности объекта – величина подключаемой мощности (нагрузки) объекта, который обязано обеспечить АО «Мосводоканал» в точках подключения (технологического присоединения), составляет 114,080 м3/сут. приема сточных вод.

1.4. Пункт 5.2 Договора в следующей редакции:

Заявитель обязан внести плату в размере, предусмотренном приложением № 4 к настоящему договору, на расчетный счет АО «Мосводоканал» в следующем порядке:

- 6 322 905 рублей 78 копеек вносится в течение 15 дней с даты заключения настоящего договора;

- 9 032 722 рубля 54 копейки вносится в течение 90 дней с даты заключения настоящего договора, но не позднее даты фактического подключения;

- 774 768 рублей 53 копейки вносится в течение 15 дней с даты заключения настоящего Дополнительного соглашения;

- 2 846 540 рублей 62 копейки (15 % платы за подключение (технологическое присоединение) вносится в течение 15 дней с даты подписания сторонами акта о подключении (технологическом присоединении) объекта к централизованной системе водоотведения по форме согласно приложению № 5, но не позднее выполнения условий подключения (технологического присоединения).

В случае если сроки фактического присоединения объекта Заявителя не соблюдаются в связи с действиями (бездействием) Заявителя и АО «Мосводоканал» выполнены все необходимые мероприятия для создания технической возможности подключения (технологического присоединения) и выполнения работ по подключению (технологическому

присоединению), оставшаяся доля платы за подключение (технологическое присоединение) вносится в течение 15 дней со дня подписания акта о выполнении мероприятий по обеспечению технической возможности подключения (технологического присоединения) по форме согласно приложению № 6 либо в течение 10 календарных дней со дня получения заявителем уведомления, АО «Мосводоканал» о расторжении настоящего договора в одностороннем порядке, но не позднее срока подключения (технологического присоединения), указанного в настоящем договоре.

1.5. Пункт 9.1. Договора в следующей редакции:

«Настоящий договор вступает в силу со дня его подписания сторонами и действует до 30.06.2026 года, а в части обязательств, не исполненных к моменту окончания срока его действия - до полного их исполнения Сторонами».

1.6. Реквизиты Заказчика изложить в следующей редакции:

ООО «СЗ Балчуг эстейт»

Юридический адрес:

115035, г. Москва, Садовническая наб., дом 69

ОГРН 1167746249406

ИНН 9705062309

КПП 770501001

р/с 40702810700480031753

в АО "Банк ДОМ.РФ"

БИК 044525266

к/с 30101810345250000266

Оператор ЭДО:

ИНН _____

ОГРН _____

1.7. Изложить приложение № 1 - «Технические условия подключения (технологического присоединения) к централизованной системе водоотведения» в новой редакции (Приложение № 1 к настоящему дополнительному соглашению).

1.8. Изложить приложение № 2 - «Параметры подключения (технологического присоединения) к централизованной системе водоотведения» в новой редакции (Приложение № 2 к настоящему дополнительному соглашению).

1.9. Изложить приложение № 3 - «Перечень мероприятий (в том числе технических) по подключению (технологическому присоединению) объекта к централизованной системе водоотведения» в новой редакции (Приложение № 3 к настоящему дополнительному соглашению).

1.10. Изложить приложение № 4 - «Размер платы за подключение (технологическое присоединение) к централизованной системе водоотведения» в новой редакции (Приложение № 4 к настоящему дополнительному соглашению).

2. Стороны подтверждают, что на момент подписания настоящего Дополнительного соглашения Заявителем внесена плата за подключение по Договору в размере: 15 355 628 (пятнадцать миллионов триста пятьдесят пять тысяч шестьсот двадцать восемь) рубля 32 копейки, в том числе НДС (20 %) 2 559 271 рубль 39 копеек.

3. Во всем, что не оговорено настоящим Дополнительным соглашением, стороны руководствуются условиями заключенного Договора.

4. Настоящее Дополнительное соглашение вступает в силу с момента его заключения.

5. Настоящее Дополнительное соглашение является неотъемлемой частью Договора.

6. Настоящее Дополнительное соглашение составлено в двух экземплярах, имеющих равную юридическую силу, по одному для каждой из Сторон.

7. К настоящему Дополнительному Соглашению прилагается и является его неотъемлемой частью:

- Приложение № 1 – «Технические условия подключения (технологического присоединения) к централизованной системе водоотведения»;

- Приложение № 2 - «Параметры подключения (технологического присоединения) к централизованной системе водоотведения»;

- Приложение №3 – «Перечень мероприятий (в том числе технических) по подключению (технологическому присоединению) объекта к централизованной системе водоотведения»;

- Приложение № 4 – «Размер платы за подключение (технологическое присоединение) к централизованной системе водоотведения».

Реквизиты и подписи Сторон:

АО «Мосводоканал»

Юридический адрес: 105005,
г. Москва, Плетешковский пер., 2

ОГРН 1127747298250

ИНН 7701984274

КПП 770101001

Р/с 40602810338000000060

в ПАО Сбербанк

К/с 30101810400000000225

БИК 044525225

Оператор ЭДО:

ООО «Компания «Тензор»

ИНН 7605016030

ОГРН 1027600787994

ООО «СЗ БАЛЧУГ ЭСТЕЙТ»

Юридический адрес:

115035, г. Москва, Садовническая наб.,
дом 69

ОГРН 1167746249406

ИНН 9705062309

КПП 770501001

р/с 40702810700480031753

в АО "Банк ДОМ.РФ"

БИК 044525266

к/с 30101810345250000266

Оператор ЭДО:

ИНН _____

ОГРН _____

Начальник управления по перспективному
развитию и присоединениям

М.П.

" " 20__ г.

Начальник СТП УР
Куриленков А.Ю.

По доверенности №(30)01.08-1640/21



Ю.А. Бобровский

15 АВГ 2024

Генеральный директор



Е.В.Савосько

" " 20__ г.

15 АВГ 2024

Приложение № 1
к Дополнительному соглашению
№ 1 от 15 АВГ 2024 г.
Приложение 1
к Договору о подключении (технологическом
присоединении) к централизованным системам
водоотведения от 26.01.2023г. № 15234ДП-К

ТЕХНИЧЕСКИЕ УСЛОВИЯ ПОДКЛЮЧЕНИЯ (ТЕХНОЛОГИЧЕСКОГО ПРИСОЕДИНЕНИЯ) К ЦЕНТРАЛИЗОВАННОЙ СИСТЕМЕ ВОДООТВЕДЕНИЯ

Сведения об исполнителе:

Полное наименование: Акционерное общество "Мосводоканал"
Сокращенное наименование: АО "Мосводоканал"
ОГРН 1127747298250
Юридический адрес: 105005, Москва, Плетешковский пер., д 2
Телефон: 8-499-763-34-34
E-mail: post@mosvodokanal.ru
Заявитель: ОБЩЕСТВО С ОГРАНИЧЕННОЙ ОТВЕТСТВЕННОСТЬЮ
"СПЕЦИАЛИЗИРОВАННЫЙ ЗАСТРОЙЩИК БАЛЧУГ ЭСТЕЙТ"
Наименование объекта Жилой комплекс с подземной автостоянкой
Адрес объекта Садовническая ул., владение 76/71

Информация о точке (точках) присоединения:

существующие колодцы на канализационной сети $d=300\text{мм}$ с восточной стороны, канализационной сети $d=450\text{мм}$ с западной стороны и в существующий колодец К-2015019 на канализационной сети $d=125-200\text{мм}$.

Информация о максимальной мощности (нагрузке) в возможных точках присоединения, в пределах которой исполнитель обязуется обеспечить возможность подключения подключаемого объекта: не запрашивалась.

Начальник управления по
перспективному развитию и
присоединениям
АО «Мосводоканал»

Генеральный директор
ООО «СЗ БАЛЧУГ ЭСТЕЙТ»

М.П.  Ю.А. Бобровский

Е.В.Савосько

М.П.

М.П.

20 ____ г.

Зам. начальника управления –
начальник
Куриленков Д.Ю. В.А.
По доверенности №(30)01.08-1640/21

15 АВГ 2024



15 АВГ 2024

ПАРАМЕТРЫ ПОДКЛЮЧЕНИЯ (ТЕХНОЛОГИЧЕСКОГО ПРИСОЕДИНЕНИЯ) К ЦЕНТРАЛИЗОВАННОЙ СИСТЕМЕ ВОДООТВЕДЕНИЯ

Основание:	Заявка на подключение № 15234ДП-К
Причина обращения:	НОВОЕ СТРОИТЕЛЬСТВО
Подключаемый объект:	Жилой комплекс с подземной автостоянкой Садовническая ул., владение 76/71
Кадастровый номер земельного участка	77:01:0002014:6383
Заявитель:	ОБЩЕСТВО С ОГРАНИЧЕННОЙ ОТВЕТСТВЕННОСТЬЮ "СПЕЦИАЛИЗИРОВАННЫЙ ЗАСТРОЙЩИК БАЛЧУГ ЭСТЕЙТ"

Точка подключения (технологического присоединения) к централизованной системе водоотведения: внешняя стенка колодца/колодцев на выпусках из здания.

Необходимо выполнить:

- строительство канализационной сети в интервале К-2015019-К-2015028 для обеспечения пропускной способности сети в нормальном гидравлическом режиме с учетом дополнительного объема стоков от подключаемого объекта;

- устройство колодца/колодцев на выпусках из здания/зданий;

- строительство канализационной сети от колодца/колодцев на выпусках из здания/зданий до точки присоединения.

Технические требования к объектам капитального строительства Заявителя, в том числе к устройствам и сооружениям для подключения (технологического присоединения), а также к выполняемым Заявителем мероприятиям для осуществления подключения (технологического присоединения):

- обеспечить сохранность транзитных сетей от зданий остающихся в эксплуатации или переключить их на проектируемые/перекладываемые канализационные сети с сохранением непрерывного водоотведения от объектов;

- канализационные сети исключаемые из эксплуатации должны быть ликвидированы, колодцы демонтированы и забутованы;

- переустройство/ликвидацию сетей, не состоящих на балансе АО "Мосводоканал" согласовать с владельцем сети. Копию согласования приложить к документации, представляемой в АО "Мосводоканал".

- выполнить все мероприятия, предусмотренные приложением № 3 к договору. Мероприятия должны быть выполнены в сроки, установленные приложением № 3.

Нарушение Заявителем условий подключения путем невыполнения предусмотренных разделом II приложения № 3 перечня мероприятий является существенным нарушением условий договора.

Проектирование и строительство внутриплощадочных сетей вести в соответствии с требованиями АО "Мосводоканал".

Предъявлять АО "Мосводоканал":

- до начала работ для определения технического состояния и качества: трубы, фасонные части, конструктивные элементы колодцев, металлоконструкции, арматуру, запорную арматуру и другое применяемое при строительстве оборудование и материалы, а также сертификаты и паспорта на них;

- выполнение скрытых работ по строительству внутриплощадочных сетей в полном объеме: основания под трубопроводы, упоры, гидроизоляцию колодцев, камер, вязку арматурных каркасов, сварные швы, телевизионный контроль и т.д.;

- гидравлические испытания трубопроводов в соответствии с СП 129.13330.2019;

- исполнительную документацию в составе:

- Акты на скрытые работы по устройству оснований, фундаментов, упоров, уплотнений грунтов, изоляции и др.;
- Сертификаты и технические паспорта на трубы, арматуру, оборудование и материалы;
- Акты гидравлических испытаний коммуникаций и сооружений на прочность и герметичность;
- Журнал производства работ;
- Исполнительная документация законченного строительством объекта с решением Комитета по архитектуре и градостроительству города Москвы (МОСКОМАРХИТЕКТУРЫ) о приемке данной исполнительной документации для ведения сводного плана подземных коммуникаций и сооружений;
- Акт технической приемки законченного строительством объекта;
- Гарантийный паспорт строительной организации на сдаваемый объект с указанием срока ответственности за скрытые дефекты;
- Акт технической приемки системы внутренней канализации объекта;
- Исполнительные чертежи (заверенные подписями и печатями Заявителя, проектной и подрядной организаций) системы внутренней канализации в составе: плана технического подполья с разводкой канализации и аксонометрического чертежа по стоякам с сантехприборами.

Отметка лотков в точке (точках) присоединения к централизованной системе водоотведения : определить проектом.

Нагрузка в точке подключения хозяйственно-бытовых сточных вод 114,08 м³/сут;
6,5 л/с

Нормативы по объему сточных вод, нормативы состава сточных вод, требования к составу и свойствам сточных вод, установленные в целях предотвращения негативного воздействия на работу централизованной системы водоотведения - не предусмотрено.

Режим отведения сточных вод – круглосуточно.

Требования к устройствам, предназначенным для отбора проб и учета объема сточных вод, требования к проектированию узла учета, к месту размещения устройств учета, требования к схеме установки устройств учета и иных компонентов узла учета, требования к техническим характеристикам устройств учета, в том числе точности, диапазону измерений и уровню погрешности (требования к устройствам не должны содержать указания на определенные марки приборов и методики измерения) – не предусмотрено.

Требования по сокращению сброса загрязняющих веществ, которые должны быть учтены в плане снижения сбросов, плане по обеспечению соблюдения требований к составу и свойствам сточных вод, установленных в целях предотвращения негативного воздействия на работу централизованной системы водоотведения – не предусмотрено.

Границы эксплуатационной ответственности по канализационным сетям АО "Мосводоканал" и Заявителя: внешняя стенка колодца/колодцев на выпусках из здания.

Информация о наличии сетей канализации в зоне проведения работ


В случае необходимости сноса (выноса) инженерных сетей и (или) сооружений, принадлежащих АО "Мосводоканал" на праве собственности, Застройщик обязан после утверждения границ строительной площадки и посадки проектируемых зданий, сооружений или линейных объектов, до начала разработки проектной документации и выполнения работ по подготовке строительной площадки обратиться в АО "Мосводоканал" с Заявкой и заключить Соглашение о компенсации потерь (далее по тексту - СКП) по объекту по форме, утвержденной и размещенной на сайте <http://www.mosvodokanal.ru/>.

Застройщик обязан: в установленном СКП порядке, размере и сроке компенсировать АО "Мосводоканал" все его расходы и убытки.

В случае наличия в проекте технического решения о сносе/выносе водопроводных и/или канализационных сетей, сооружений, зданий, оборудования или иного имущества (далее по тексту - Объекты), принадлежащего на праве собственности городу Москве, мероприятия по сносу/выносу Объектов обеспечиваются Застройщиком с обязательным соблюдением требований постановлений Правительства Москвы от 29.06.2010 №540-ПП "Об утверждении положения об управлении объектами нежилого фонда, находящимися в собственности города Москвы" и от 15.12.2015 № 861-ПП "О порядке осуществления денежной компенсации городу Москве в связи со сносом инженерных сетей и сооружений, сооружений связи, линий связи и сетей связи, объектов электросетевого хозяйства, находящихся в собственности города Москвы, осуществляемых в процессе строительства объектов капитального строительства".

Начальник управления по
перспективному развитию и
присоединениям
АО «Мосводоканал»

Ю.А. Бобровский

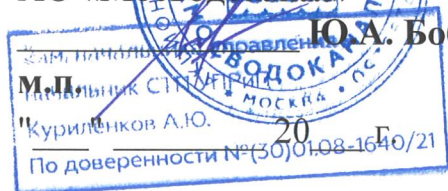

Генеральный директор
ООО «СЗ БАЛЧУГ ЭСТЕЙТ»

Е.В.Савосько



15 АВГ 2024


20 ____ г.

Строительство объекта: "Жилой комплекс", расположенный по адресу:
по адресу: г. Москва, ЦАО, Садовническая ул., вл. 76/77

ПЛАН ЗЕМЕЛЬНОГО УЧАСТКА М1:2000

Судостроение	Вод. транспорт
_____ в _____	Водоснабжение
_____ к _____	Канализация
_____ в _____	Газоснабжение
_____ в _____	Теплофикация
_____ в _____	Эл. снабжение
_____ в _____	Телекомму.
_____ в _____	Водосб.
_____ в _____	Радиосвязь
_____ в _____	Развлек.-культ.
_____ в _____	Клубы

СЛОВНЫЕ ОБОЗНАЧЕНИЯ ЛИНИЙ
РАДОСТРОИТЕЛЬНОГО РЕГУЛИРОВАНИЯ:

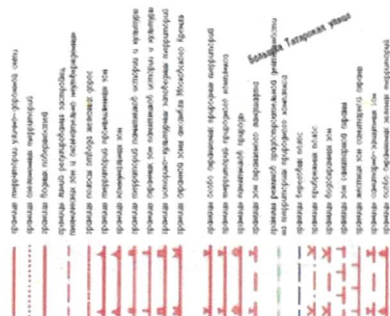[illegible]

количество	единиц	1 шт.
количество	единиц	количество
231 м/м		
количество	единиц	467
м/м		

Тип сетки		Будинг	Потребляемое количество	Примечание
Коробчатая	Холодильные ящики	м ² /шт	106,39	
	Вентиляторы	шт	4,4	
	Покрывочные	шт	310	
Полосчатая	Вентиляторы	шт	419,4	
	Покровные	шт	132,62	
	Вентиляторы	шт	6	
Коробчатая	Вентиляторы	шт	129	
	Покровные	шт	419,7	
	Вентиляторы	шт	1117,1/200,3	
Полосчатая	Вентиляторы	шт	5	
	Покровные	шт		
	Вентиляторы	шт		
Коробчатая	Вентиляторы	шт		
	Покровные	шт		
	Вентиляторы	шт		

Наименование	Доплатные вспомогательные	Таблица забоя	ГВС тр.	Коэффициент ГВС, макс. (работы)	Прочие	Всего (с учетом ГВС макс.)	Всего (с учетом ГВС макс.)
Таблица маршрута, Гкал/час	0,586	1,442	0,0775	0,5552	0,0	2,3627	2,6595

ВНИИ ГРАДОСТРОИТЕЛЬНОГО РЕГУЛИРОВАНИЯ ОТОБРАЖЕНЫ ПО ДАННЫМ СВОДНОГО ПЛАНА РЕГУЛИРОВАНИЯ ИСПОЛЬЗОВАНИЯ ТЕРРИТОРИИ ГОРОДА МОСКВЫ НА 10.09.2012 Г.

[illegible]

Условные обозначения	
	Граница участка
	Существующая застройка
	Проектируемая застройка
	Сохраняемая застройка (восстановление)
	Контуры подземной части
	ВРУ
	Водомерный узел
	ИТП
	Ввод теплоты
	Ввод водоснабжения (В 1)
	Выпуск канализации (К 1)
	Выпуск дождевой канализации (К 2)

ГОСУДАРСТВЕННОЕ УНИТАРНОЕ ПРЕДПРИЯТИЕ
города Москвы по эксплуатации московских водоотводящих систем
«МОСВОДОСТОК»

119017, Москва, Новокузнецкая ул., 26/8 стр. 1
ОГРН 1027739015567

тел.: (495) 953-29-01
Email: cancel@mosvodostok.info

ТЕХНИЧЕСКИЕ УСЛОВИЯ

№ 957/22 от 25.10.2022 г.

**на подключение к централизованной системе водоотведения поверхностных сточных вод.
Технологическое подключение объекта осуществляется на основании
заключенного договора о подключении.**

№ письма: 0001-90000003-068701-0014981/22

Заявитель: ООО "БАЛЧУГ ЭСТЕЙТ"

Объект: Жилой комплекс

Адрес: Город Москва, Улица Садовническая Земельный участок Владение 76/71

Планируемая нагрузка: 129 л/сек.

**Осуществить подключение к централизованной системе водоотведения поверхностных
сточных вод:**

D=400мм вблизи Садовнической улицы, дом 67с1 в смотровой колодез К1.

Максимальная нагрузка в точке присоединения: 150 л/сек.

Эксплуатационный гидротехнический район по адресу объекта - ЭГТР-1, тел.: +7(495) 685-38-20

Срок действия технических условий: 3 года от даты выдачи.

В случае если в течение 12 календарных месяцев (при комплексном развитии территории в течение 36 календарных месяцев) со дня выдачи технических условий заявителем не будет подано заявление о подключении, срок действия технических условий прекращается.

Приложение: ситуационный план с обозначением точки подключения.


Инженер 1 категории
Тел.: (495) 657-87-19 (1180)

Н.И. Подсадник

Главный инженер

А.А. Чибриков



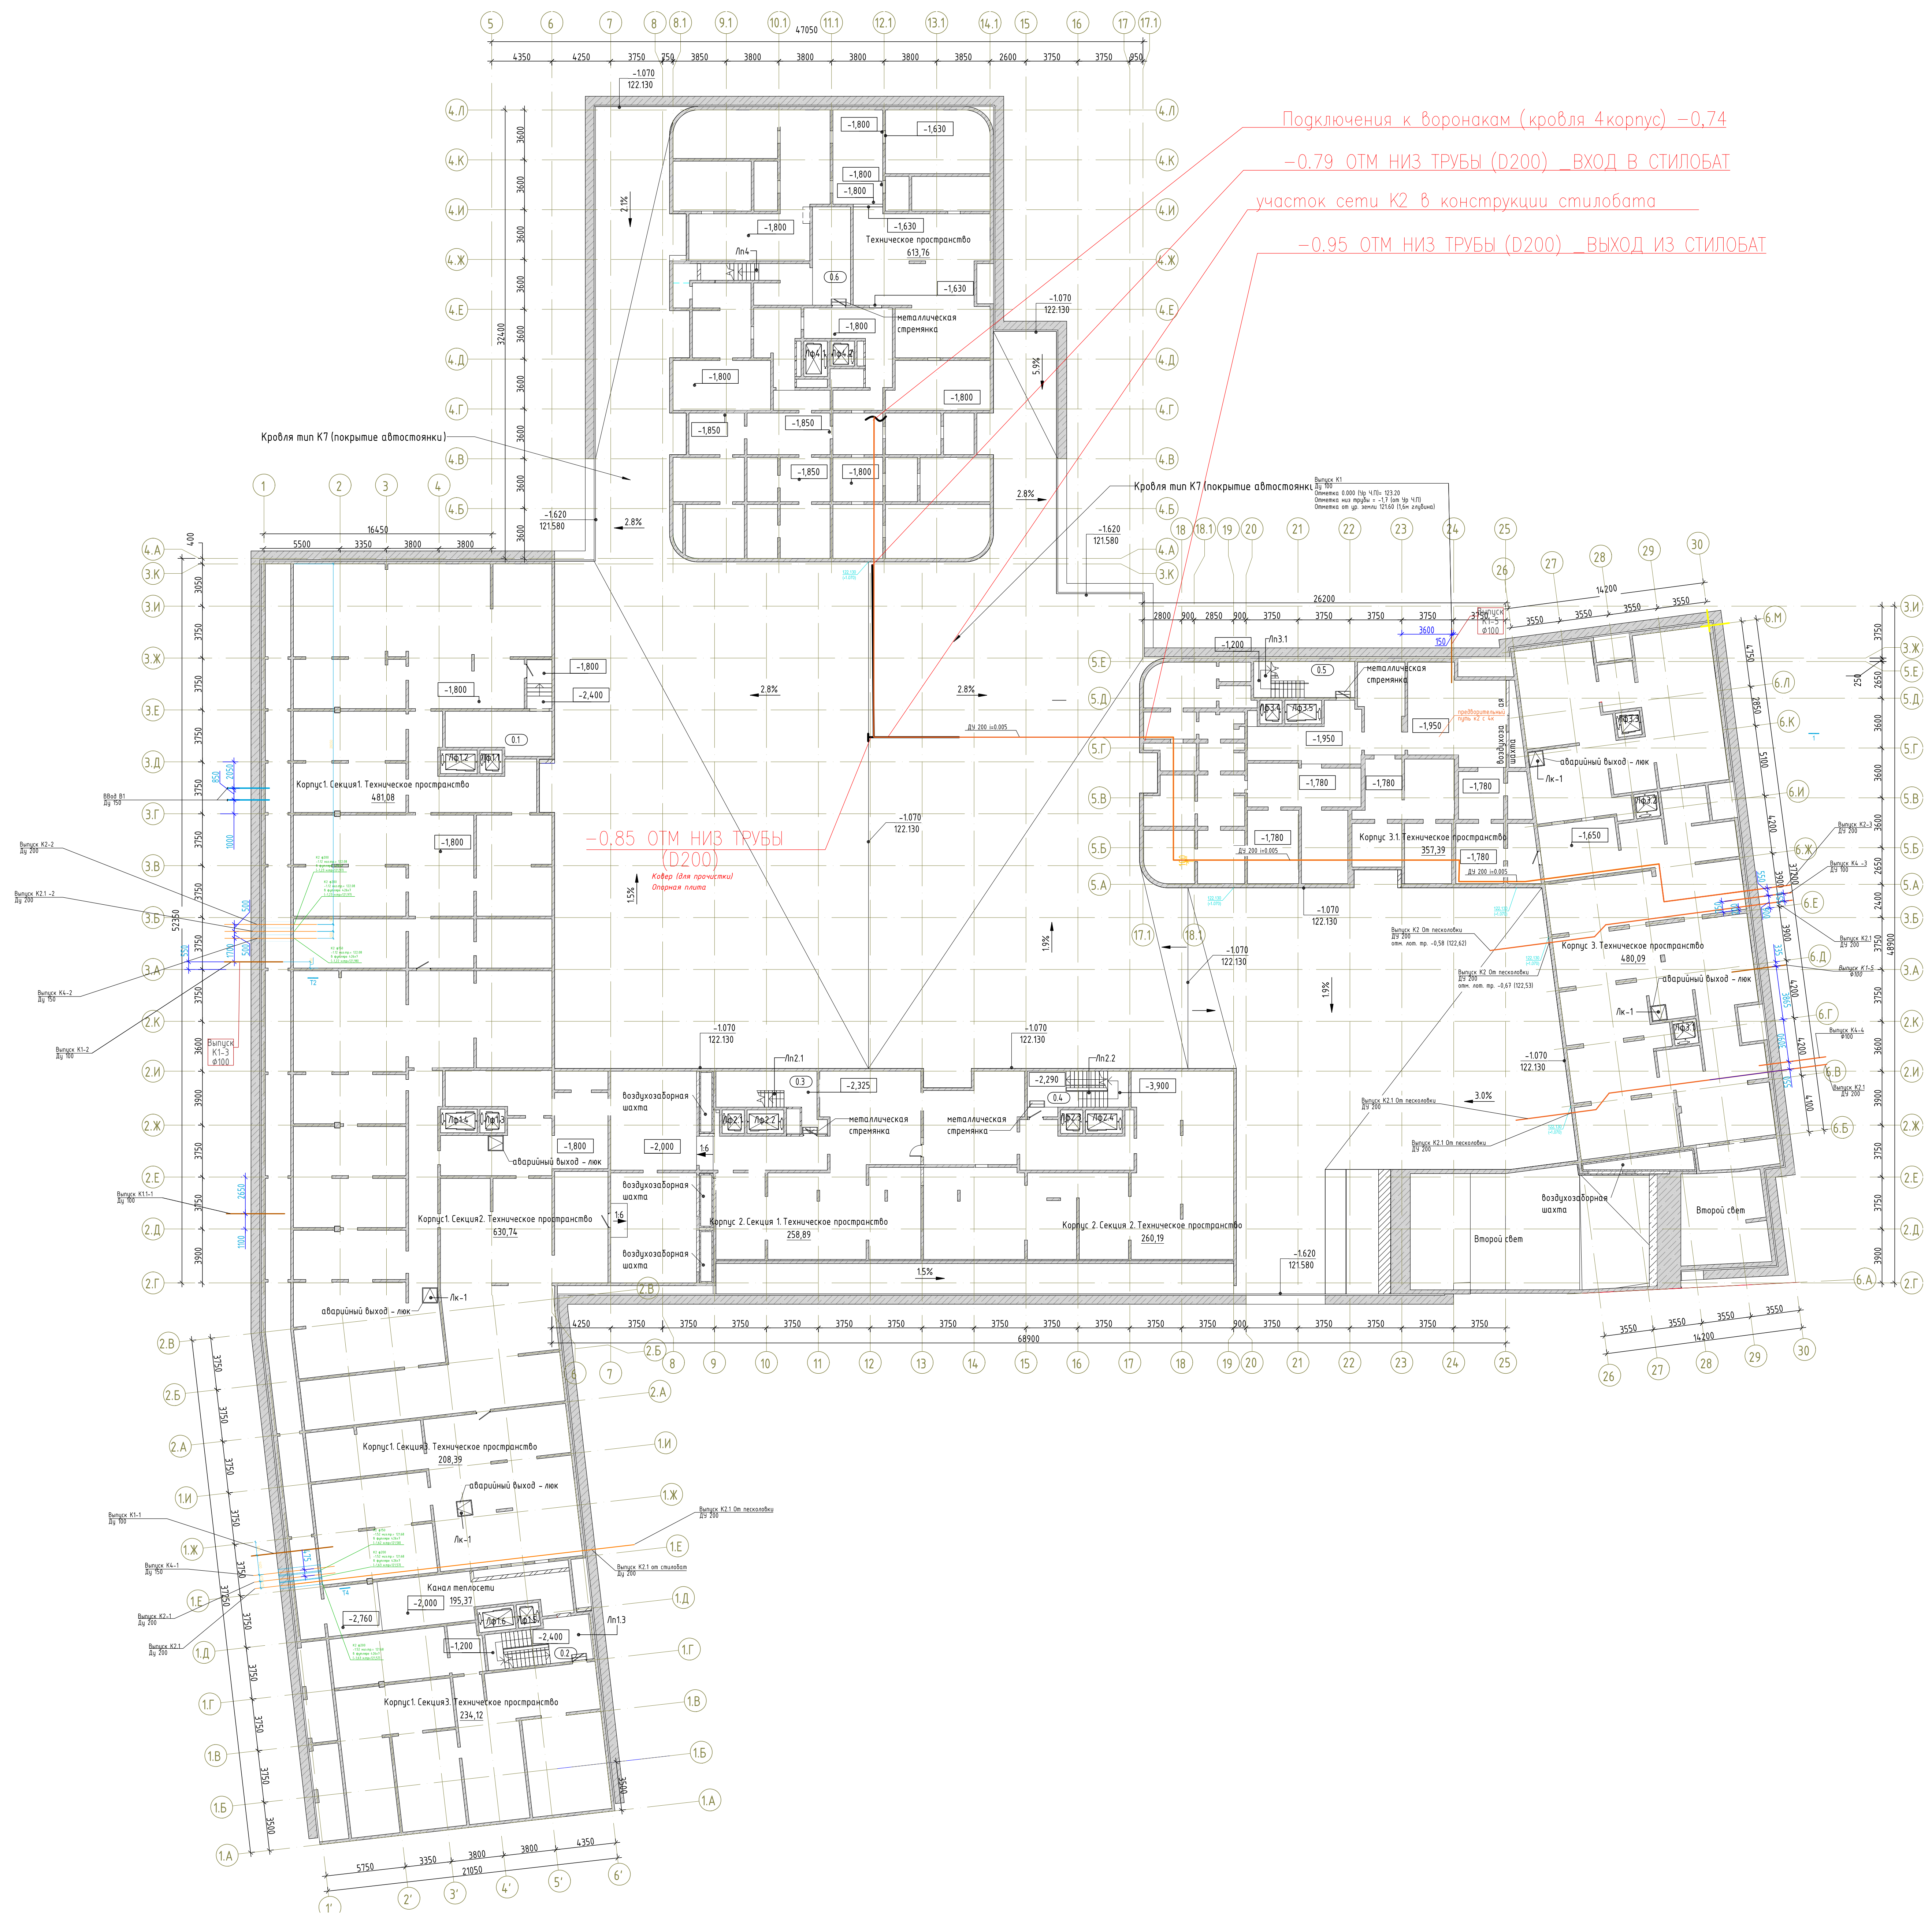

Экспликация помещений			
Номер помещения	Наименование	Площадь, м²	Кат. помещения
0.1	Лестничная клетка Лн1.1	28,98	
0.2	Лестничная клетка Лн1.3	22,23	
0.3	Лестничная клетка Лн2.1	21,97	
0.4	Лестничная клетка Лн2.2	20,52	
0.5	Лестничная клетка Лн3.1	18,98	
0.6	Лестничная клетка Лн4	36,36	
		169,04	

Экспликация технических пространств		
Наименование	Площадь, м²	Кат. помещения
Корпус1 Секция1. Техническое пространство	481,08	
Корпус1 Секция2. Техническое пространство	630,74	
Корпус1 Секция3. Техническое пространство	234,12	
Корпус1 Секция3. Техническое пространство	208,39	
Корпус 2 Секция 1. Техническое пространство	258,89	
Корпус 2 Секция 2. Техническое пространство	260,19	
Корпус 3.1. Техническое пространство	357,39	
Корпус 3. Техническое пространство	480,09	
Техническое пространство	613,76	
		3524,65

Канал теплосети	195,37	
-----------------	--------	--

Подключения к воронкам (крыша 4 корпус) -0.74
-0.79 ОТМ НИЗ ТРУБЫ (D200) _ВХОД В СТИЛОБАТ
участок сети K2 в конструкции стилобата
-0.95 ОТМ НИЗ ТРУБЫ (D200) _ВЫХОД ИЗ СТИЛОБАТ

-0.85 ОТМ НИЗ ТРУБЫ (D200)
Котел (для проточной)
Открытая плита